

平潭综合实验区苏平镇剑湖-东占村2021年高标准农田提升改造项目规划图 1:2000



项目区耕地坡度分析表

分村	总面积	0~2° 面积	2~6° 面积	6~15° 面积	15~25° 面积	25° 以上面积
剑湖村	53.55	1.07	9.13	43.35	0.00	0.00
东占村	59.67	0.00	4.36	49.29	6.01	0.00
总计	113.21	1.07	13.50	92.64	6.01	0.00

田间排灌系统设施情况及拟利用情况表


序号	设施名称及编号	长度(米)	宽度(米)	深度(米)	结构情况	拟利用方式
1	道路边沟A01	383	2.5	1.2	土质	利用现状
2	原有沟渠A02	352	1.0	0.5	砌石	利用现状
3	原有沟渠A03	262	2.0	1.2	砼	利用现状
4	溢洪道A04	61	3.0	1.8	砼	利用现状

道路交通设施情况及拟利用情况表

序号	道路名称及编号	长度(米)	宽度(米)	路肩情况	垫层情况	路面情况	拟利用方式
1	原有道路 A01	321	3	无	有	水泥路面	利用现状
2	原有道路 A02	118	1.2	无	无	土质	利用现状
3	原有道路 A03	147	1.2	无	无	土质	利用现状
4	原有道路 A04	241	1.2	无	无	土质	利用现状

项目区土地利用现状地类面积表

一级类		二级类		现状地类面积（二调）	
编号	名称	编号	名称	（亩）	比例(%)
01	耕地	013	旱地	113.21	71.49
小计				113.21	71.49
03	林地	031	有林地	6.18	3.90
		033	其他林地	11.13	7.03
小计				17.30	10.93
04	草地	043	其他草地	0.76	0.48
小计				0.76	0.48
10	交通运输用地	104	农村道路	0.51	0.32
小计				0.51	0.32
11	水域及水利设施用地	117	沟渠	1.61	1.01
小计				1.61	1.01
12	其他土地	123	田坎	24.97	15.77
小计				24.97	15.77
合计				158.36	100

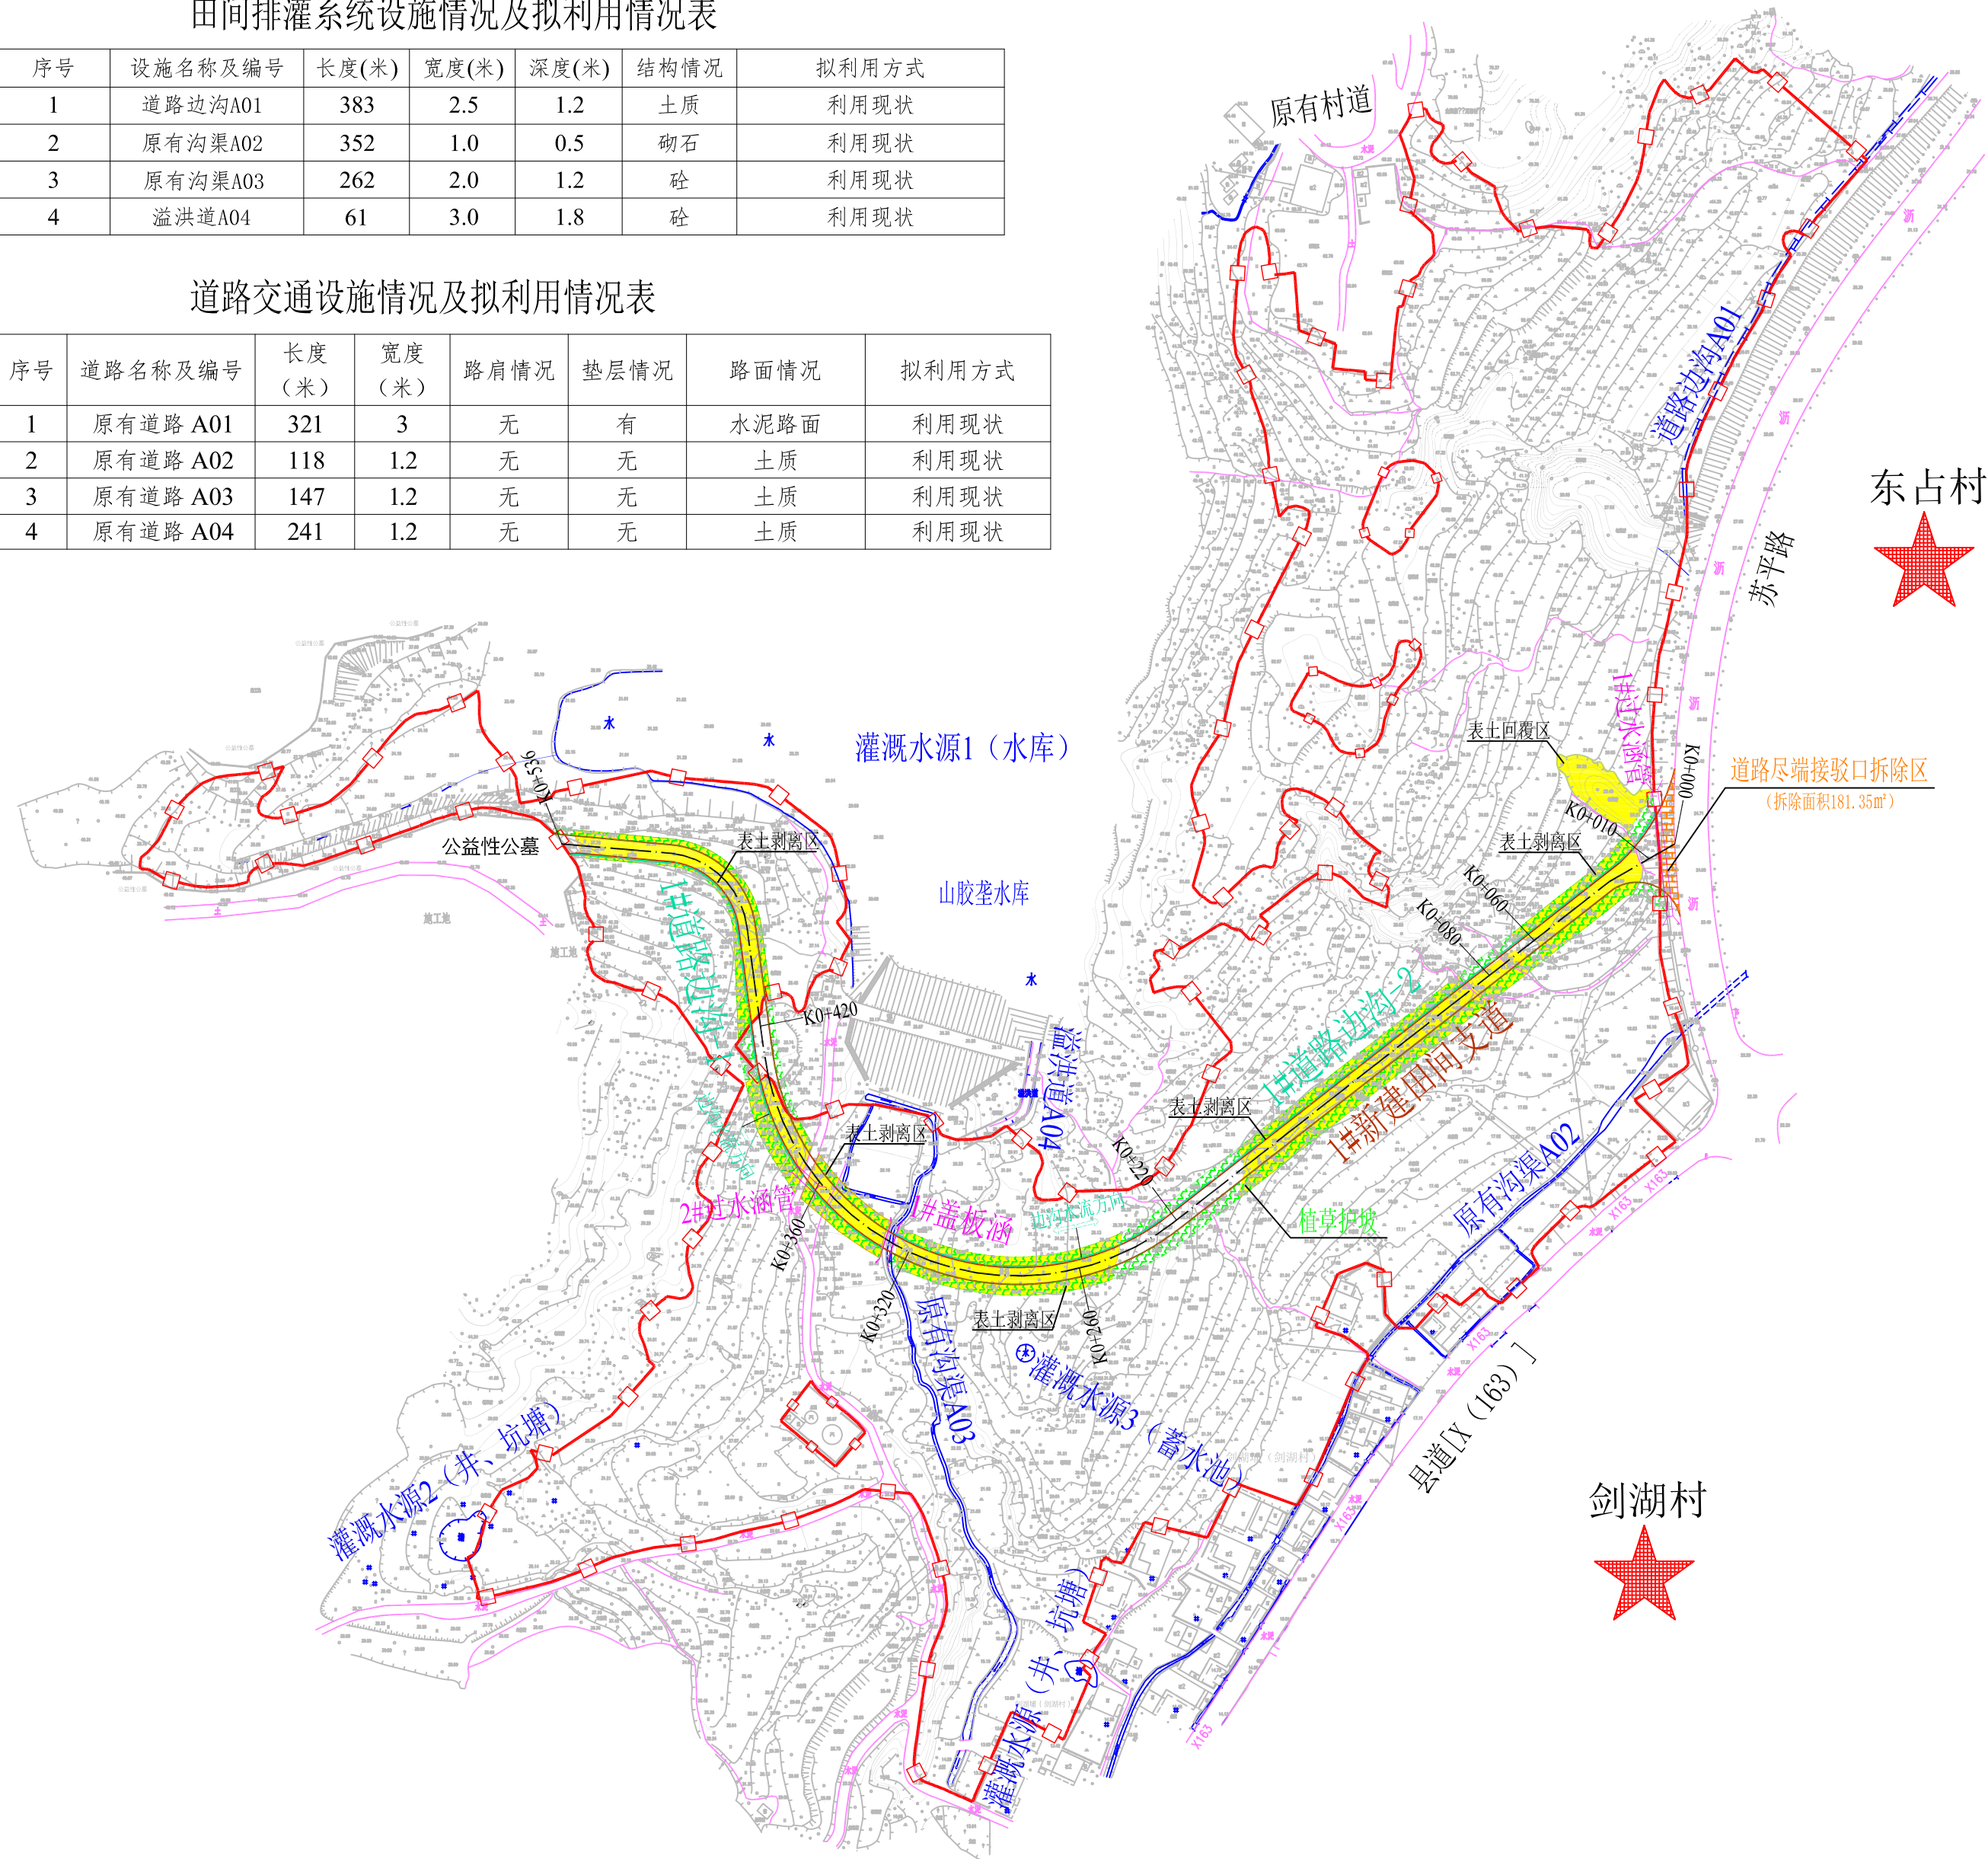

图例		现状水系		排水涵洞(管)
		原有路		盖板涵
		沟渠		护坡植草
		田间道		拆除工程区
		道路中线		表土剥离区
		项目区范围线		表土回覆区

- 说明:
- 项目区涉及平潭综合实验区苏平镇剑湖村和东占村，距平潭综合实验区22km。项目区总规模为158.36亩。
 - 该项目地形图由福建省地质测绘院于2021年6月份数字化测图；2000国家大地坐标系,1985国家高程基准，等高距为1.0米，2007版图式。

福建省地质测绘院

审定	林月辉	工程名称	平潭综合实验区苏平镇剑湖-东占村2021年高标准农田提升改造项目		
校核	彭枫	项目区规划图		比例	1:2000
设计	彭震	单项工程	总平面布置	日期	2021.12
制图	彭震	设计阶段	规划设计	图号	PTSP-GH-02