


海坛片区中山大道与海坛路交叉口西北侧SC202100012地块红线图

福州市勘测院
地形图专用章(3)
保密资料 严禁复制

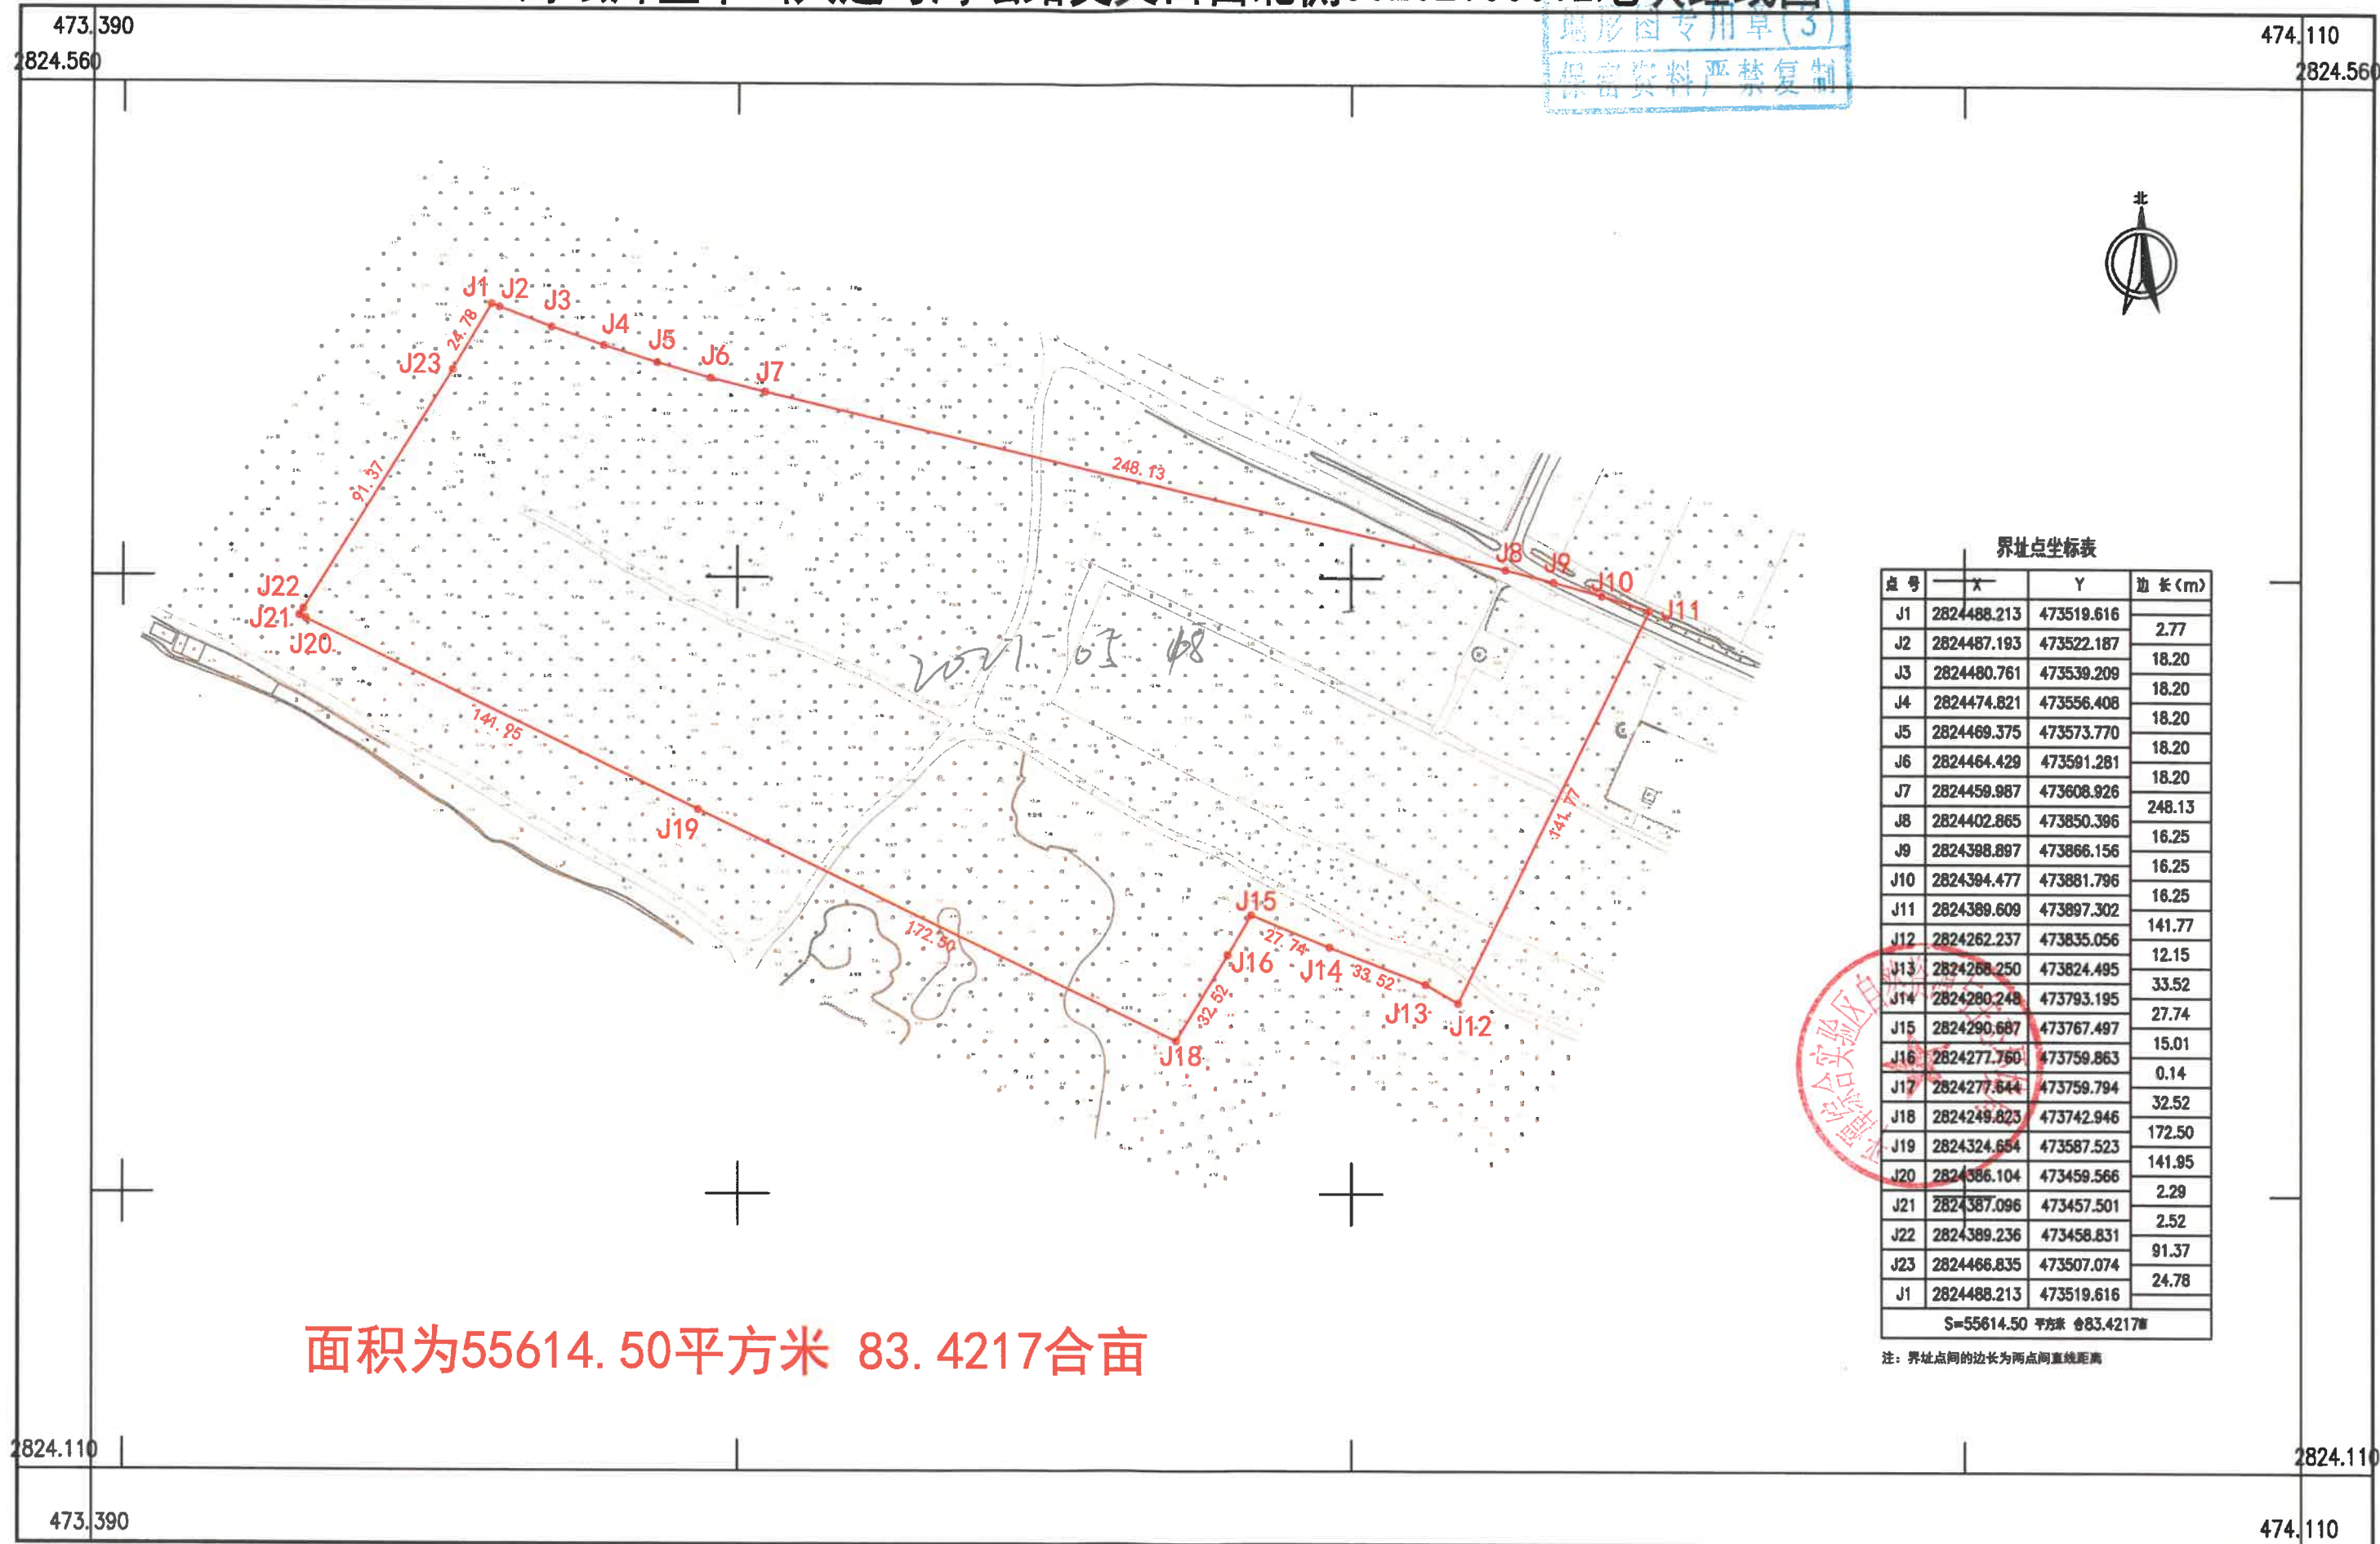

界址点坐标表			
点号	X	Y	边长(m)
J1	2824488.213	473519.616	
J2	2824487.193	473522.187	2.77
J3	2824480.761	473539.209	18.20
J4	2824474.821	473556.408	18.20
J5	2824469.375	473573.770	18.20
J6	2824464.429	473591.281	18.20
J7	2824459.987	473608.926	18.20
J8	2824402.865	473850.396	248.13
J9	2824398.897	473866.156	16.25
J10	2824394.477	473881.796	16.25
J11	2824389.609	473897.302	16.25
J12	2824262.237	473835.056	141.77
J13	2824268.250	473824.495	12.15
J14	2824280.248	473793.195	33.52
J15	2824290.687	473767.497	27.74
J16	2824277.760	473759.863	15.01
J17	2824277.844	473759.794	0.14
J18	2824249.823	473742.946	32.52
J19	2824324.654	473587.523	172.50
J20	2824386.104	473459.566	141.95
J21	2824387.096	473457.501	2.29
J22	2824389.236	473458.831	2.52
J23	2824466.835	473507.074	91.37
J1	2824488.213	473519.616	24.78
S=55614.50 平方米 83.4217亩			

2010年7月数字化成图
2000国家大地坐标系
1985国家高程基准
2009年福州基础地理信息数据图式
加盖福州市勘测院地形图蓝章，方为正式材料

1:2000