


海坛片区下洋村南侧SC202000038地块红线图

福州市勘测院
地形图专用章(3)
保密资料 严禁复制

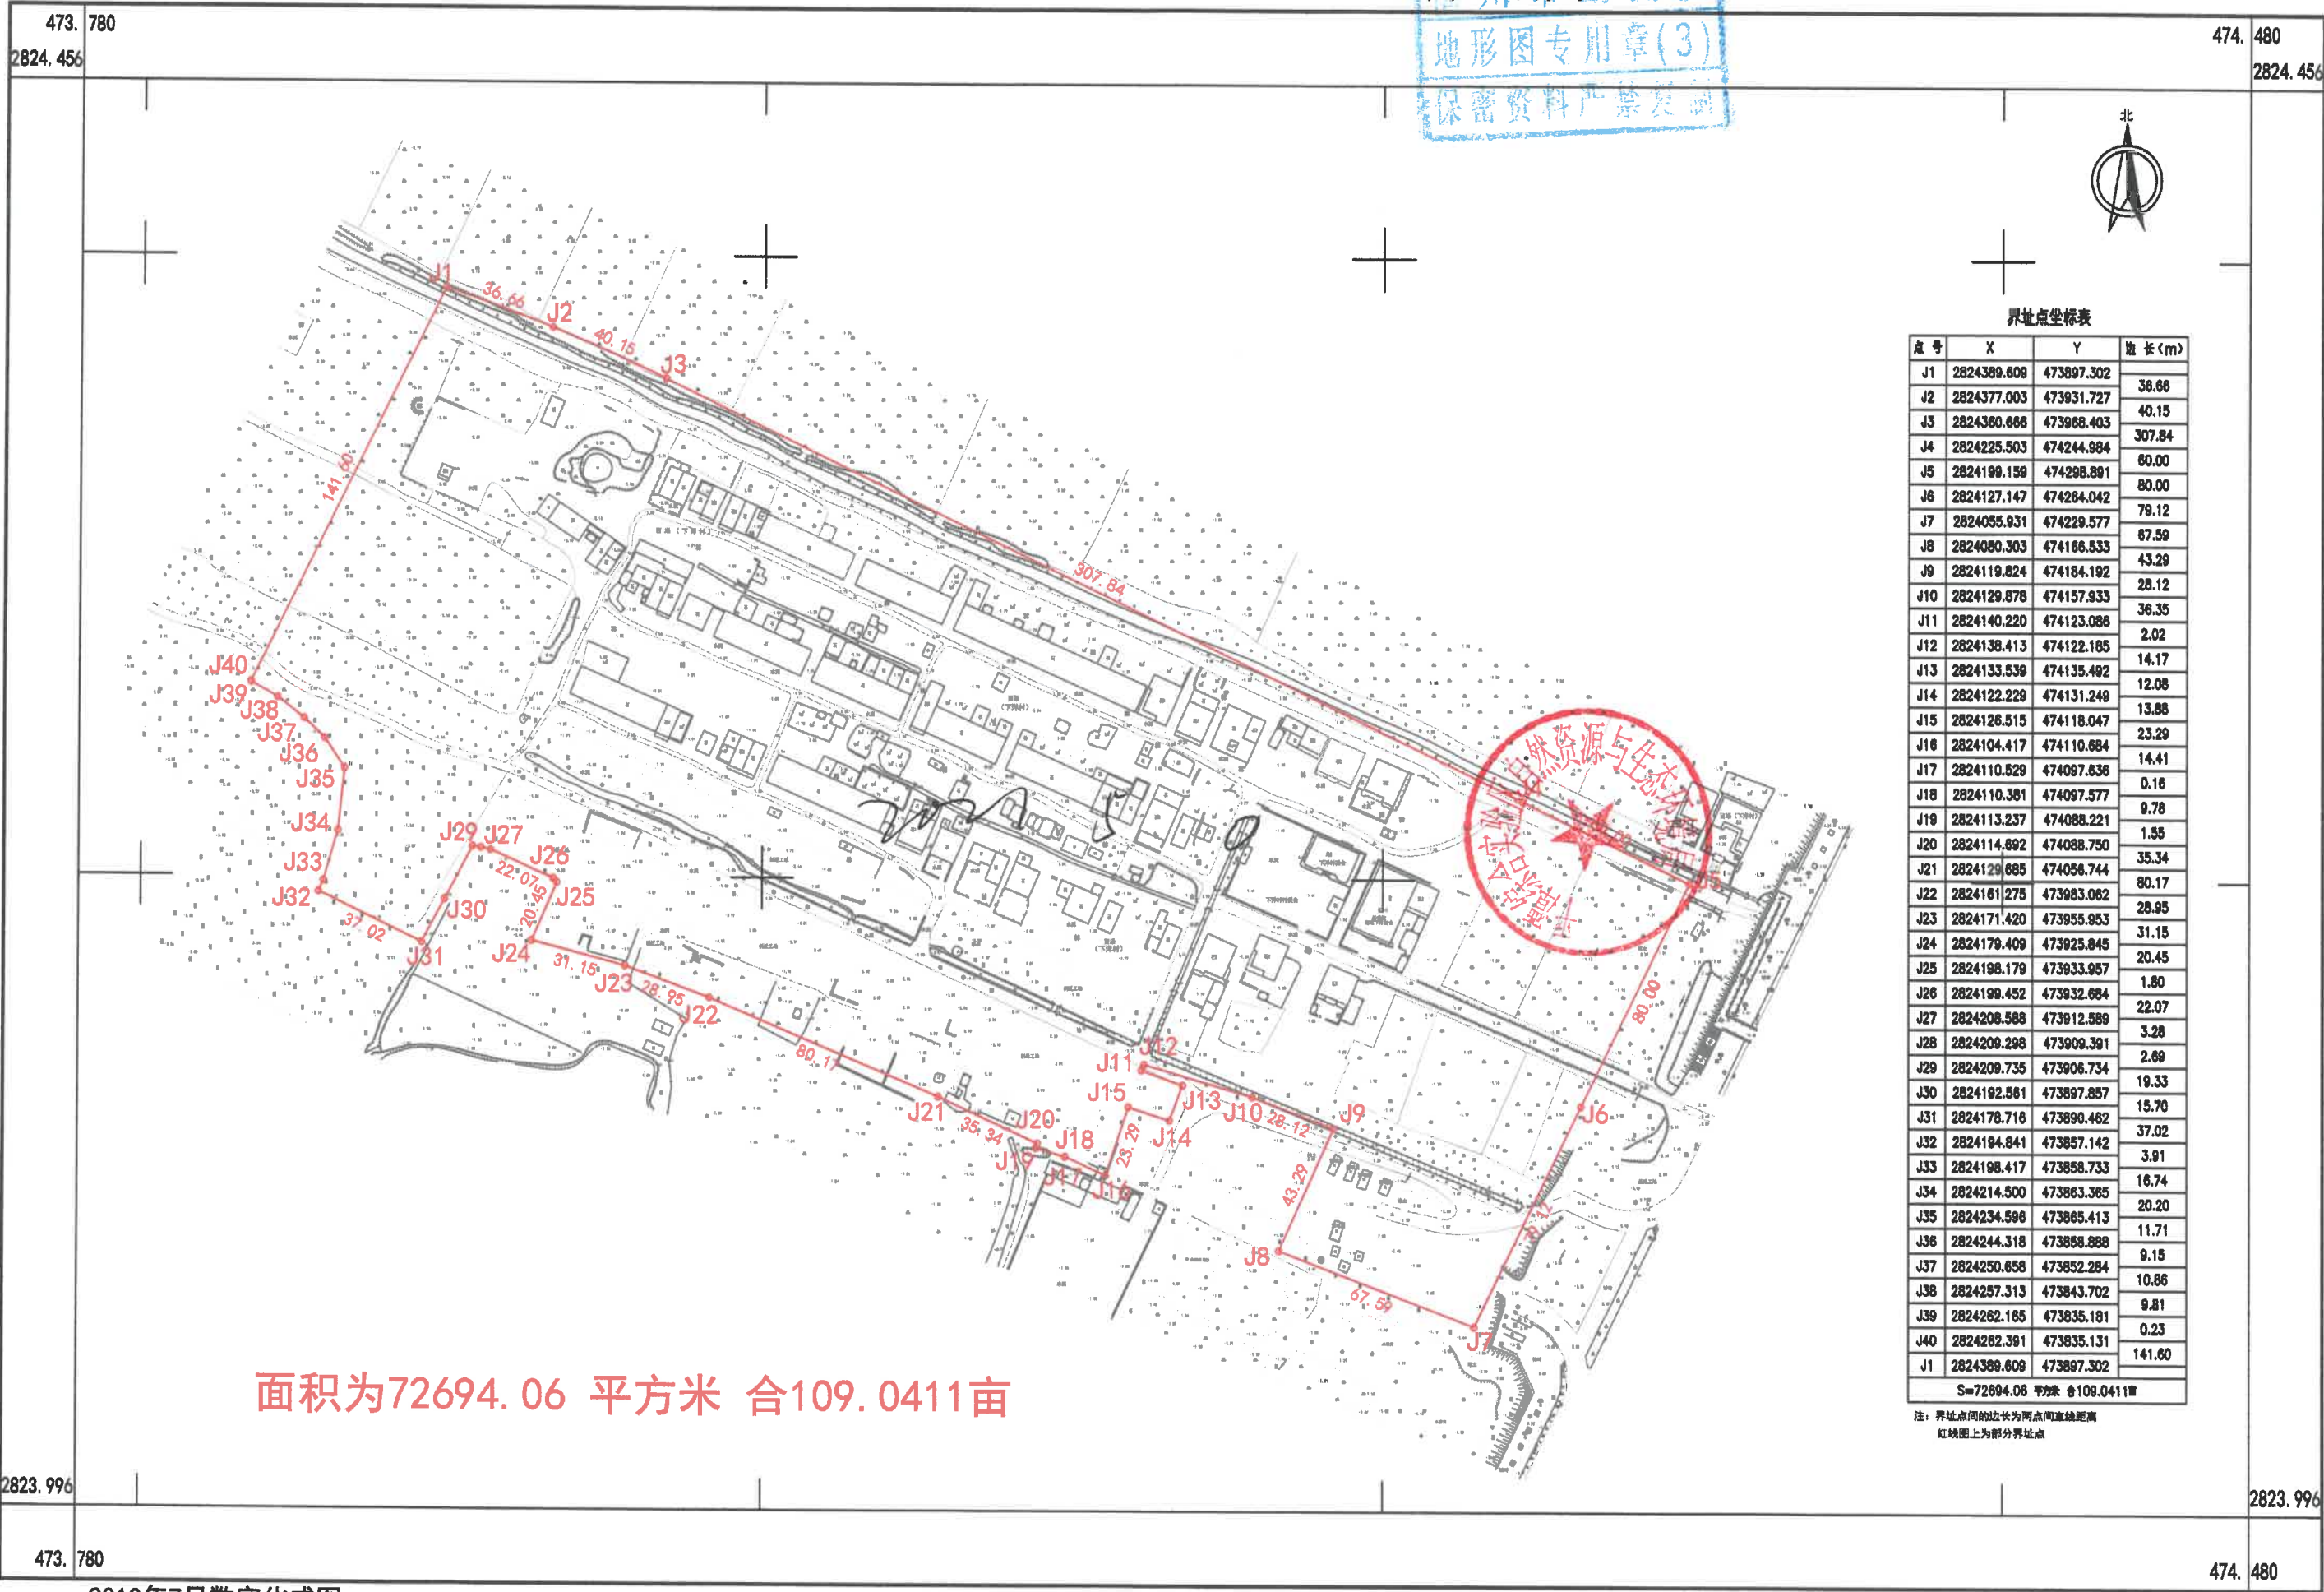

界址点坐标表

点号	X	Y	边长(m)
J1	2824389.608	473897.302	
J2	2824377.003	473831.727	36.66
J3	2824360.666	473968.403	40.15
J4	2824225.503	474244.984	307.84
J5	2824190.159	474298.891	80.00
J6	2824127.147	474284.042	80.00
J7	2824055.931	474229.577	79.12
J8	2824080.303	474166.533	67.59
J9	2824119.824	474184.192	43.29
J10	2824129.878	474157.933	28.12
J11	2824140.220	474123.086	36.35
J12	2824138.413	474122.185	2.02
J13	2824133.539	474135.492	14.17
J14	2824122.229	474131.249	12.08
J15	2824126.515	474118.047	13.88
J16	2824104.417	474110.684	23.29
J17	2824110.529	474097.636	14.41
J18	2824110.381	474097.577	0.16
J19	2824113.237	474088.221	9.78
J20	2824114.692	474088.750	1.55
J21	2824129.685	474056.744	35.34
J22	2824161.275	473983.062	80.17
J23	2824171.420	473955.953	28.95
J24	2824179.409	473925.845	31.15
J25	2824198.179	473933.957	20.45
J26	2824198.452	473932.684	1.80
J27	2824208.588	473912.589	22.07
J28	2824206.298	473909.391	3.28
J29	2824209.735	473906.734	2.69
J30	2824192.561	473897.857	19.33
J31	2824178.716	473890.462	15.70
J32	2824184.841	473857.142	37.02
J33	2824198.417	473858.733	3.91
J34	2824214.500	473863.365	16.74
J35	2824234.596	473865.413	20.20
J36	2824244.318	473856.888	11.71
J37	2824250.658	473852.284	9.15
J38	2824257.313	473843.702	10.86
J39	2824262.165	473835.181	9.81
J40	2824262.391	473835.131	0.23
J1	2824389.608	473897.302	141.60

S=72694.06 平方米 合109.0411亩
注：界址点间的边长为两点点间直线距离
红线图上为部分界址点