


# 福建省平潭及闽江口水资源配置（一闸三线）工程（平潭段）金井湾管道项目选址红线图

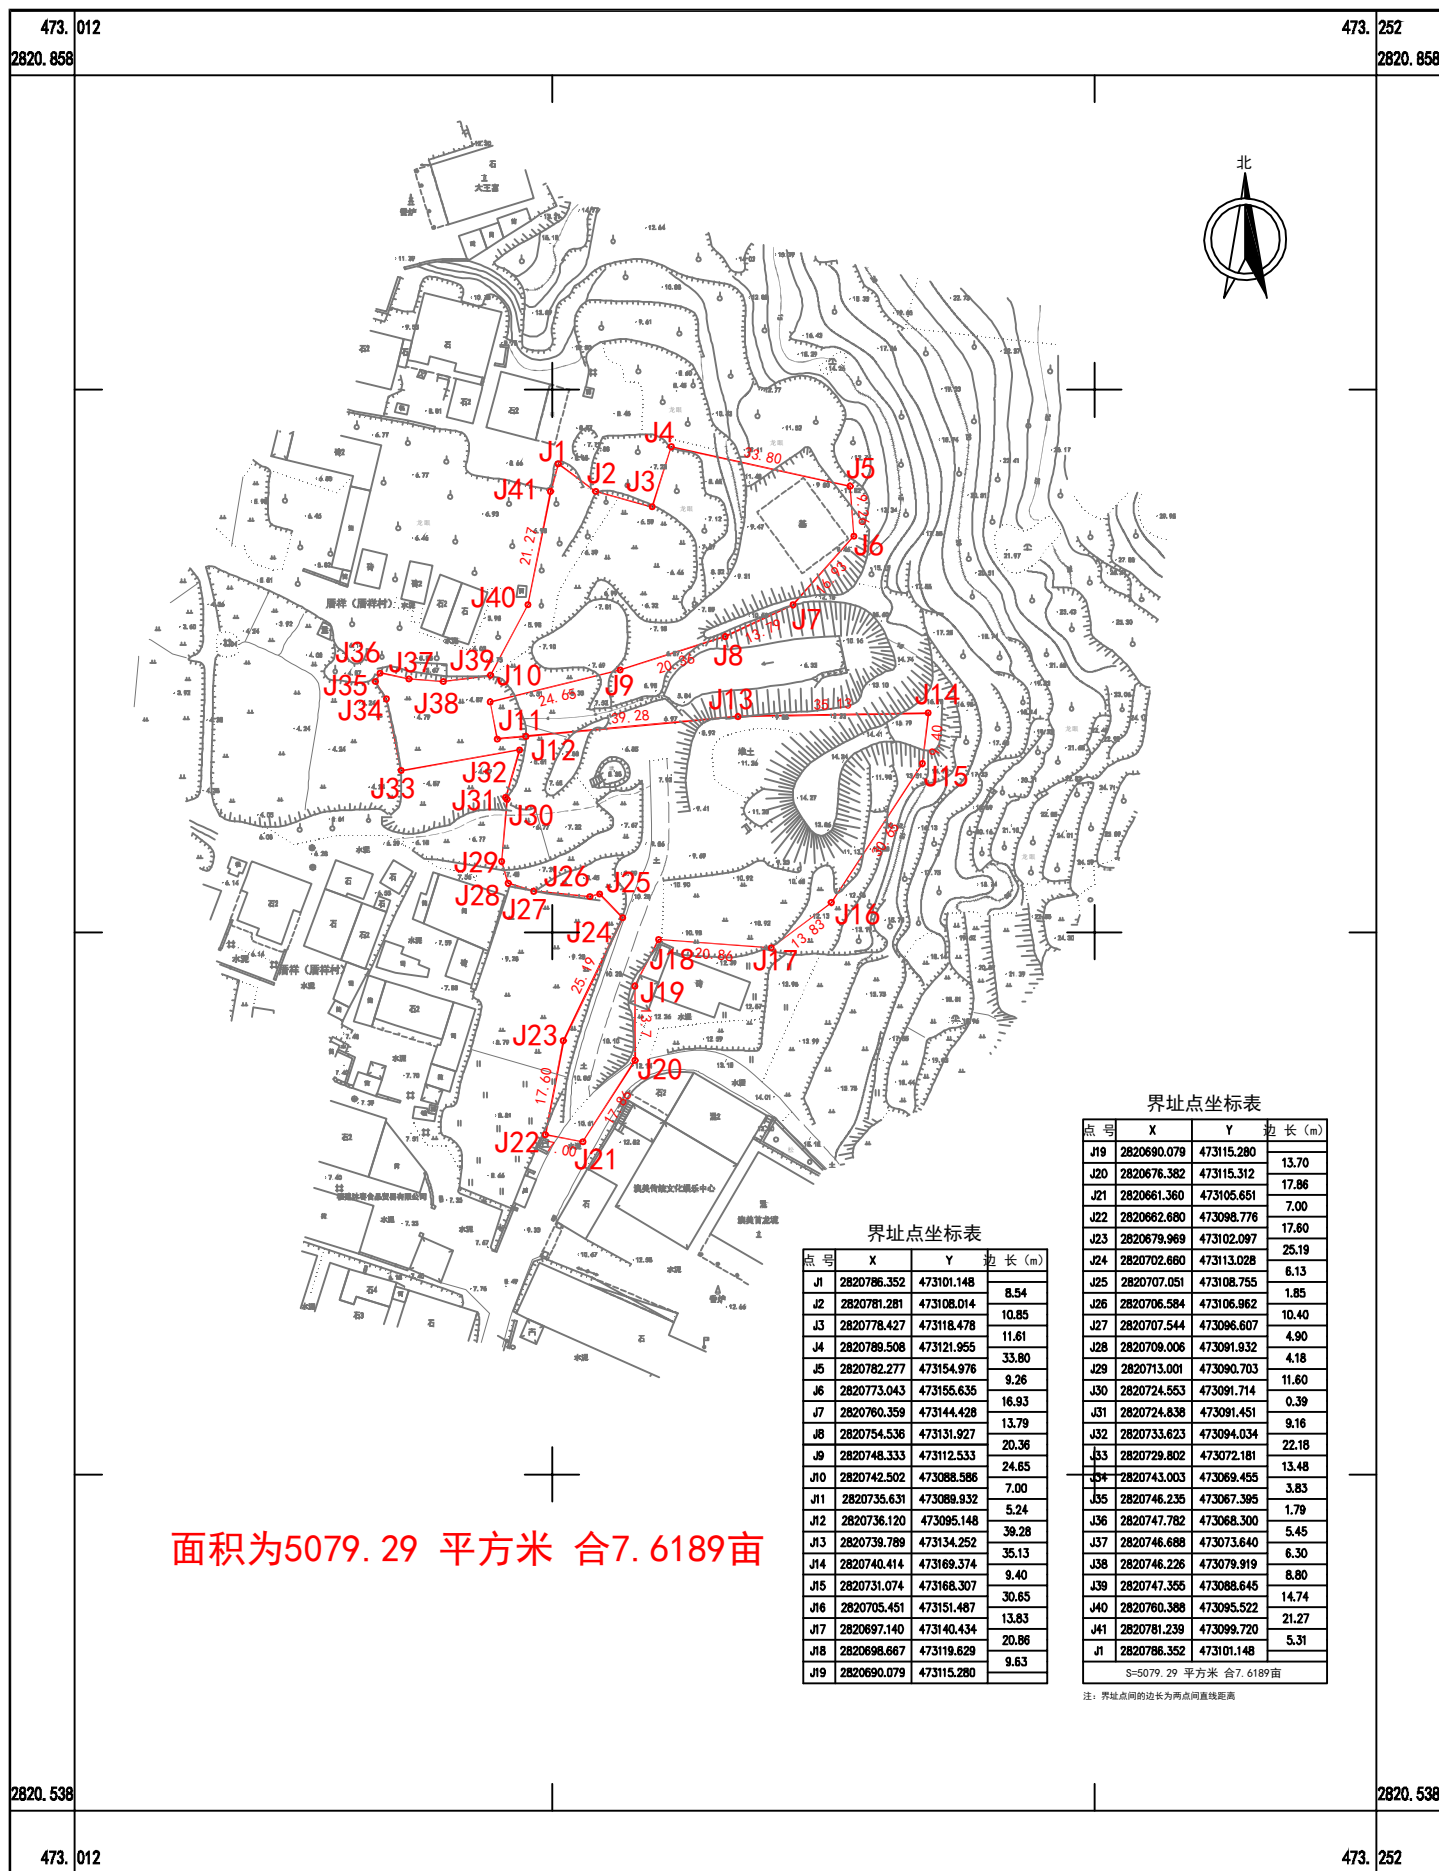

2010年7月数字化成图  
2000国家大地坐标系  
1985国家高程基准  
2009年福州基础地理信息数据图式  
加盖福州市勘测院地形图蓝章，方为正式材料

1:1000