

平潭综合实验区潭城管理单元金峰路与竹屿湖东路交叉口 西北侧地块控制性详细规划


01.区域位置图



规划范围于平潭岛中的位置




规划范围于潭城组团中的位置

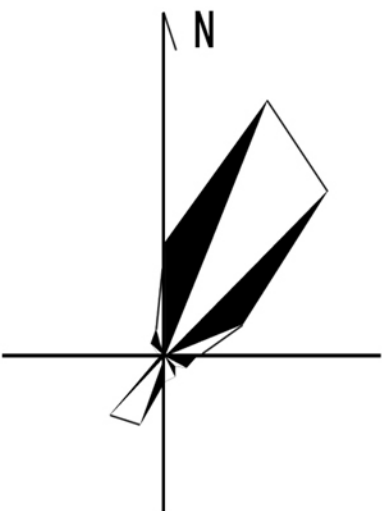

平潭综合实验区潭城管理单元金峰路与竹屿湖东路交叉口
西北侧地块控制性详细规划

03.用地规划图

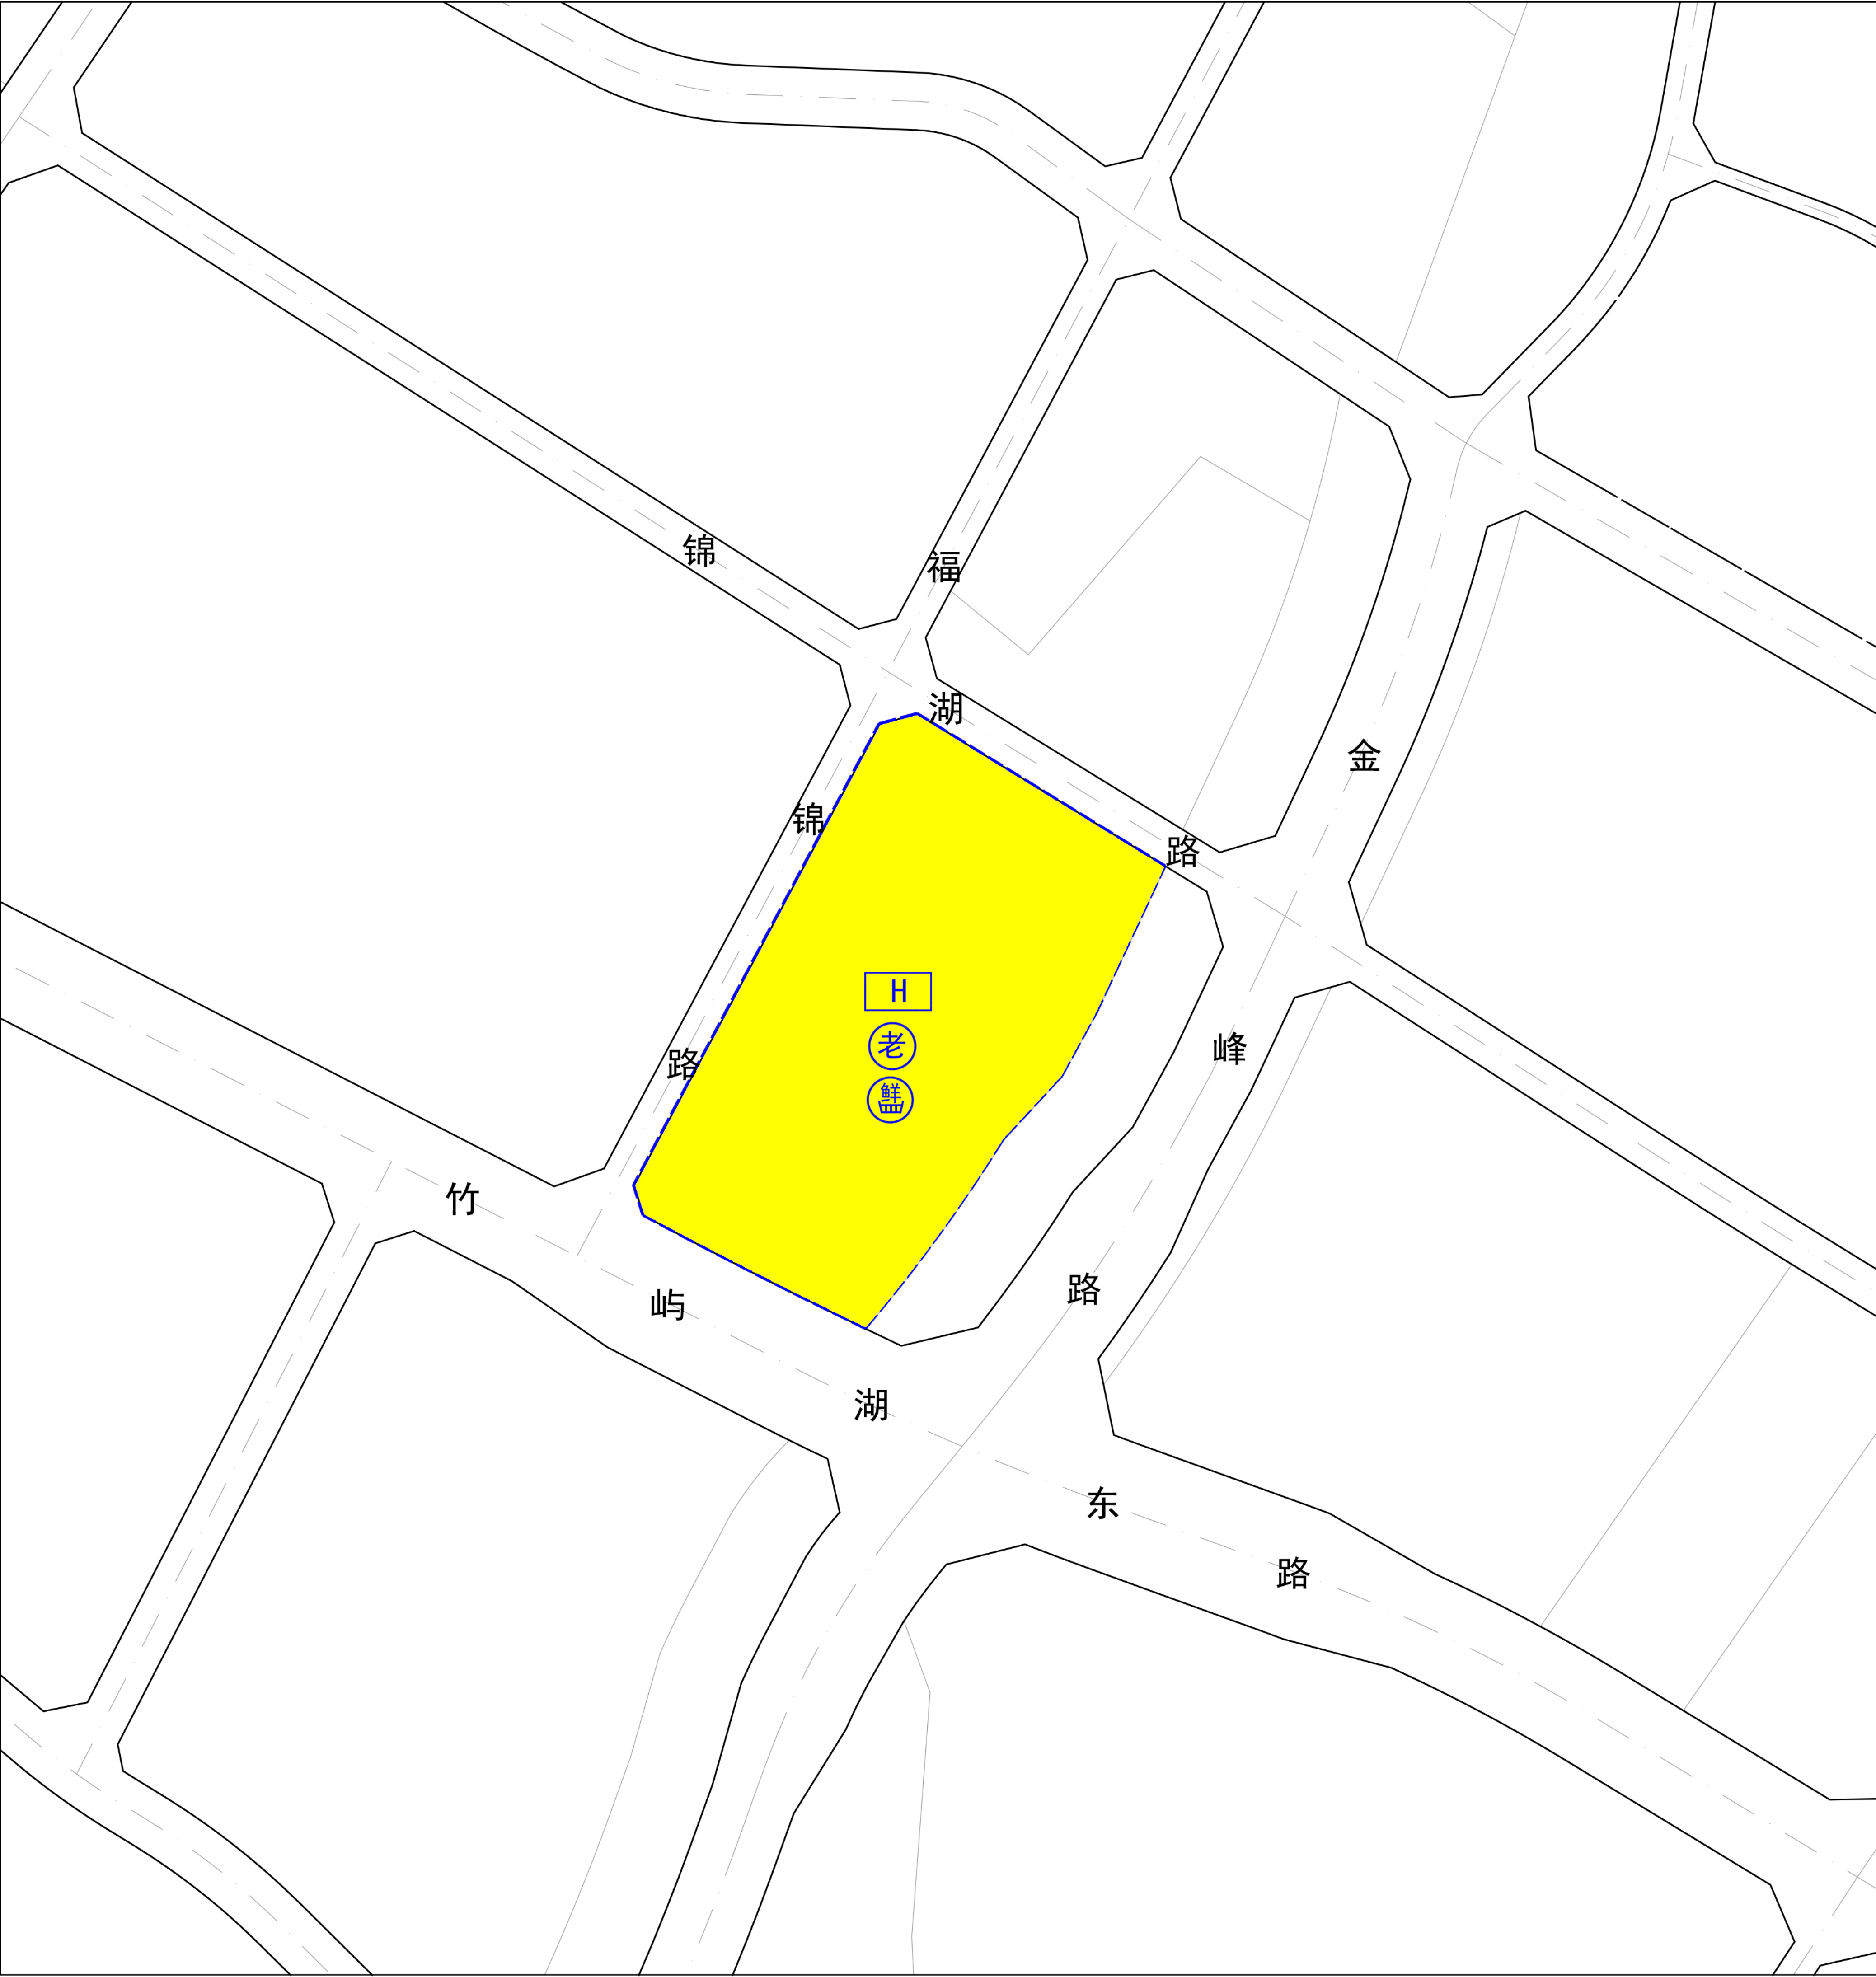




二类城镇住宅用地

城市道路

规划范围

厦门市城市规划设计研究院有限公司 | 厦门市规划院（平潭）规划设计有限公司 | 2022

平潭综合实验区潭城管理单元金峰路与竹屿湖东路交叉口西南侧地块控制性详细规划

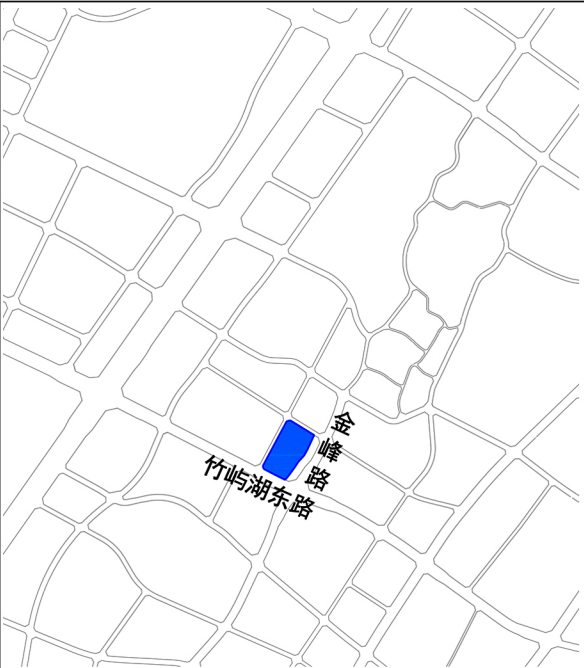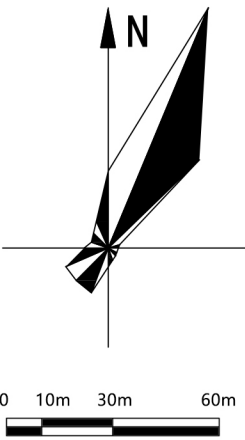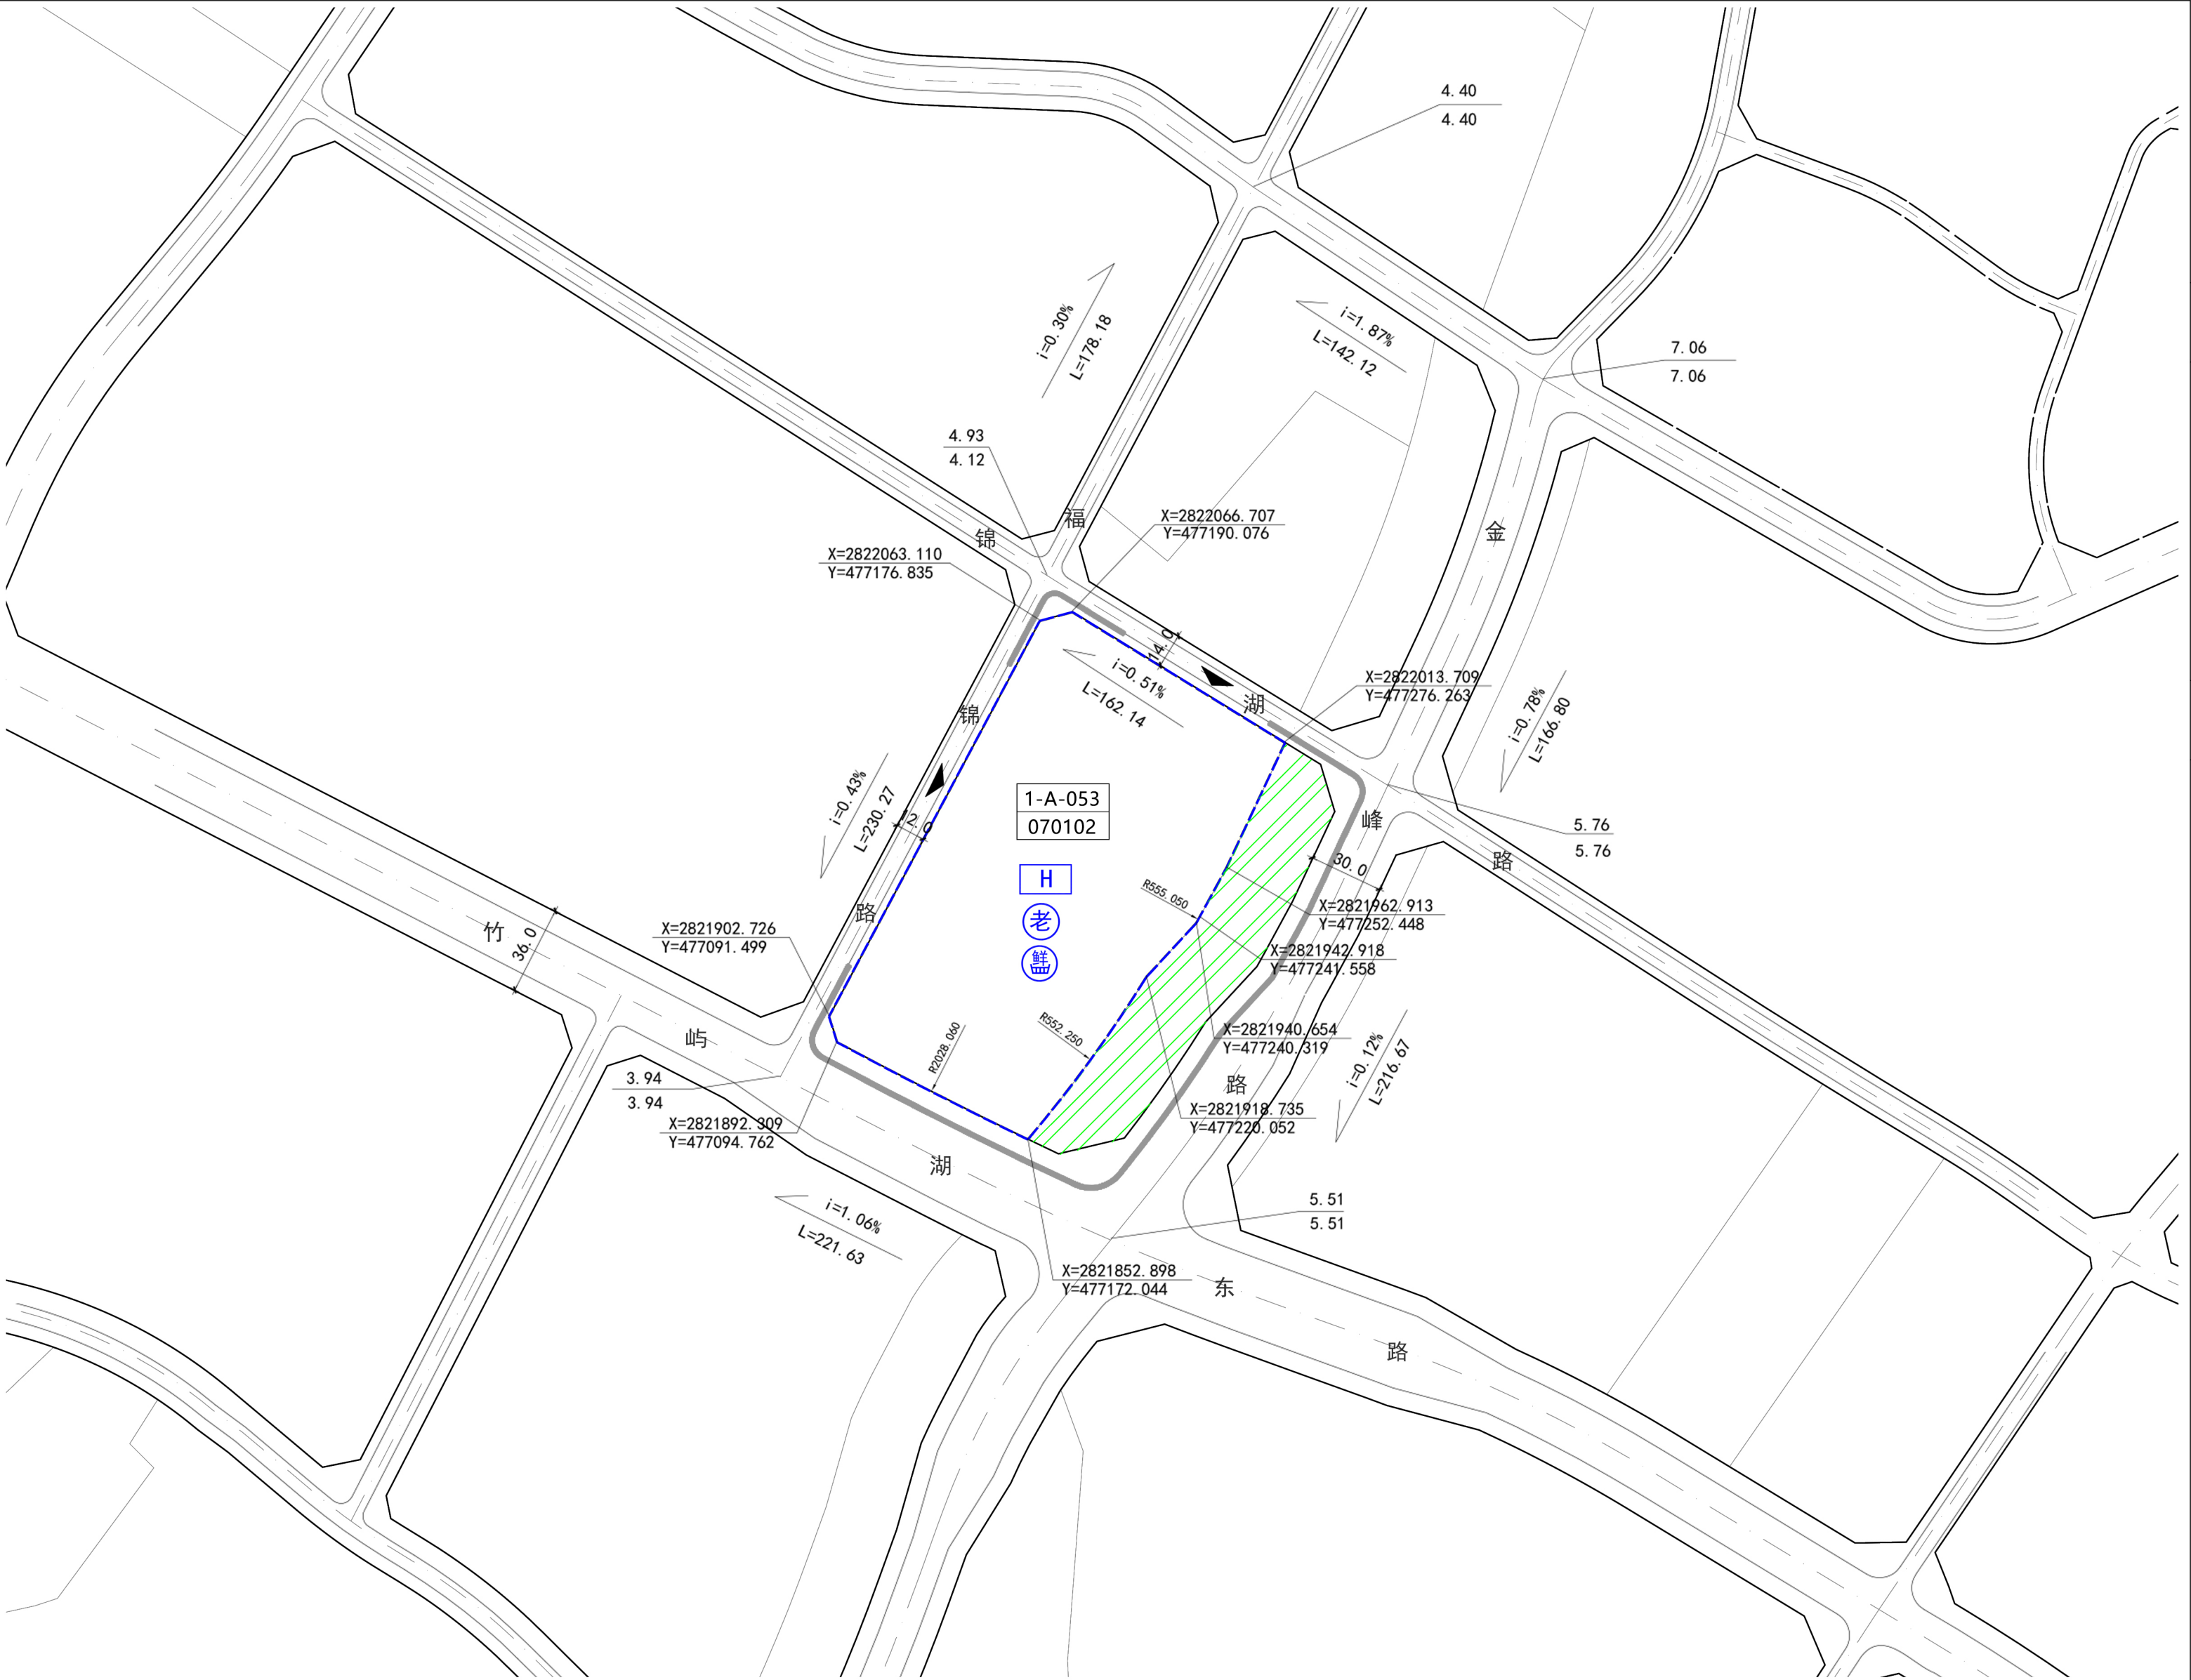

图例

- 地块控制点坐标
- 城市道路
- 规划范围
- 道路红线宽度
- 坡度-坡向-坡长
- 道路规划标高
- 道路现状标高
- 禁止机动车开口线
- 绿地
- 机动车出入口
- 地块编号
用地性质
- 10kV环网站
- 综合为老服务中心
- 生鲜超市便利店

规划控制条文

- 1、规划地块用地性质为二类城镇住宅用地，用地面积约2.09公顷。不得随意更改地块用地规模和位置。
- 2、“五线”属于强制性内容，其线位、规模及性质一经确定不得擅自调整。
道路红线：竹屿湖东路，道路宽度36米；金峰路，道路宽度30米；锦湖路，道路宽度14米；福锦路，宽度宽度12米。
城市绿线：金峰路西侧绿地，宽度30米。
- 3、“三大设施”控制应按照《福建省城市规划管理技术规定》（2017）公共服务设施配置标准，具体指标如下：
1-A-053地块配建1处综合为老服务中心，套内建筑面积不小于1000平方米；1处生鲜超市便利店，套内建筑面积不小于200平方米；1处10kV环网站，套内建筑面积不小于50平方米。
- 4、配套设施的项目、数量和用地或建筑面积不得少于规划的规定，如有变更，必须申报城乡行政主管部门批准。
- 5、建筑间距须符合日照、防火、消防、抗震、环保、工程管线和文物、建筑保护等方面的要求，同时还应满足《福建省城市规划管理技术规定》（2017）中的建筑间距控制要求。
- 6、地块出入口及配建停车位应满足《福建省城市规划管理技术规定》（2017）要求。
- 7、地块城市设计应注重于周边城市主次干路的关系；竖向及市政工程管线规划应与周边道路的竖向及工程管线相衔接；图中道路的线位、断面形式、交叉口形式、控制点标高及具体位置均以批准的工程方案为准。
- 8、地块图则未涉及的其它规划要求由平潭综合实验区自然资源与生态环境局根据相关规定确定并执行。

地块控制指标表	地块编号	用地代码	用地性质	用地面积（平方米）	建筑面积（平方米）	容积率	建筑密度（%）	绿地率（%）	建筑限高（米）	配建设施
	1-A-053	070102	二类城镇住宅用地	20925.512	≤46036	≤2.2	≤30	≥35	80	鲜老H
备注	控制指标未明确的市政公用设施、交通设施等地块，可按照相关行业标准要求或者行业主管部门意见确定具体项目用地、建设规模及规划控制指标等，作为审批依据。									

图名

地块编码及图则

编制单位

厦门市城市规划设计研究院有限公司
厦门市规划院（平潭）规划设计有限公司

图号

12

日期

2022.04