


平潭综合实验区平原管理单元平潭青峰二期风电场项目 控制性详细规划


01.区域位置图



规划范围于平潭岛中的位置

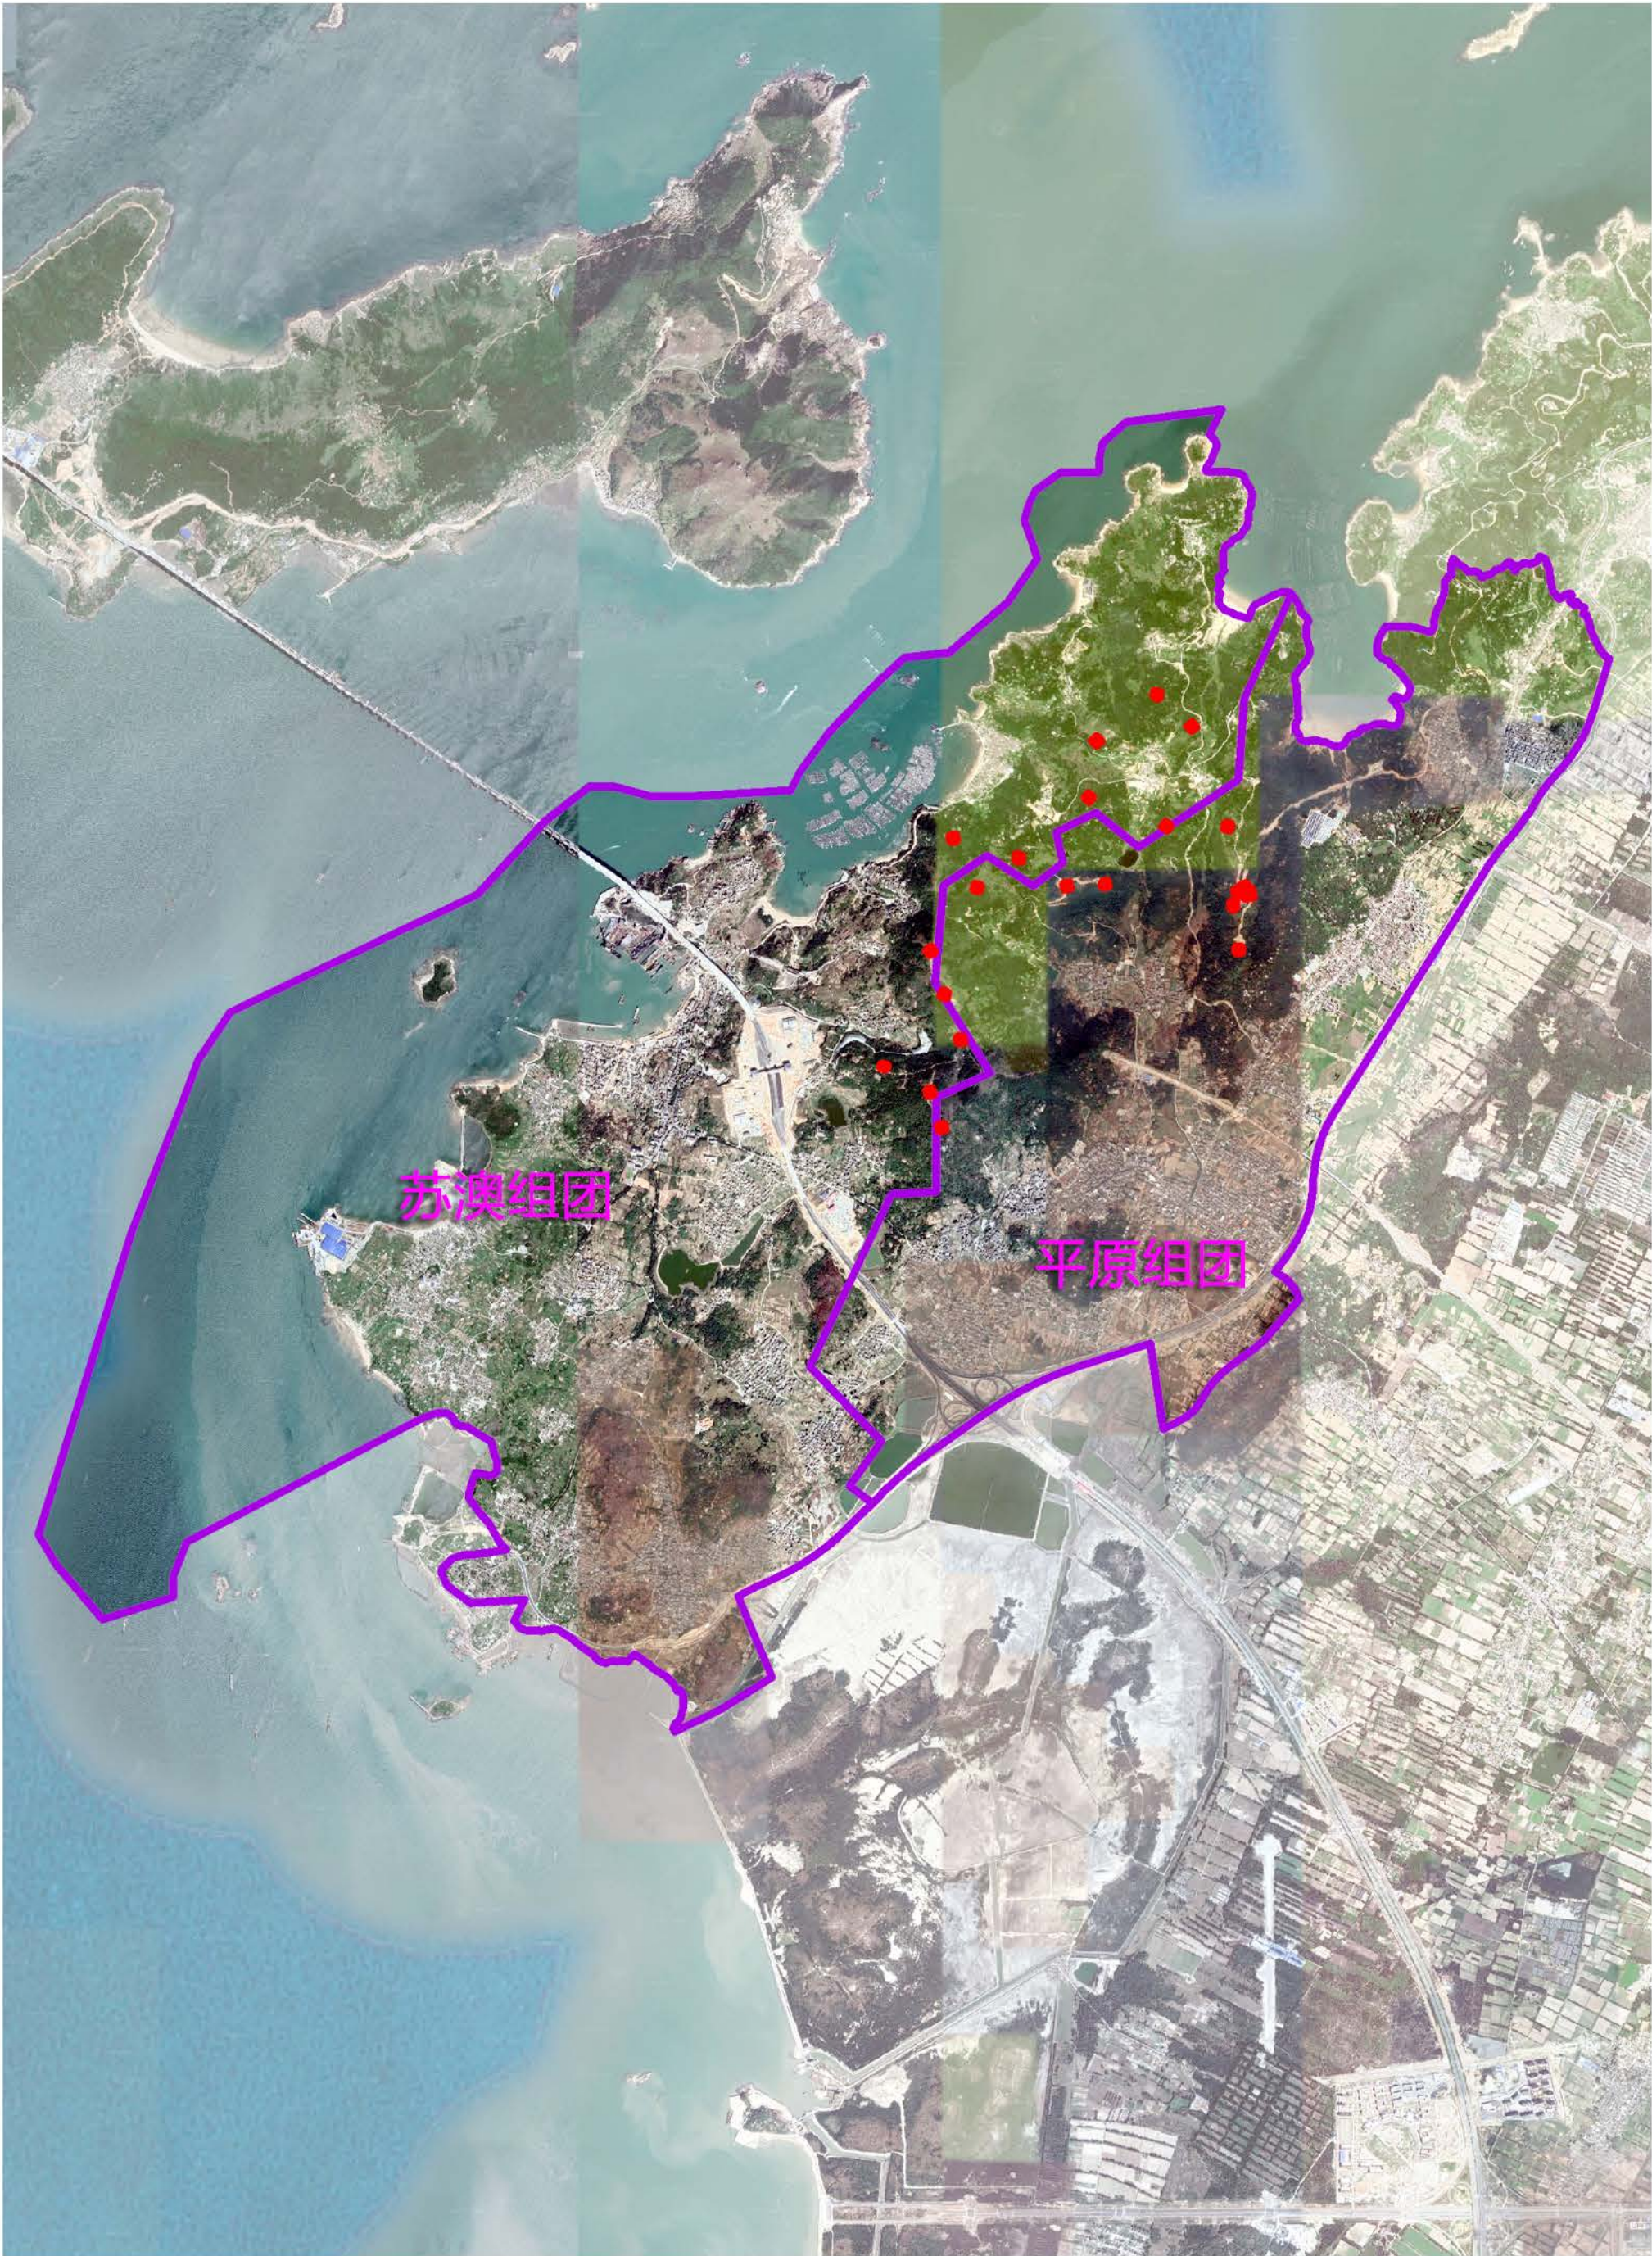


规划范围于平原组团与苏澳组团中的位置

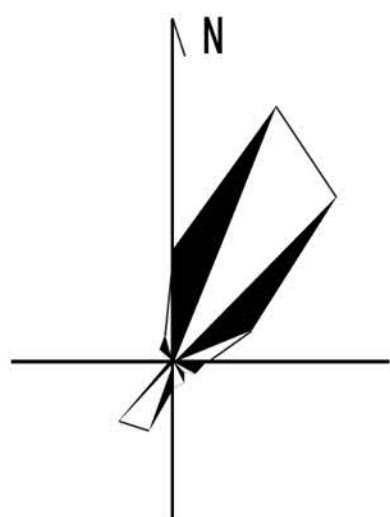

平潭综合实验区平原管理单元平潭青峰二期风电场项目 控制性详细规划


03.用地规划图


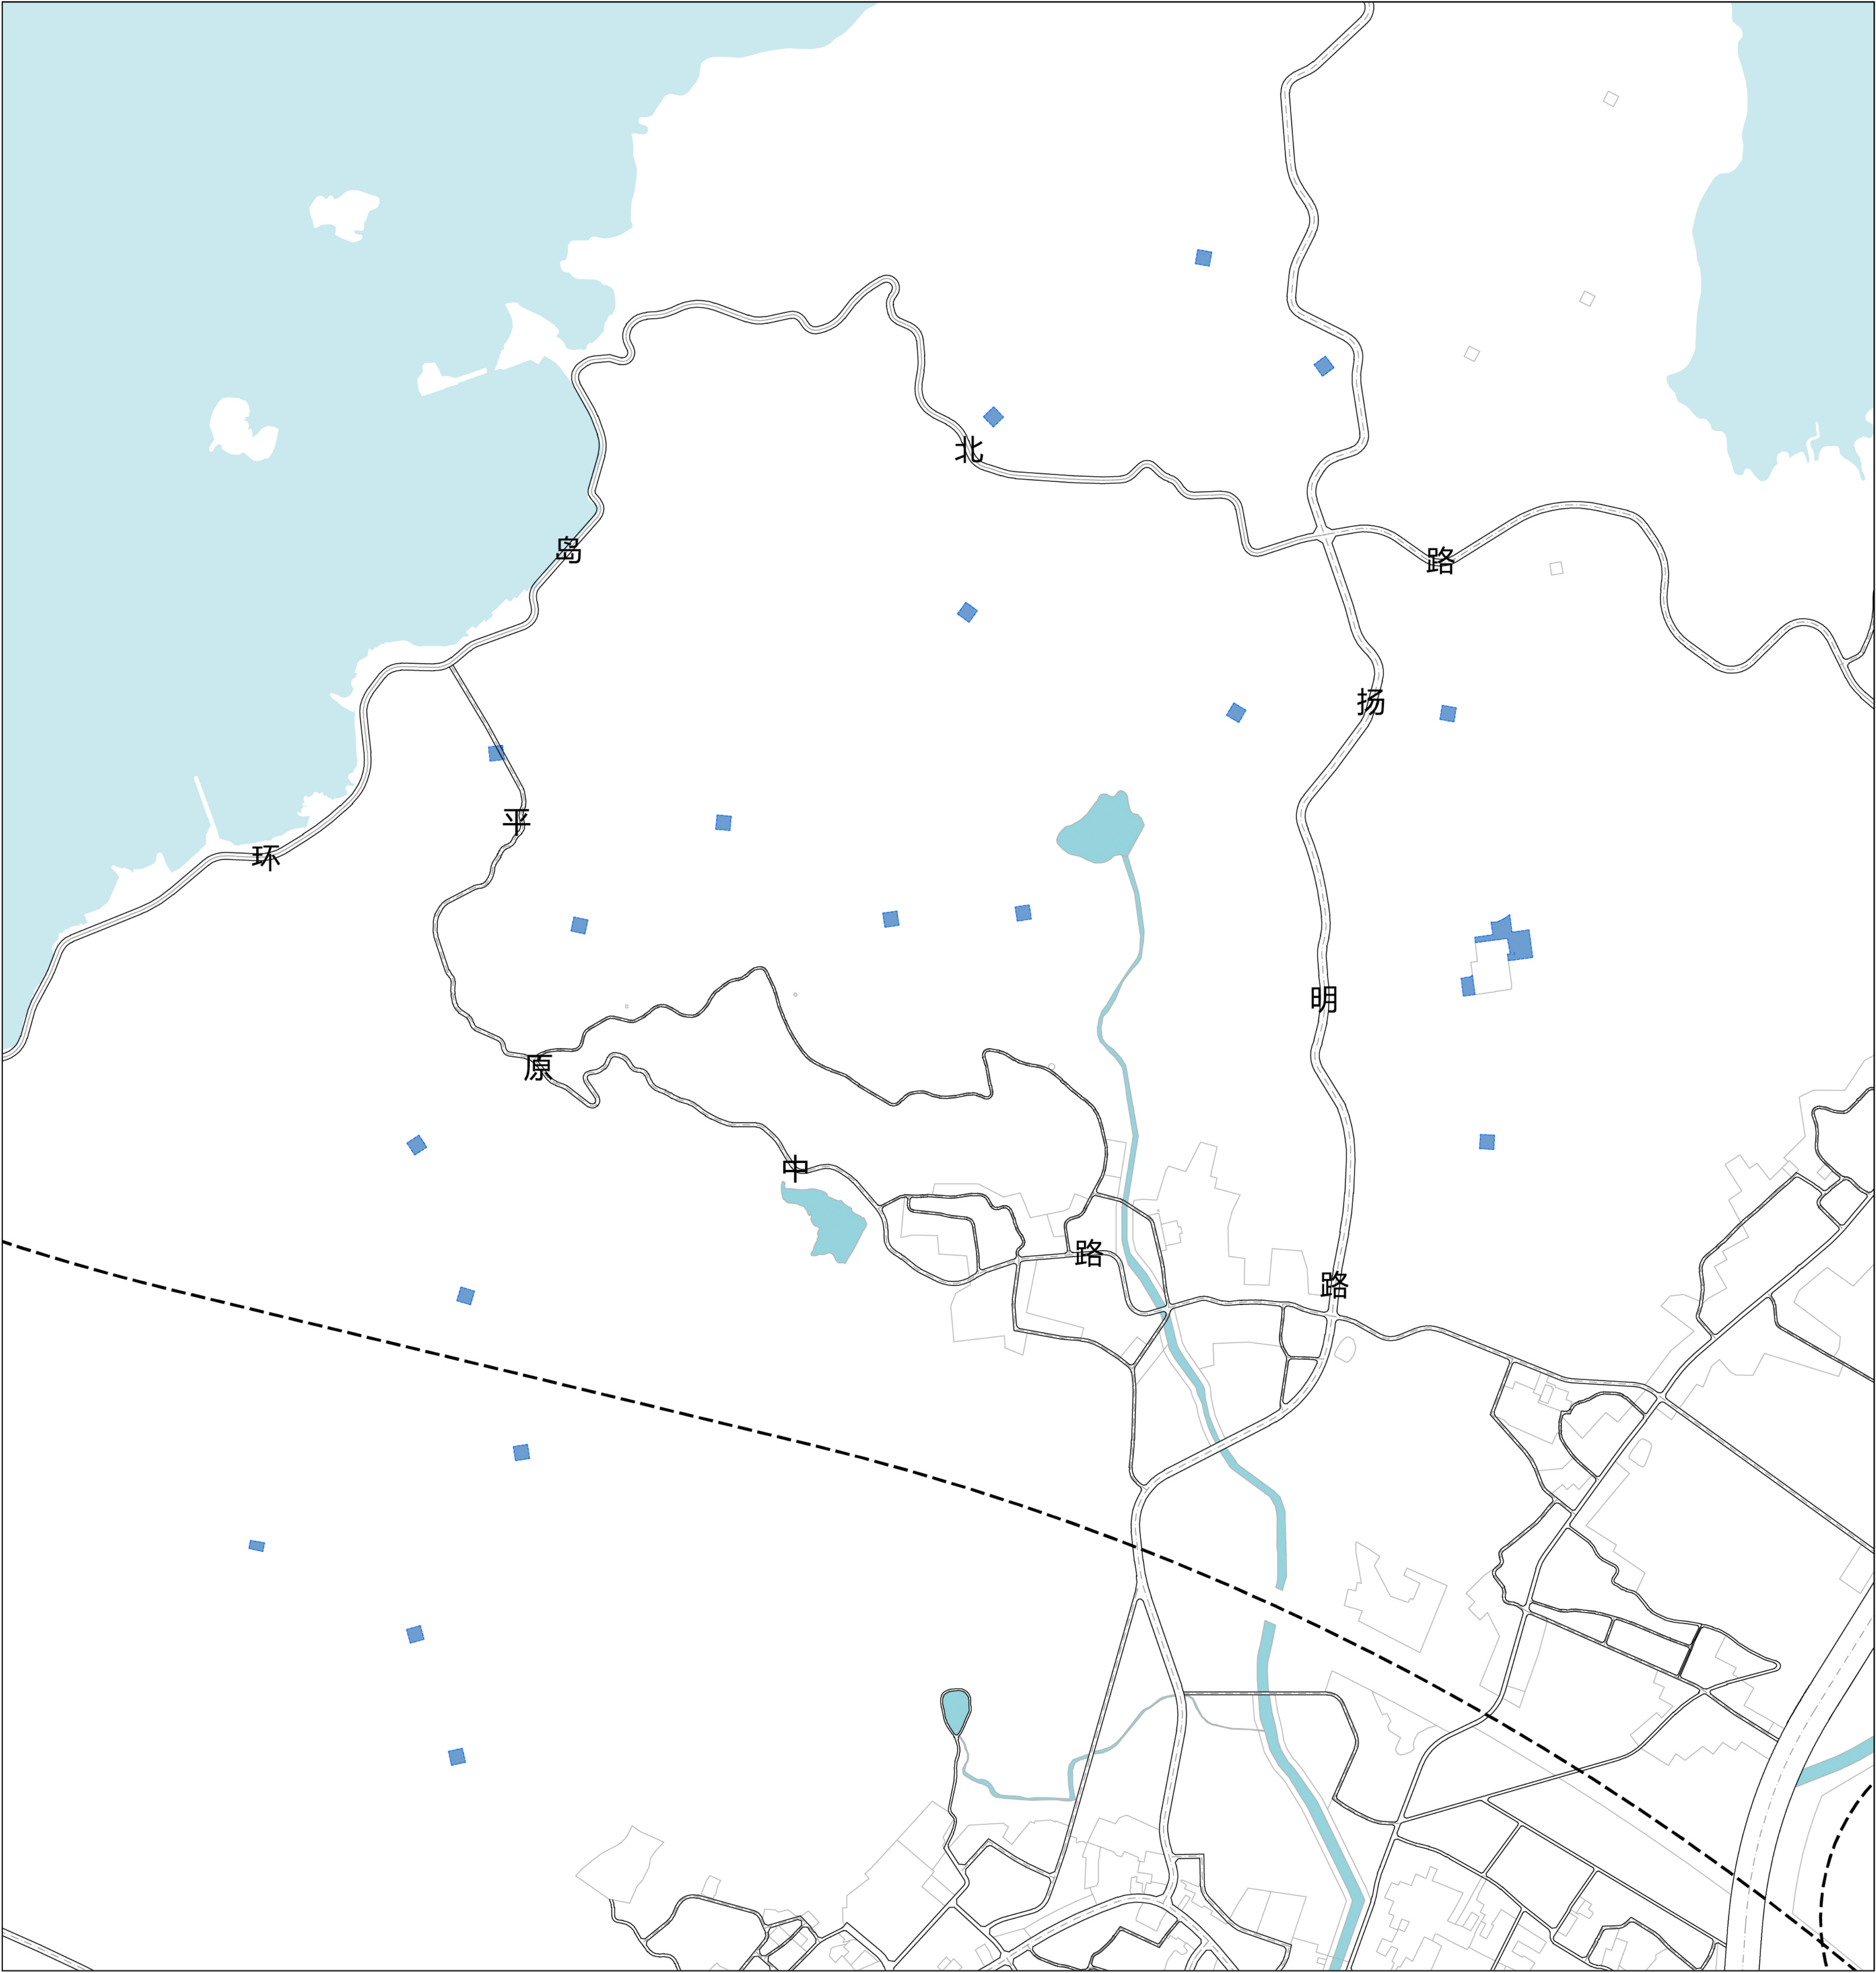


- 供电用地
- 陆地水域
- 城市道路
- 规划范围

厦门市城市规划设计研究院有限公司 | 厦门市规划院（平潭）规划设计有限公司 | 2022

平潭综合实验区平原管理单元平潭青峰二期风电场项目控制性详细规划

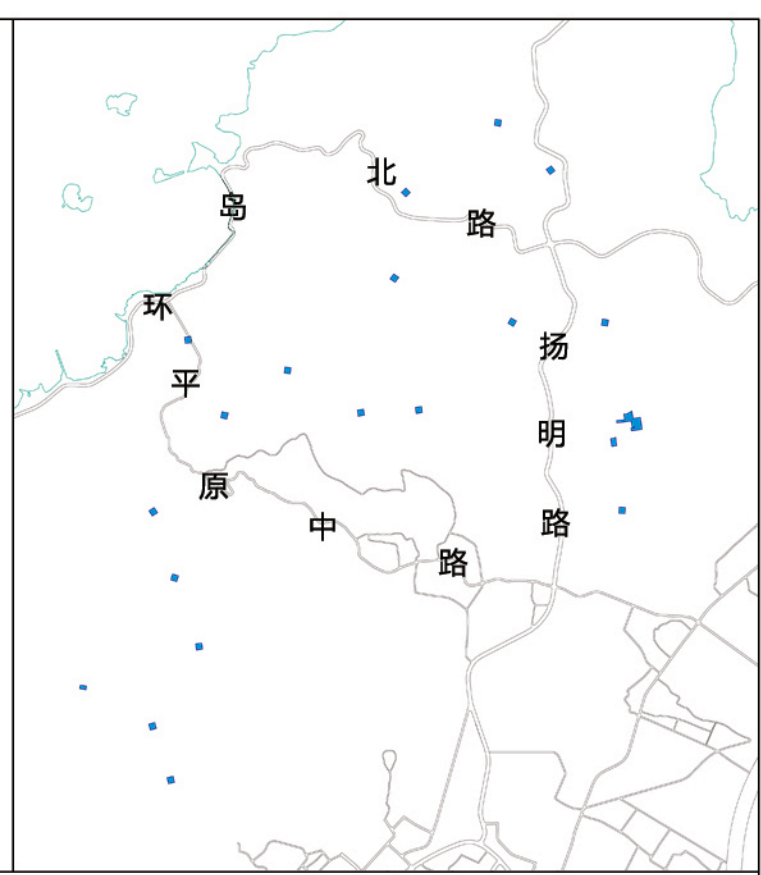

  	地块控制点坐标		禁止机动车开口线
	城市道路		水域
	规划范围		绿地
	道路红线宽度		机动车出入口
	坡度-坡向-坡长		地块编号
	道路规划标高 道路现状标高		用地性质

- 1、规划地块用地性质为供电用地，用地面积约1.49公顷。不得随意更改地块用地规模和位置。
- 2、“五线”属于强制性内容，其线位、规模及性质一经确定不得擅自调整。

道路红线：扬明路红线宽度15米；环岛北路红线宽度12米；平原中路红线宽度7米。

- 3、建筑间距须符合日照、防火、消防、抗震、环保、工程管线和文物、建筑保护等方面的要求，同时还应满足《福建省城市规划管理技术规定》（2017）中的建筑间距控制要求。
- 4、地块出入口及配建停车位应满足《福建省城市规划管理技术规定》（2017）要求。
- 5、地块城市设计应注重于周边城市主次干路的关系；竖向及市政工程管线规划应与周边道路的竖向及工程管线相衔接；图中道路的线位、断面形式、交叉口形式、控制点标高及具体位置均以批准的工程方案为准。
- 6、地块图则未涉及的其它规划要求由平潭综合实验区自然资源与生态环境局根据相关规定确定并执行。

地块控制指标表	地块编号	用地代码	用地性质	用地面积（平方米）	建筑面积（平方米）	容积率	建筑密度（%）	绿地率（%）	建筑限高（米）	配套设施	图名	地块编码及图则		
	14-A-02	1303	供电用地	14924.007	——	——	——	——	——	——	编制单位	厦门市城市规划设计研究院有限公司 厦门市规划院（平潭）规划设计有限公司		
											图号	06	日期	2022.04
备注	控制指标未明确的市政公用设施、交通设施等地块，可按照相关行业标准要求或者行业主管部门意见确定具体项目用地、建设规模及规划控制指标等，作为审批依据。													