

平潭综合实验区北部生态廊道游客服务中心地块 控制性详细规划


01.区域位置图



规划地块在平潭岛中的位置





规划地块在ZC-03管理单元中的位置

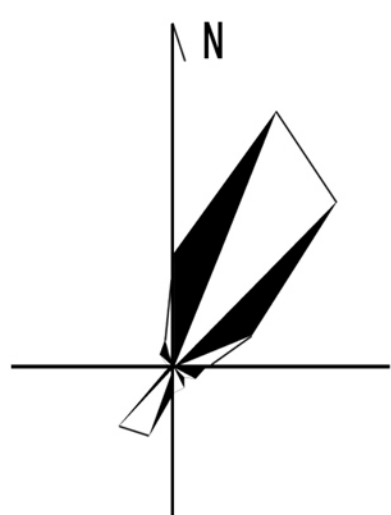




平潭综合实验区北部生态廊道游客服务中心地块 控制性详细规划

03.用地规划图

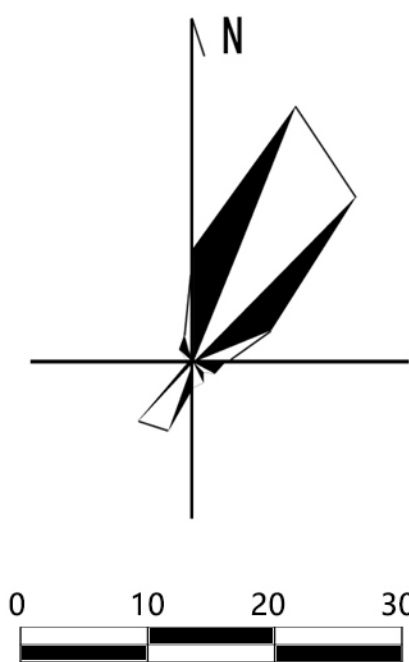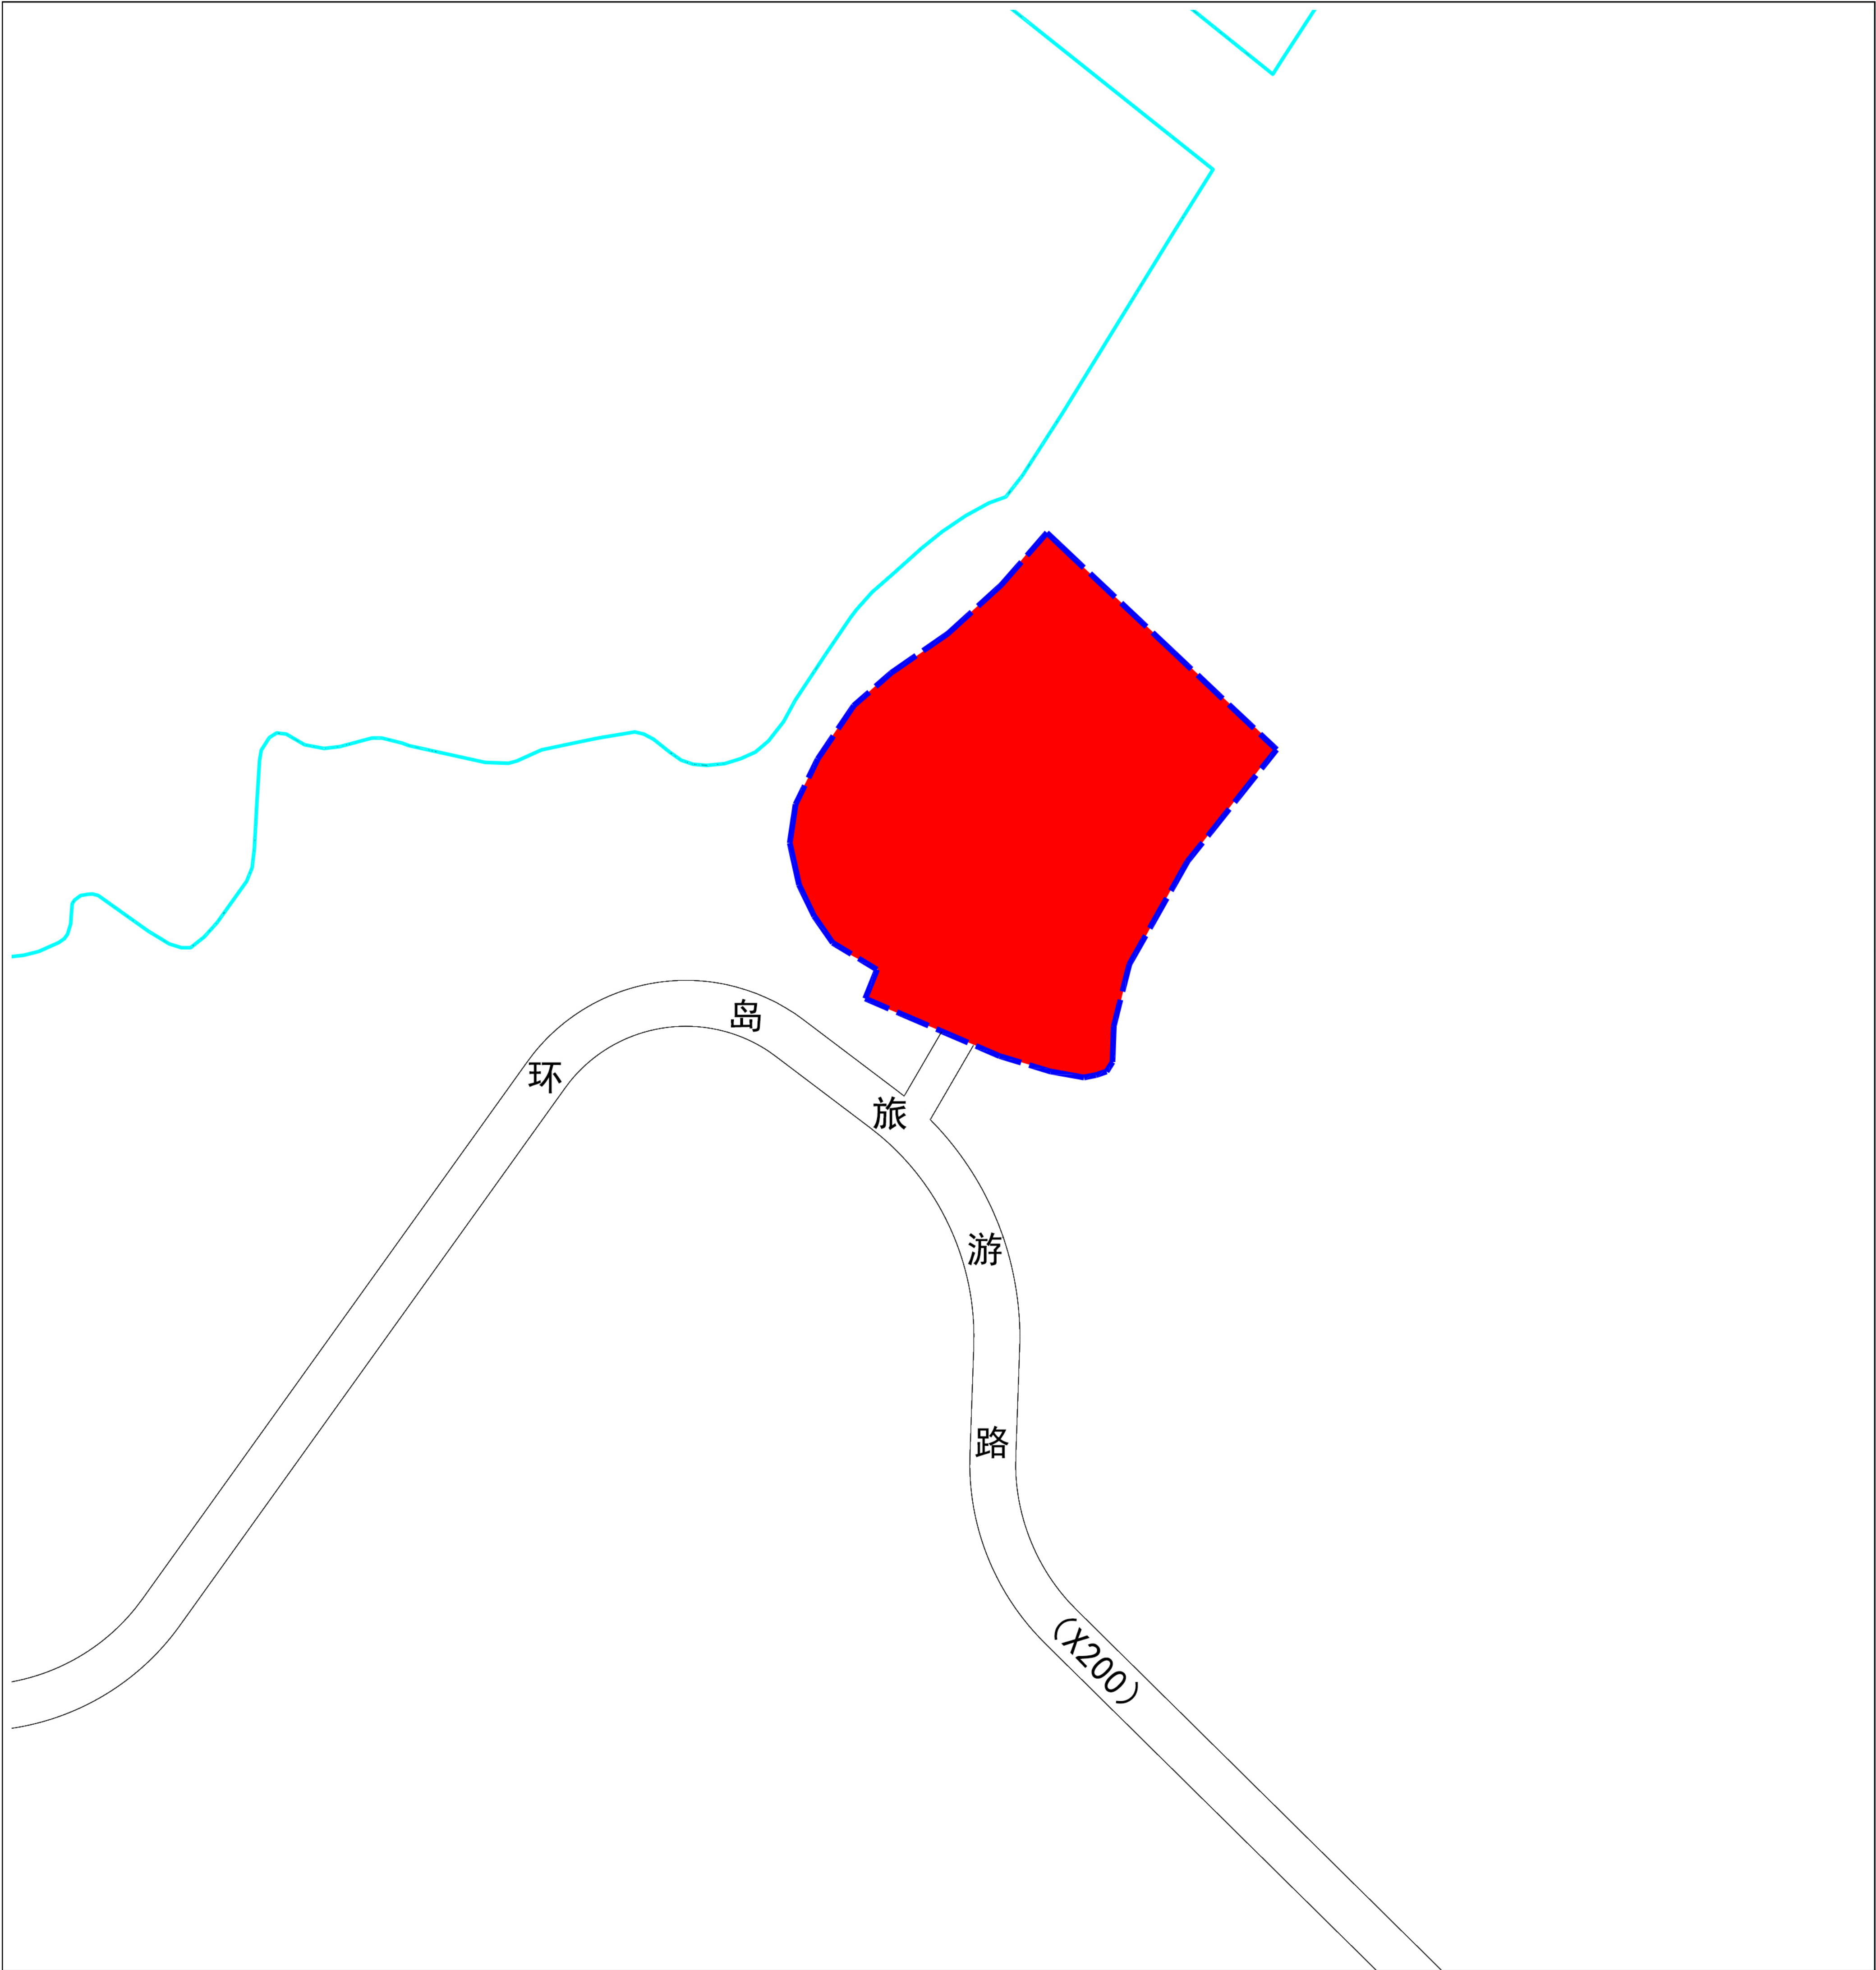


- 商业用地
- 岸线
- 农村公路
- 规划范围

平潭综合实验区北部生态廊道游客服务中心地块控制性详细规划

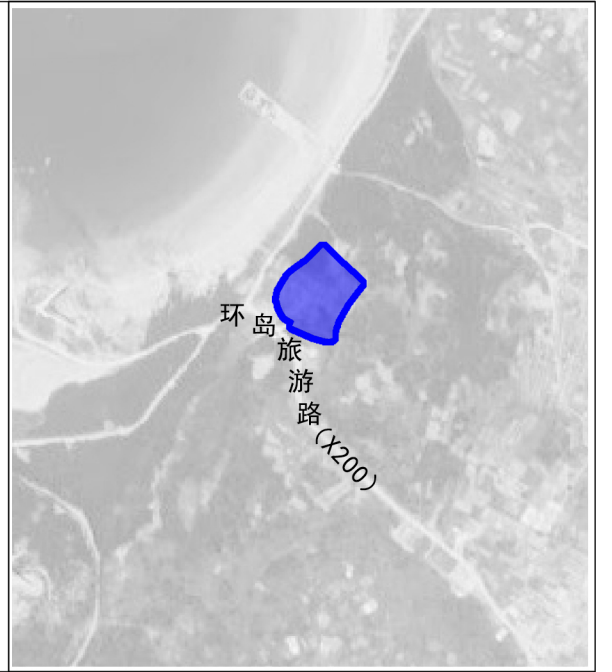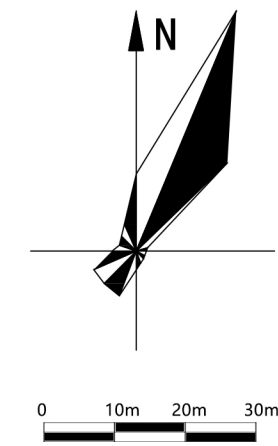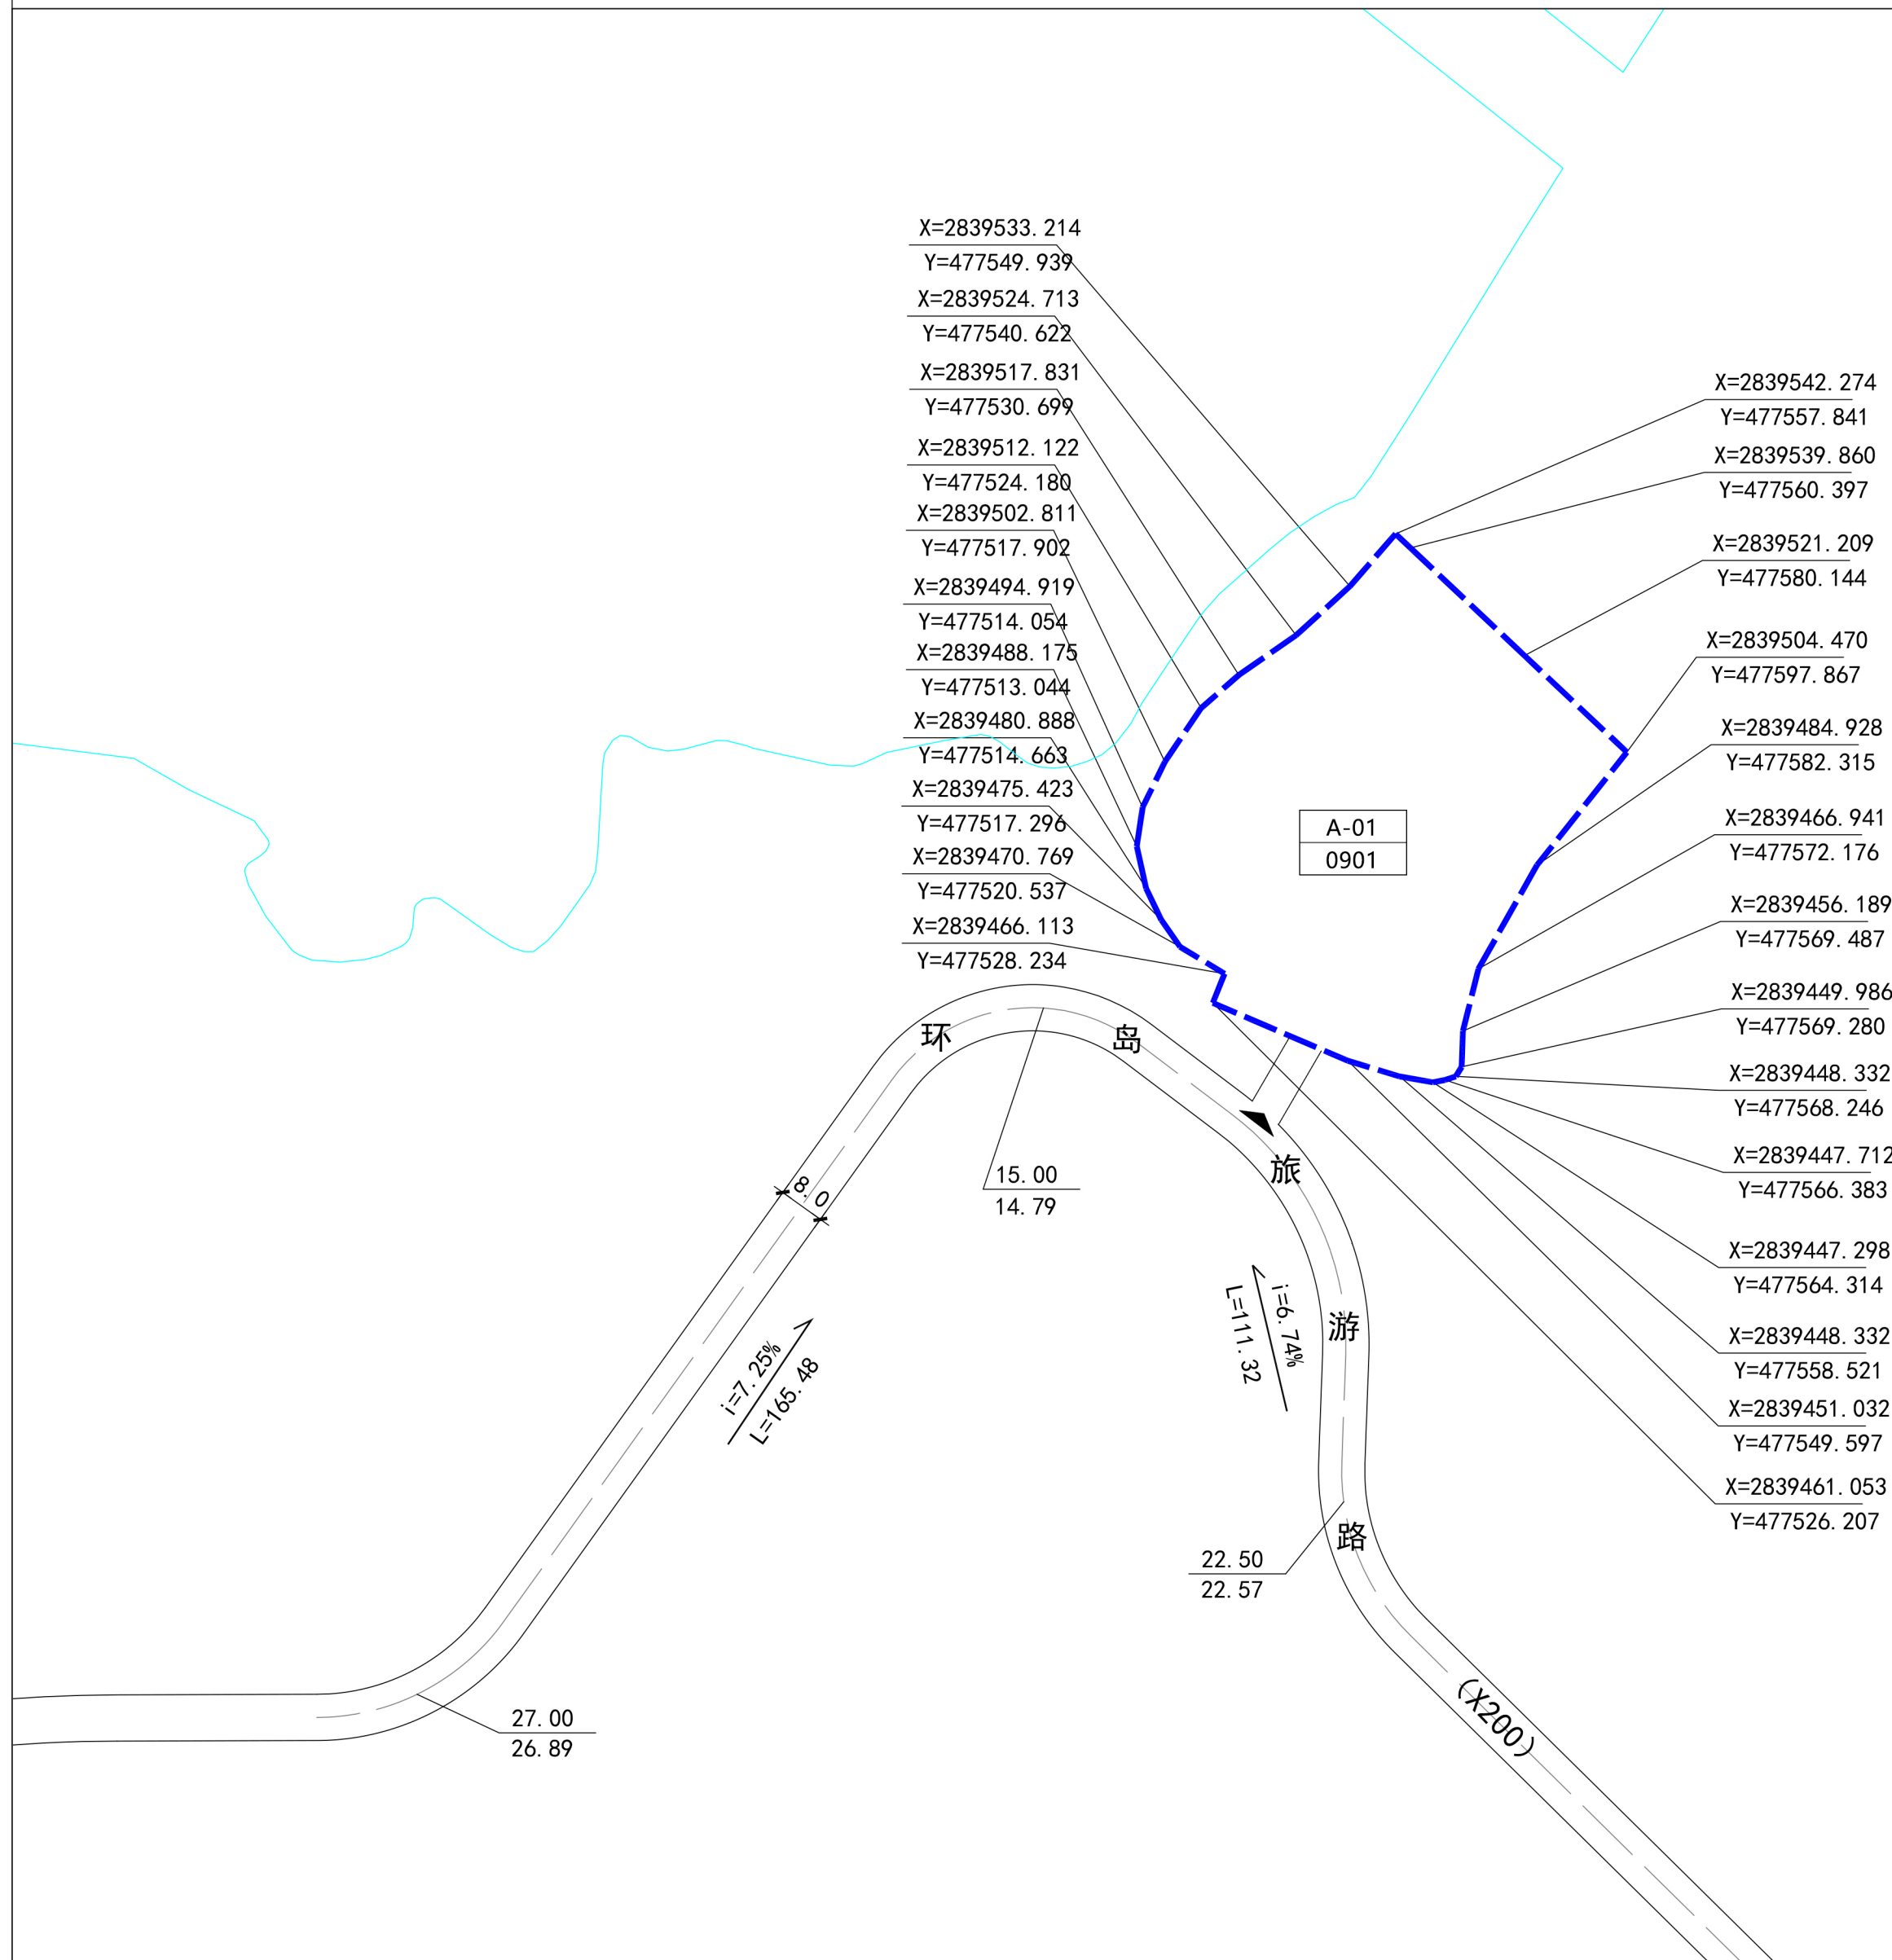

图例

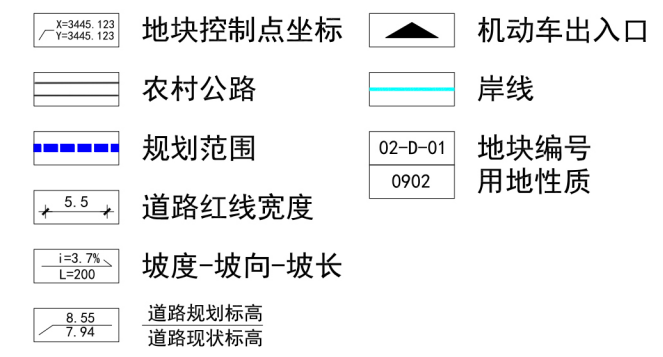

规划控制条文

- 1、规划地块用地性质为商业用地，用地面积约0.47公顷。不得随意更改地块用地规模和位置。
 - 2、“五线”属于强制性内容，其线位、规模及性质一经确定不得擅自调整。
- 道路红线：环岛旅游路（X200），道路宽度8米。
- 3、建筑间距须符合日照、防火、消防、抗震、环保、工程管线和文物、建筑保护等方面的要求，同时还应满足《福建省城市规划管理技术规定》（2017）中的建筑间距控制要求。
 - 4、地块出入口及配建停车位应满足《福建省城市规划管理技术规定》（2017）要求。
 - 5、地块建筑设计应注重与周边道路的关系；竖向及市政工程管线规划应与周边道路的竖向及工程管线相衔接；图中道路的线位、断面形式、交叉口形式、控制点标高及具体位置均以批准的工程方案为准。
 - 6、地块图则未涉及的其它规划要求由平潭综合实验区自然资源与生态环境局根据相关规定确定并执行。

地块控制指标表	地块编号	用地代码	用地性质	用地面积（平方米）	建筑面积（平方米）	容积率	建筑密度（%）	绿地率（%）	建筑限高（米）	配套设施	图名	地块编码及图则			
	A-01	0901	商业用地	4662.185	≤7000	≤1.5	≤40	≥10	24	——	编制单位	厦门市城市规划设计研究院有限公司 厦门市规划院（平潭）规划设计有限公司			
												图号	10	日期	2022.04
	备注	控制指标未明确的市政公用设施、交通设施等地块，可按照相关行业标准要求或者行业主管部门意见确定具体项目用地、建设规模及规划控制指标等，作为审批依据。													