

平潭综合实验区三十六脚湖生态管理单元客水泵站 地块控制性详细规划


01.区域位置图



规划范围于平潭岛中的位置





规划范围于三十六脚湖组团中的位置

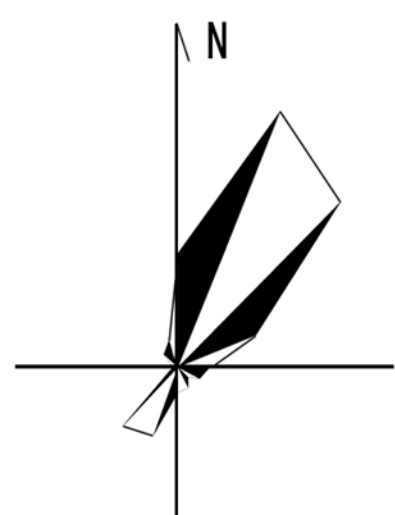




平潭综合实验区三十六脚湖生态管理单元客水泵站 地块控制性详细规划

03.用地规划图

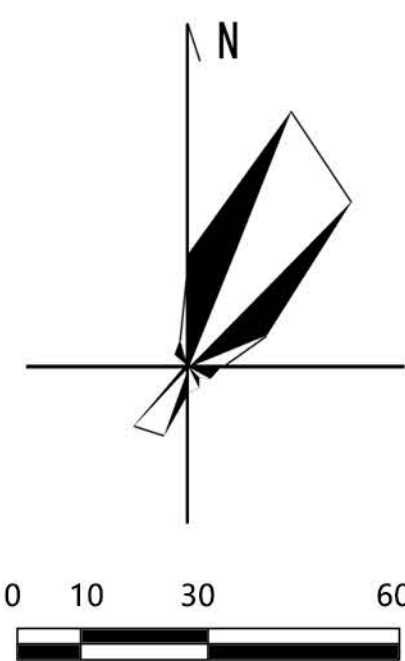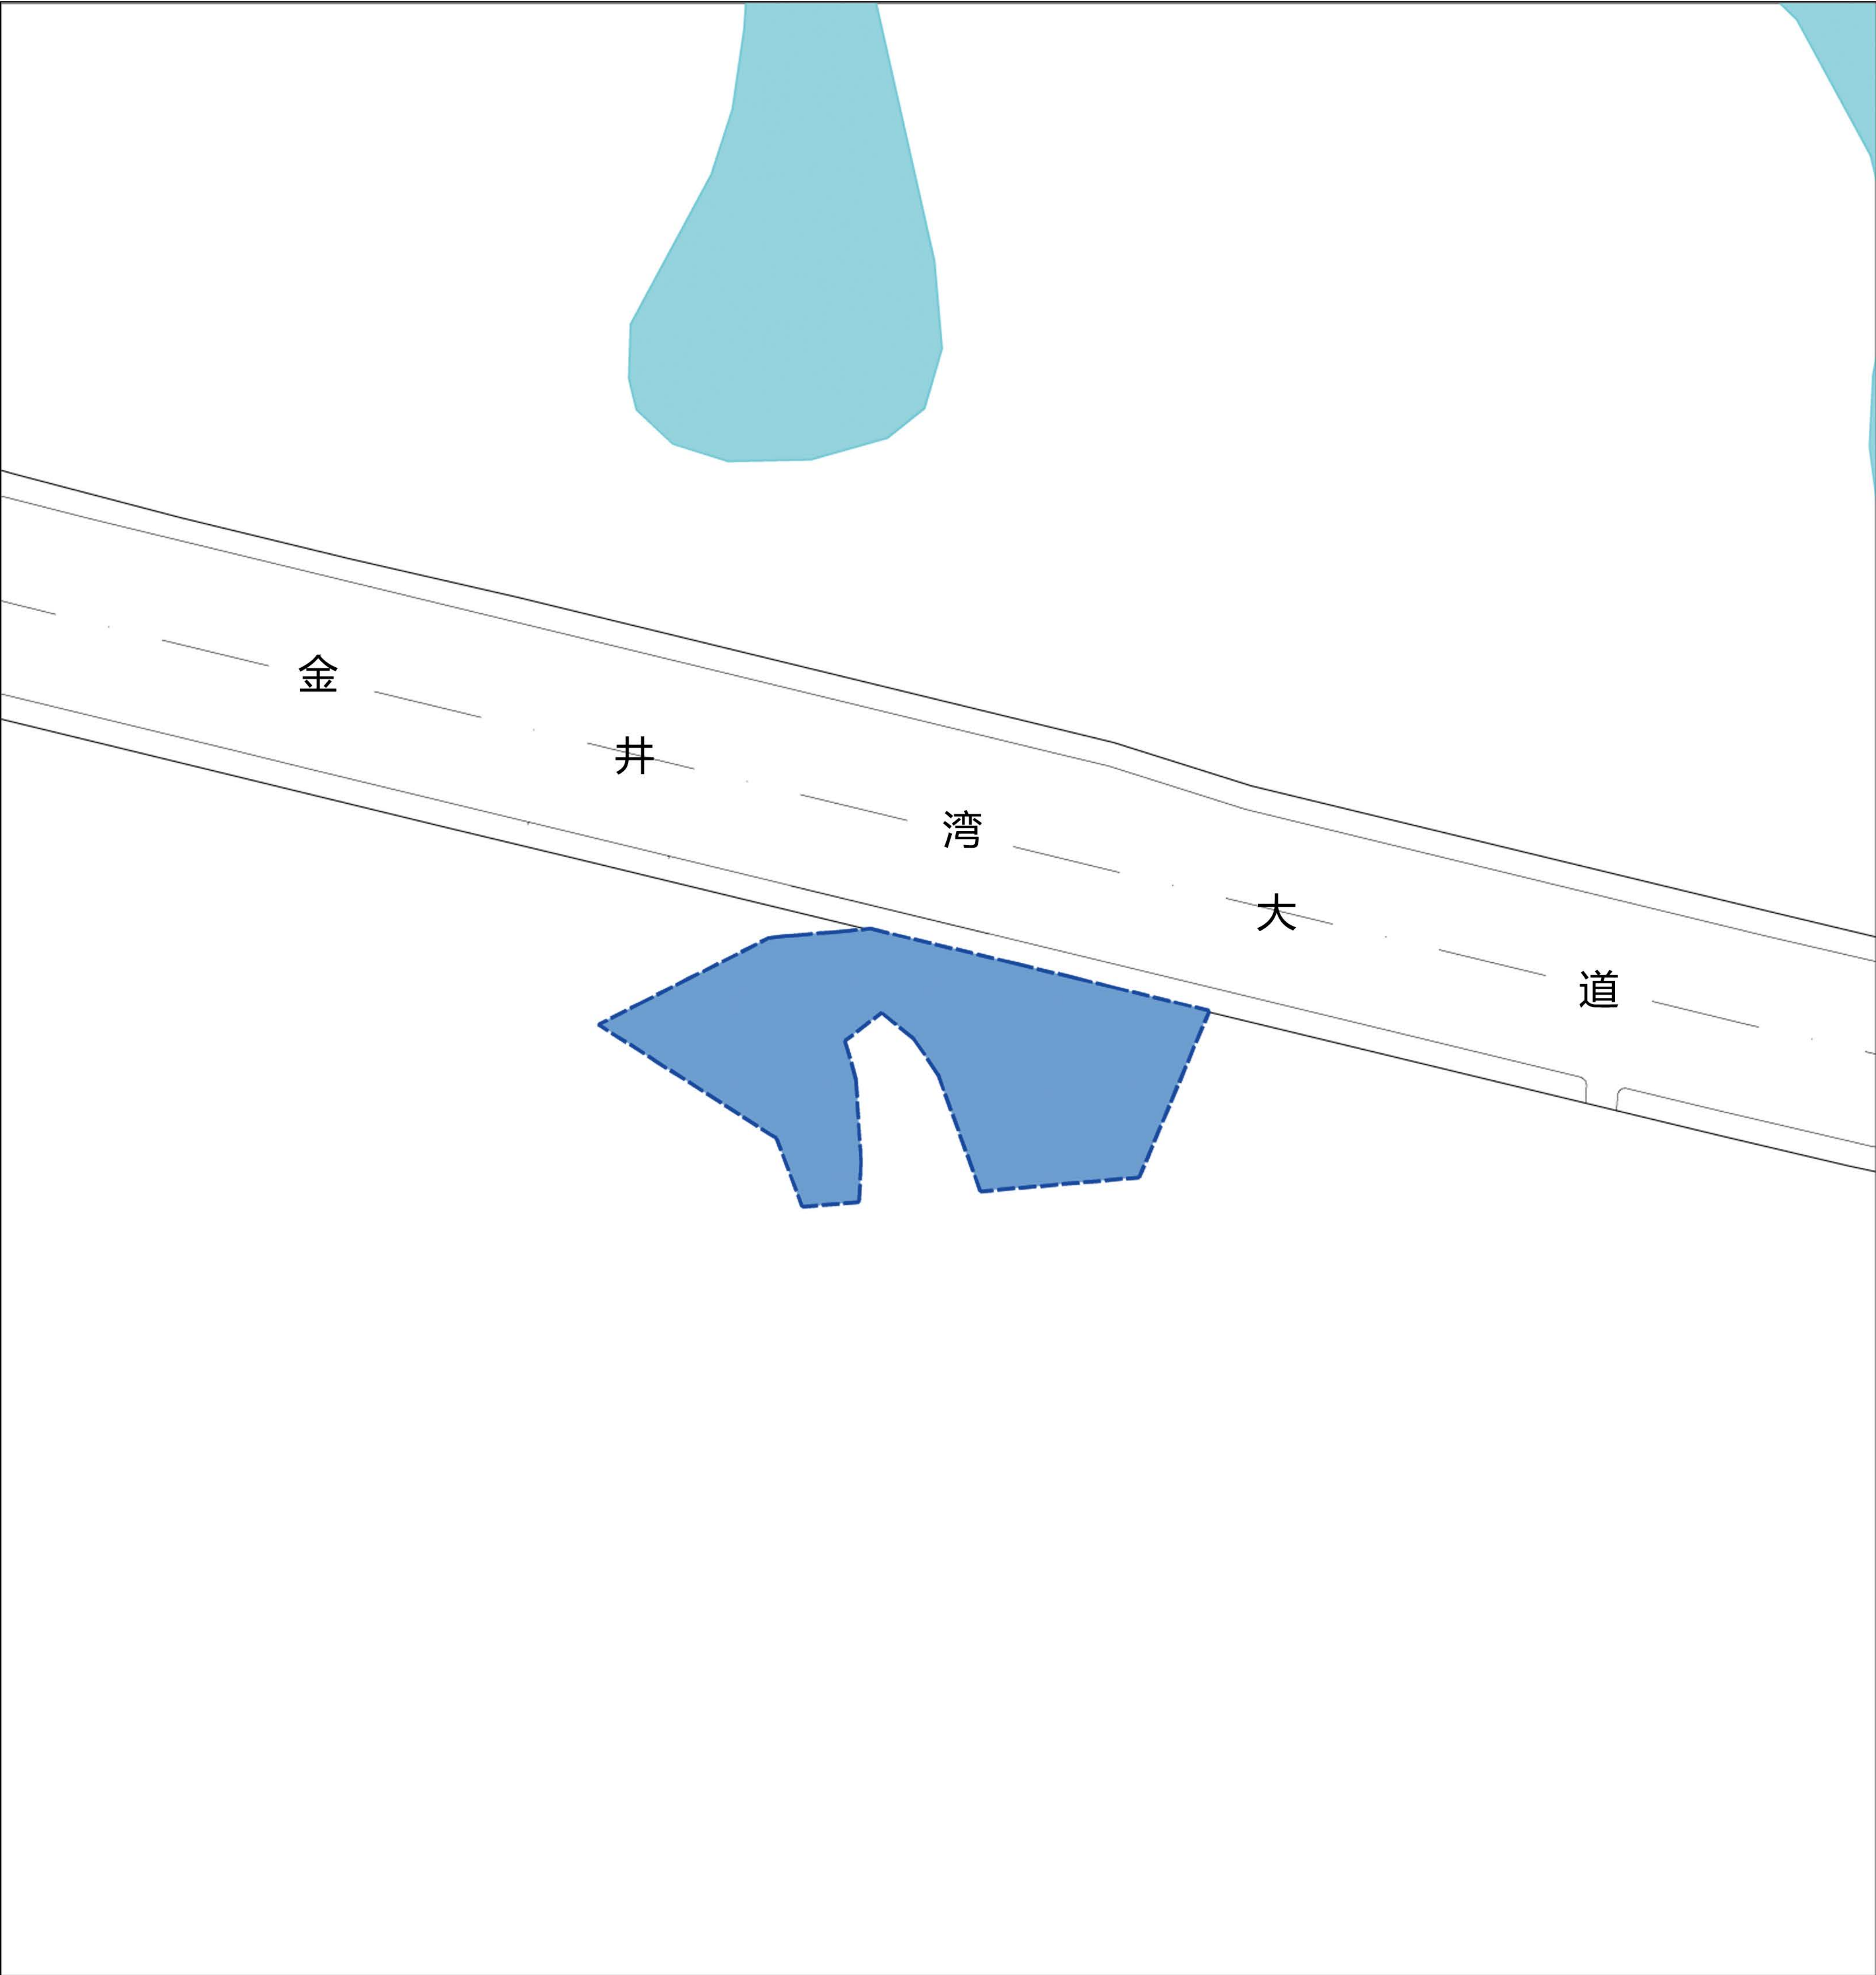

- | | | |
|--|------|--|
| | 供水用地 | |
| | 陆地水域 | |
| | 城市道路 | |
| | 规划范围 | |

平潭综合实验区三十六脚湖生态管理单元客水泵站地块控制性详细规划

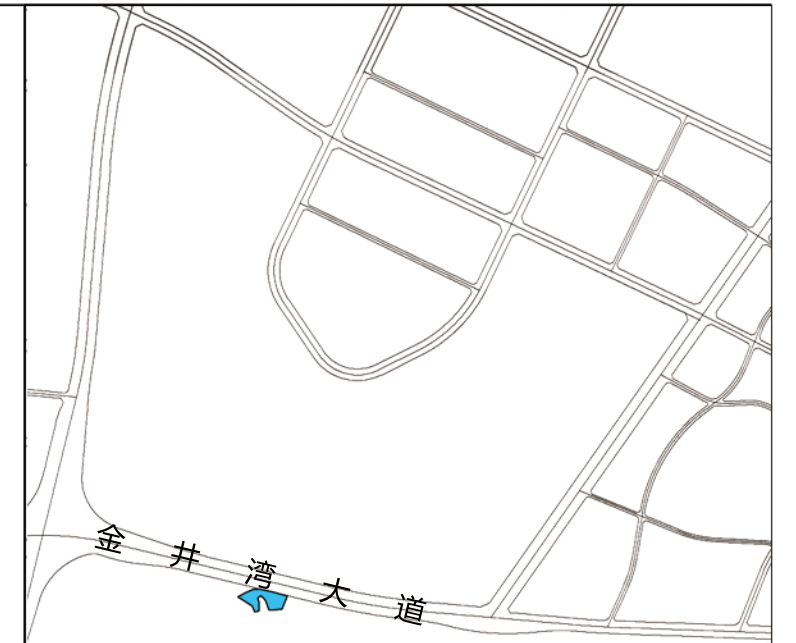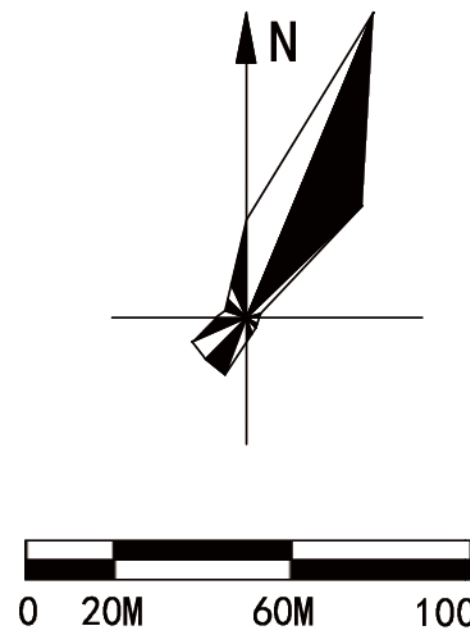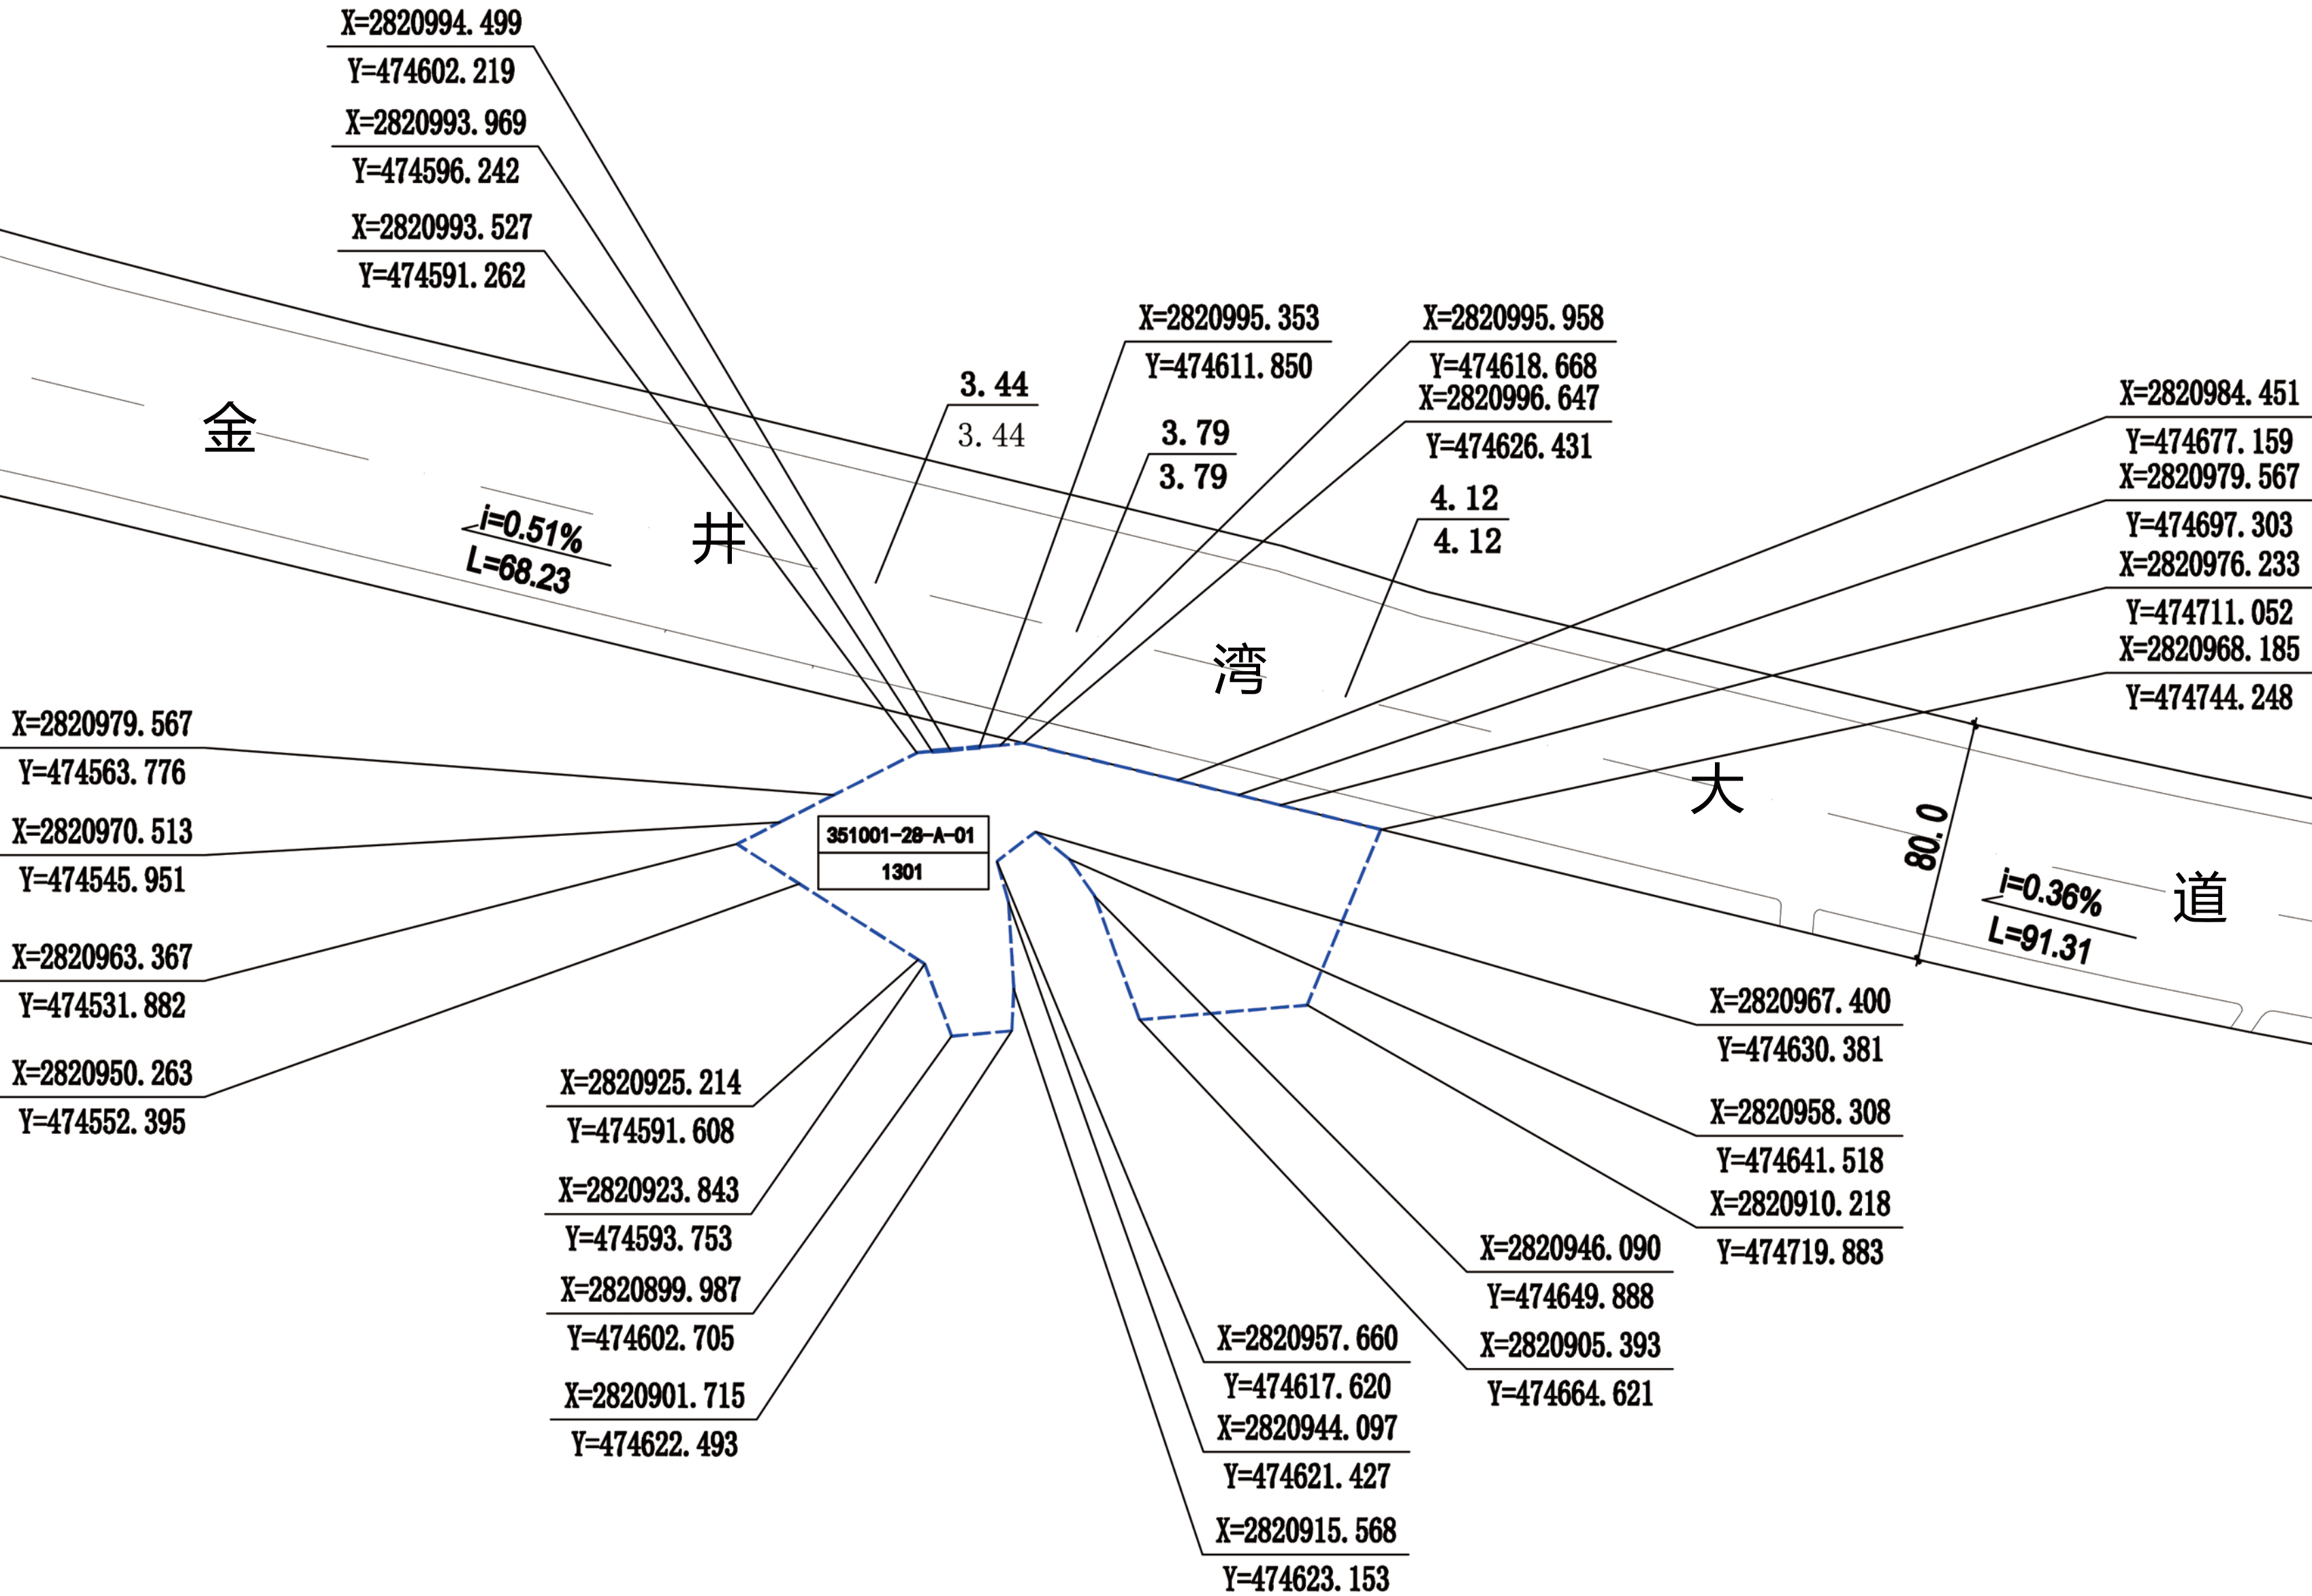

图例

	地块控制点坐标		禁止机动车开口线
	城市道路		水域
	规划范围		绿地
	道路红线宽度		机动车出入口
	坡度-坡向-坡长		地块编号
	道路规划标高 道路现状标高		用地性质

规划控制条文

- 1、规划地块用地性质为供水用地，用地面积约1.14公顷。不得擅自更改地块用地规模和位置。
- 2、“五线”属于强制性内容，其线位、规模及性质一经确定不得擅自调整，控制内容如下：
道路红线：金井湾大道红线宽度80米。
- 3、“三大设施”控制应按照《福建省城市规划管理技术规定》（2017年版）公共服务设施配置标准，具体指标如下：
本地块配建一处客水泵站，其建筑面积不大于2200平方米。
- 4、配套设施的项目、数量和用地或建筑面积不得少于规划的规定，如有变更，必须申报城乡行政主管部门批准。
- 5、建筑间距须符合日照、防火、消防、抗震、环保、工程管线和文物、建筑保护等方面的要求，同时还应满足《福建省城市规划管理技术规定》（2017）中的建筑间距控制要求。
- 6、地块出入口及配建停车位应满足《福建省城市规划管理技术规定》（2017）要求。
- 7、地块城市设计应注重于周边城市主次干路的关系；竖向及市政工程管线规划应与周边道路的竖向及工程管线相衔接；图中道路的线位、断面形式、交叉口形式、控制点标高及具体位置均以批准的工程方案为准。
- 8、地块图则未涉及的其它规划要求由平潭综合实验区自然资源与生态环境局根据相关规定确定并执行。

地块控制指标表	地块编号	用地代码	用地性质	用地面积（平方米）	建筑面积（平方米）	容积率	建筑密度（%）	绿地率（%）	建筑限高（米）	配套设施	图名	地块编码及图则		
	351001-28-A-01	1301	供水用地	11433. 203	不大于2200	不大于0. 2	不大于15%	不小于35%	14米以下	——				
											编制单位	厦门市城市规划设计研究院有限公司 厦门市规划院（平潭）规划设计有限公司		
备注	控制指标未明确的市政公用设施、交通设施等地块，可按照相关行业标准要求或者行业主管部门意见确定具体项目用地、建设规模及规划控制指标等，作为审批依据。										图号	12	日期	2022.05