


平潭综合实验区岚城组团 2019G067 地块建筑设计方案 (工规变更)

建设单位：平潭仁新置业有限公司
建筑设计单位：厦门上城建筑设计有限公司

2022 年 09 月

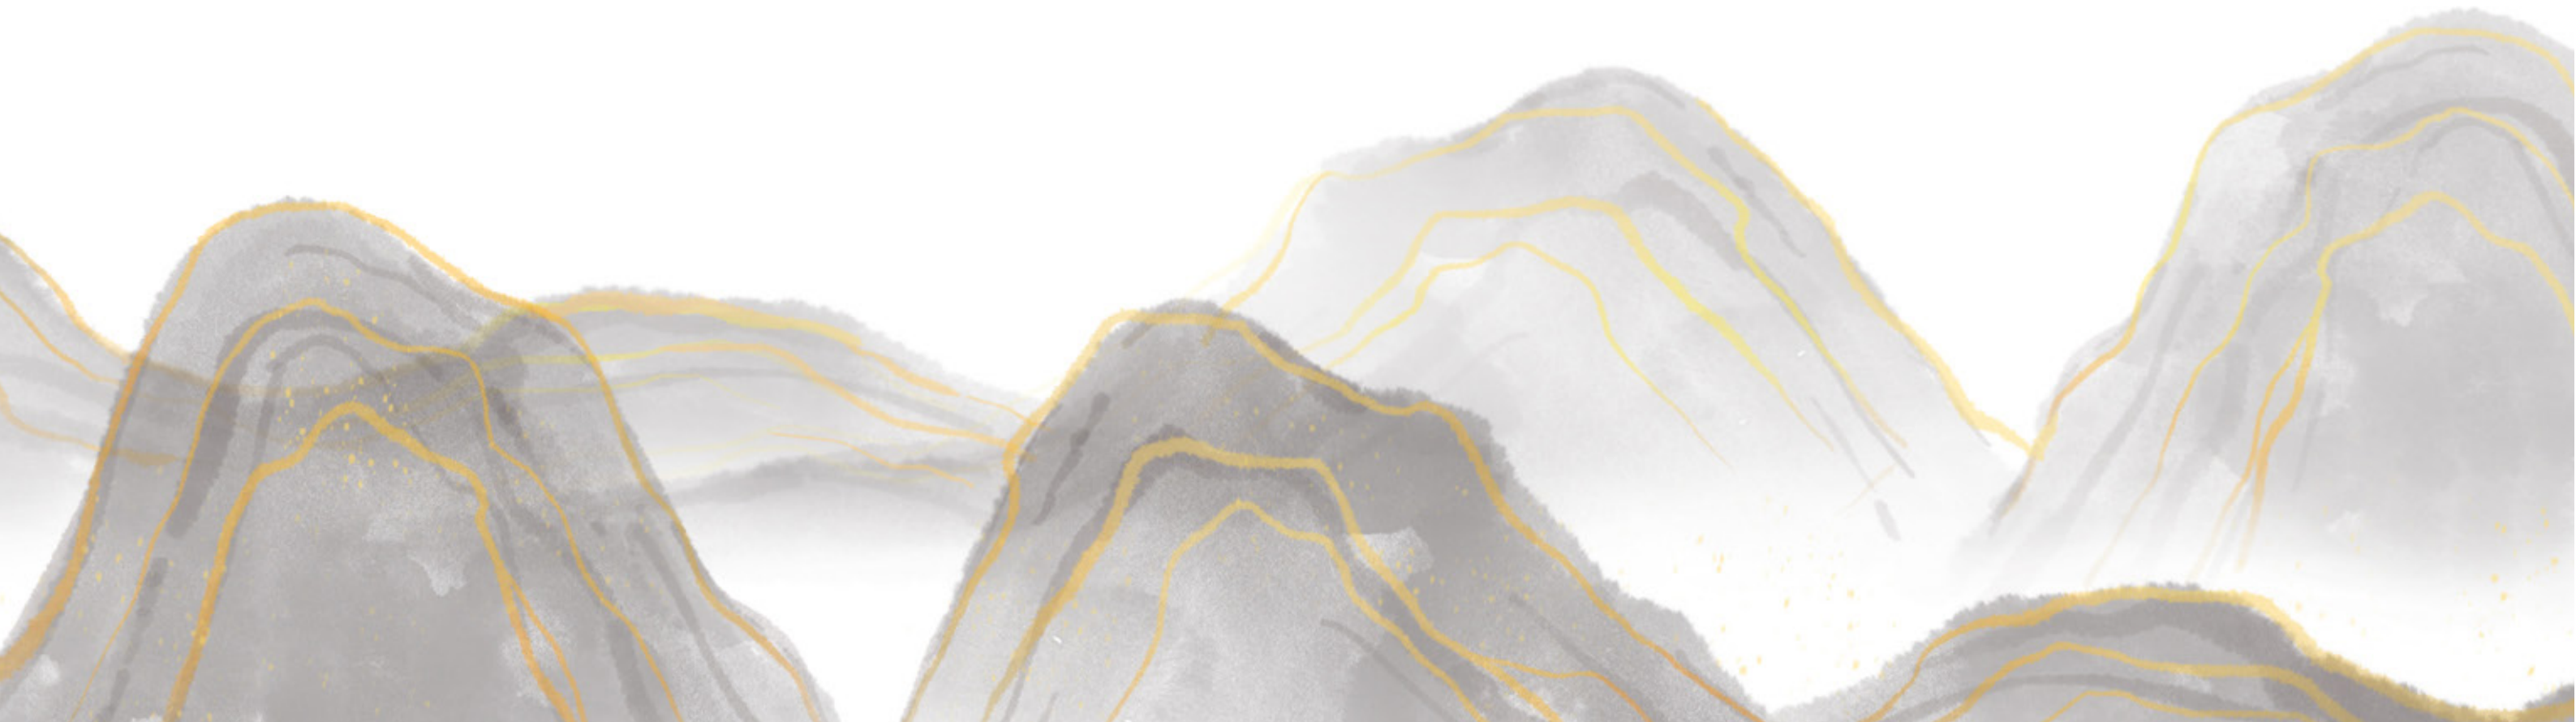

平潭综合实验区岚城组团2019G067地块工规变更调整内容

一、总平调整、单体调整

2#楼东侧裙房，生鲜超市调整为商业、消控室、物业管理用房

7#楼一层，消控室、物业管理用房调整为生鲜超市

二、指标调整

指标面积与原工规指标一致，无调整；

电动汽车充换电站车位配置和统计方式				
总配建停车位车位数	电动汽车充电桩车位数 数量及充电桩配置比例	电动汽车充电桩数量占 总配建车位的比例	快充停车位数量占 总配建车位的比例	快充停车位配置数
住宅	387	78	4%	4
商业	7	2%	12%	1
公共	1	2%	12%	1

备注：1、执行《福建省电动汽车充电基础设施建设技术规范》，100%配建电动汽车充电设施和充电桩设备；2、居住建筑电动汽车100%配建电动汽车充电设施充电桩设备，商业建筑电动汽车充电桩设备按照10%配建，公共建筑电动汽车充电桩设备按照5%配建。

公共充电桩停车位数量占住宅停车位数量的10%。

公共充电桩停车位数量占商业停车位数量的10%。

公共充电桩停车位数量占公共停车位数量的10%。

1、住宅总配建停车位387辆，其中公共停车位208个（地下车库一层停车位），其中公共充电桩停车位占住宅总车位的5%，为78个（208×20%÷168）；公共充电桩停车位占住宅总车位的10%，为38个（387×10%÷168）。

本工程计容建筑面积为38632平方米，人防面积按计容建筑面积7%计算
合计所需人防面积为2704.24平方米。共2个人员掩蔽所。

具体意见以人防部门为准

H1=室外地坪到建筑顶层屋面层高度

H2=室外地坪到建筑顶层女儿墙高度

H3=室外地坪至建筑檐口加上檐口挑出的宽度

坐标系采用“2000国家大地坐标系”，高程采用“1985国家高程基准”

本项目满足绿色建筑一星标准

图例：

- | | | | |
|---|--------|---|----------|
|  | 用地红线 |  | 无障碍停车位 |
|  | 地下室范围线 |  | 机动车停车位 |
|  | 小区围墙线 |  | 充电机动车停车位 |
|  | 消防扑救场地 |  | 快充停车位 |
|  | 绿地 | R12 | 道路转弯半径 |
|  | 非机动车位 | | |



出图章

注册建筑师执业章

注册工程师执业章

施工图审查单位

施工图审查合格书编号

本图纸须经建设、规划、消防、审查等相关部门

建设单位 平潭仁新置业有限公司

工程名称 2019G067 地


子项名称

图名

总平面图

工程编号			
审 定	陈为东		
审 核	蔡金彬		
工程负责人	赖伟胜		
专业负责人	赖伟胜		
专业负责人助理	蔡大林		
校对人	陈培基		
设计人	蔡大林		
制图人	蔡大林		
图 别		图 号	
版本号	日期	版本号	日期

调整后

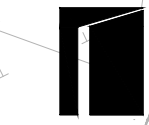

厦门上城建筑设计有限公司
XIAMEN U-TOWN ARCHITECTURE DESIGN INSTITUTE CO., LTD.
资质证书编号: A135007271

合作单位

出图章

注册建筑师执业章

注册工程师执业章

施工图审查单位

施工图审查合格书编号

本图纸须经建设、规划、消防、审查等相关单位
审核通过后方可作为正式施工图

建设单位
平潭仁新置业有限公司

工程名称
2019G067地块

子项名称

图名

总平面图

工程编号

审定 陈为东

审核 蔡金彬

工程负责人 赖伟胜

专业负责人 赖伟胜

专业负责人助理 蔡大林

校对 陈培基

设计人 蔡大林

制图人 蔡大林

图别


版本号

日期

版本号

日期

G067地块项目主要技术经济指标				
序号	分项	单位	数值	规划要求
1	总用地面积 (m²)	m²	19316.00	18米<H≤60米 (限高为建筑总高度)
2	总建筑面积 (m²)	m²	52798.28	
3	其中			
4	地上建筑面积	m²	40938.54	
5	地下建筑面积	m²	12539.54	
6	计容建筑面积 (m²)	m²	38632.00	大于19316平方米, 且不大于38632平方米
7	住宅建筑面积	m²	36739.59	大于18686平方米, 且不大于37422平方米
8	配套商业建筑面积	m²	1158.75	大于380平方米, 且不大于1160平方米
9	沿街商店	m²	873.12	
10	生鲜超市便利店	m²	205.48	套内建筑面积不小于200平方米
11	电子商务代收服务点	m²	80.15	建筑面积不小于80平方米
12	配套公建建筑面积	m²	733.66	
13	物业管理用房	m²	128.84	不小于总建筑面积2%, 最少不低于100平
14	变配电室	m²	375.60	
15	通信机房	m²	32.13	
16	电视机房	m²	18.87	
17	附建式环网站	m²	53.20	套内建筑面积不小于50平方米
18	柴油发电机房	m²	57.50	
19	消防控制室	m²	48.15	
20	室外梯 (配套)	m²	5.33	
21	弱电	m²	14.94	
22	不计容建筑面积 (m²)	m²	14166.28	
23	架空层	m²	1610.64	
24	垃圾环保屋	m²	16.10	套建筑面积不小于15平方米
25	地下室	m²	12539.54	
26	其中			
27	应建人防建筑面积	m²	2705.00	人防建筑面积按计容7%, 38632*7%=2704.24
28	人防地下室车库	m²	9834.54	
29	容积率		2.00	
30	建筑占地面积 (m²)	m²	4572.49	建筑密度 (上限) 30%
31	建筑密度 (%)	%	23.67%	
32	绿地面积 (m²)	m²	6765.00	绿地率 (下限) 35%
33	绿地率 (%)	%	35.02%	
34	居住人数	人	1127	
35	总户数	户	322	户均人数3.5人
36	机动车停车位 (个)	辆	400	1.地上机动车停车位≤超过10%, 2.公共车位39个, 3.充电车位82个 (其中快充6个)
37	其中			
38	地上	辆	20	
39	地下	辆	380	
40	非机动车位	辆	445	停车位计算详“停车配比表”
41	其中			
42	地上	辆	445	
43	地下	辆	0	
机动车停车指标				
建筑类型		户数	建筑面积	规划停车系数
住宅				
建筑面积>150m²		0		1.5车位/户
建筑面积90~150m²		322		1.2车位/户
建筑面积45~90m²		0		0.8车位/户
小计		322		387
配套			733.66	0.8辆/100m²
商业			1158.75	0.6辆/100m²
总计				400
非机动车停车指标				
住宅				
建筑面积>150m²		0		1.0车位/户
建筑面积90~150m²		322		1.0车位/户
建筑面积45~90m²		0		2.0车位/户
配套			733.66	4辆/100m²
商业			1158.75	8辆/100m²
总计				93
电动汽车充电停车位配置计算表				
电动汽车充电停车位配置计算方式				
总配建机动车车位数	电动汽车充电停车位配置数量占配建机动车停车位总数的比例	电动汽车充电停车位配置数量	快充停车位配置数量占充电停车位总数的比例	快充停车位配置数量
住宅	387	20%	78	4%
商业	7	20%	2	12%
公共配套	6	20%	2	10%
备注: 1、执行《福建省电动汽车充电基础设施技术规程》, 100%预留配电线路通道和充电设备位置; 2、居住建筑配建停车位按100%预留配电线路通道及充电设备位置, 并适当预留相关配电设备设置条件, 规定数量的充电停车位在建设初期配建变压器容量; 3、公共车位及充电车位占相应车位数的10%。				
地下公共停车位配置计算表				
1、住宅总配建停车位387辆, 其中公共停车位387x10%=39辆 (公共停车位设置地下一层停车场), 其中公共充电停车位占住宅充电车位的20%, 为387x20%=78辆 (其中快充停车位为16x0.094=1辆)				

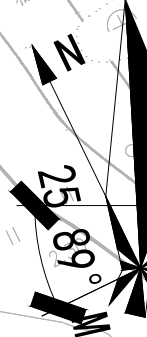

总平面图 1:500

说明:

本工程计容建筑面积为38632平方米, 人防面积按计容建筑面积7%计算
合计所需人防面积为2704.24平方米。共2个人员掩蔽所。

具体意见以人防部门为准

H1=室外地坪到建筑顶层屋面层高度

H2=室外地坪到建筑顶层女儿墙高度

H3=室外地坪至建筑檐口加上檐口挑出的宽度


坐标系采用“2000国家大地坐标系”, 高程采用“1985国家高程基准”

本项目满足绿色建筑一星标准

图例:

用地红线	无障碍停车位
地下室范围线	机动车停车位
小区围墙线	充电机动车停车位
消防扑救场地	快充停车位
绿地	R12 道路转弯半径
非机动车位	

规划初中

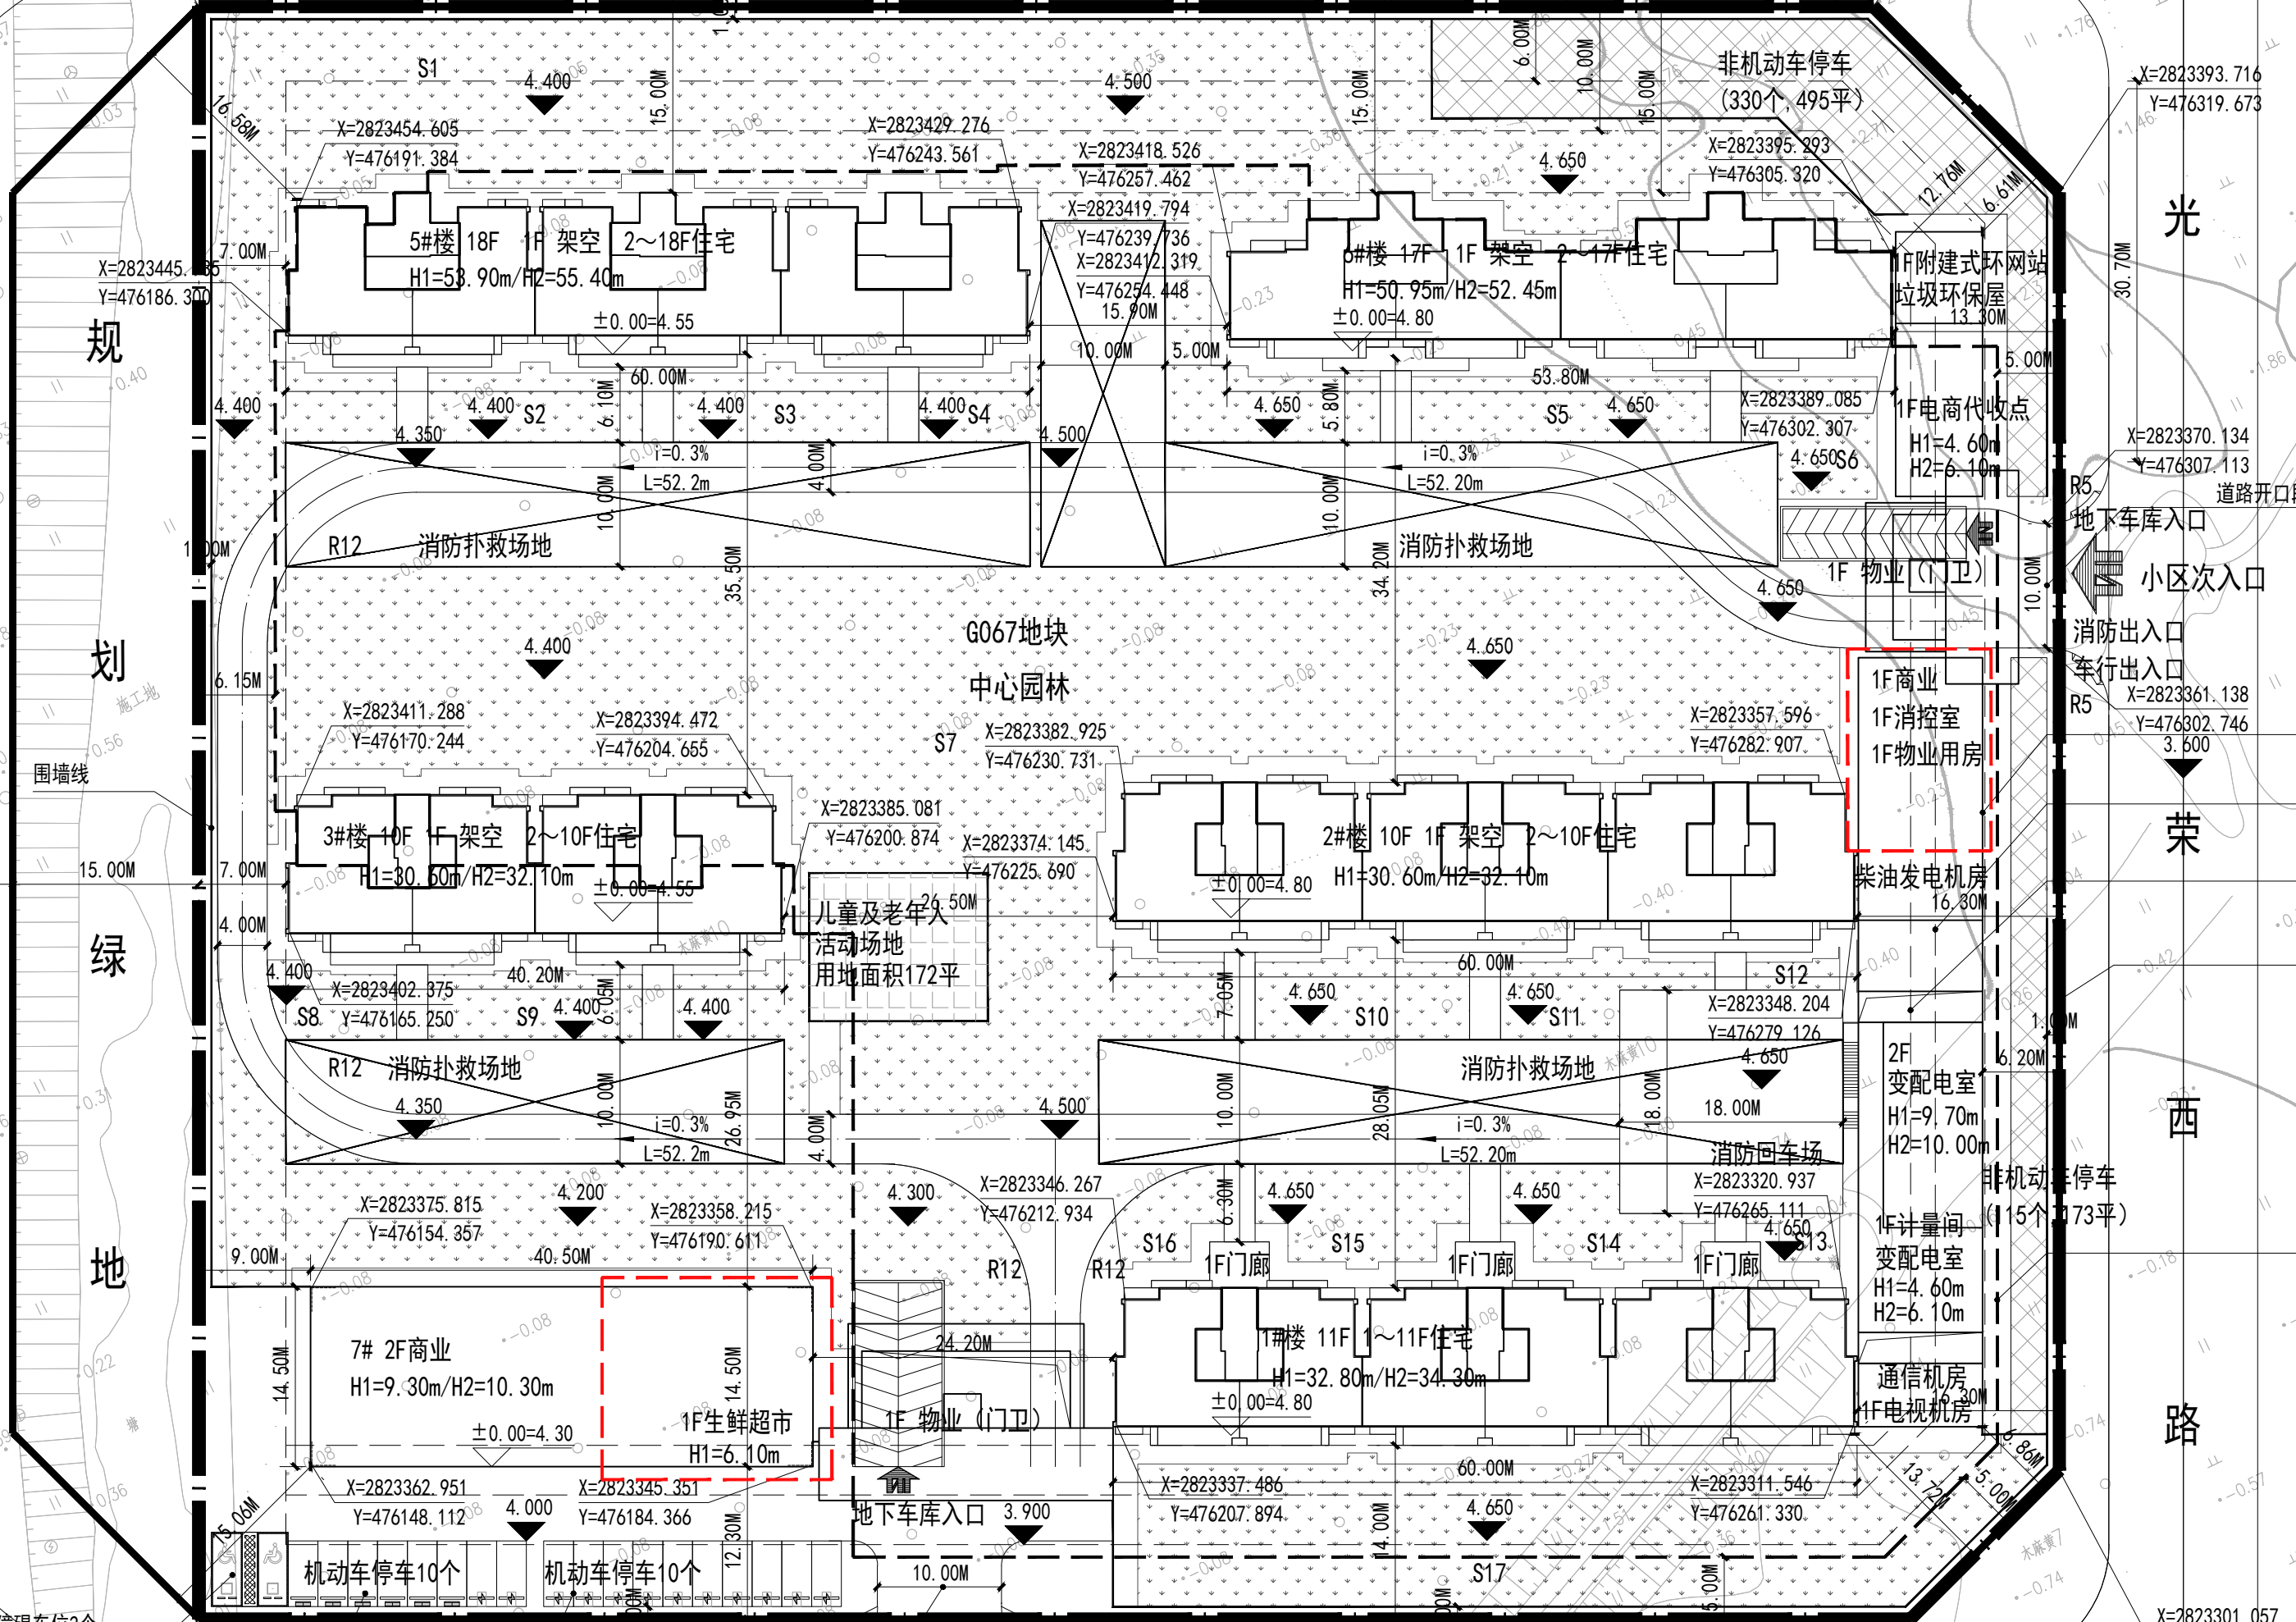


2019G065地块

专业	姓名	日期
电气		
给排水		
暖通		
姓名	日期	
专业	姓名	日期
建筑		
结构		

调整前

消防回车场

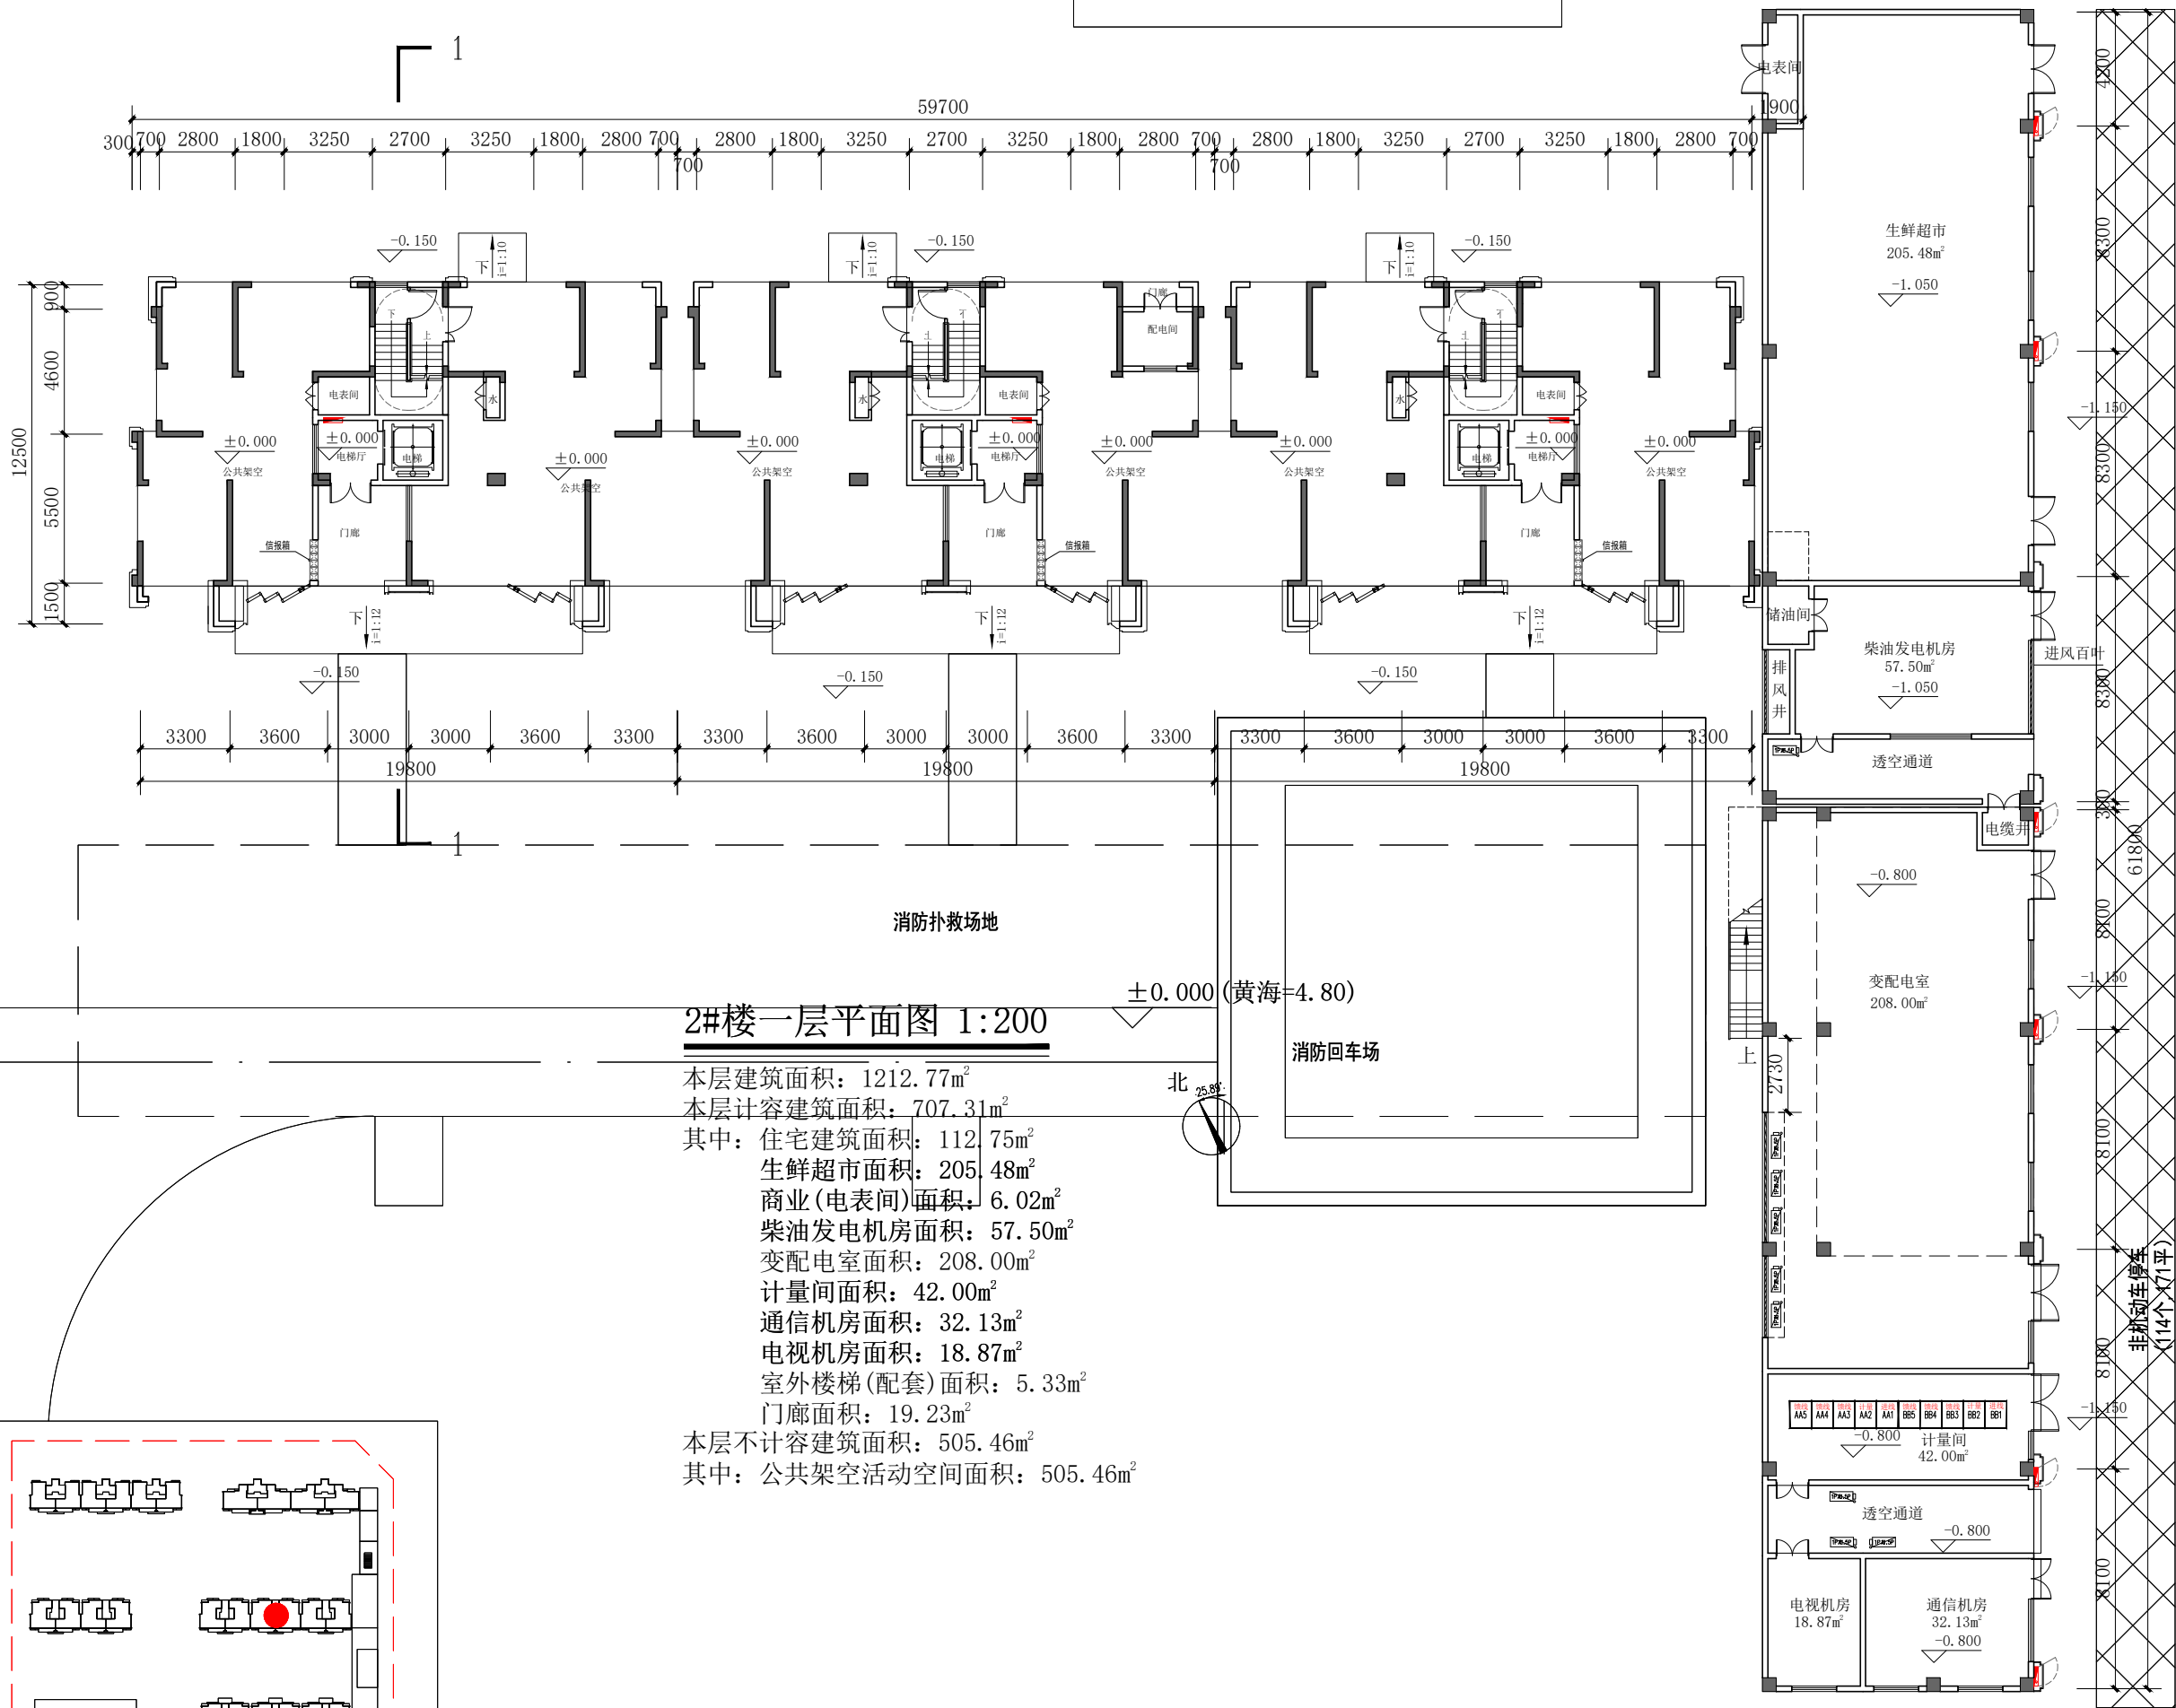

2#楼一层平面图 1:200

本层建筑面积: 1212.77m²
本层计容建筑面积: 707.31m²
其中: 住宅建筑面积: 112.75m²
生鲜超市面积: 205.48m²
商业(电表间)面积: 6.02m²
柴油发电机房面积: 57.50m²
变配电室面积: 208.00m²
计量间面积: 42.00m²
通信机房面积: 32.13m²
电视机房面积: 18.87m²
室外楼梯(配套)面积: 5.33m²
门廊面积: 19.23m²
本层不计容建筑面积: 505.46m²
其中: 公共架空活动空间面积: 505.46m²

区位示意

厦门上城建筑设计有限公司
XIAMEN U-TOWN ARCHITECTURE DESIGN INSTITUTE CO.,LTD.
资质证书编号: A135007271

合作单位

出图章

注册建筑师执业章

注册工程师执业章

本图纸须经建设、规划、消防、审查等相关部门
审批通过后方可作为正式施工图纸

施工图审查单位

施工图审查合格书编号

建设单位
平潭仁新置业有限公司

工程名称
2019G067地块

子项名称
2#楼

图名
一层平面图


工程编号

审定	陈为东
审核	蔡金彬
工程负责人	赖伟胜
专业负责人	赖伟胜
专业负责人助理	蔡大林
校对	佟肇雄
设计	陈培基
制图	陈培基

图别	图号
版本号	日期
版本号	日期
版本号	日期
版本号	日期

专业	姓名	日期
建筑		
结构		
电气		
给排水		
暖通		

调整后

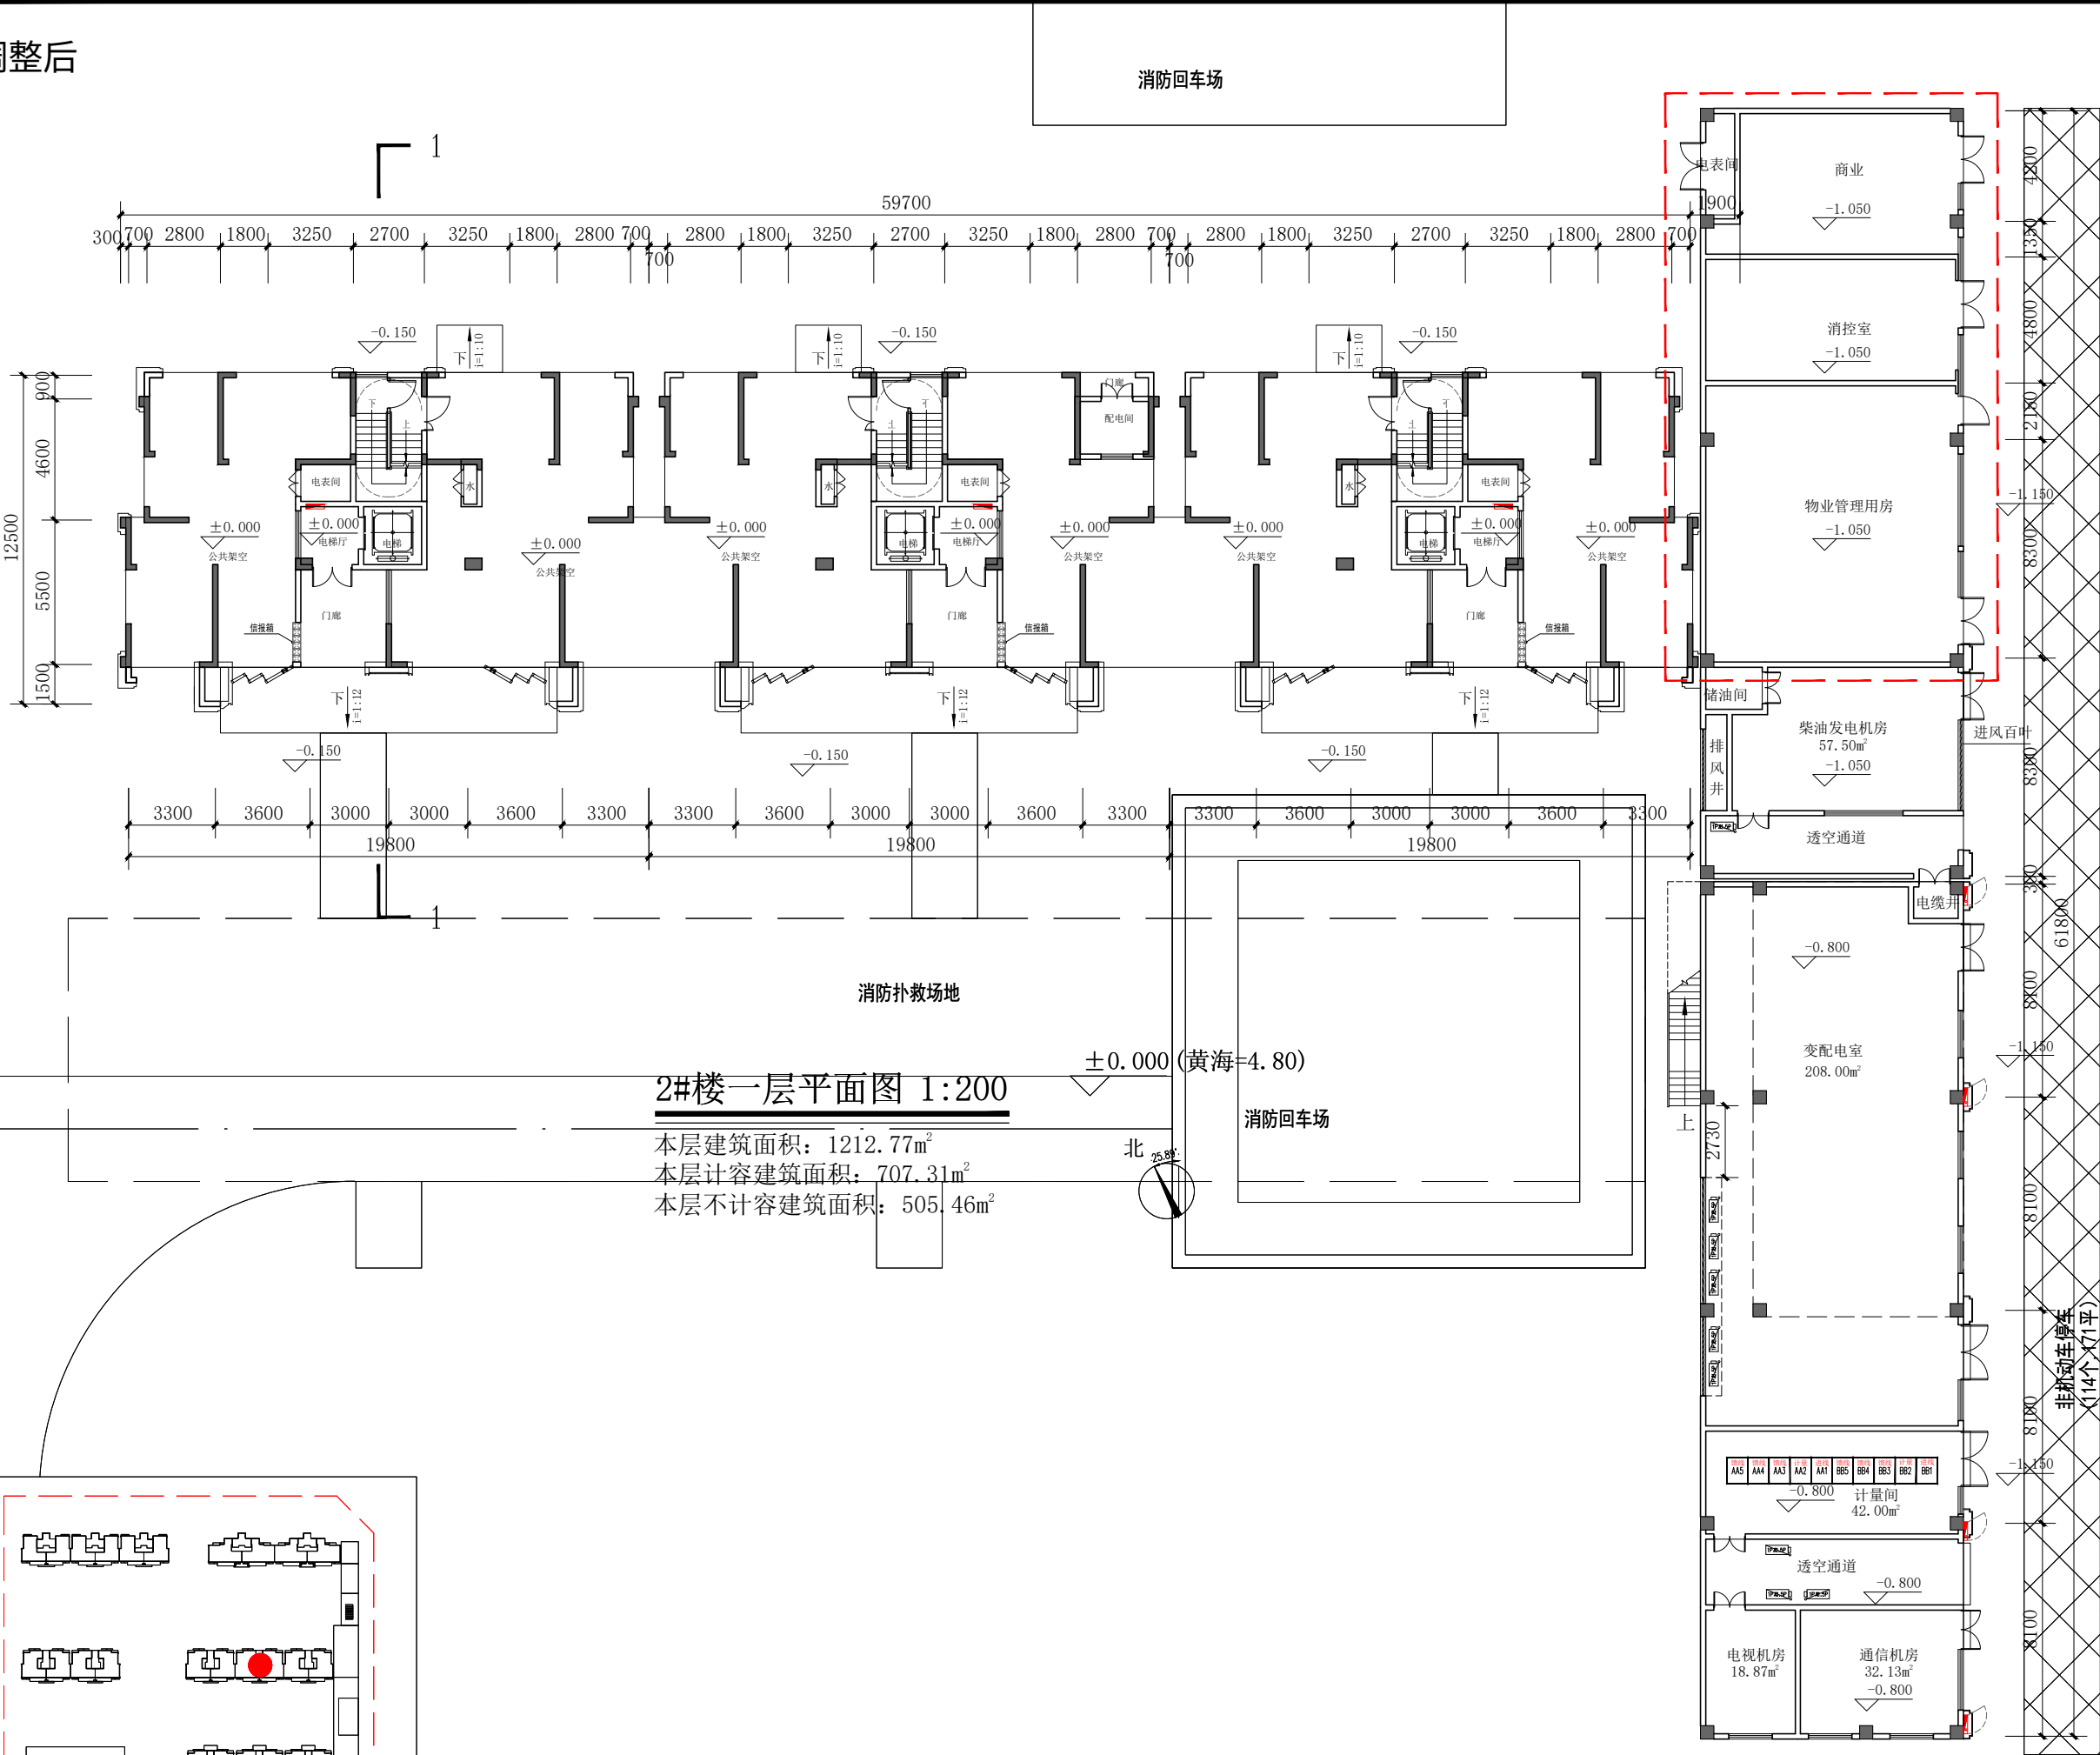

区位示意



厦门上城建筑设计有限公司
XIAMEN U-TOWN ARCHITECTURE DESIGN INSTITUTE CO.,LTD.
资质证书编号: A135007271

合作单位

出图章

注册建筑师执业章

注册工程师执业章

本图纸须经建设、规划、消防、审查等相关部门
审批通过后后方可作为正式施工图纸

施工图审查单位

施工图审查合格书编号

建设单位
平潭仁新置业有限公司

工程名称
2019G067地块

子项名称
2#楼

图名
一层平面图


工程编号

审定	陈为东	
审核	蔡金彬	
工程负责人	赖伟胜	
专业负责人	赖伟胜	
专业负责人助理	蔡大林	
校对	佟肇雄	
设计人	陈培基	
制图人	陈培基	

图别	图号	图号	图号
版本号	日期	版本号	日期

专业	姓名	日期
建筑		
结构		
专业	姓名	日期
电气		
给排水		
暖通		


调整前

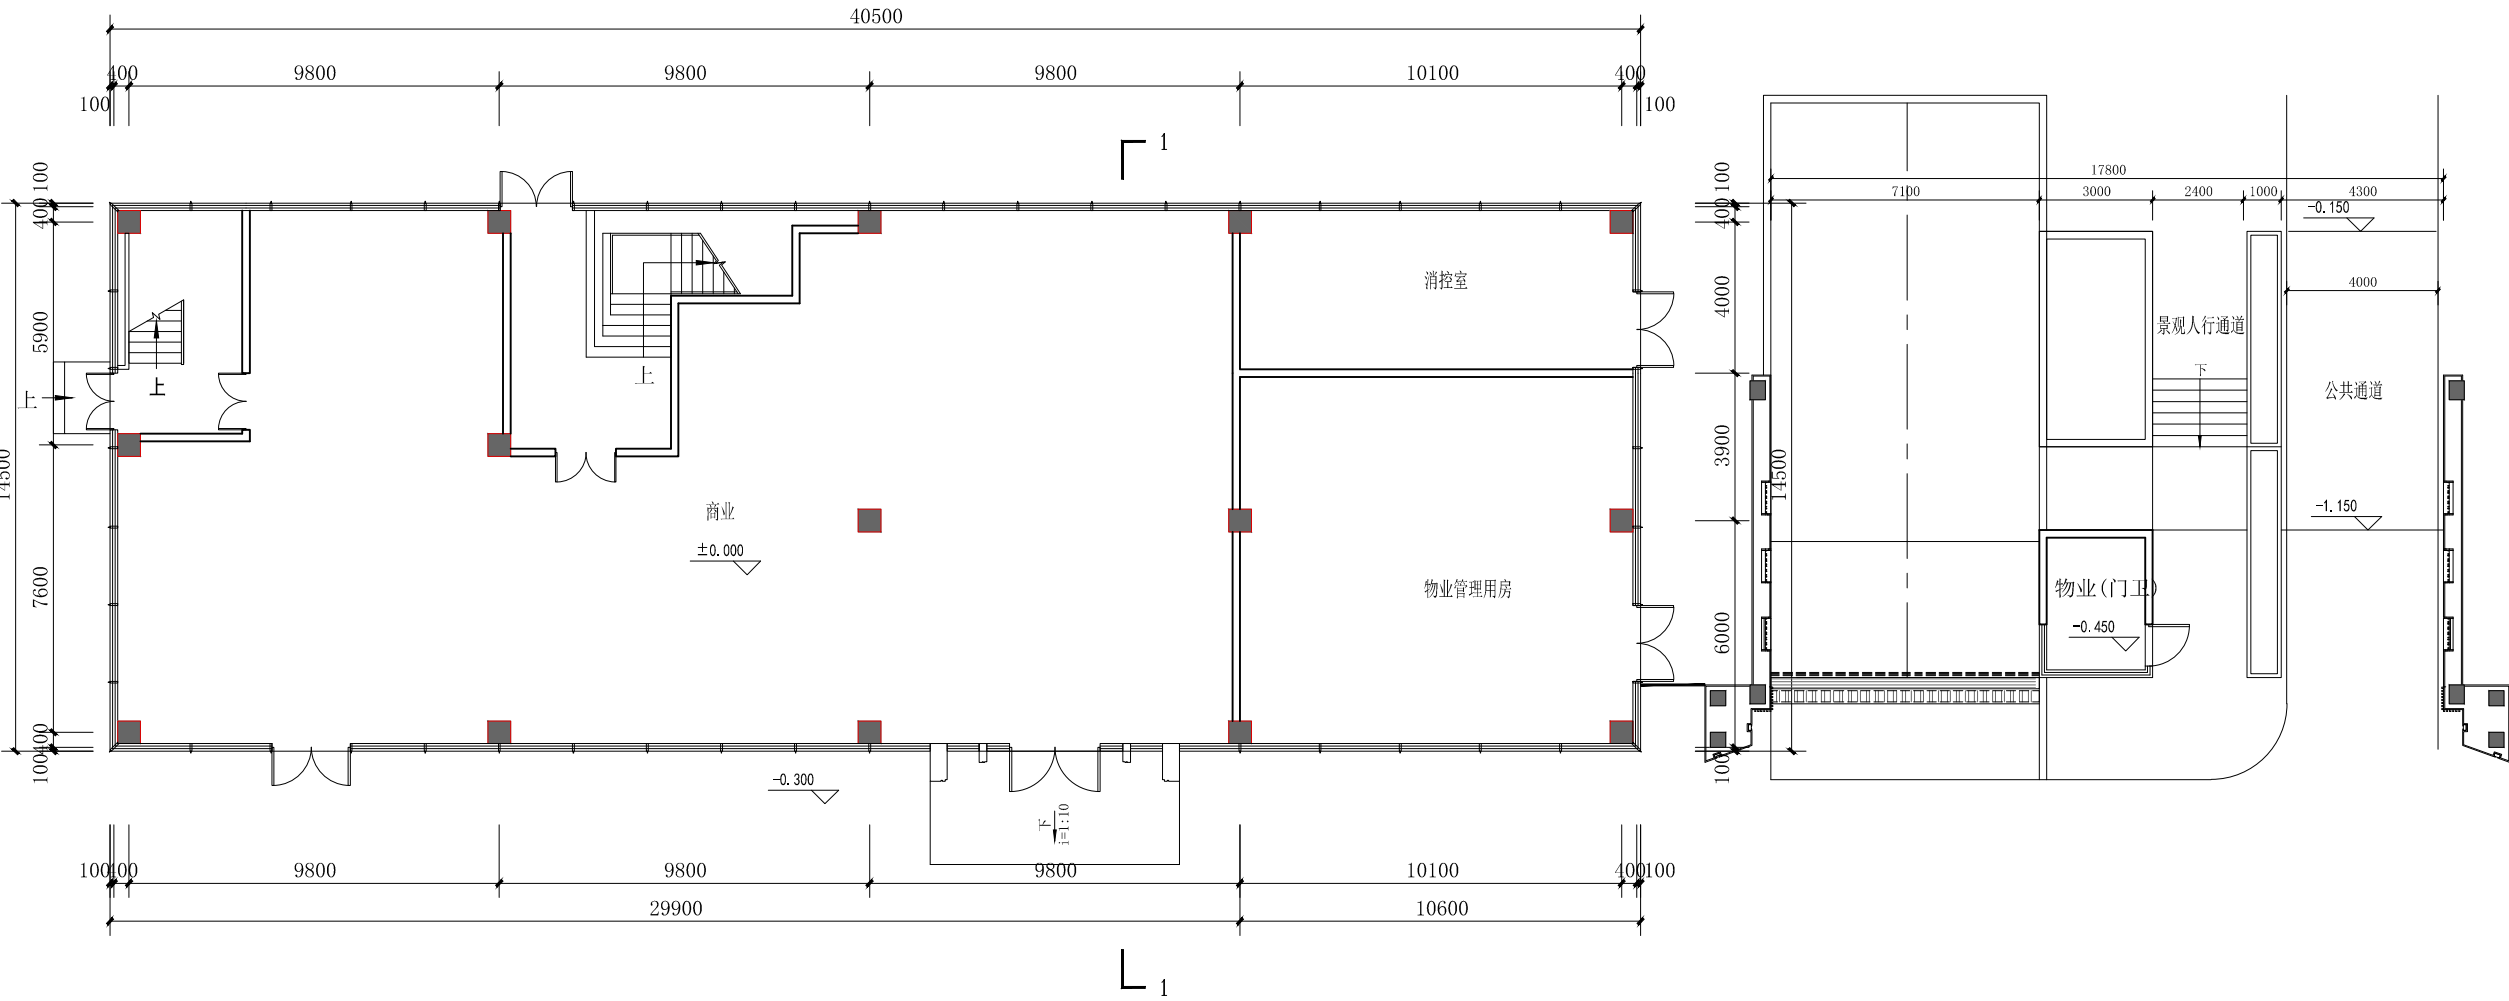

7#楼一层平面图 1:200

本层建筑面积: 598.95m²
本层计容建筑面积: 598.95m²
其中: 物业管理用房面积: 118.70m²
消控室面积: 48.15m²
商业建筑面积: 432.10m²

区位示意

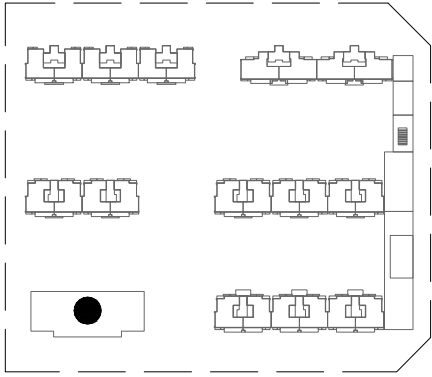

厦门上城建筑设计有限公司
XIAMEN U-TOWN ARCHITECTURE DESIGN INSTITUTE CO.,LTD.
资质证书编号: A135007271

合作单位

出图章

注册建筑师执业章

注册工程师执业章

本图纸须经建设、规划、消防、审查等相关部门
审批通过后方可作为正式施工图纸

施工图审查单位

施工图审查合格书编号

建设单位
平潭仁新置业有限公司

工程名称
2019G067地块

子项名称
7#楼

图名
一层平面图


工程编号

审定	陈为东
审核	蔡金彬
工程负责人	赖伟胜
专业负责人	赖伟胜
专业负责人助理	蔡大林
校对	佟肇雄
设计	陈培基
制图	陈培基

图别	图号
版本号	日期
版本号	日期
版本号	日期


专业	姓名	日期
建筑		
结构		
专业	姓名	日期
电气		
给排水		
暖通		

调整后

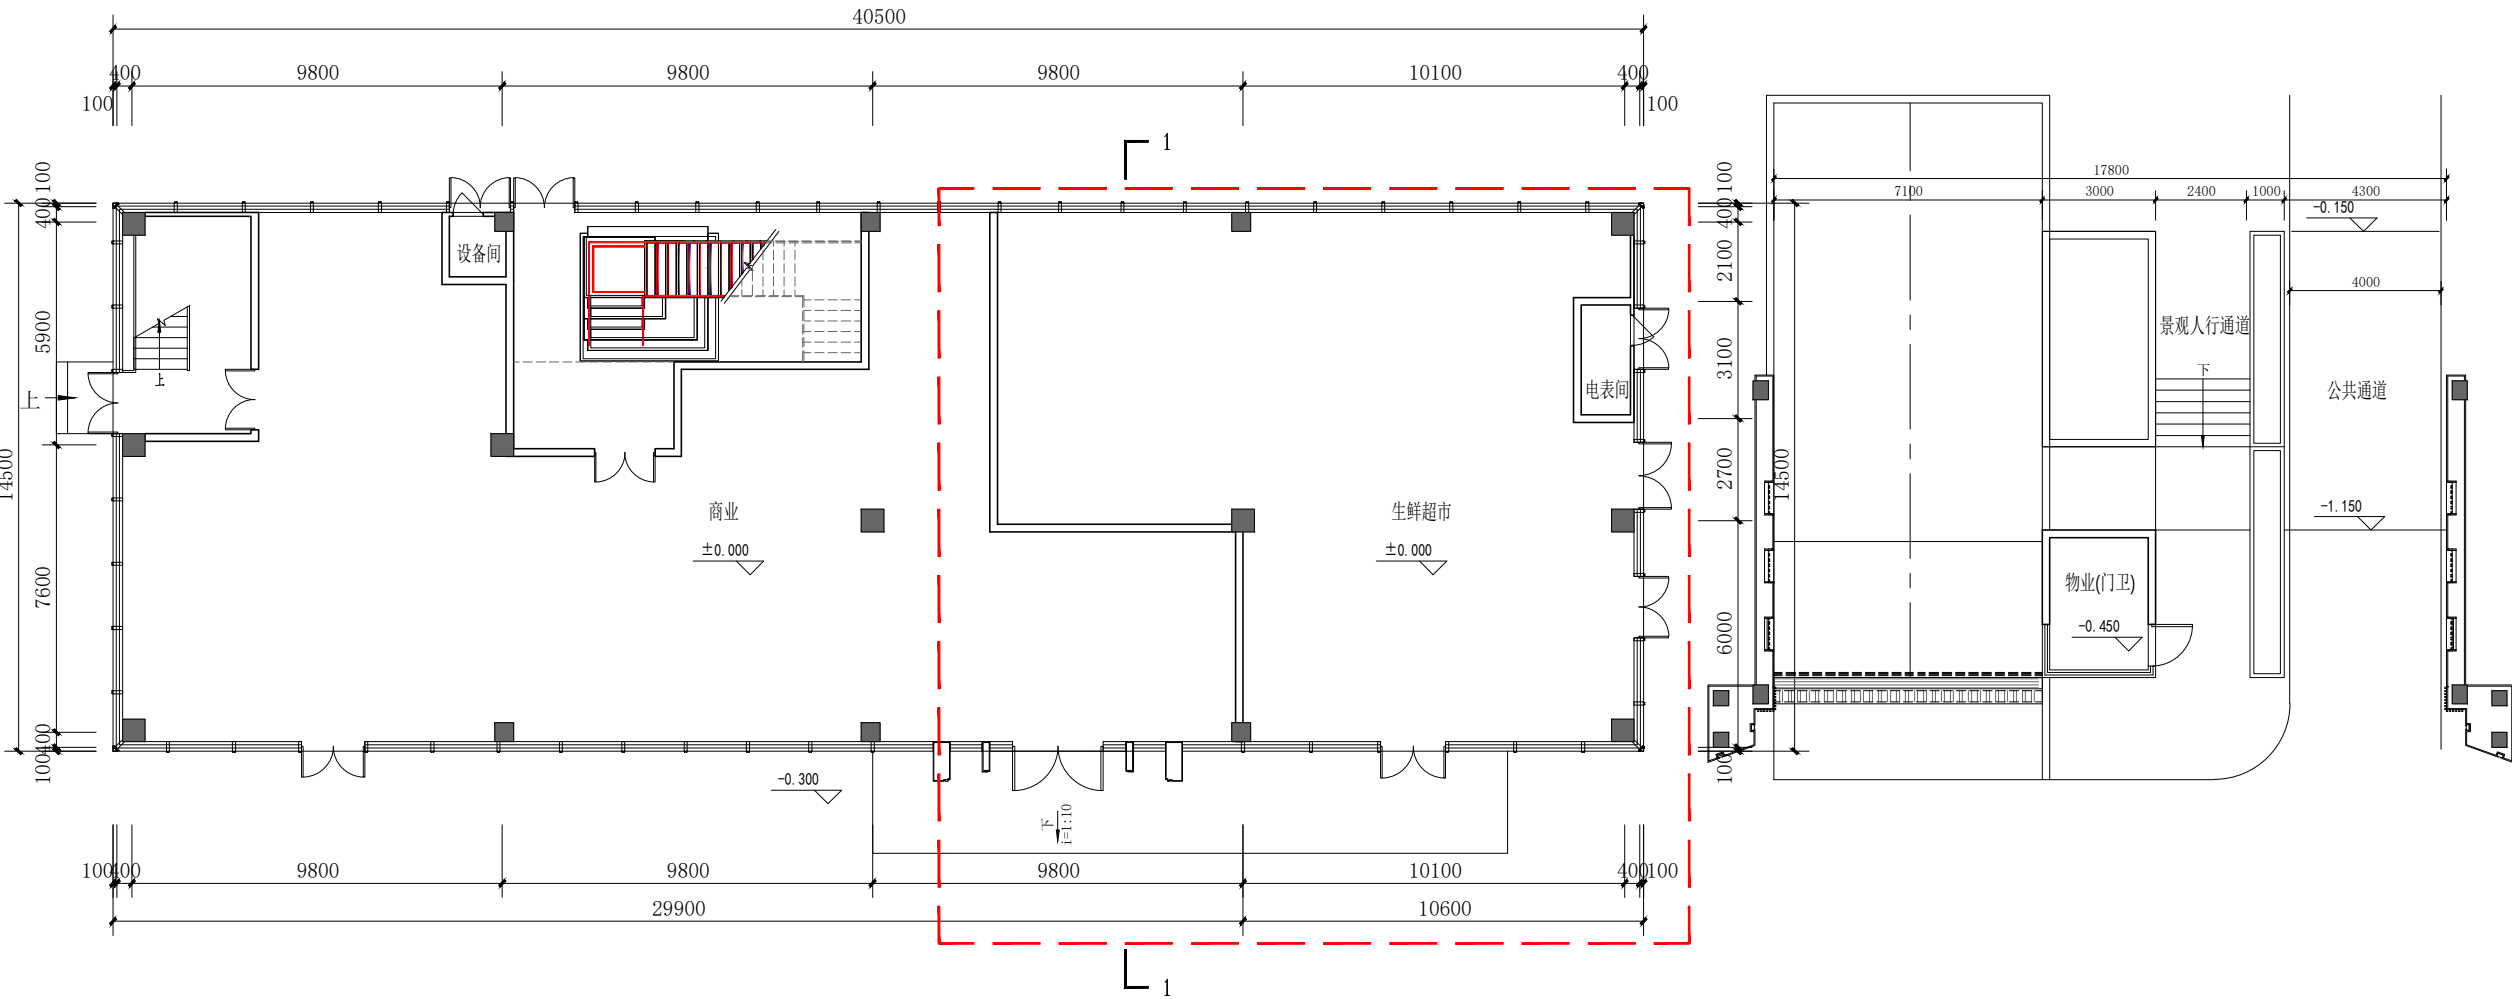


7#楼一层平面图 1:200

本层建筑面积: 598.95m²
本层计容建筑面积: 598.95m²

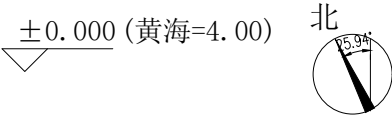

区位示意

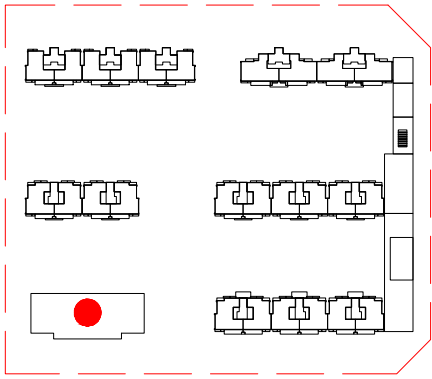

合作单位

出图章

注册建筑师执业章

注册工程师执业章

本图纸须经建设、规划、消防、审查等相关部门
审批通过后方可作为正式施工图纸

施工图审查单位

施工图审查合格书编号

建设单位
平潭仁新置业有限公司

工程名称
2019G067地块

子项名称
7#楼

图名
一层平面图


工程编号

审定	陈为东
审核	蔡金彬
工程负责人	赖伟胜
专业负责人	赖伟胜
专业负责人助理	蔡大林
校对	佟肇雄
设计	陈培基
制图	陈培基


图别	图号
版本号	日期

专业	姓名	日期	专业	姓名	日期
建筑			电气		
结构			给排水		
			暖通		

调整前

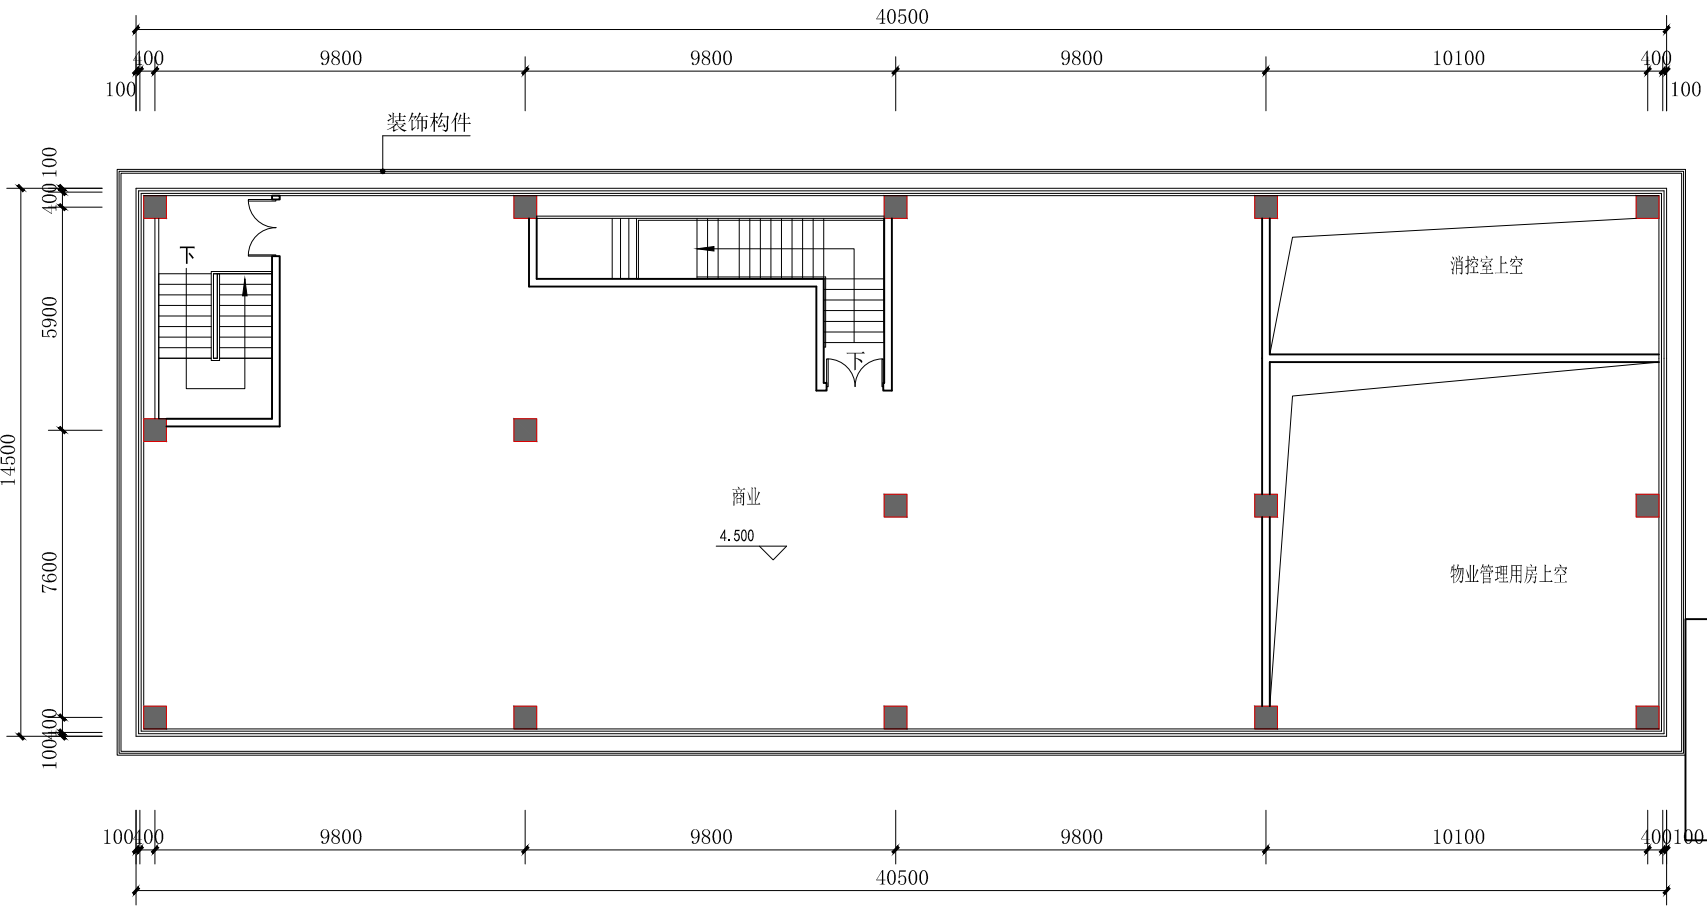

区位示意

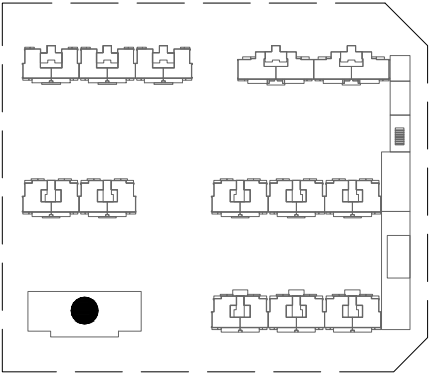

厦门上城建筑设计有限公司

XIAMEN U-TOWN ARCHITECTURE DESIGN INSTITUTE CO.,LTD.

资质证书编号: A135007271

合作单位

出图章

注册建筑师执业章

注册工程师执业章

本图纸须经建设、规划、消防、审查等相关部门
审批通过后方可作为正式施工图纸

施工图审查单位

施工图审查合格书编号

建设单位
平潭仁新置业有限公司

工程名称
2019G067地块

子项名称
7#楼

图名
二层平面图

工程编号

审 定
陈为东

审 核
蔡金彬

工程负责人
赖伟胜

专业负责人
赖伟胜

专业负责人助理
蔡大林

校对
佟肇雄

设计人
陈培基

制图人
陈培基

图 别
图 号


版本号
日期
版本号
日期

7#楼二层平面图 1:200

本层计容建筑面积: 435.00m²

专业	姓名	日期
建筑		
结构		
电气		
给排水		
暖通		


调整后

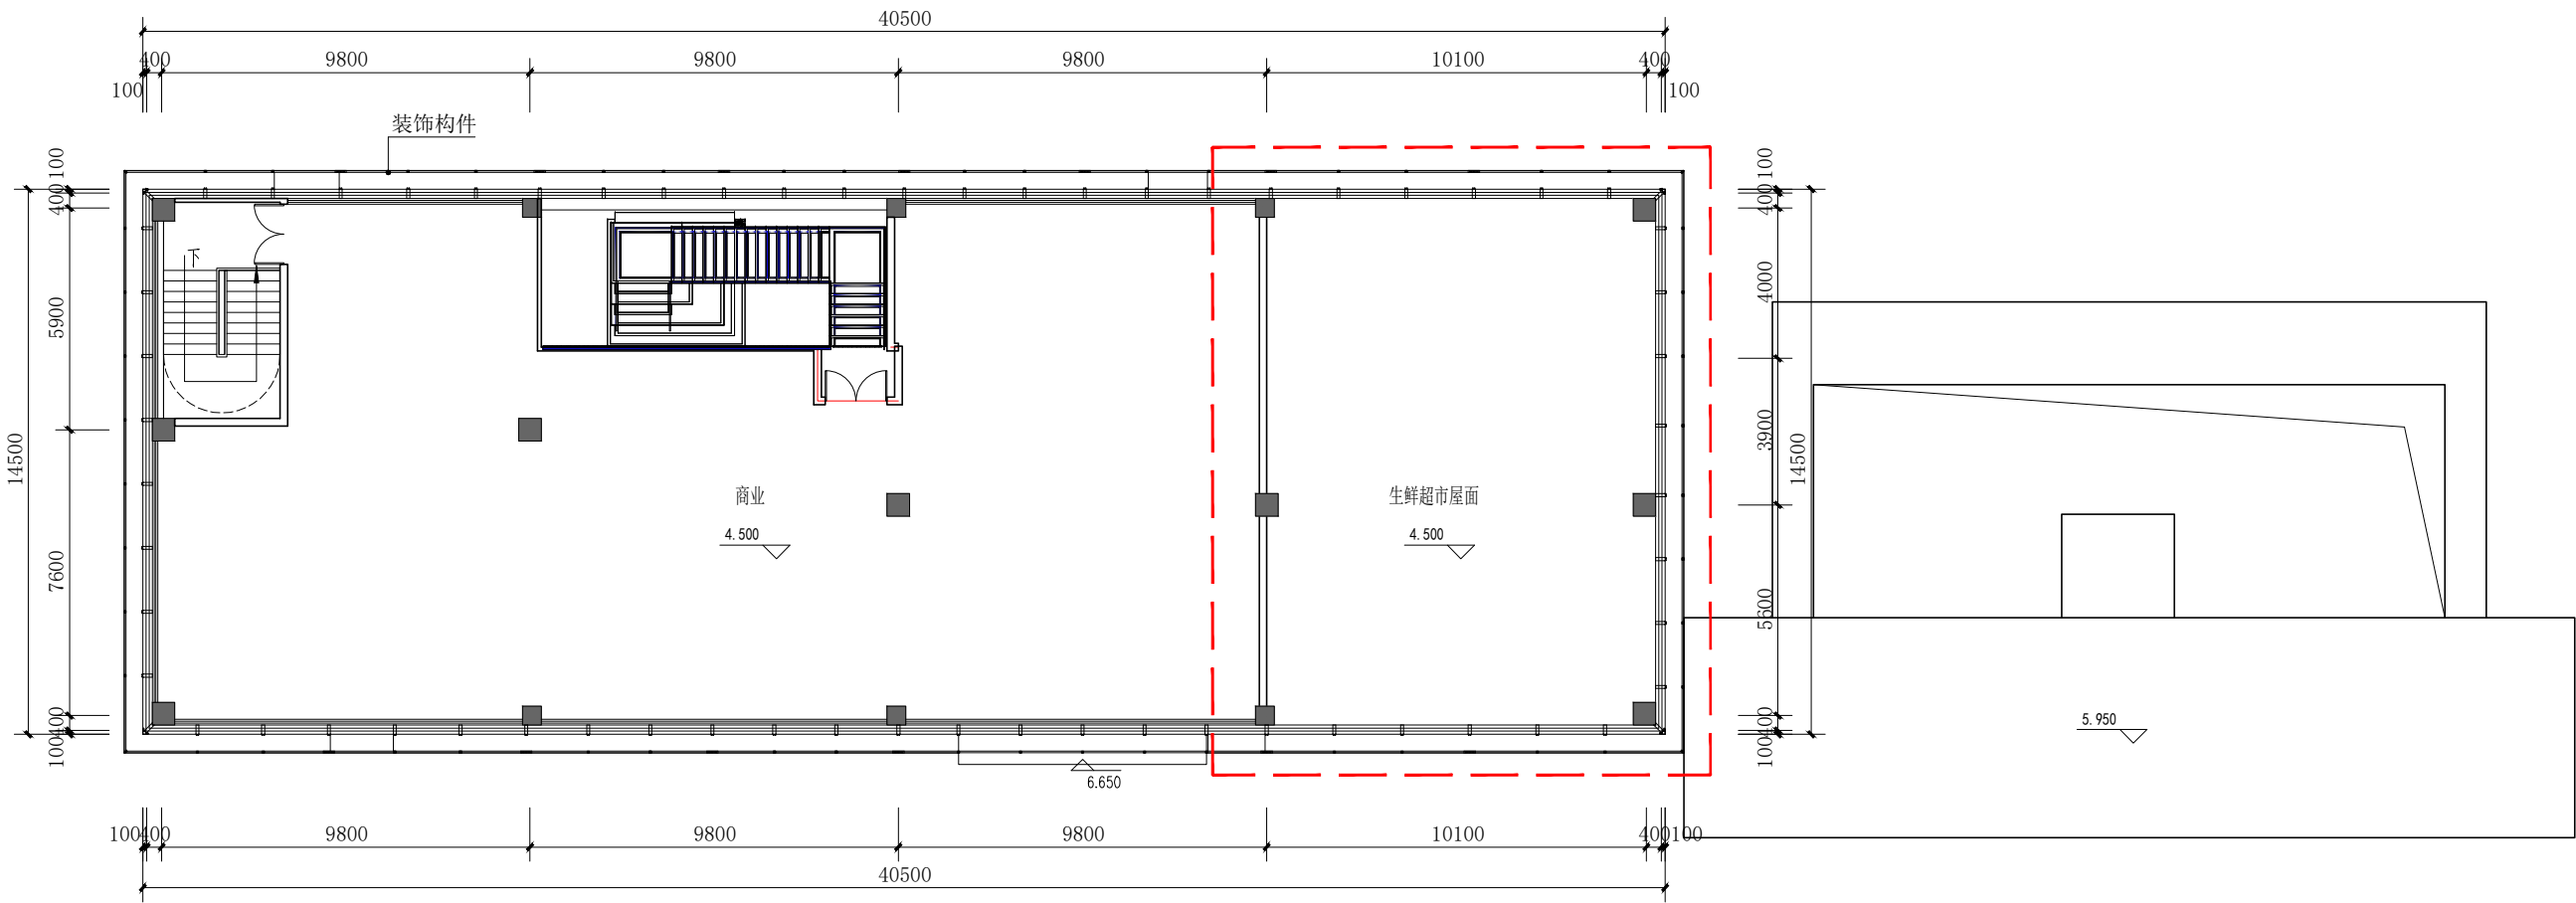

7#楼二层平面图 1:200

本层计容建筑面积：435.00m²

区位示意

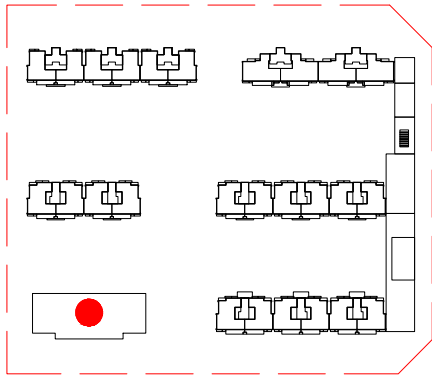

合作单位

出图章

注册建筑师执业章

注册工程师执业章

本图纸须经建设、规划、消防、审查等相关部门
审批通过后方可作为正式施工图纸

施工图审查单位

施工图审查合格书编号

建设单位
平潭仁新置业有限公司

工程名称
2019G067地块

子项名称
7#楼

图名
二层平面图

工程编号

审 定	陈为东	
审 核	蔡金彬	
工程负责人	赖伟胜	
专业负责人	赖伟胜	
专业负责人助理	蔡大林	
校对人	佟肇雄	
设计人	陈培基	
制图人	陈培基	

图 别		图 号	
版本号	日期	版本号	日期