


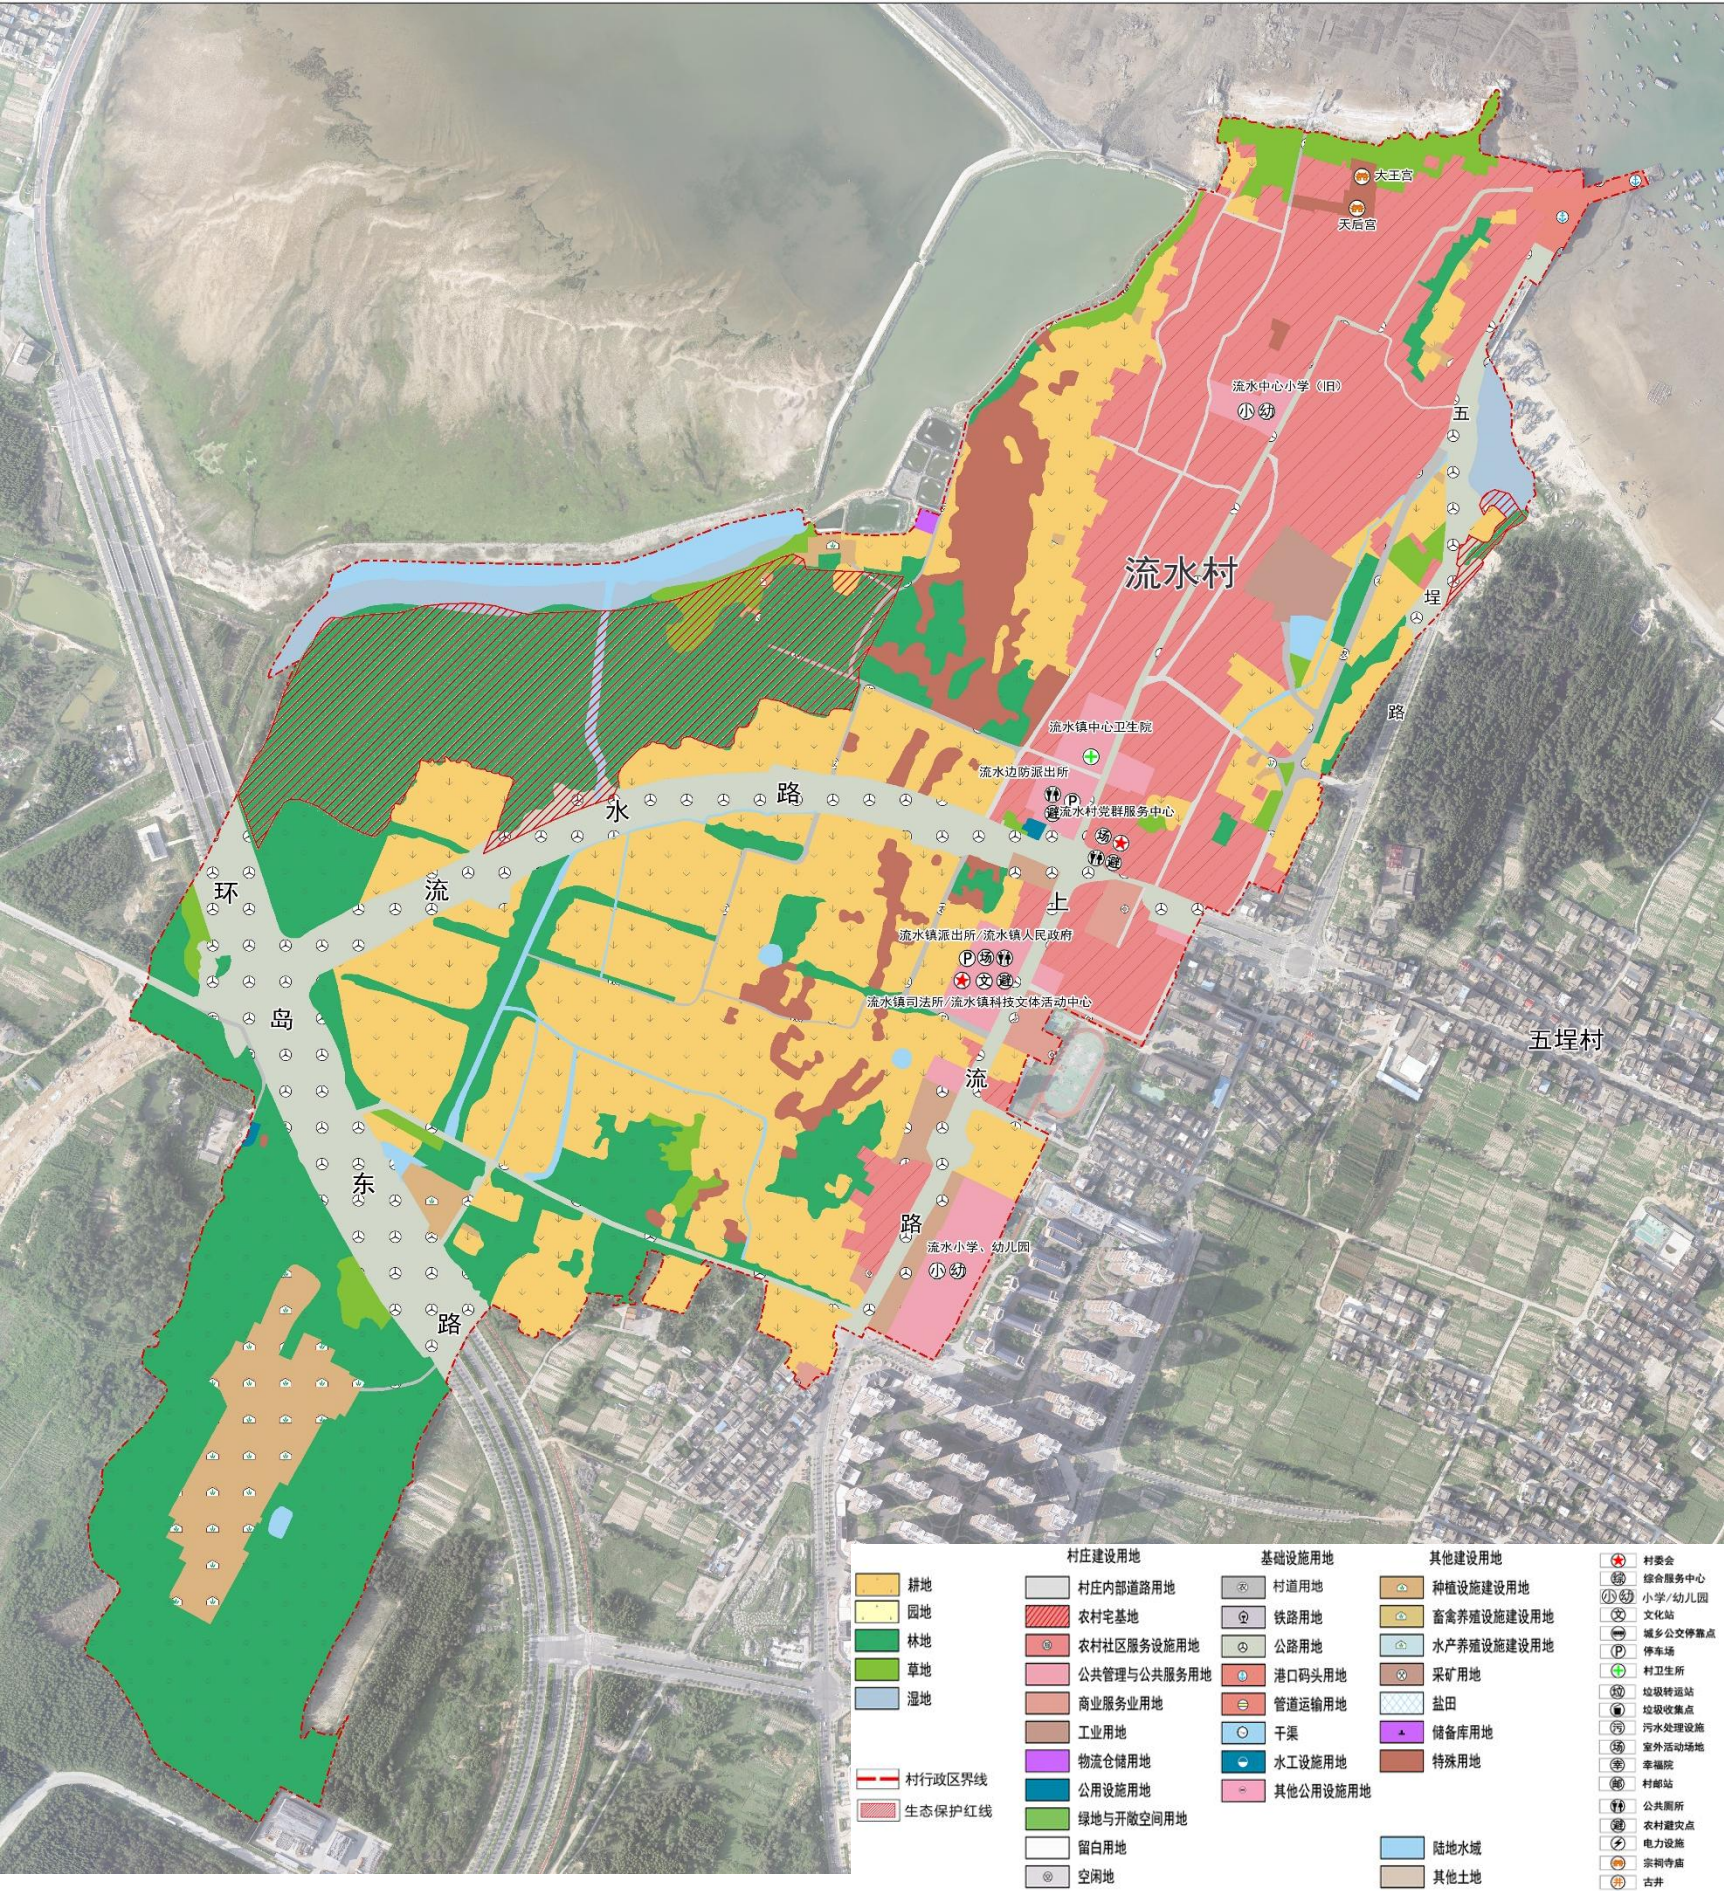


全域土地利用现状

根据“三调”村域内现有村庄建设用地33.19公顷、基础设施用地16.48公顷；其他建设用地6.04公顷。现状人均建设用地为82.97m²/人。

用地用海类型					规划基期年		
					面积（公顷）	比重（%）	
耕地（01）					36.31	24.18	
园地（02）					0.00	0.00	
林地（03）					41.96	27.95	
草地（04）					4.08	2.72	
湿地（05）					2.38	1.58	
合计					84.73	56.43	
农业设施 建设用地	村道用地				1.79	1.19	
	种植设施建设用地				4.71	3.14	
	畜禽养殖设施建设用地				0.00	0.00	
	水产养殖设施建设用地				0.00	0.00	
	合计				6.50	4.33	
村域建设 用地	村域城乡 建设用地	城镇用地			0.00	0.00	
		居住用地	农村社区服务设施用地		0.00	0.00	
			农村宅基地		25.00	16.65	
		公共管理与公共服务用地			4.09	2.72	
		商业服务业用地			0.84	0.56	
		工业用地			0.86	0.58	
		仓储用地			0.06	0.04	
		村庄内部道路用地			1.26	0.84	
		交通场站用地			1.00	0.67	
		其他交通设施用地			0.00	0.00	
		公用设施用地			0.08	0.05	
		绿地与开敞空间用地			0.00	0.00	
		留白用地			0.00	0.00	
		空闲地			0.00	0.00	
		合计			33.19	22.11	
		合计				33.19	22.11
		区域基础设施用地				16.48	10.98
	其他建设用地				6.04	4.02	
合计					55.70	37.10	
陆地水域					3.21	2.14	
渔业用海					0.00	0.00	
工矿通信用海					0.00	0.00	
交通运输用海					0.00	0.00	
游憩用海					0.00	0.00	
特殊用海					0.00	0.00	
其他土地					0.00	0.00	
其他海域					0.00	0.00	
总计					150.14	100.00	



◆ 村域综合规划图

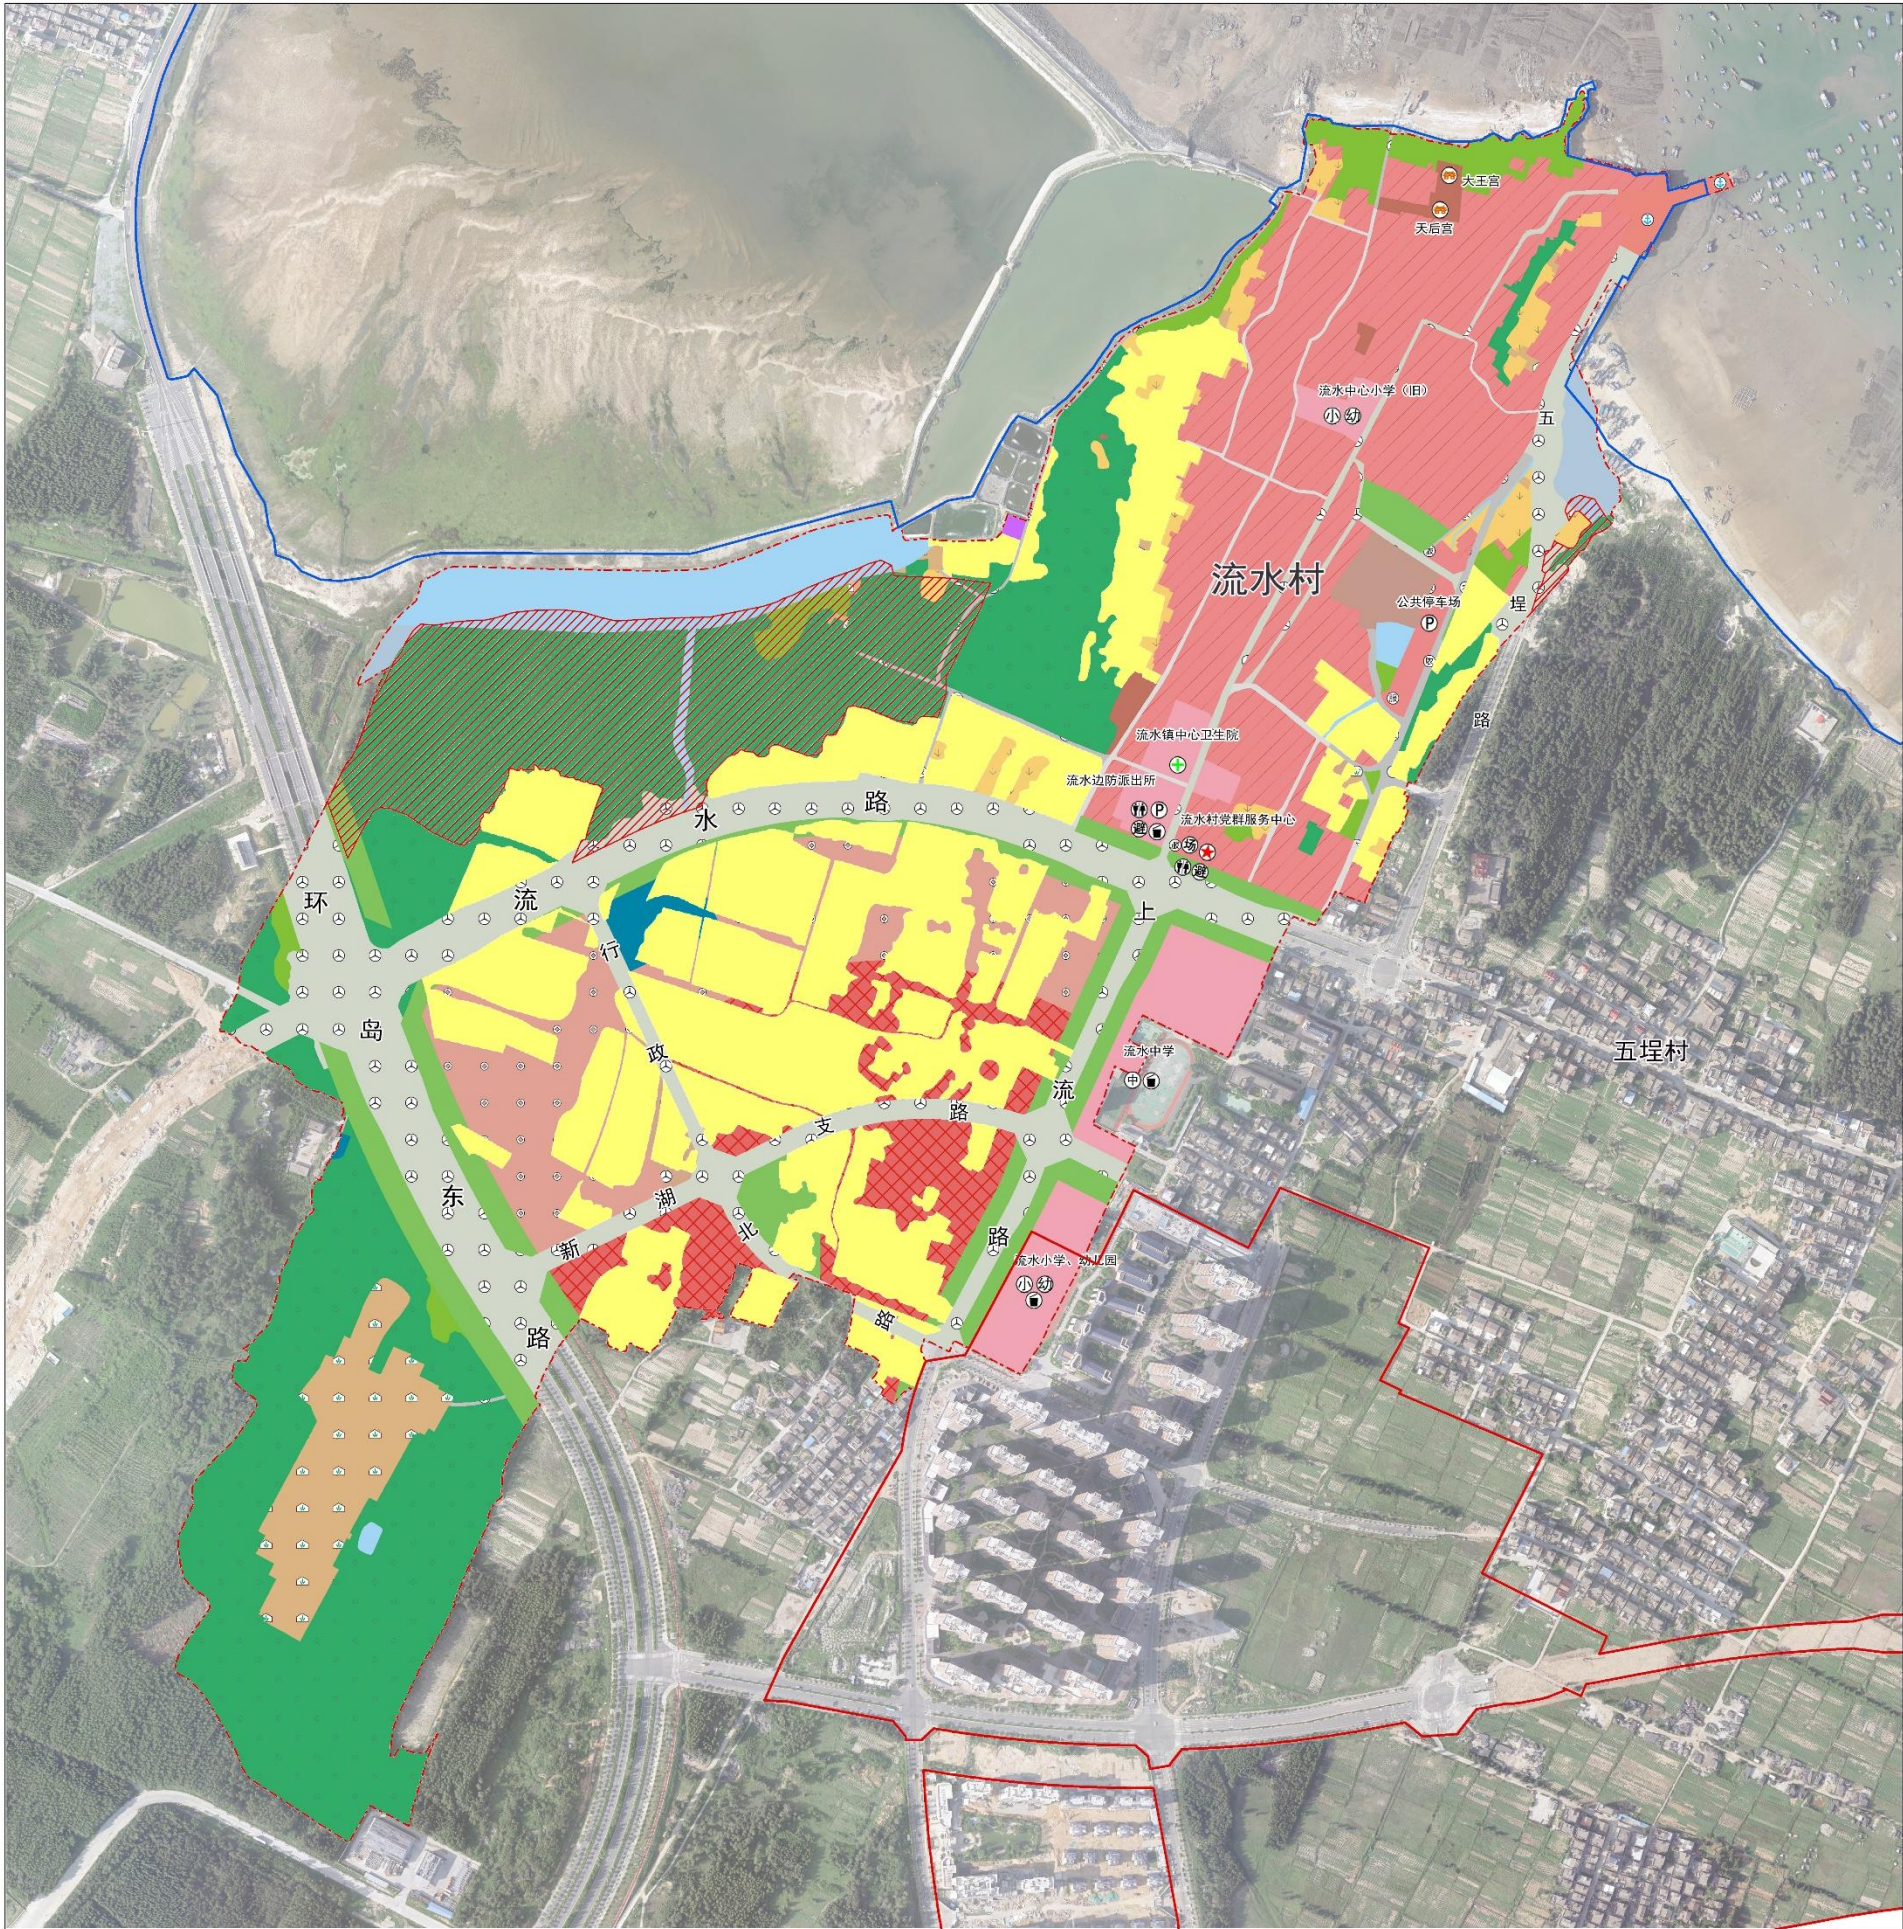

空间功能结构调整表							
用地用海类型			规划基期年		规划目标年		
			面积（公顷）	比重（%）	面积（公顷）	比重（%）	
耕地（01）			36.31	24.18	31.12	20.72	
园地（02）			0.00	0.00	0.00	0.00	
林地（03）			41.96	27.95	35.59	23.70	
草地（04）			4.08	2.72	2.80	1.87	
湿地（05）			2.38	1.58	0.95	0.63	
合计			84.73	56.43	70.45	46.92	
农业设施建设用地	村道用地		1.79	1.19	1.25	0.83	
	种植设施建设用地		4.71	3.14	0.00	0.00	
	畜禽养殖设施建设用地		0.00	0.00	0.00	0.00	
	水产养殖设施建设用地		0.00	0.00	4.21	2.80	
	合计		6.50	4.33	5.46	3.63	
村域建设用地	村域城乡建设用地	城镇用地		0.00	0.00	24.28	16.17
		居住用地	农村社区服务设施用地	0.00	0.00	0.67	0.45
			农村宅基地	25.00	16.65	21.18	14.11
		公共管理与公共服务用地		4.09	2.72	1.59	1.06
		商业服务业用地		0.84	0.56	0.00	0.00
		工业用地		0.86	0.58	0.89	0.59
		仓储用地		0.06	0.04	0.06	0.04
		村庄内部道路用地		1.26	0.84	0.93	0.62
		交通场站用地		1.00	0.67	0.02	0.01
		其他交通设施用地		0.00	0.00	0.00	0.00
		公用设施用地		0.08	0.05	0.04	0.02
		绿地与开敞空间用地		0.00	0.00	0.71	0.47
		留白用地		0.00	0.00	0.00	0.00
		空闲地		0.00	0.00	0.00	0.00
	合计		33.19	22.11	26.08	17.37	
	合计		33.19	22.11	50.36	33.54	
	区域基础设施用地		16.48	10.98	18.46	12.30	
	其他建设用地		6.04	4.02	0.60	0.40	
	合计		55.70	37.10	69.42	46.24	
	陆地水域		3.21	2.14	4.81	3.20	
渔业用海		0.00	0.00	0.00	0.00		
工矿通信用海		0.00	0.00	0.00	0.00		
交通运输用海		0.00	0.00	0.00	0.00		
游憩用海		0.00	0.00	0.00	0.00		
特殊用海		0.00	0.00	0.00	0.00		
其他土地		0.00	0.00	0.00	0.00		
其他海域		0.00	0.00	0.00	0.00		
总计		150.14	100.00	150.14	100.00		



规划一张表

用地用海类型				规划基期年		规划目标年		用地调整（公顷）	
				面积（公顷）	比重（%）	面积（公顷）	比重（%）		
耕地（01）				36.31	24.18	31.12	20.72	-5.19	
园地（02）				0.00	0.00	0.00	0.00	0.00	
林地（03）				41.96	27.95	35.59	23.70	-6.38	
草地（04）				4.08	2.72	2.80	1.87	-1.28	
湿地（05）				2.38	1.58	0.95	0.63	-1.43	
合计				84.73	56.43	70.45	46.92	-14.28	
农业设施建设用地	村道用地			1.79	1.19	1.25	0.83	-0.54	
	种植设施建设用地			4.71	3.14	0.00	0.00	-4.71	
	畜禽养殖设施建设用地			0.00	0.00	0.00	0.00	0.00	
	水产养殖设施建设用地			0.00	0.00	4.21	2.80	4.21	
合计				6.50	4.33	5.46	3.63	-1.04	
村域建设用地	村域城乡建设用地	城镇用地			0.00	0.00	24.28	16.17	24.28
		居住用地	农村社区服务设施用地		0.00	0.00	0.67	0.45	0.67
			农村宅基地		25.00	16.65	21.18	14.11	-3.82
		公共管理与公共服务用地			4.09	2.72	1.59	1.06	-2.50
		商业服务业用地			0.84	0.56	0.00	0.00	-0.84
		工业用地			0.86	0.58	0.89	0.59	0.02
		仓储用地			0.06	0.04	0.06	0.04	0.00
		村庄内部道路用地			1.26	0.84	0.93	0.62	-0.33
		交通场站用地			1.00	0.67	0.02	0.01	-0.99
		其他交通设施用地			0.00	0.00	0.00	0.00	0.00
		公用设施用地			0.08	0.05	0.04	0.02	-0.05
		绿地与开敞空间用地			0.00	0.00	0.71	0.47	0.71
		留白用地			0.00	0.00	0.00	0.00	0.00
		空闲地			0.00	0.00	0.00	0.00	0.00
		合计			33.19	22.11	26.08	17.37	-7.11
		合计			33.19	22.11	50.36	33.54	17.17
		区域基础设施用地			16.48	10.98	18.46	12.30	1.98
		其他建设用地			6.04	4.02	0.60	0.40	-5.44
	合计				55.70	37.10	69.42	46.24	13.72
	陆地水域				3.21	2.14	4.81	3.20	1.60
	渔业用海				0.00	0.00	0.00	0.00	0.00
	工矿通信用海				0.00	0.00	0.00	0.00	0.00
交通运输用海				0.00	0.00	0.00	0.00	0.00	
游憩用海				0.00	0.00	0.00	0.00	0.00	
特殊用海				0.00	0.00	0.00	0.00	0.00	
其他土地				0.00	0.00	0.00	0.00	0.00	
其他海域				0.00	0.00	0.00	0.00	0.00	
总计				150.14	100.00	150.14	100.00	0.00	


序号	指标	属性	单位	现状基期年	规划目标年
一、村庄发展性指标					
1	村域建设用地总面积	约束性	公顷	55.70	69.42
2	村域城乡建设用地面积	约束性	公顷	33.19	50.36
3	村庄建设用地规模	预期性	公顷	33.19	26.08
4	公共管理与公共服务用地规模	预期性	公顷	4.09	1.59
5	公用设施用地规模	预期性	公顷	0.08	0.04
6	人均村庄建设用地面积	预期性	平方米/人	82.97	75.31
二、村庄保护性指标					
7	生态保护红线面积	约束性	公顷	14.82	14.82
8	永久基本农田保护面积	约束性	公顷	31.22	31.22
9	耕地保有量	约束性	公顷	36.31	31.12
10	林地保有量	约束性	公顷	41.96	35.59
11	湿地面积	约束性	公顷	2.38	0.95
12	大陆自然海岸线保有率	约束性	%	80	90
13	自然和文化遗产	预期性	处	0.00	0.00




平潭综合实验区君山片区流水村村庄规划（2022-2035）

VILLAGE PLANNING OF LIUSHUI VILLAGE, PINGTAN TOWN

农村居民点规划布局图

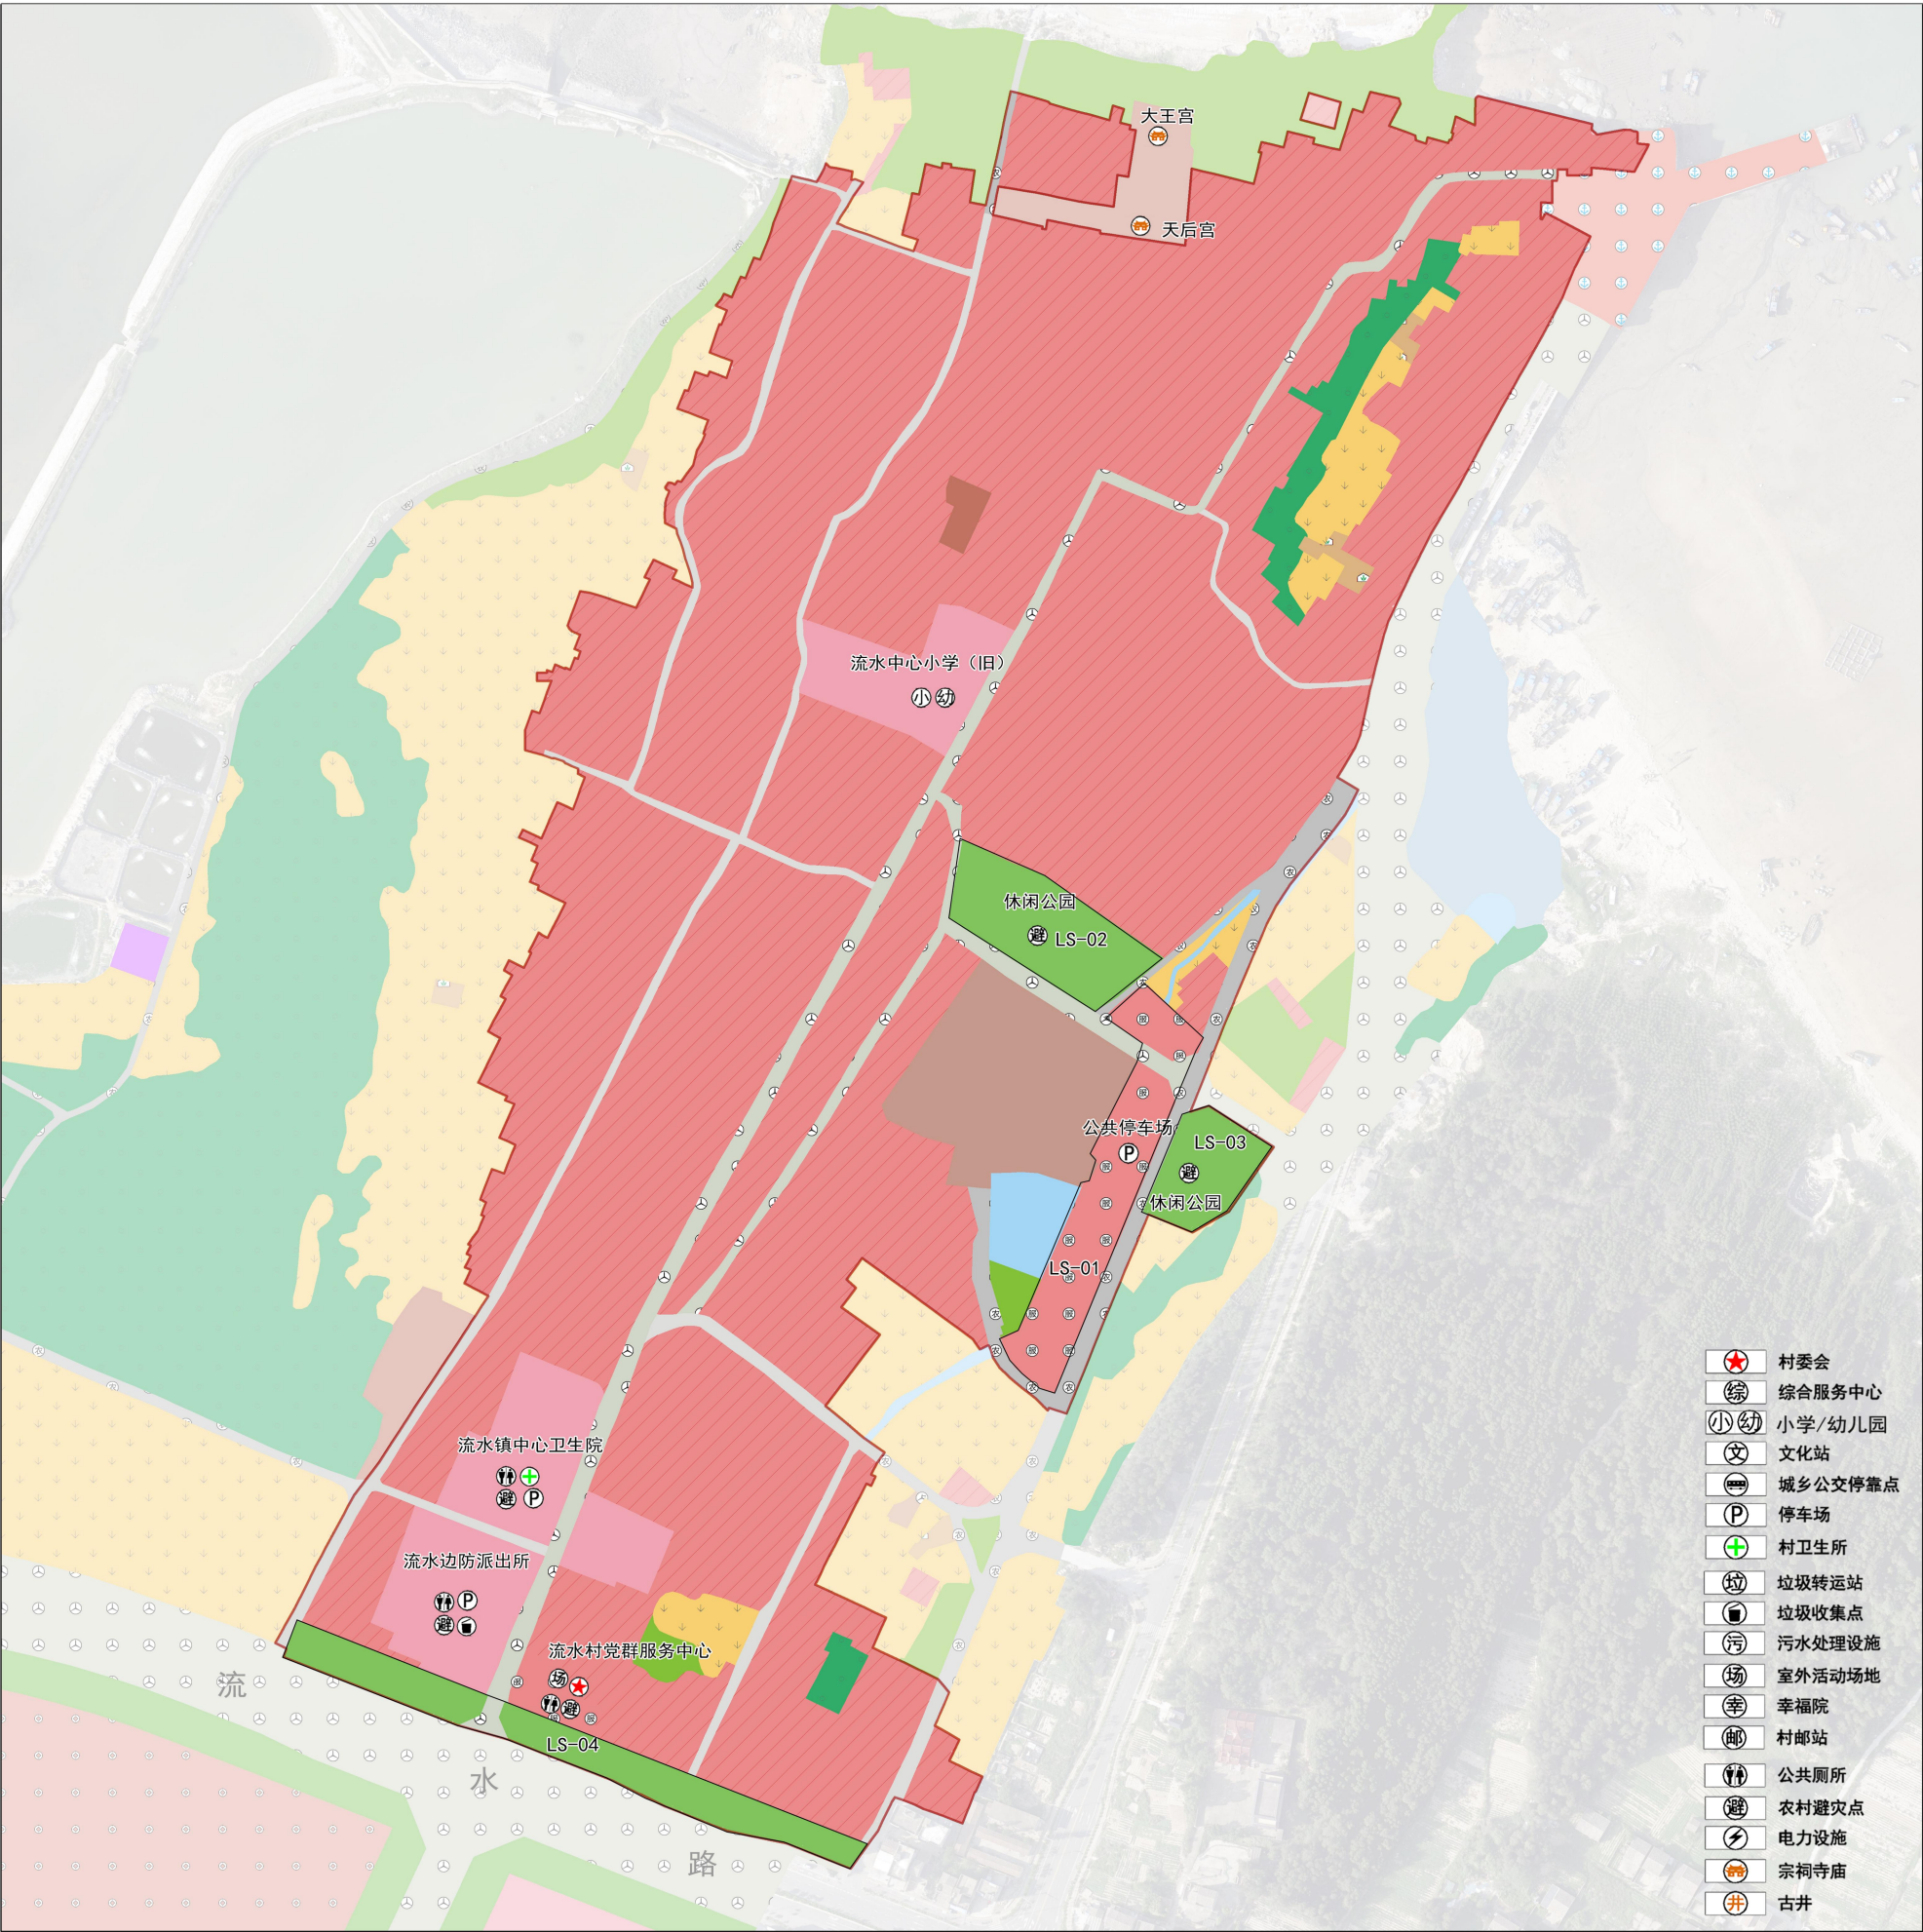

风玫瑰与比例尺

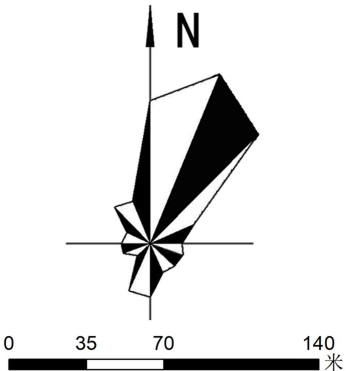

区位图



图例

- 村行政区界线

耕地

林地

草地

湿地

园地

弹性发展空间

村庄建设边界
- 村庄建设用地

村庄内部道路用地

农村宅基地

农村社区服务设施用地

公共管理与公共服务用地

公用设施用地

绿地与开敞空间用地

工业用地
- 基础设施用地

村道用地

公路用地

港口码头用地

干渠

水工设施用地
- 其他建设用地

种植设施建设用地

特殊用地

陆地水域

其他土地

指标一览表

地块编号	用地		用地面积	户数		建筑高度	名称	备注
	用地代码	用地性质		现状户数	规划户数			
LS-01	0704	农村社区服务设施用地	5705	0	0	限高9m	公共停车场	落位流水组团单元控规，合理利用水产冷冻厂东侧空闲地修建停车场，并增设相关配套设施
LS-02	1401	公园绿地	4425	0	0	限高9m	健身广场	合理利用村内空闲地，提升改造室外健身活动场地；配套健身器材
LS-03	1401	公园绿地	2446	0	0	限高9m	休闲公园	利用新建停车场东侧的空闲地，打造休闲公园，给居民提供休闲娱乐场所
LS-04	1401	公园绿地	879	0	0	限高9m	口袋公园	流水路旁空闲地，打造休闲漫步的口袋公园，提升村庄形象

管制规则

村庄公共设施：流水村现状村庄公共基础设施完善，规划主要以维护为主，可将现状宗祠寺庙进行提升改造，设置成老年人活动场所，有条件的新增相关配套设施；合理利用村内空闲地，新建两处休闲公园，有条件的可增设部分健身器材。

道路交通设施：现状对外交通主要由流水路及村内主干道承当，村庄内部道路交通沿用村中已有的道路，在原有的基础上维护并衔接部分流水组团单元控规路网；拆除部分质量较差建筑，优化道路线行，满足道路规范要求；利用村西侧空闲地修建停车场。


市政设施：沿道路按30~50m距离设置垃圾收集点，按服务半径约300m配建公厕，服务游客和村民；完善村庄水电配套，远期采用雨污分离排放模式，按照不大于120m的距离配建消防栓，文保单位重点设置。

村庄住宅管制：村庄居民点住宅建筑以保留及改造为主，原则上不大量新增宅基地，严禁核心保护区内开发建设村民住宅，建设控制地带内严控建设高度、体量、色彩，严格按照本次设计户型建设，风貌与村落协调一致。建筑严格按照“一户一宅”政策，每户宅基地面积控制在120m²以内，新建住宅建筑层数不超过3层，高度不得超过14m，每户住宅面积控制在300m²以内，住宅建筑间距与前建筑高度比不低于1:1，相邻建筑山墙间距不低于4m，建筑宜朝南、南偏东或偏西布置，建筑后退村庄道路不得少于1m。


根据《福建省村庄规划编制指南（试行）》中指出：“对村民进行集中安置的新村安置小区、公共服务设施、经营性用地可根据需求适当增加建筑高度，原则上不应超过 6 层。”新建住宅每户住宅占地面积控制120m²以内。



主要农村居民点总平面示意图

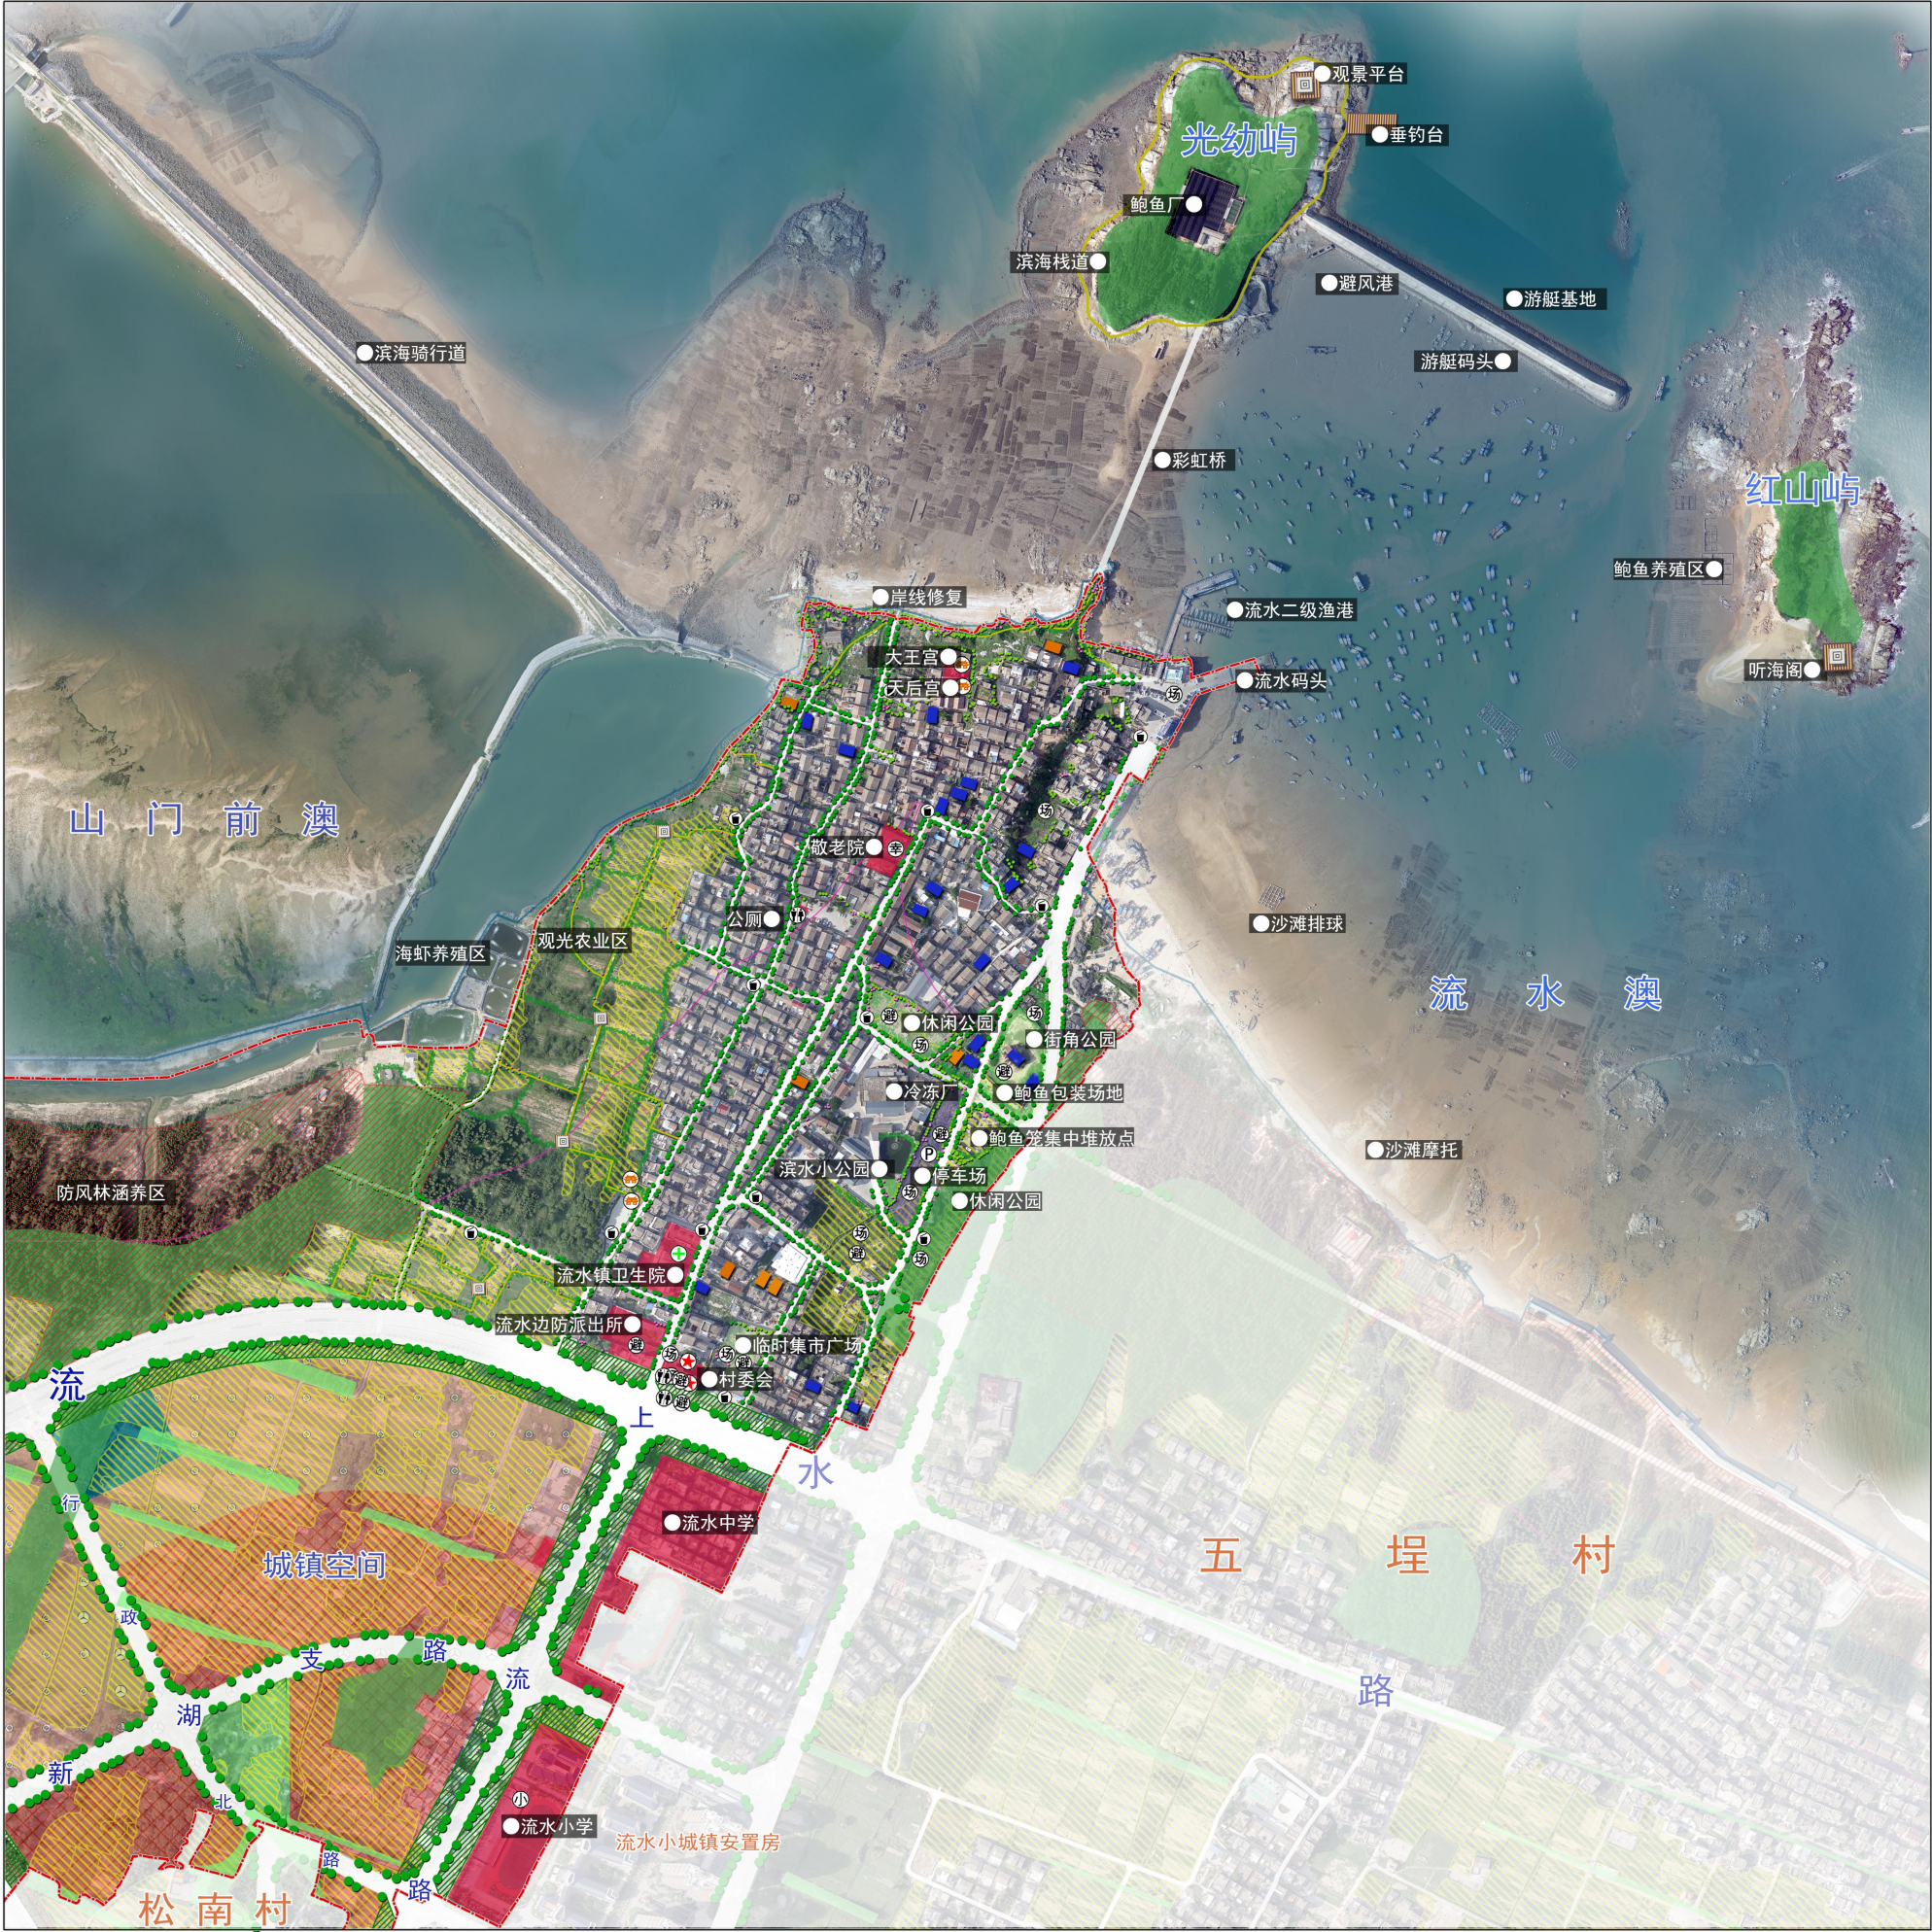

风玫瑰与比例尺

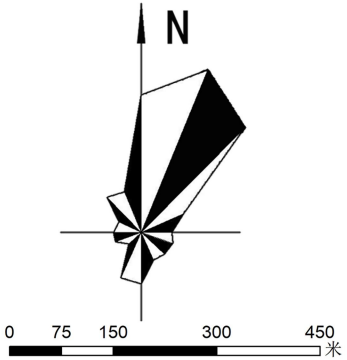

区位图



图例

	村行政区划线		保留建筑		村委会		室外活动场地		城乡公交停靠点
	海岸线		保留建筑		综合服务中		幸福院		停车场
	县级生态公益林		新建建筑		文化站		村卫生所		垃圾转运站
	省级生态公益林		公共建筑		中学		集贸市场		垃圾收集点
	海岸退距线				小学		村邮站		污水处理设施
	永久基本农田				幼儿园		公共厕所		农村避灾点
	生态保护红线				宗祠寺庙		供水设施		电力设施
	道路退距防护绿地								

建设方案指引

9mX13m地块
(二层住宅模式)



村民建房应当遵守以下技术标准规定：

(一) 规划：村民建房要符合国土空间总体规划及各类专项规划，靠近城市、县城、乡镇所在地住宅小区，引导参照城市居住区规划设计相关标准，鼓励建设多层单元式住宅。

(二) 选址：村民建房选址应避开地质复杂、地基承载力差、地势低洼不易排涝以及易受风口、滑坡、雷电和洪水侵袭等自然灾害影响的地段，杜绝安全隐患问题。

(三)层数和面积：农村独栋式、并联式或联排式自建住宅不得超过三层，每户住宅建筑面积控制在300平方米以内；多层单元式住宅的，每户住宅建筑面积控制在200平方米左右。

(四)层高：一层层高控制在4.8米以内，二层以上层高控制在3.3米以内，建筑总高度不超过14米，建筑屋顶原则上应按坡屋顶设计。

(五)间距和朝向：住宅建筑前后间距与建筑高度比一般不低于1:1，相邻房屋山墙之间（外墙至外墙）的间距不低于4米，建筑宜朝南、朝南偏东或偏西布置。新建建筑宜后退村庄干路红线3米以上，后退村庄支路红线1米以上。

因旧房改造、扩建等受用地条件限制的,根据实际情况由属地乡镇人民政府合理确定相邻距离。

(六)抗震：新建住宅必须符合工程抗震设防要求，板、梁、柱不得采用石结构。

(七)建筑单体：应满足村民生产生活需求，住宅平面布局应设有客厅、卧室、厨房、卫生间、储藏间（农具堆放间）应满足面积、通风、采光等要求。房屋造型简洁美观，宜采用坡屋面，符合地方建筑特色，外观应进行一次性装修。

(八)配套：应同步配建化粪池等处理设施；集中建设住宅小区的，给水排水、电力通信、道路、广电、绿化和社区服务等配套设施要同步规划建设，小区建筑密度控制在30%左右，绿地率不低于30%。

其他细则参考《福州市规范农村宅基地和建房管理实施细则(试行)》。