



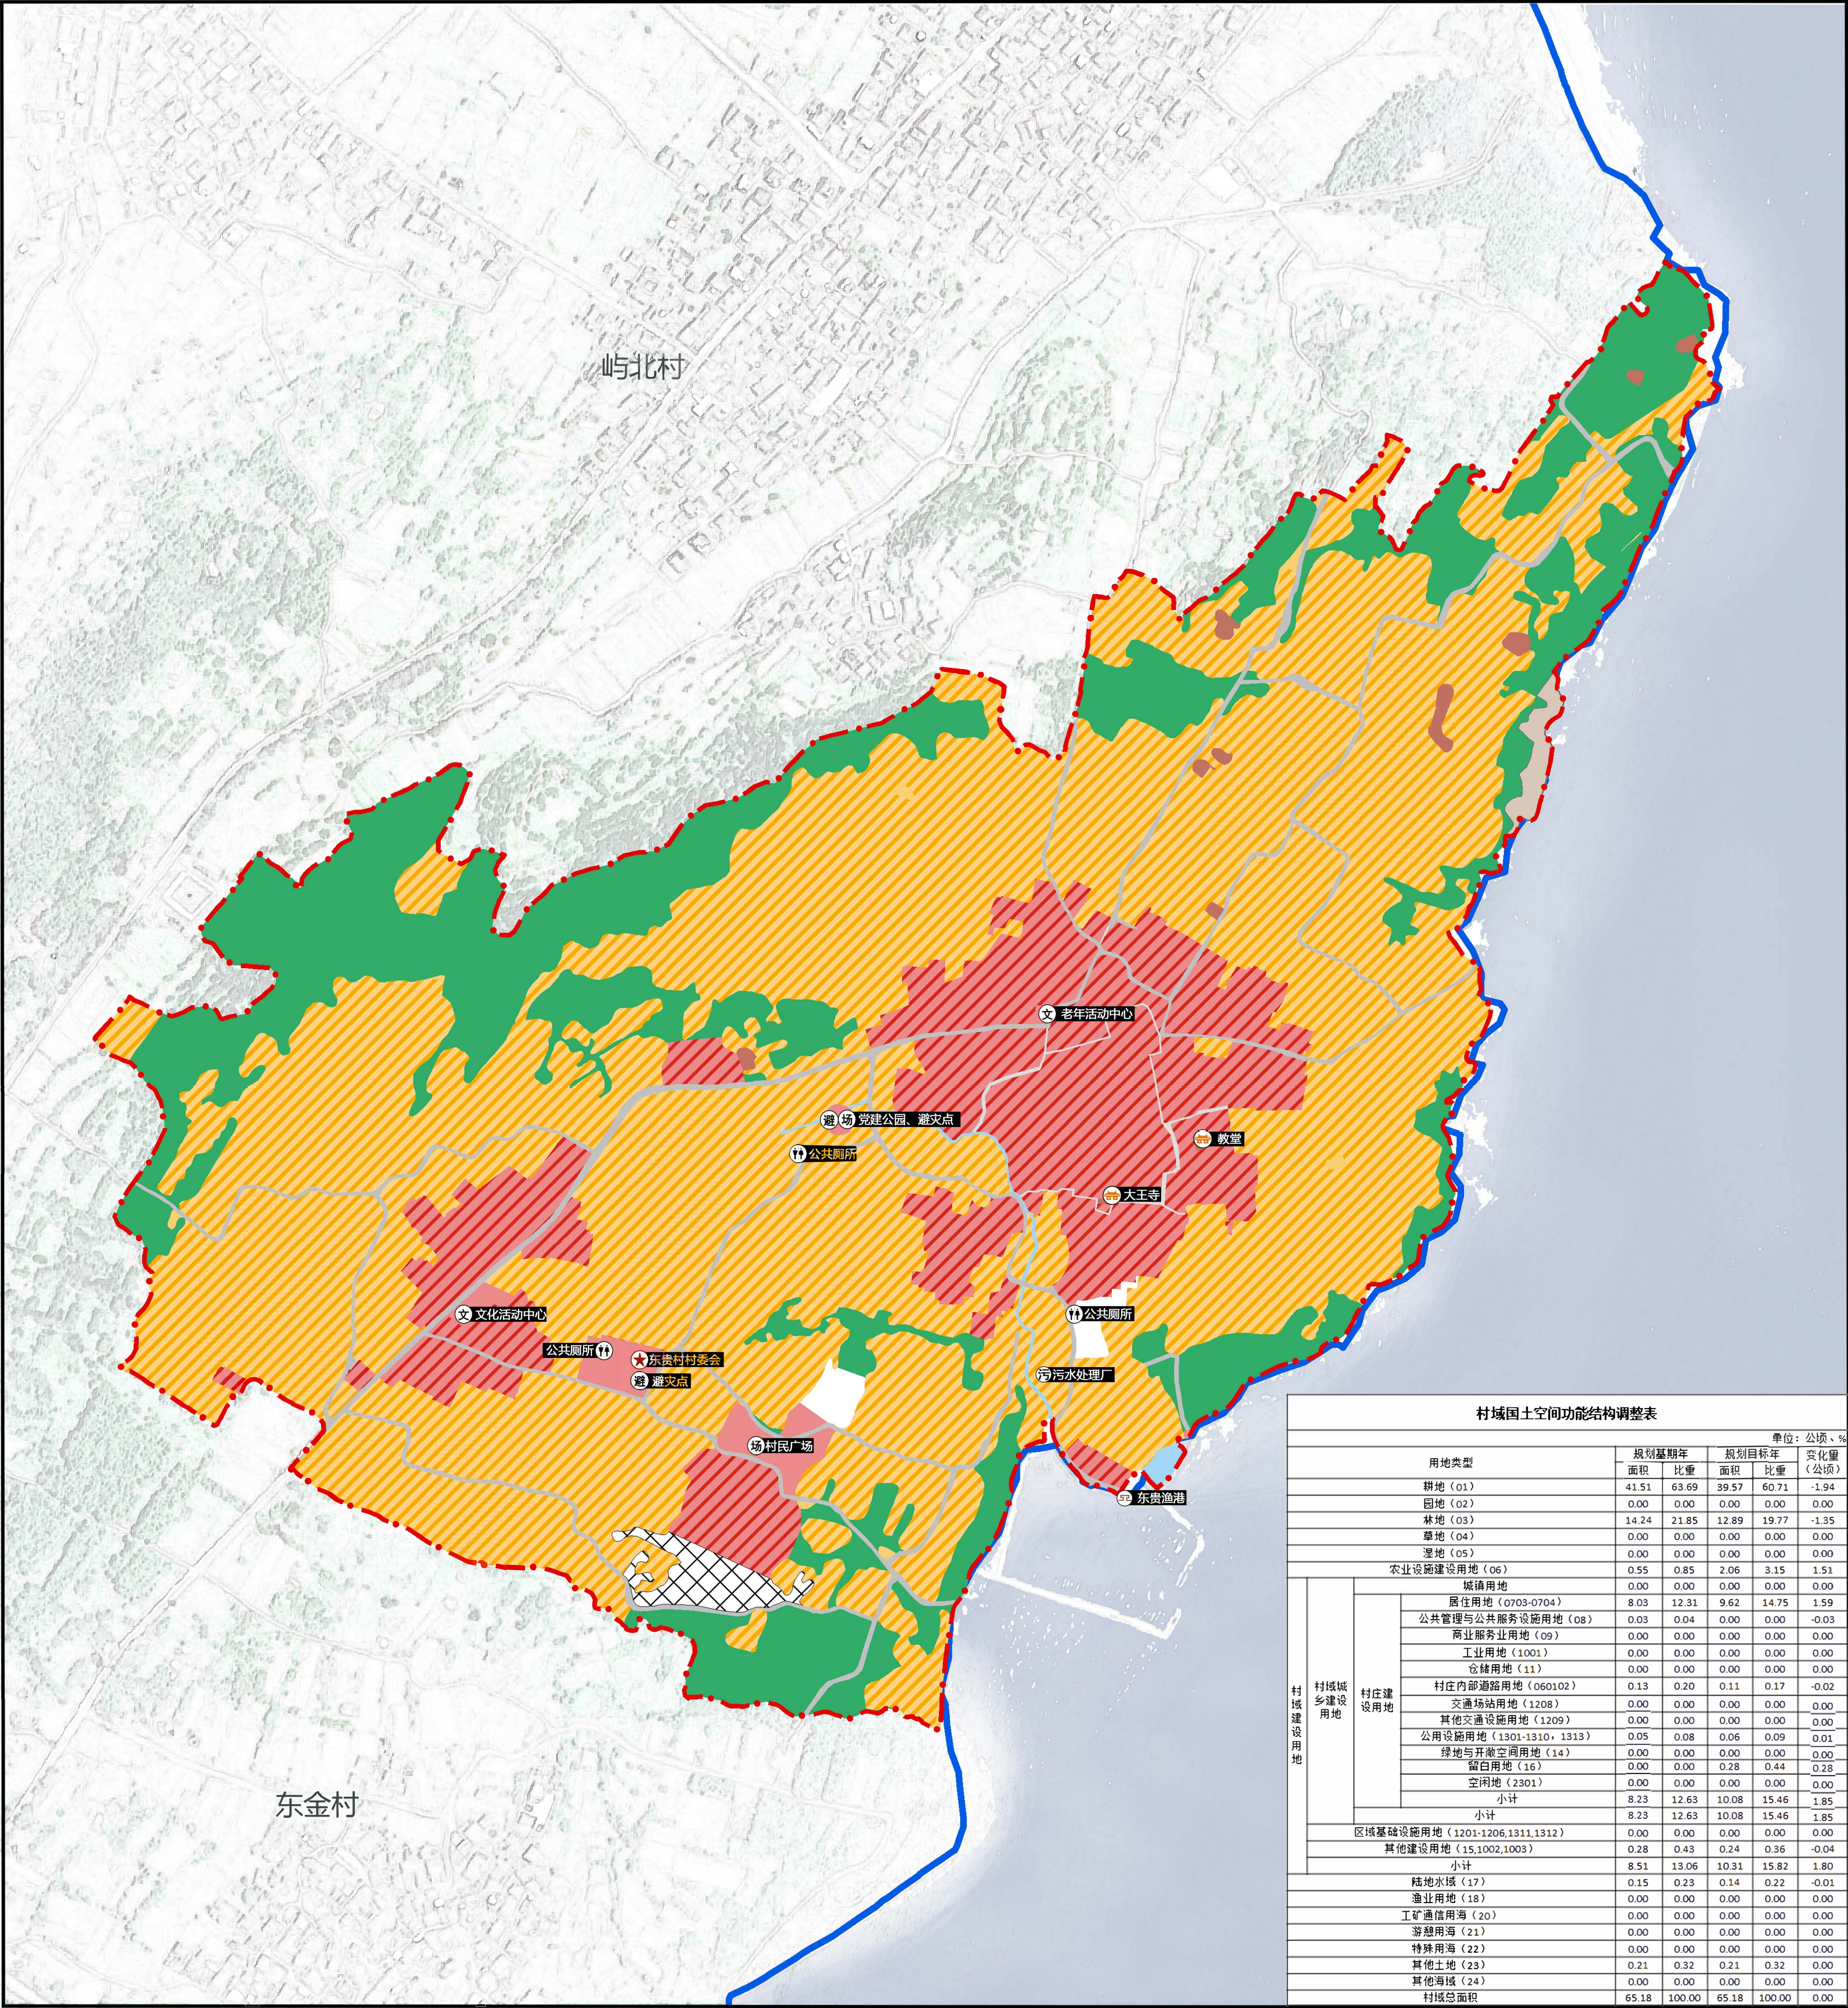

村域国土空间功能结构调整表					
单位:公顷、%					
用地类型	面积	比重	面积	比重	变化量
耕地 (01)	41.51	63.69	39.57	60.71	-1.94
园地 (02)	0.00	0.00	0.00	0.00	0.00
林地 (03)	14.24	21.85	12.89	19.77	-1.35
草地 (04)	0.00	0.00	0.00	0.00	0.00
湿地 (05)	0.00	0.00	0.00	0.00	0.00
农业设施建设用地 (06)	0.55	0.85	2.06	3.15	1.51
城镇用地	0.00	0.00	0.00	0.00	0.00
居住用地 (0703-0704)	8.03	12.31	9.62	14.75	1.59
公共管理与公共服务设施用地 (08)	0.03	0.04	0.00	0.00	-0.03
商业服务业用地 (09)	0.00	0.00	0.00	0.00	0.00
工业用地 (1001)	0.00	0.00	0.00	0.00	0.00
仓储用地 (11)	0.00	0.00	0.00	0.00	0.00
村庄内部道路用地 (060102)	0.13	0.20	0.11	0.17	-0.02
交通场站用地 (1208)	0.00	0.00	0.00	0.00	0.00
其他交通设施用地 (1209)	0.00	0.00	0.00	0.00	0.00
公用设施用地 (1301-1310, 1313)	0.05	0.08	0.06	0.09	0.01
绿地与开敞空间用地 (14)	0.00	0.00	0.00	0.00	0.00
留白用地 (16)	0.00	0.00	0.28	0.44	0.28
空闲地 (2301)	0.00	0.00	0.00	0.00	0.00
小计	8.23	12.63	10.08	15.46	1.85
区域基础设施用地 (1201-1206,1311,1312)	0.00	0.00	0.00	0.00	0.00
其他建设用地 (15,1002,1003)	0.28	0.43	0.24	0.36	-0.04
小计	8.51	13.06	10.31	15.82	1.80
陆地水域 (17)	0.15	0.23	0.14	0.22	-0.01
渔业用地 (18)	0.00	0.00	0.00	0.00	0.00
工矿通信用地 (20)	0.00	0.00	0.00	0.00	0.00
游憩用地 (21)	0.00	0.00	0.00	0.00	0.00
特殊用地 (22)	0.00	0.00	0.00	0.00	0.00
其他土地 (23)	0.21	0.32	0.21	0.32	0.00
其他海域 (24)	0.00	0.00	0.00	0.00	0.00
村域总面积	65.18	100.00	65.18	100.00	0.00

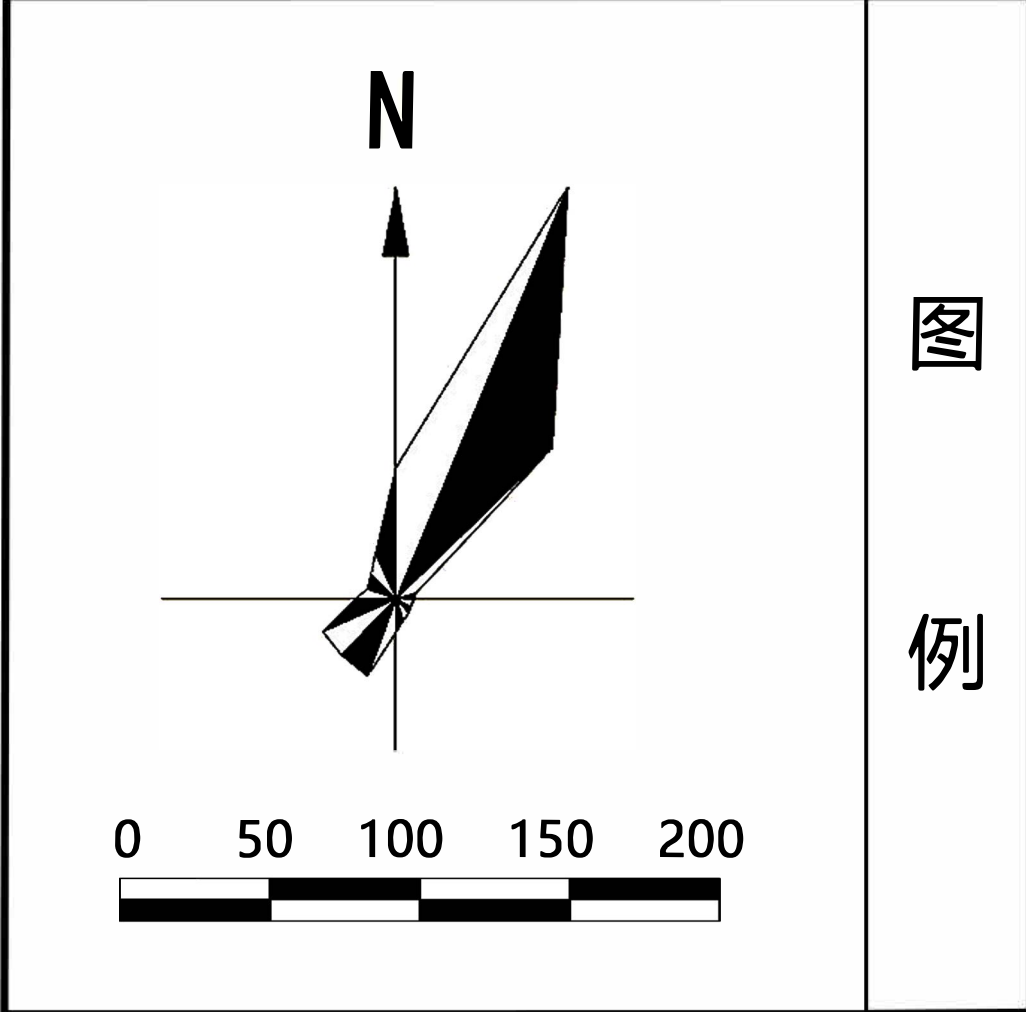

图例

- 村域

永久基本农田

生态保护红线

生态林

村庄建设边界

村庄弹性发展区

海岸线

耕地

园地

林地

草地

村道用地

村庄内部道路用地

种植设施建设用地

禽畜养殖设施建设用地

农村宅基地

农村社区服务设施用地

公共管理与公共服务用地

商业服务业用地

工矿用地

交通运输用地

公路用地

公用设施用地

绿地与开敞空间用地

特殊用地

留白用地

陆地水域

其他土地

村委会

文化活动现场

健身场地

幸福院

村卫生所

公共厕所

污水处理设施


老年活动中心

宗祠、寺庙

平潭综合实验区苏平片区东贵村村庄规划(2022-2035)

农村主要居民点
规划布局图

类型		地块编号	内容	总体要求	要求	说明	管控方式	
存量	村庄建设用地	农村宅基地	CA-01、CA-02、CA-03、CA-04、CA-05、CA-06、CA-07、CA-08、CA-09、CA-10、CA-11、CA-12、CA-13、CA-14、CA-15、CA-16、CA-17、CA-18、CA-19、CA-20	一般住宅区	用地面积：8022.34m ² 建筑限高（H）：H≤12m 容积率（FAR）：1≤FAR≤1.5	(1) 宅基地管控：村民户只能拥有1处宅基地，村民在宅基地之外申请新建住宅的，其原有宅基地由村委会收回，重新规划后统一安排使用。村委会制定办法收回村民宅基地的经济补偿方案。 (2) 新增（新建）宅基地管控要求：村庄新增（新建）宅基地规模应符合《福建省农村村民住宅建设管理办法》有关要求，每户宅基地面积不得超过80平方米至120平方米，不得超过三层，每户住宅建筑面积控制在300平方米以内。 (3) 建筑退距和建筑间距：①新建改建建筑间距，距离省道1.5米以上，县道10米以上，乡道5米以上，村庄干路3米以上，村庄支路1米以上。②建筑间距应满足日照间距的要求，南北向平行布置的建筑间距不小于南侧建筑高度的1.0倍，东西向平行布置的建筑间距不小于南侧建筑高度的0.8倍，东西向平行布置的道路宽度4米，设置消防通道的多层建筑山墙最小退距不小于6米。③新建建筑与市政公用设施、工业企业之间的最小退距不小于5米；除此之外东西向应预留3.5米。④沟渠、水塘等水系两侧应设置防护绿地和缓冲带，道路宽度8米以下的带状水道（沟渠等）两侧公共空间应预留不小于2米；道路宽度8米及以上的带状水道不宜小于8米，面状水面退让距离不宜小于10米，在此范围内的村民不得随意新建建筑。	实行刚性控制	
			CB-01	党群公司	用地面积：428.73m ²	保留现状党群公司。	实行刚性控制	
			CB-02	村委会	用地面积：2001.68m ² 建筑限高（H）：H≤15m	三南用地为农村宅基地，规划时对其进行更正，为村委会。	实行刚性控制	
			CB-09	幸福院	用地面积：254.51m ² 建筑限高（H）：H≤15m	保留现状幸福院。	实行刚性控制	
			公共管理与公共服务设施用地	—	—	—	—	
			商业服务业用地	—	—	—	—	
			工业用地	—	—	—	—	
			交通场站用地	—	—	—	—	
			公用设施用地	CG-01	环卫设施用地	用地面积：91.45m ²	保留现状。	实行刚性控制
			绿地与开敞空间用地	CG-02	水工程设施用地	用地面积：520.51m ²	保留现状。	实行刚性控制
增量	村庄建设用地	农村宅基地	CJ-01、CJ-02、CJ-03、CJ-04、CJ-05、CJ-06、CJ-07、CJ-08、CJ-09、CJ-10	散养用地	用地面积：1863.71m ²	保留现状。	实行刚性控制	
			ZA-01、ZA-02、ZA-03	一般住宅区	用地面积：9301.34m ² 建筑限高（H）：H≤12m 容积率（FAR）：1≤FAR≤1.5	同存量用地中一般住宅区的控制要求。	实行刚性控制	
			ZB-01	文化活动场所	用地面积：712.57m ² 建筑限高（H）：H≤15m 容积率（FAR）：1≤FAR≤1.5	新建东贵村文化活动中心。	实行刚性控制	
			ZB-02	村民广场	用地面积：2419.23m ² 建筑限高（H）：H≤15m 容积率（FAR）：1≤FAR≤1.5	新建东贵村民广场。	实行刚性控制	
			ZB-03	村民广场	用地面积：524.69m ² 建筑限高（H）：H≤12m 容积率（FAR）：1≤FAR≤1.5	新建东贵村民广场。	实行刚性控制	
			公共管理与公共服务设施用地	—	—	—	—	
			商业服务业用地	—	—	—	—	
			工业用地	—	—	—	—	
			交通场站用地	—	—	—	—	
			公用设施用地	—	—	—	—	
绿地与开敞空间用地	—	—	—	—				
基础设施用地	其他建设用地	ZH-01	留白用地	用地面积：1339.42m ²	预留留白用地，应对村庄未来发展的不确定性，留白规划用地，暂不明确规划用地性质。	—		
		ZH-02	留白用地	用地面积：1498.32m ²	—	—		
		特殊用地	—	—	—	—		
		—	—	—	—	—		

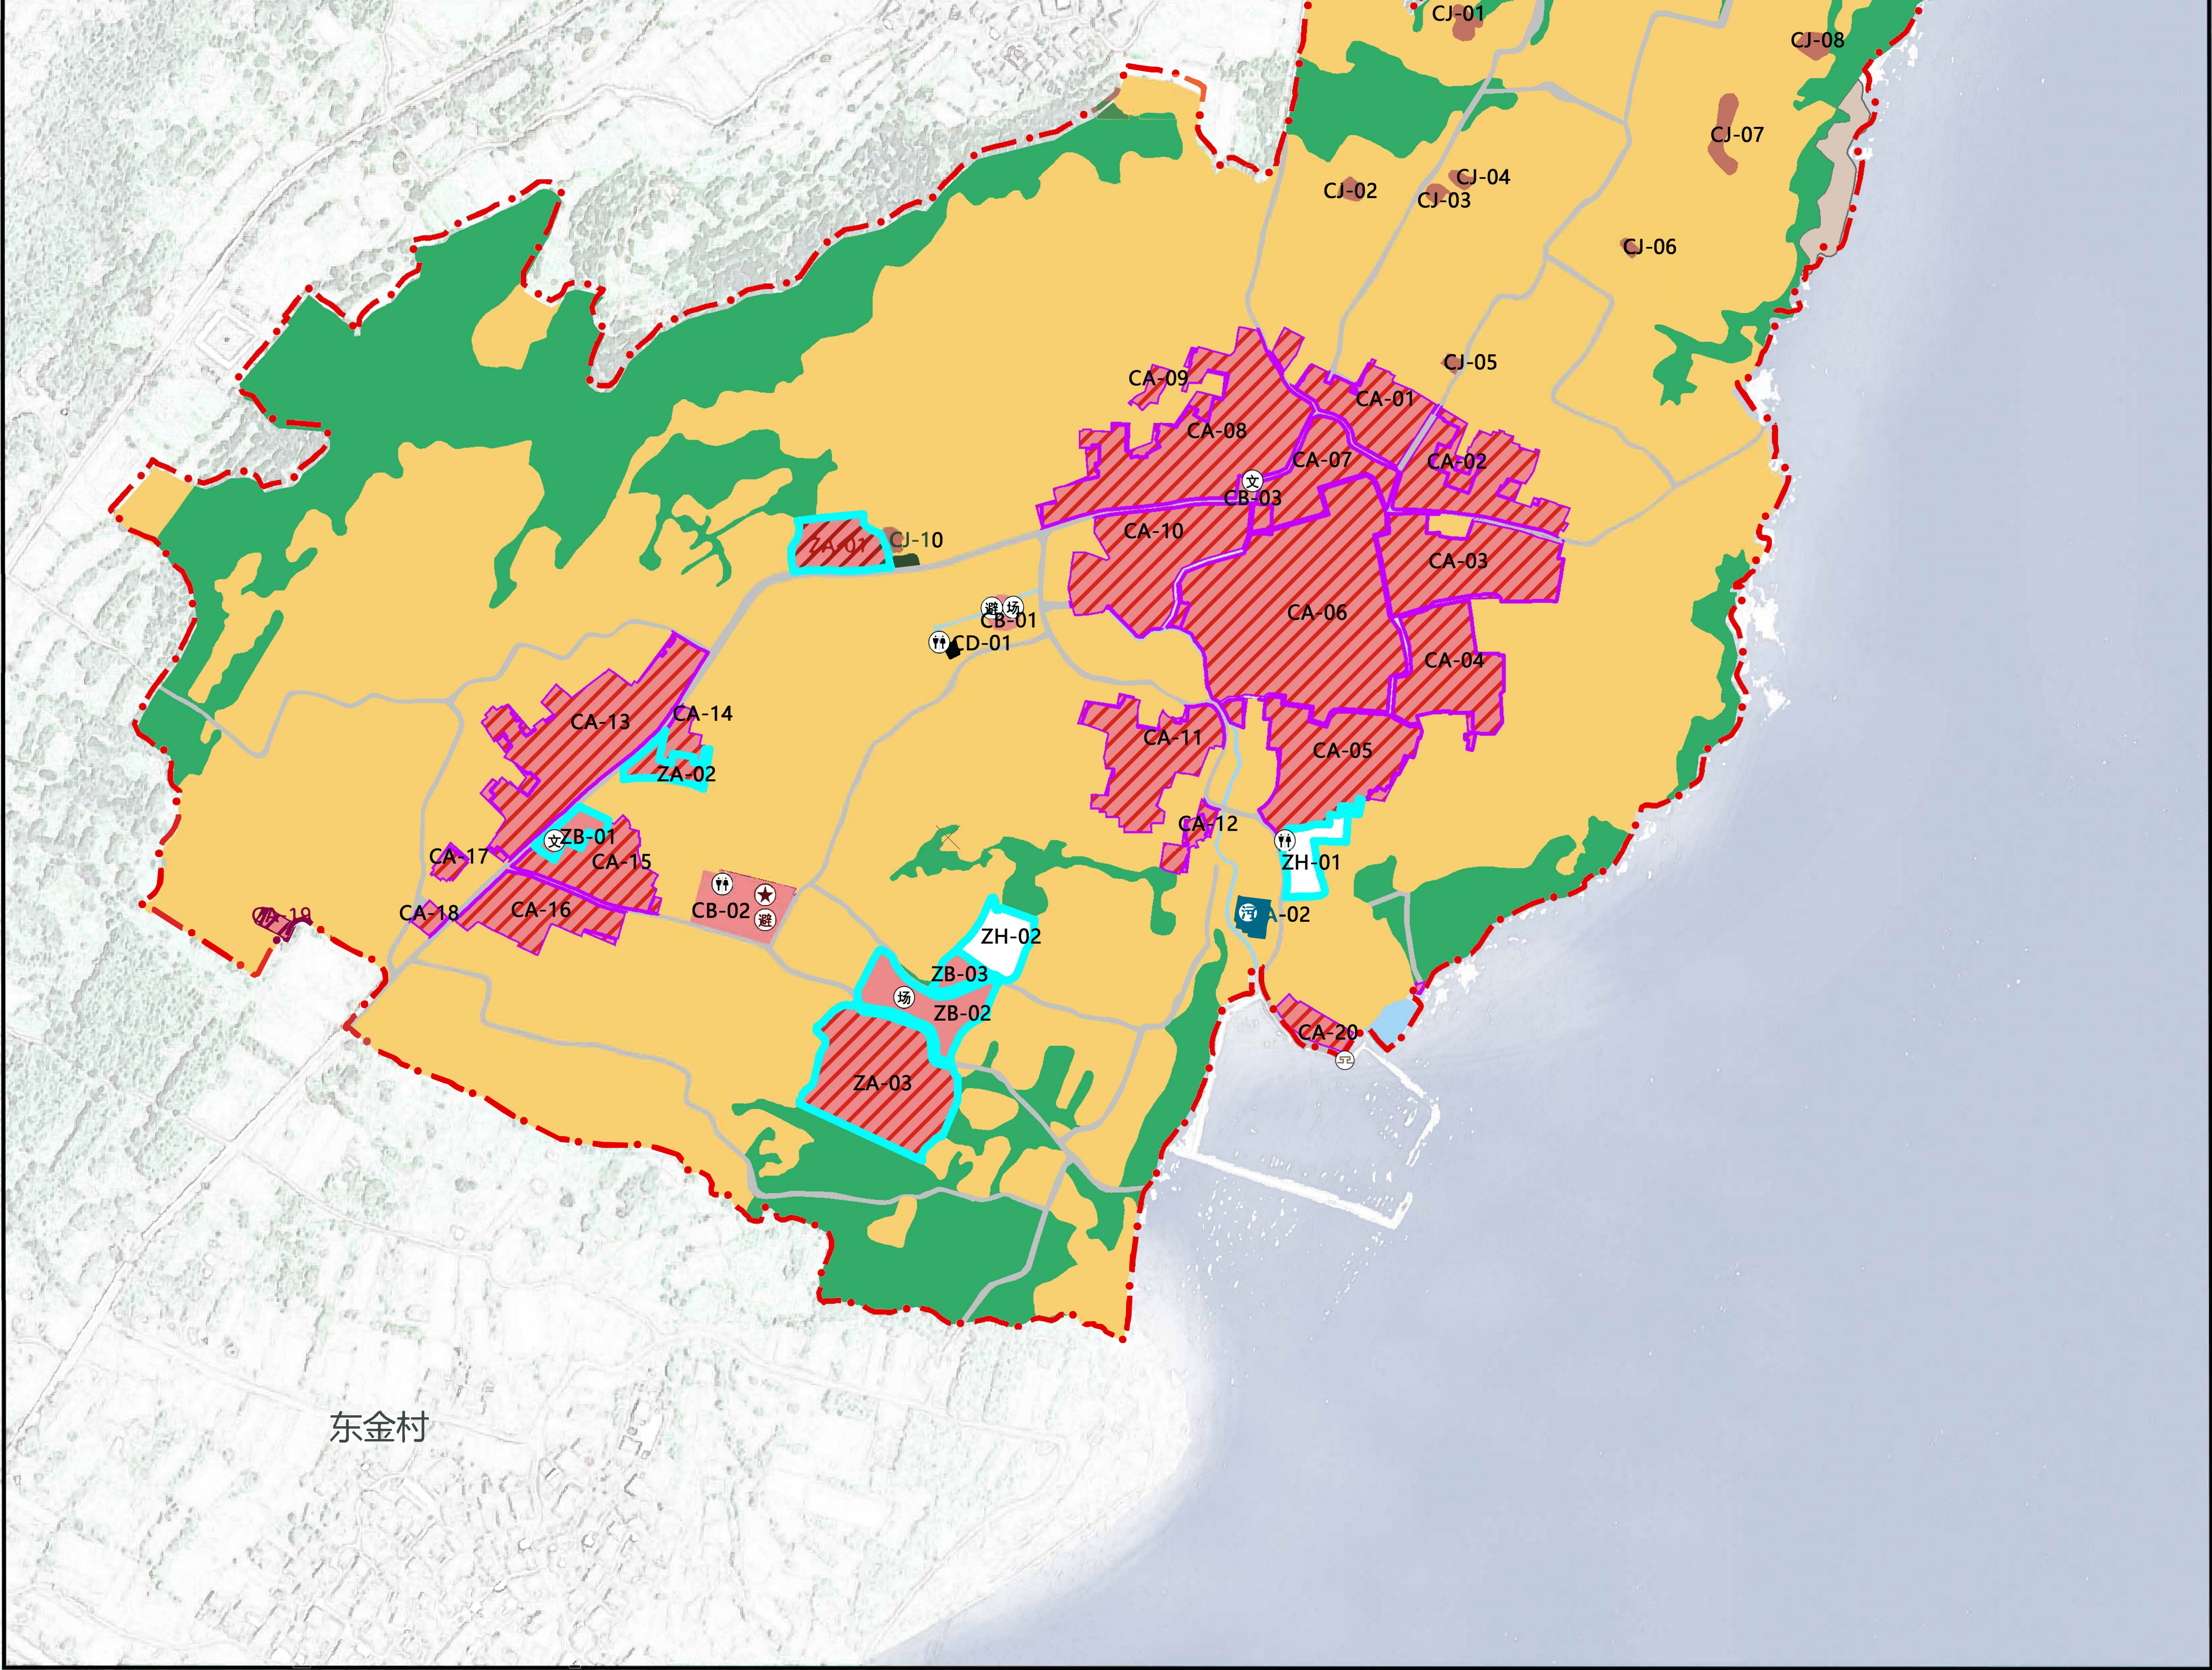

平潭综合实验区苏平片区东贵村村庄规划(2022-2035)

主要农村居民点
总平面图示意图



图例

01 教堂

02 幸福院

03 大王寺

04 公共厕所

05 党建公园

06 公共厕所

07 农村宅基地

08 文化活动中心


09 村委会

10 农村宅基地

新建建筑

保留建筑

村域红线

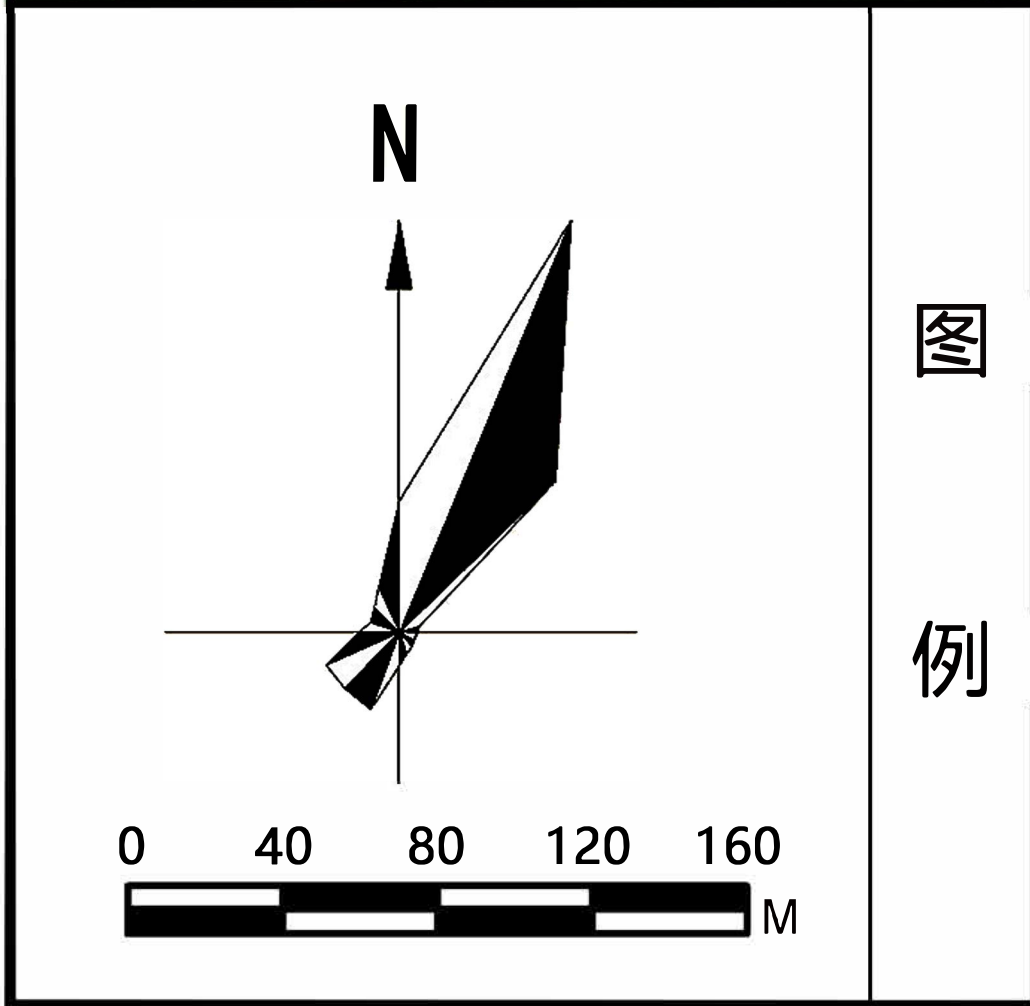

图例

近期项目表							
序号	项目类型	项目名称	项目规模		建设年限	投资额 (万元)	建议资金来源
			内容	数量			
1	基础设施建设	村部前广场硬化	村部前广场硬化, 设施篮球场与健身器材区域	1处	2022-2025	30	村庄自筹+上级核拨
2		公共厕所	选址建设一处公共厕所	1处	2022-2025	15	上级核拨
3		路灯	下东贵沿路路灯	沿路	2022-2025	5	上级核拨
4	公共设施建设	幸福院建设	对幸福院进行整修	1处	2022-2025	100	村庄自筹+上级核拨