



平潭综合实验区苏平片区**招康村**村庄规划（公示材料）

（2022-2035年）

■ 保护开发特色村庄

厦门市城市规划设计研究院有限公司

2022.11

平潭综合实验区苏平片区白青乡招康村村庄规划（2022-2035）

村域综合现状图

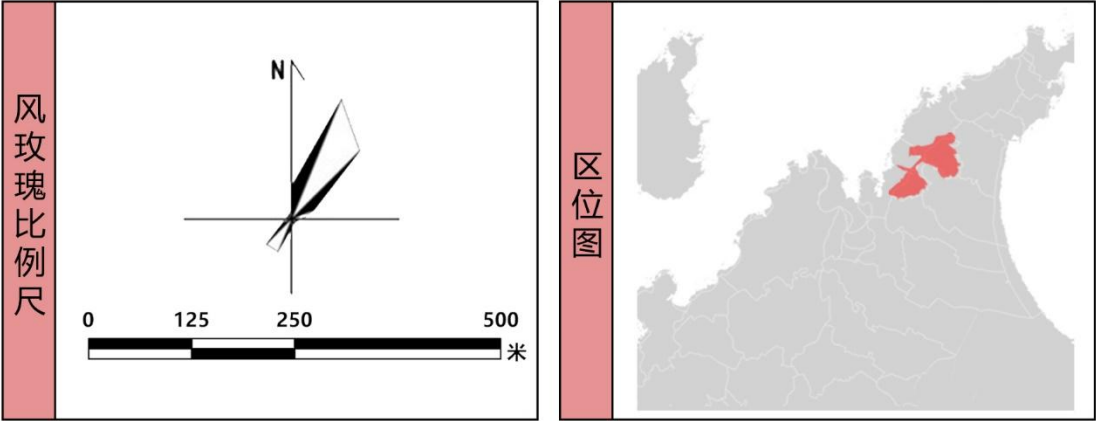
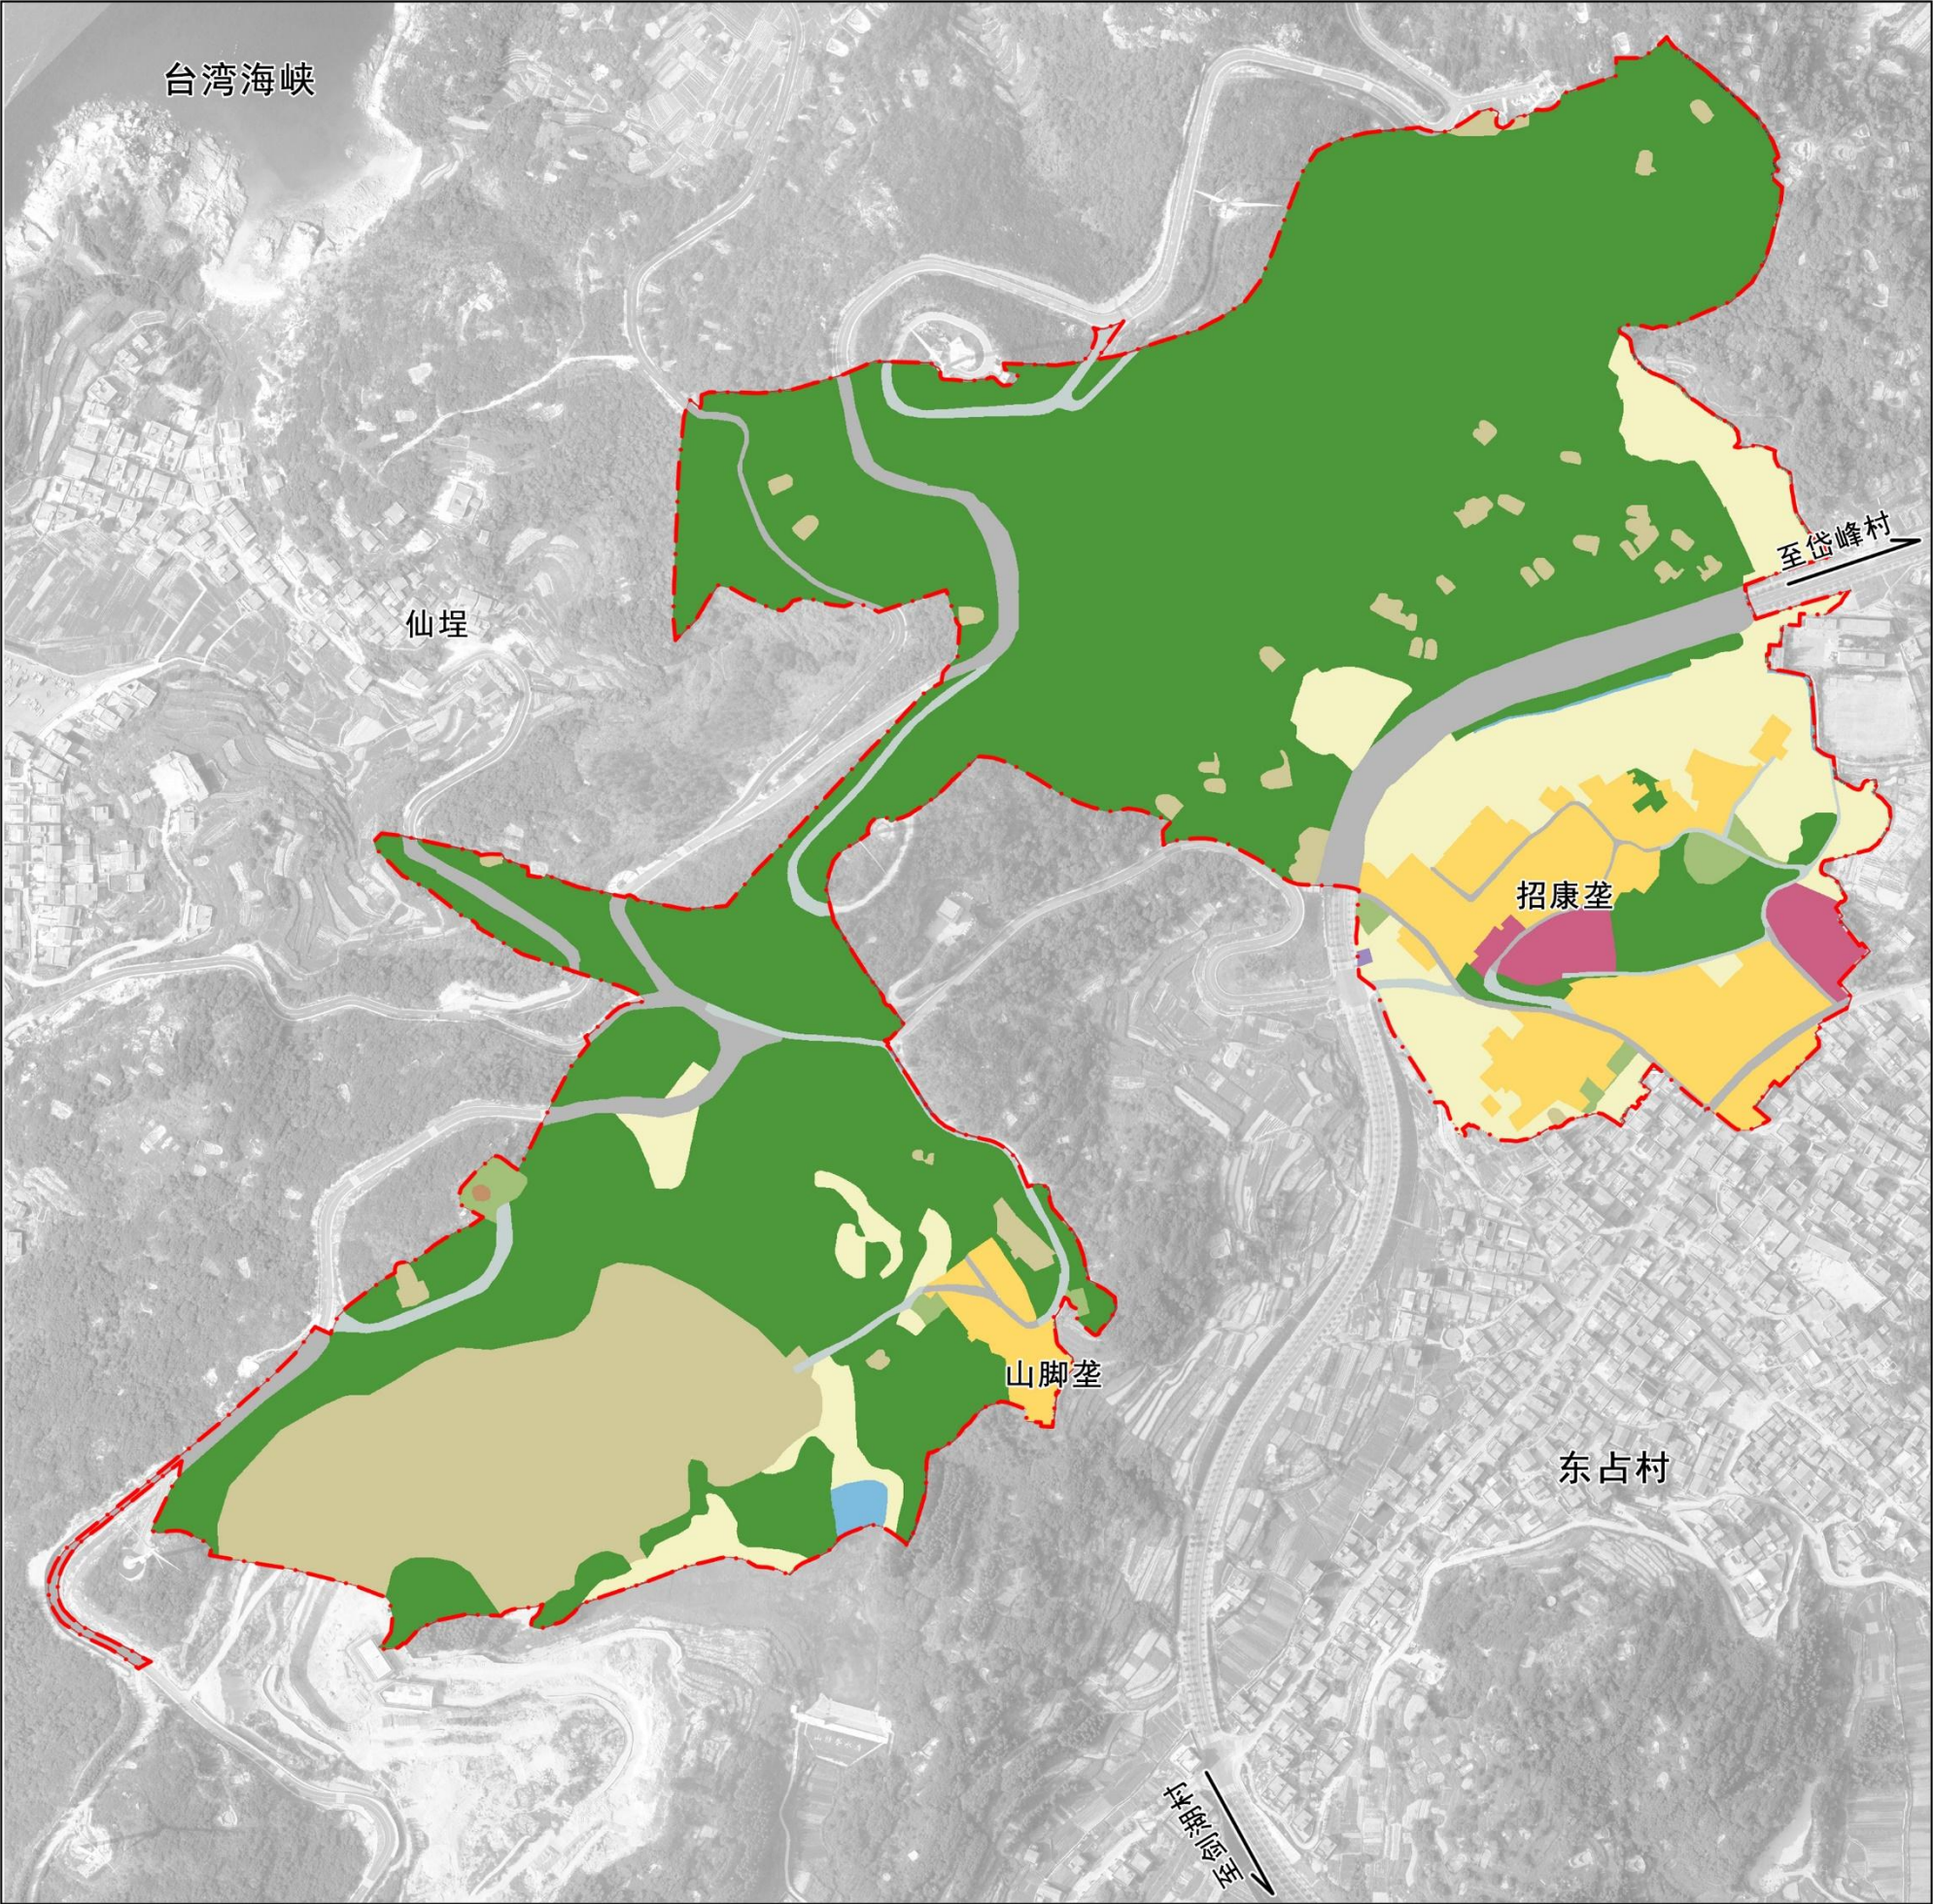


图 例					
	乡村道路用地		其他特殊用地		水库水面
	公共管理与公共服务用地		殡葬用地		沟渠
	公用设施用地		居住用地		耕地
	公路用地		工业用地		草地
	城镇道路用地				林地

现状国土空间功能结构表			
用地类型		规划基期年	
		面积(ha)	比重(%)
耕地 (01)		7.02	10.72%
林地 (03)		40.10	61.23%
草地 (04)		0.49	0.75%
村域建设用地	城镇用地 (07-09, 1001, 11, 1207-1209, 1301-1310, 1313, 14,16, 2301)	0.28	0.43%
	居住用地 (0703-0704)	4.63	7.07%
	公共管理与公共服务设施用地 (08)	0.82	1.25%
	工业用地 (1001)	0.02	0.02%
	村庄内部道路用地 (060102)	1.15	1.76%
	公用设施用地 (1301-1310, 1313)	0.01	0.02%
	小计	6.63	10.12%
	小计	6.91	10.55%
	区域基础设施用地 (1201-1206, 1311, 1312)	2.96	4.52%
	其他建设用地 (15, 1002, 1003)	7.81	11.93%
小计		17.68	27.00%
陆地水域 (17)		0.20	0.30%
总计		65.48	100.00%

平潭综合实验区苏平片区白青乡 **招康村** 村庄规划（2022-2035）

村域综合规划图

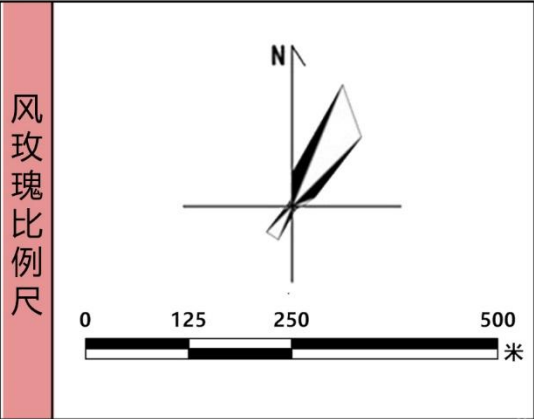
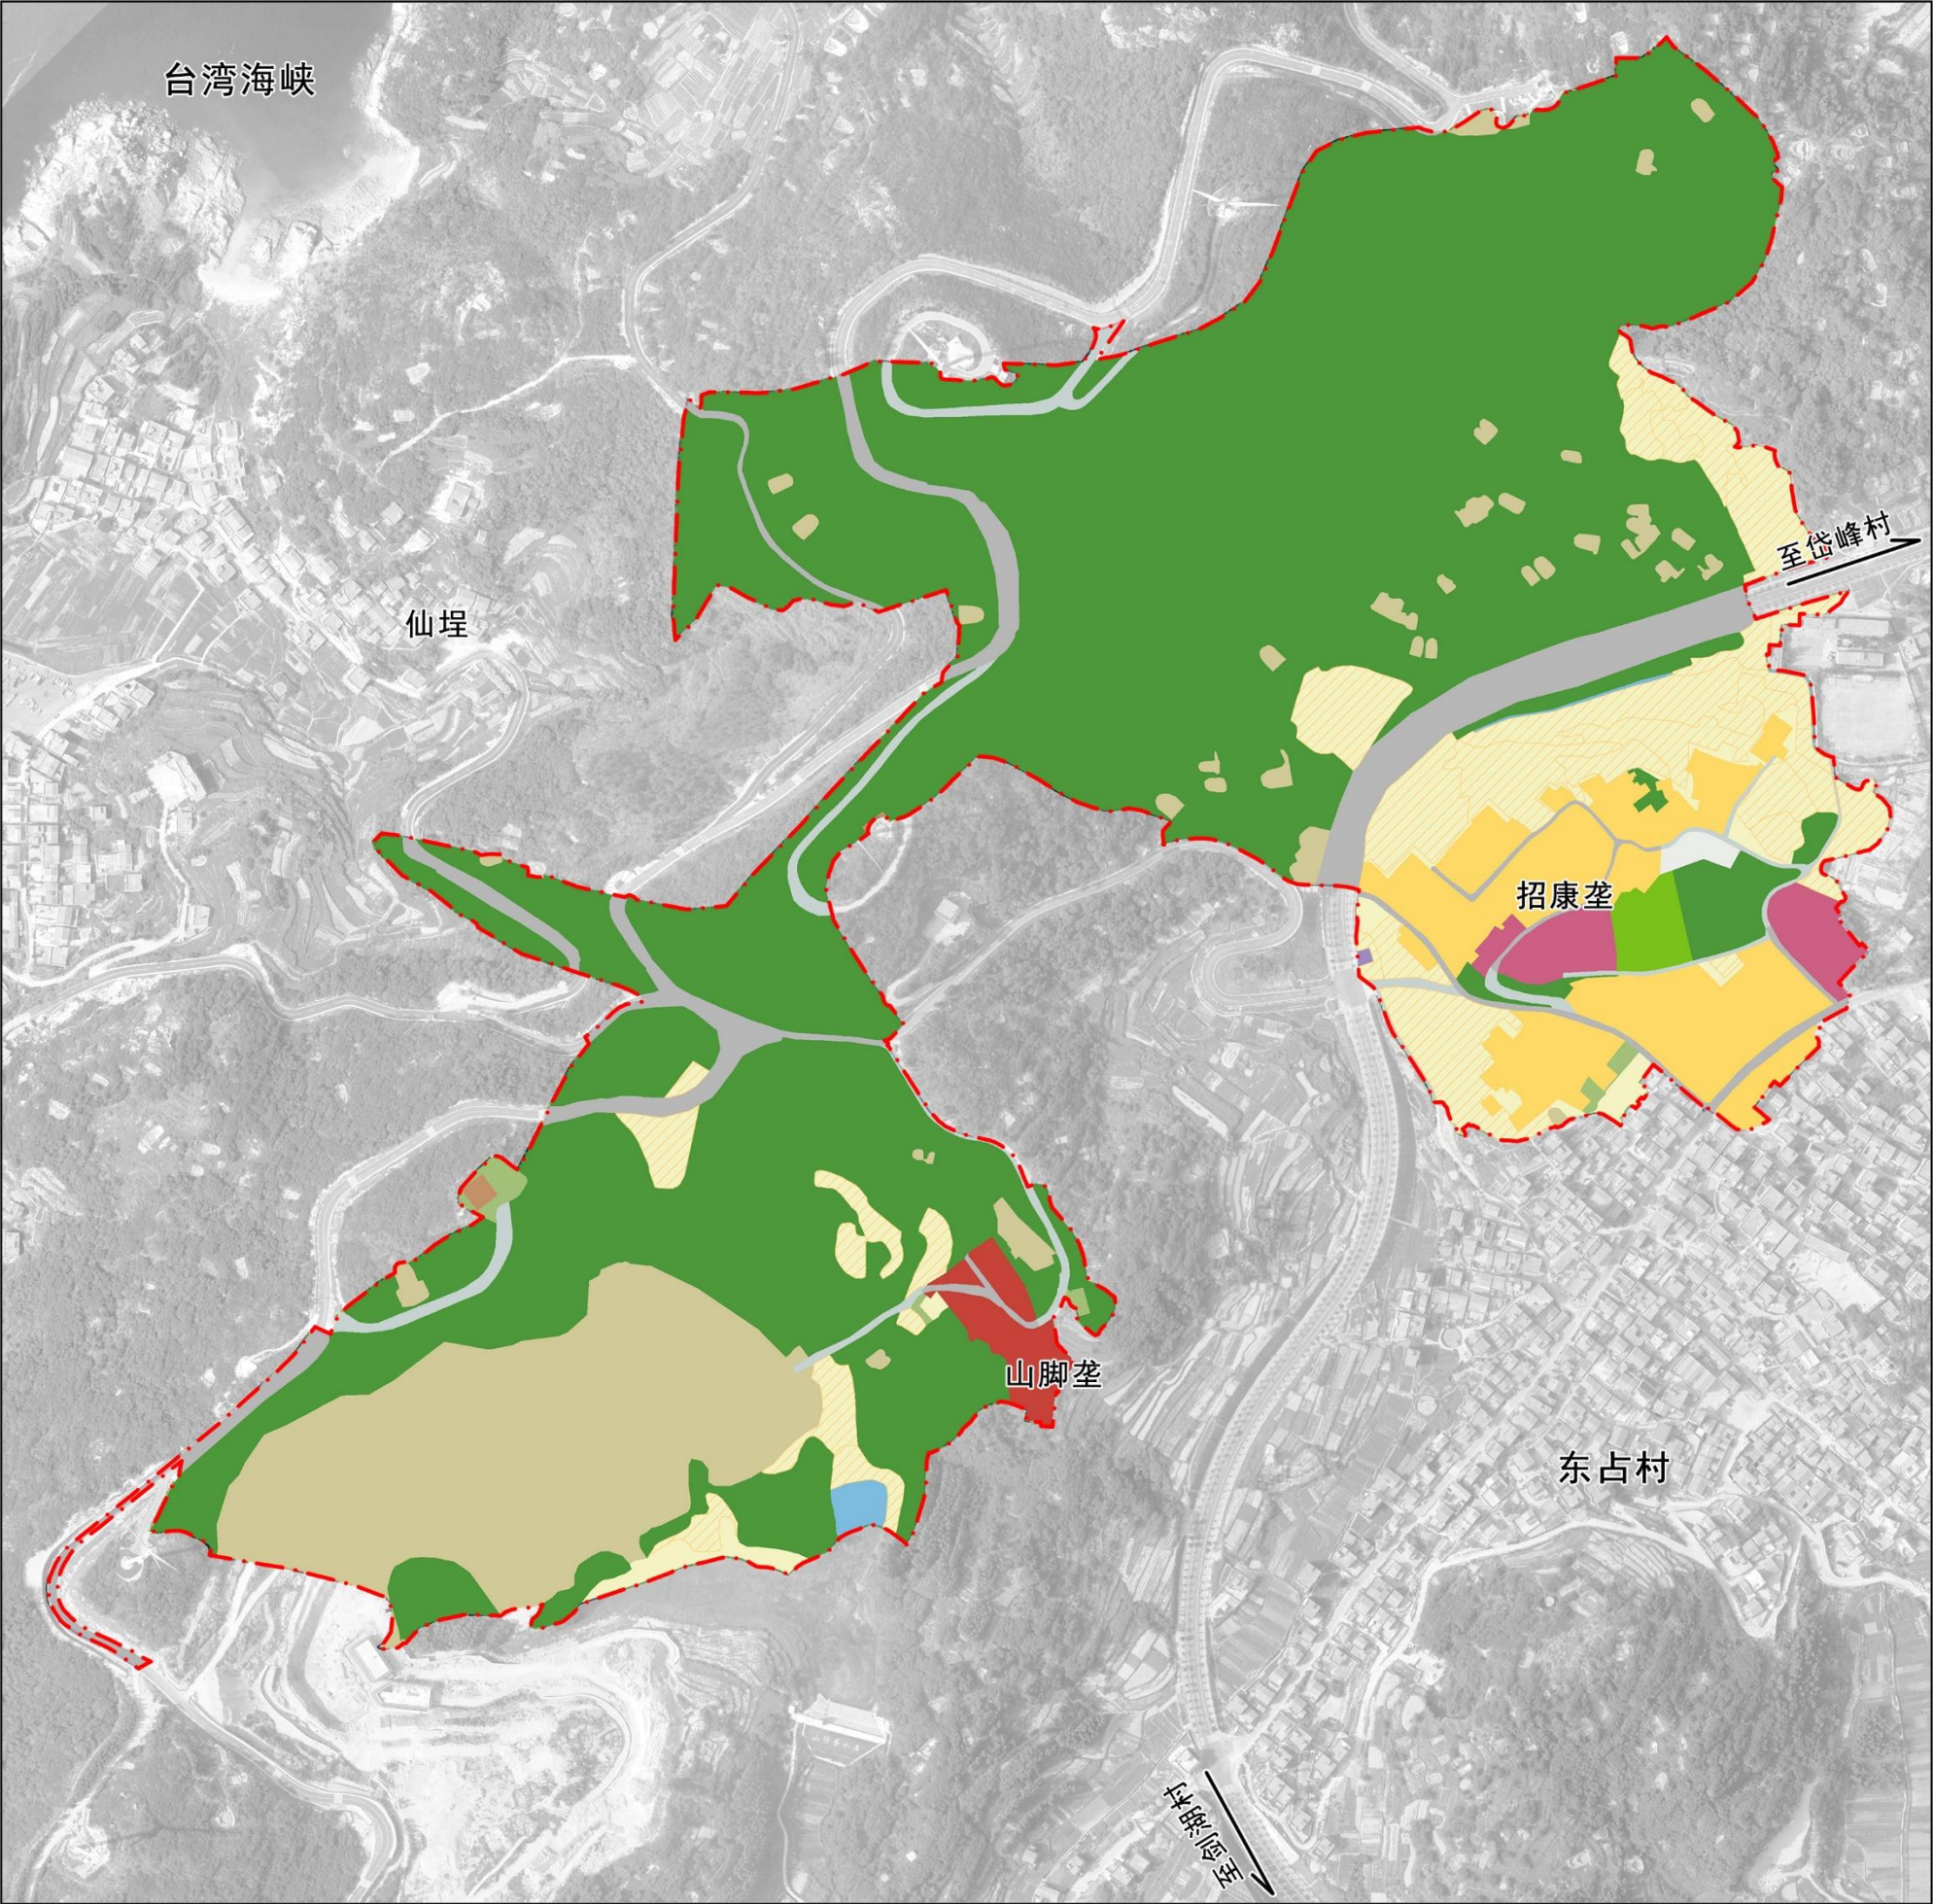


图 例			
乡村道路用地	居住用地	特殊用地	林地
公共管理与公共服务用地	工业用地	留白用地	弹性发展区
公用设施用地	商业服务业用地	绿地及开敞空间用地	永久基本农田
公路用地	水库水面	耕地	
城镇道路用地	沟渠	草地	

平潭综合实验区苏平片区白青乡 **招康村** 村庄规划（2022-2035）


规划一表

用地类型			规划基期年		规划目标年		
			面积(ha)	比重(%)	面积(ha)	比重(%)	
耕地 (01)			7.02	10.72%	7.14	10.90%	
园地 (02)			0	0.00%	0	0.00%	
林地 (03)			40.1	61.23%	39.69	60.61%	
草地 (04)			0.49	0.75%	0.22	0.33%	
湿地 (05)			0	0.00%	0	0.00%	
农业设施建设用地 (06)			0	0.00%	0	0.00%	
村域建设用地	村域城乡建设用地	城镇用地 (07-09, 1001, 11, 1207-1209, 1301-1310, 1313, 14,16, 2301)	5.76	8.80%	6.25	9.54%	
		村庄建设用地	居住用地 (0703-0704)	4.63	7.07%	4.02	6.14%
			公共管理与公共服务设施用地 (08)	0.82	1.25%	0.82	1.25%
			商业服务业用地 (09)	0	0.00%	0.61	0.93%
			工业用地 (1001)	0.02	0.02%	0.05	0.07%
			仓储用地 (11)	0	0.00%	0	0.00%
			村庄内部道路用地 (060102)	1.15	1.76%	0	0.00%
			交通场站用地 (1208)	0	0.00%	0	0.00%
			其他交通设施用地 (1209)	0	0.00%	0	0.00%
			公用设施用地 (1301-1310, 1313)	0.01	0.02%	0.01	0.02%
			绿地与开敞空间用地 (14)	0	0.00%	0.34	0.52%
		留白用地 (16)	0	0.00%	0.12	0.18%	
		空闲地 (2301)	0	0.00%	0	0.00%	
		小计	6.63	10.12%	5.97	9.12%	
	小计		12.39	18.92%	12.22	18.66%	
	区域基础设施用地 (1201-1206, 1311, 1312)		2.96	4.52%	3.03	4.63%	
	其他建设用地 (15, 1002, 1003)		7.81	11.93%	7.9	12.06%	
	小计		23.16	35.37%	23.15	35.35%	
	陆地水域 (17)			0.2	0.30%	0.2	0.30%
	渔业用地 (18)			0	0.00%	0	0.00%
工矿通信用海 (19)			0	0.00%	0	0.00%	
交通运输用海 (20)			0	0.00%	0	0.00%	
游憩用海 (21)			0	0.00%	0	0.00%	
特殊用海 (22)			0	0.00%	0	0.00%	
其他土地 (23)			0	0.00%	0	0.00%	
其他海域 (24)			0	0.00%	0	0.00%	
总计			65.48	100.00%	65.48	100.00%	

序号	指标	属性	单位	现状基期年	规划目标年
一、村庄发展性指标					
1	村庄建设用地总面积	约束性	公顷	6.63	5.97
2	村域城乡建设用地面积	约束性	公顷	12.39	12.22
3	村庄建设用地规模	预期性	公顷	23.16	23.15
4	公共管理与公共服务用地规模	预期性	公顷	0.82	0.82
5	公用设施用地规模	预期性	公顷	0.01	0.01
6	人均村庄建设用地面积	预期性	平方米/人	73.59	66.70
二、村庄保护性指标					
7	生态保护红线面积	约束性	公顷	0.00	0.00
8	永久基本农田保护面积	约束性	公顷	6.36	6.36
9	耕地保有量	约束性	公顷	0.66	0.83
10	林地保有量	约束性	公顷	40.1	39.69
11	湿地面积	约束性	公顷	0.00	0.00
12	大陆自然海岸线保有率	约束性	%	0.00	0.00
13	自然和文化遗产	预期性	处	21.87	21.87

平潭综合实验区苏平片区白青乡招康村村庄规划（2022-2035）

村庄居民点图则

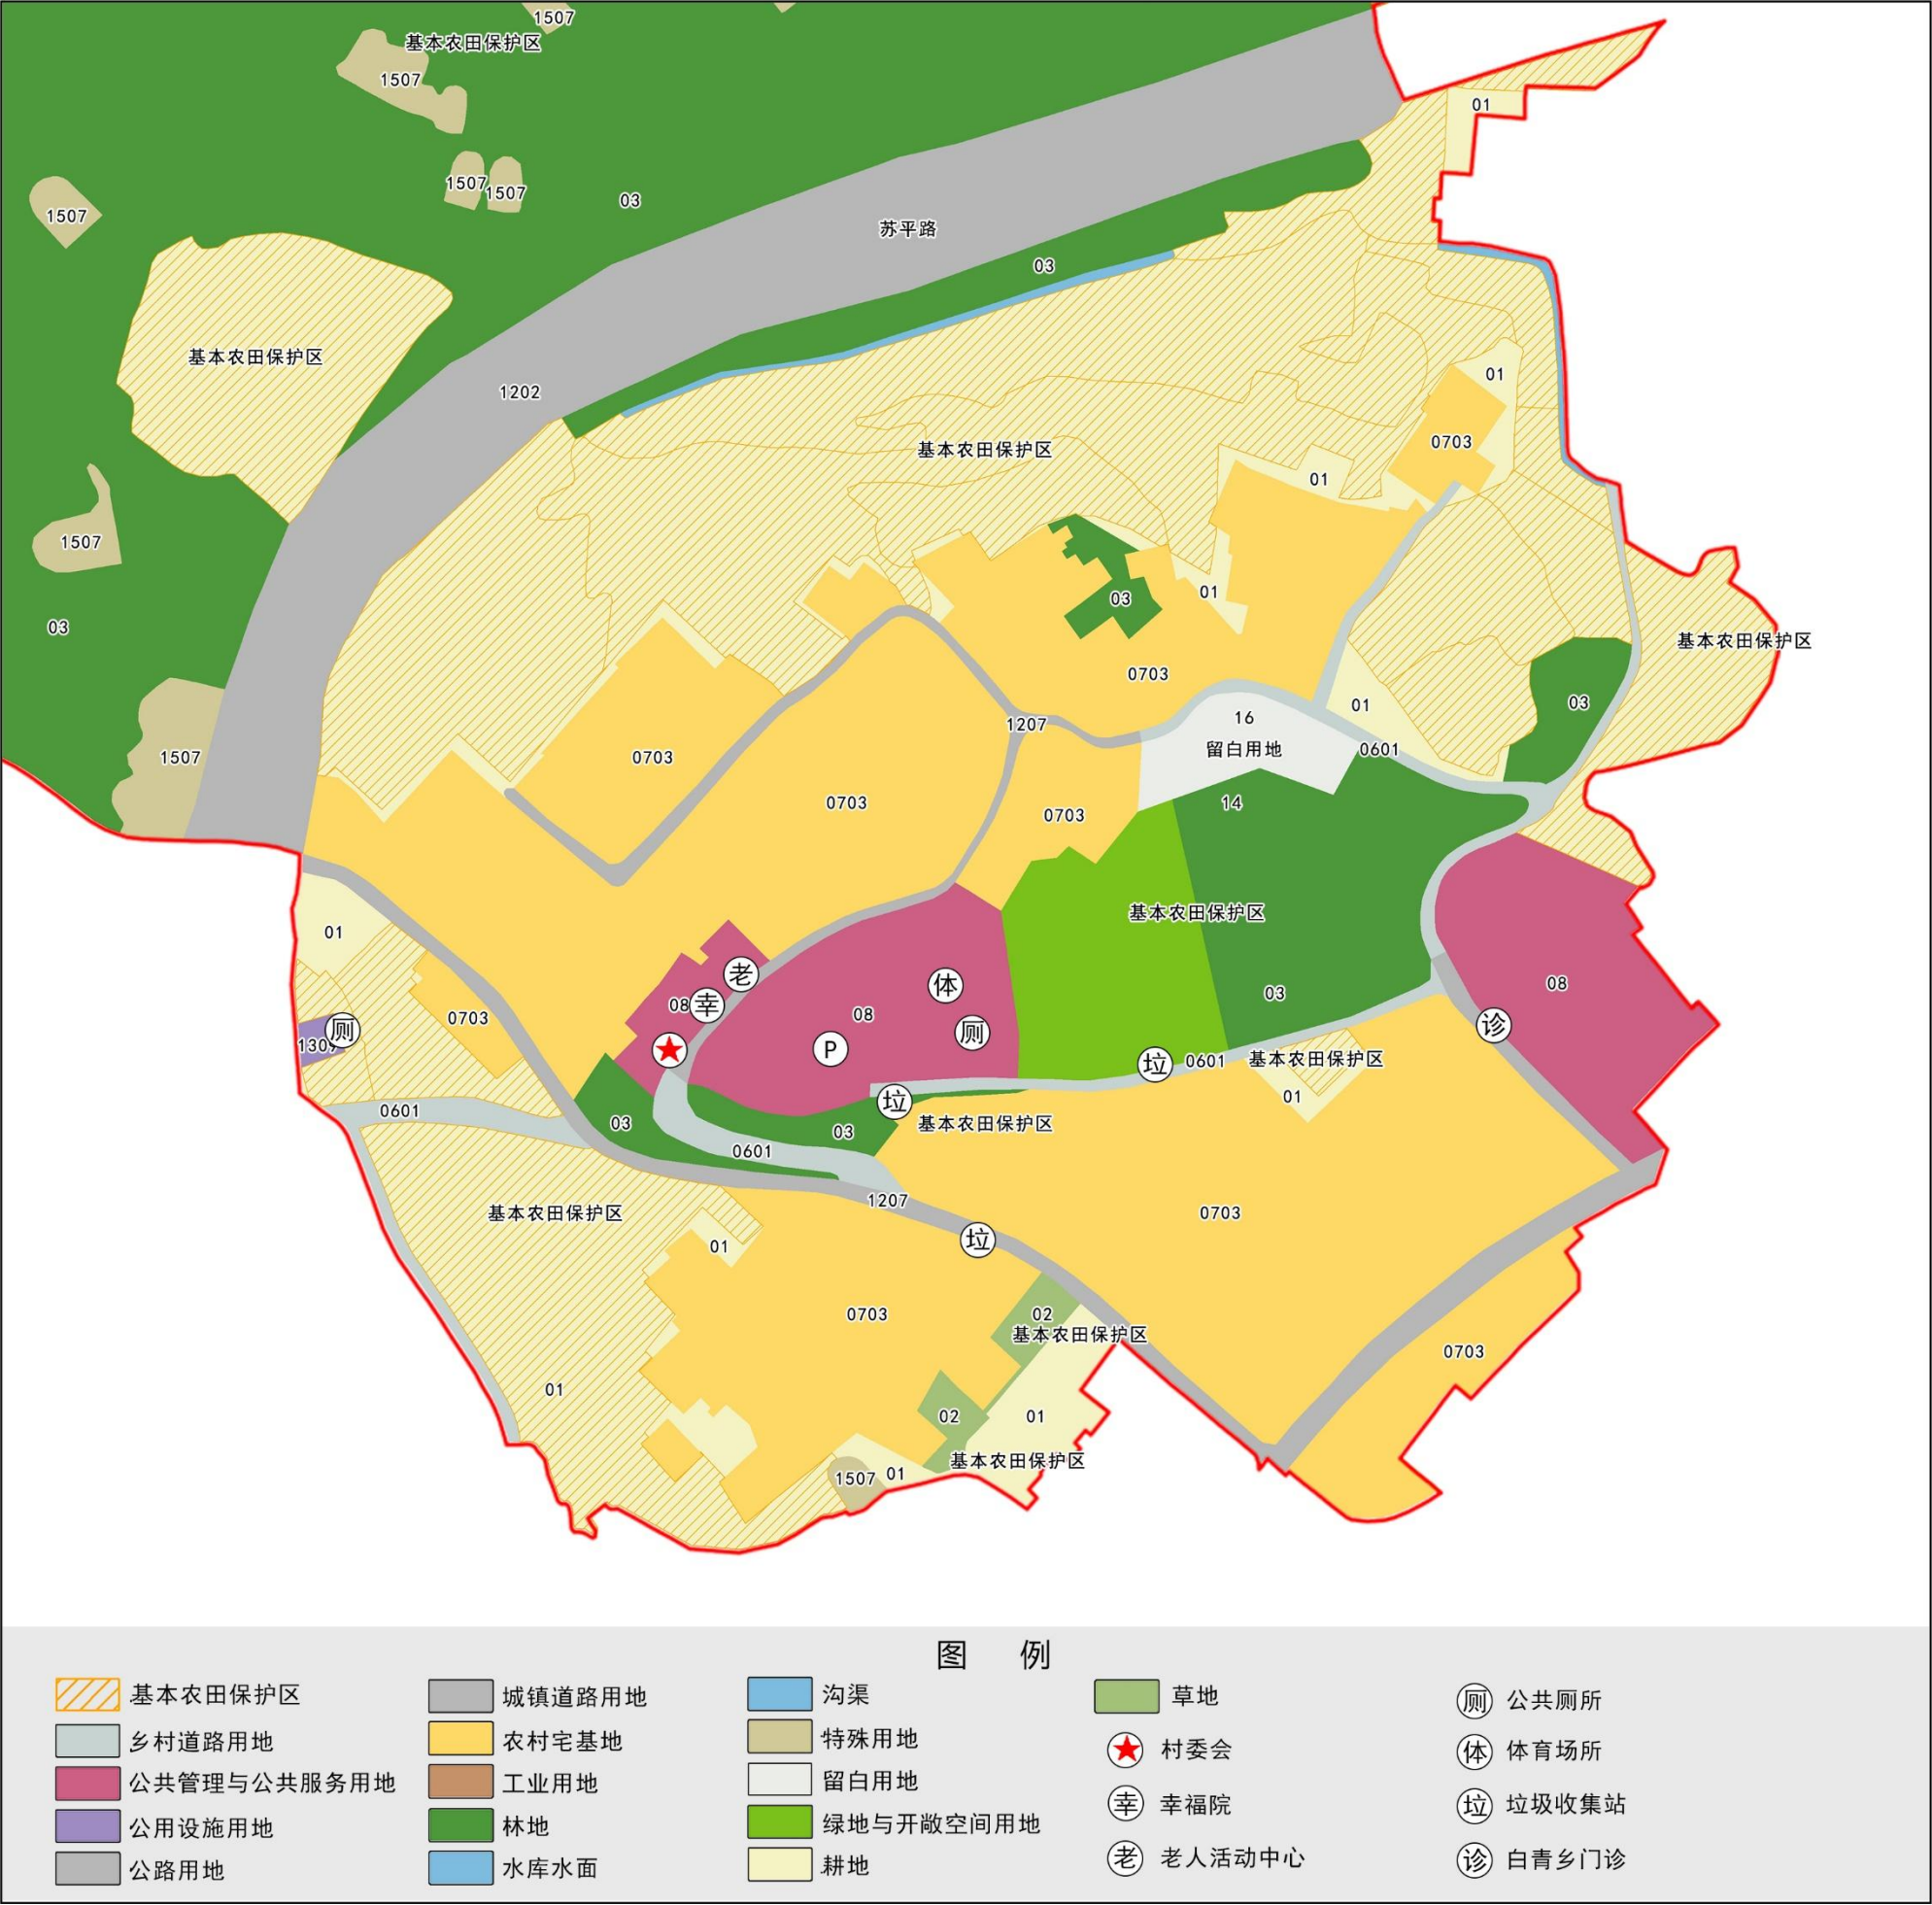

风玫瑰比例尺

区位图

管 控 规 则

1. 村庄建设活动应在村庄建设边界内进行，不得占用生态保护红线，永久基本农田，尽量少占耕地，不占耕地。


2. 规划期间内限制单独户分散居民点的发展，原则上不再新增宅基地，若有刚性宅基地建设需求，应充分利用原来的宅基地进行翻建，严格落实一户一宅和每户120㎡宅基地基底面积的标准；村民建房建筑层数不超过3层，建筑高度不高于12m；

3. 农村社区服务设施用地为村集体所有，禁止改变土地用途及非法出让，禁止出租从事非公益性活动；绿地与开敞空间用地为村集体所有，禁止改变土地用途，禁止在绿地与开敞空间用地进行宅基地建设；不得占用村庄内部道路用地建房；鼓励利用现有建设地进行挖潜，转化为商业类、仓储类经营性建设用地，用于促进村庄特色农业发展。

4. 对暂时难以明确具体用途的建设用地，规划予以“留白”。“留白”用地宜以村庄基础设施、社会公益、农村新产业新业态发展产业项目为主。

平潭综合实验区苏平片区白青乡招康村村庄规划（2022-2035）

规划总平面图

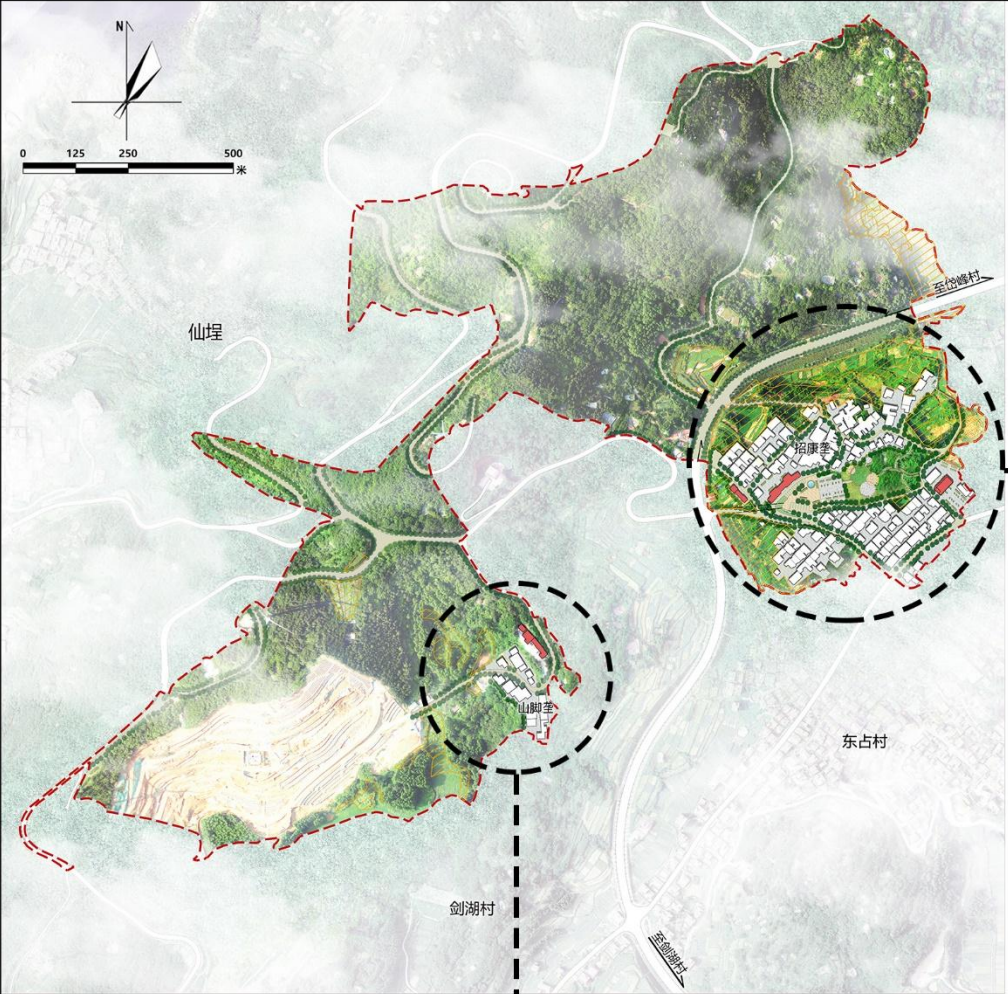

- 图例
- 1. 游客服务中心
 - 2. 村委会
 - 3. 幸福院
 - 4. 老年活动中心、文化站
 - 5. 室外活动场地
 - 6. 旅游集散停车场
 - 7. 休闲广场
 - 8. 生态公园
 - 9. 村卫生所
 - 10. 公墓管理用房
 - 11. 公墓配套服务区
 - 12. 下穿涵洞
 - 13. 村邮站

