



平潭综合实验区苏平镇半山村庄规划(2022-2035)


村域综合现状图

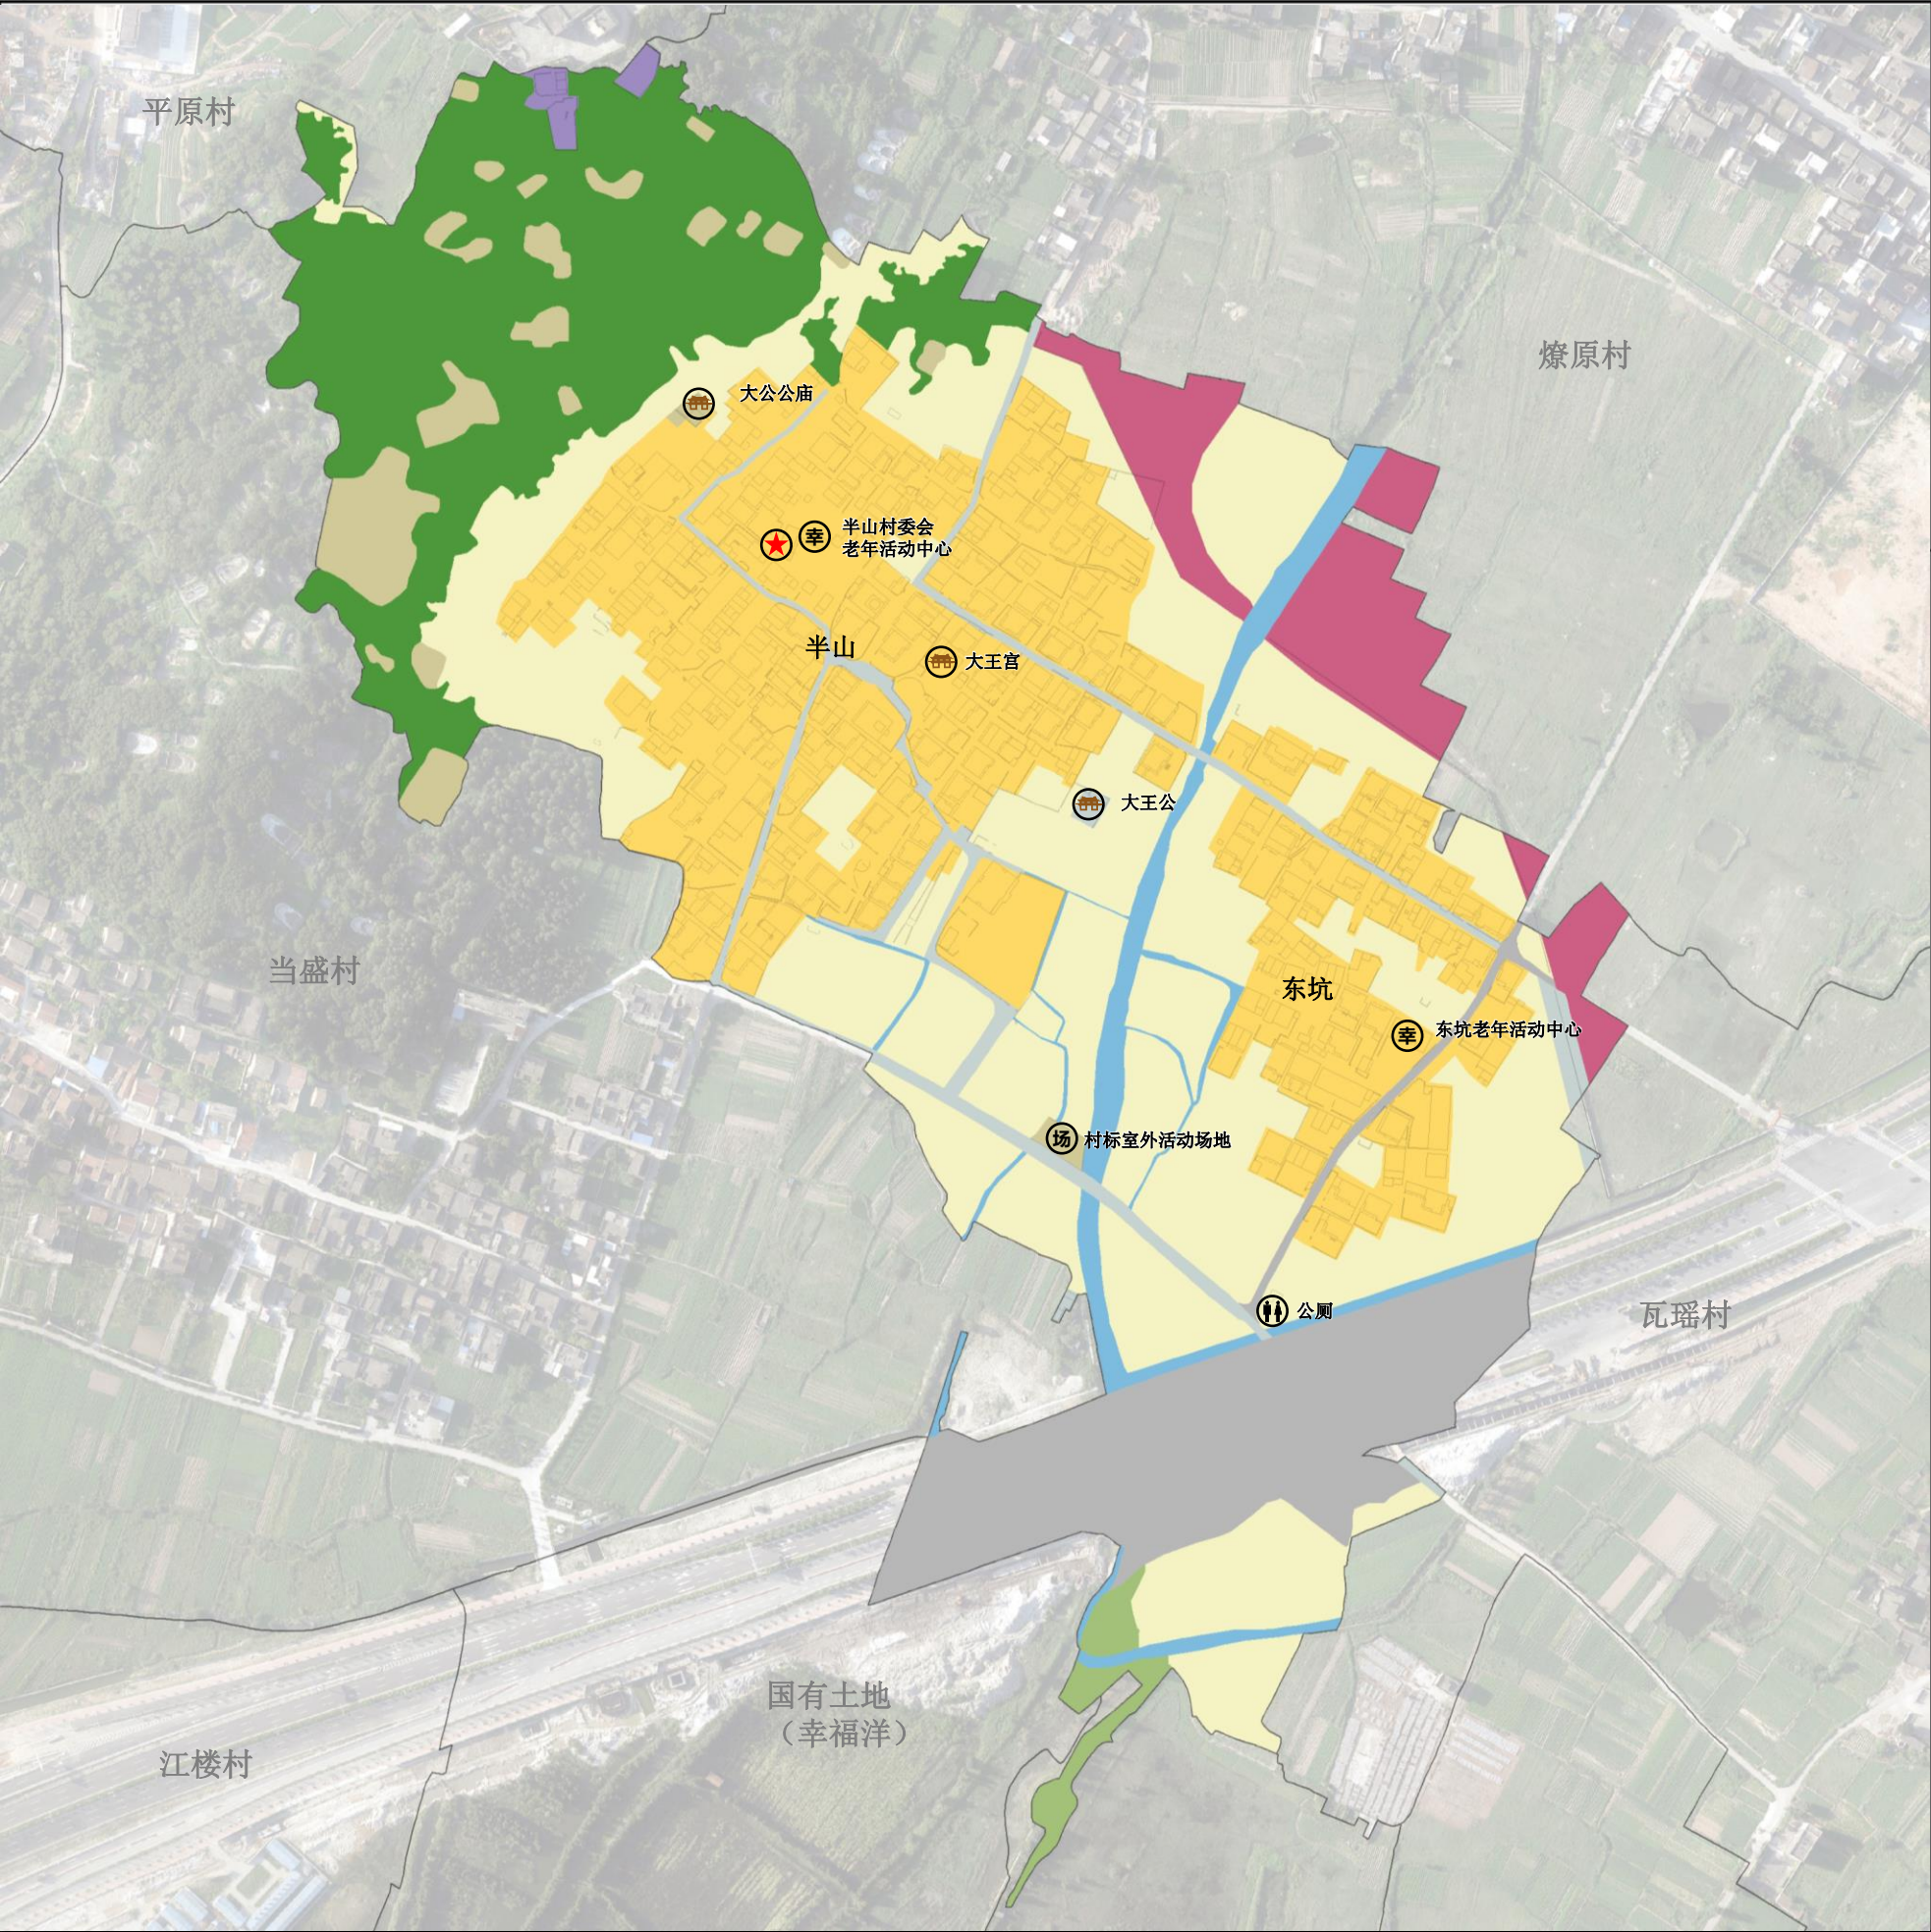

风玫瑰与比例尺

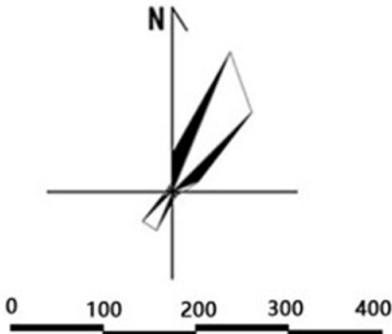

位置图

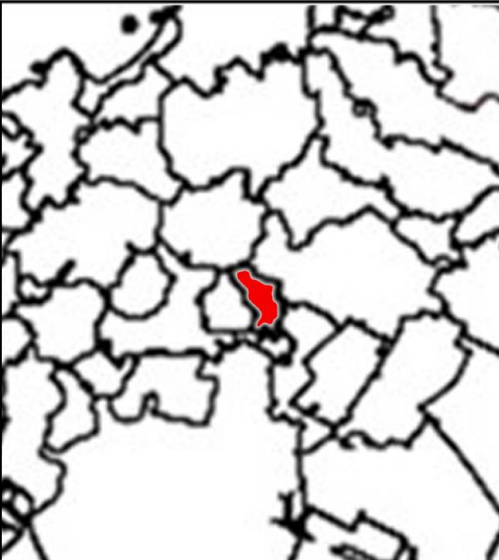

图例

- 村界

耕地

林地

草地
- 陆地水域

种植设施建设用地

农村宅基地

公共管理与公共服务用地
- 村庄内部道路用地

公用设施用地

公路用地


特殊用地

国土空间功能结构调整表


用地类型				面积	比重
耕地（01）				9.91	31.38
园地（02）				0.00	0.00
林地（03）				4.85	15.34
草地（04）				0.30	0.94
湿地（05）				0.00	0.00
农业设施建设用地（06）				0.47	1.50
村域建设 用地	村域城乡 建设用地	城镇用地		0.00	0.00
		村庄建设 用地	居住用地	9.20	29.11
			公共管理与公共服务用地	1.56	4.95
			村庄内部道路用地	0.43	1.37
			公用设施用地	0.11	0.36
			小计	11.30	35.78
		小计		11.30	35.78
		区域基础设施用地		2.87	9.07
	其他建设用地		0.93	2.96	
	小计		15.10	47.81	
陆地水域（17）				0.95	3.02
其他土地（23）				0.00	0.00
总计				31.59	100.00

平潭综合实验区苏平镇半山村村庄规划(2022-2035)


国土空间管控边界图

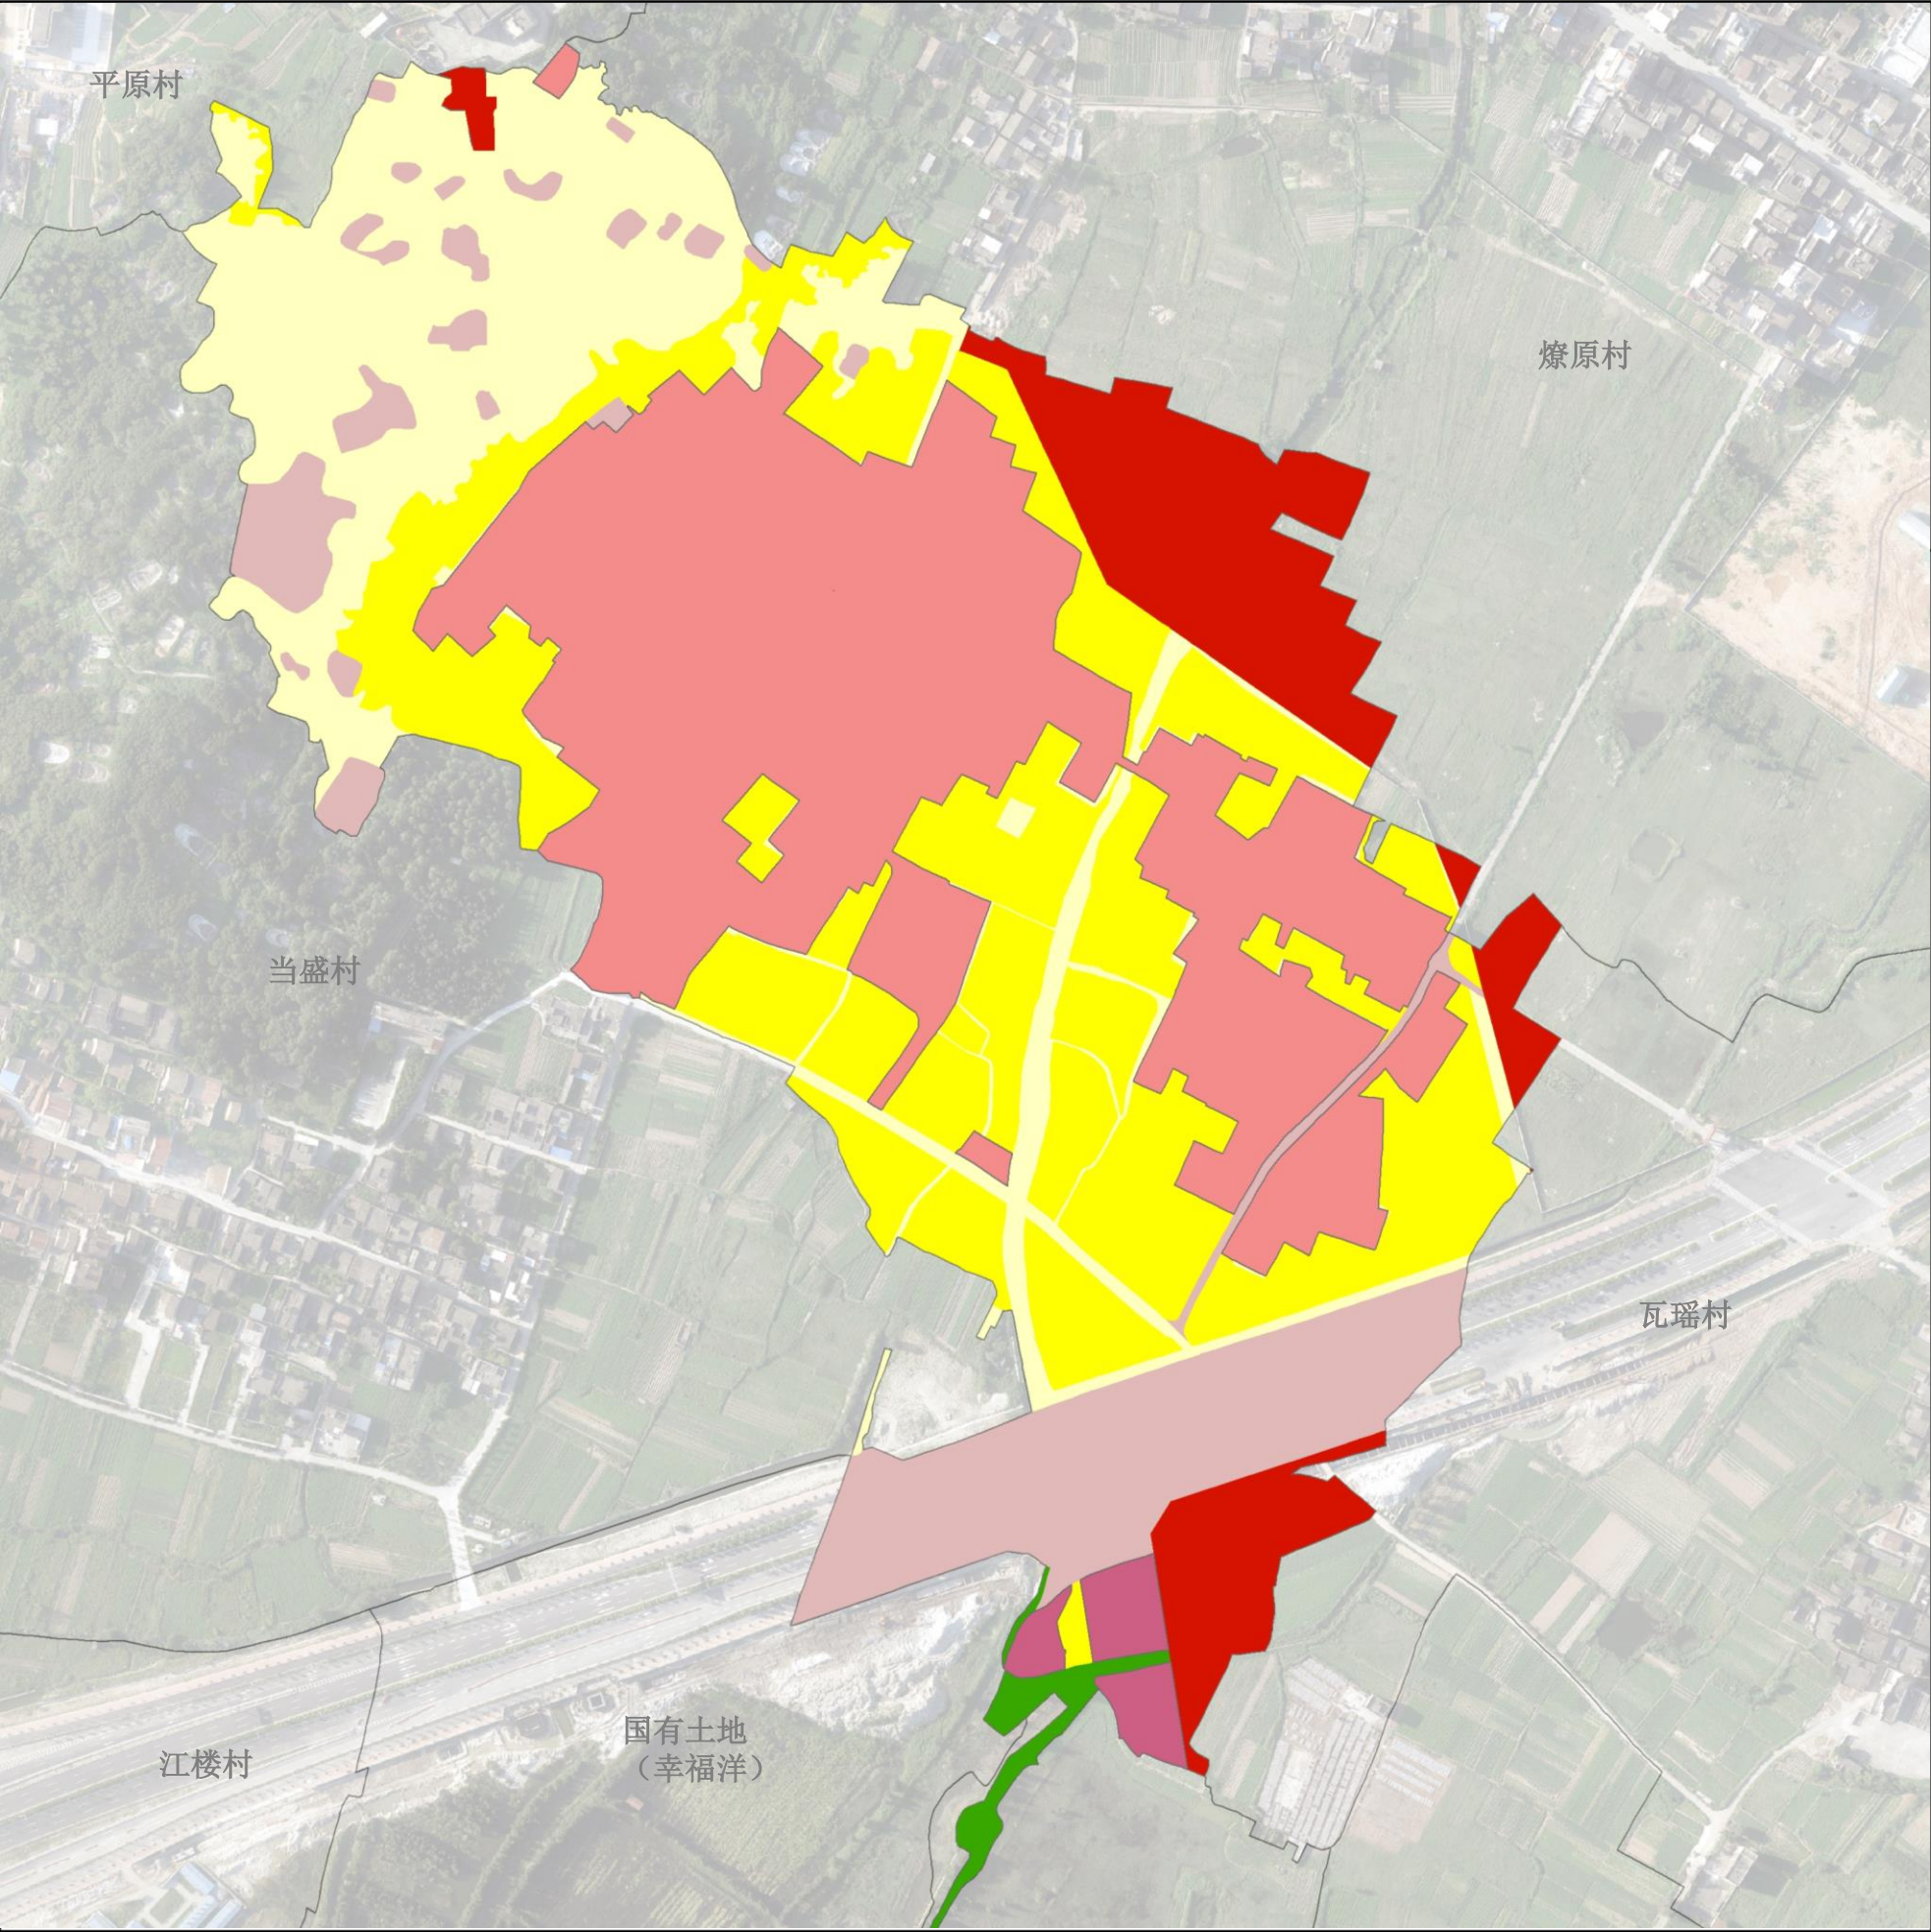

风玫瑰与比例尺

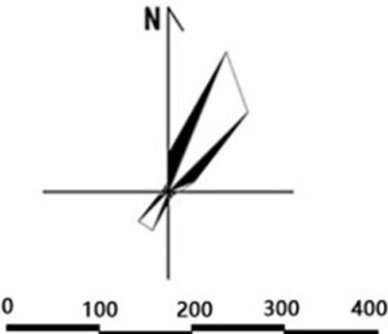

位置图

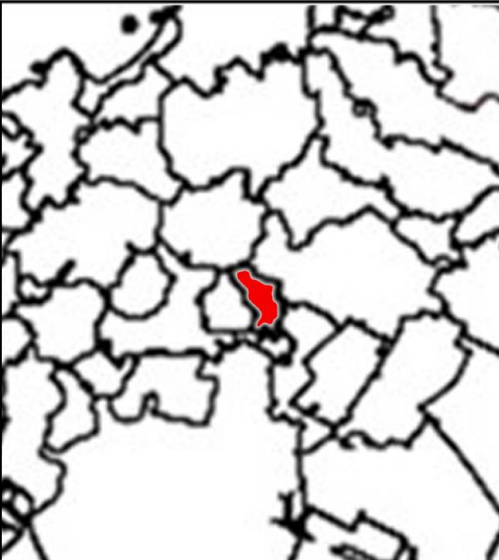

图例

- 一般生态空间
-
- 永久基本农田

村域管控指标一览表

序号		空间类型	面积（公顷）	占村域比例（%）
1	其中	农业空间	14.23	45.05
		永久基本农田	8.24	26.08
		一般农业空间	6.00	18.98
2	其中	生态空间	0.28	0.90
		生态保护红线	0.00	0.00
		一般生态空间	0.28	0.90
3	其中	建设空间	17.07	54.05
		城镇空间	3.12	9.86
		村庄集中建设区	10.04	31.79
		弹性发展区	0.44	1.40
		其他	3.47	10.99


规划指标一览表

序号	指标	属性	单位	现状基期年	规划目标年
一、村庄发展性指标					
1	村域建设用地总面积	约束性	公顷	15.10	16.63+0.53
2	村域城乡建设用地面积	预期性	公顷	11.30	13.14+0.53
3	村庄建设用地规模	预期性	公顷	11.30	10.02+0.53
4	公共管理与公共服务用地规模	预期性	公顷	1.56	0.11
5	公用设施用地规模	预期性	公顷	0.11	0.04
6	人均村庄建设用地面积	预期性	平方米/人	103.48	95.02
二、村庄保护性指标					
7	永久基本农田保护面积	约束性	公顷	8.24	8.24
8	耕地保有量	约束性	公顷	9.91	8.72
9	林地保有量	约束性	公顷	4.85	4.85

注释：规划预留0.53公顷的建设用地机动指标用于满足村民居住、农村公共公益设施等项目建设用地需求。


平潭综合实验区苏平镇半山村村庄规划(2022-2035)

村域综合规划图

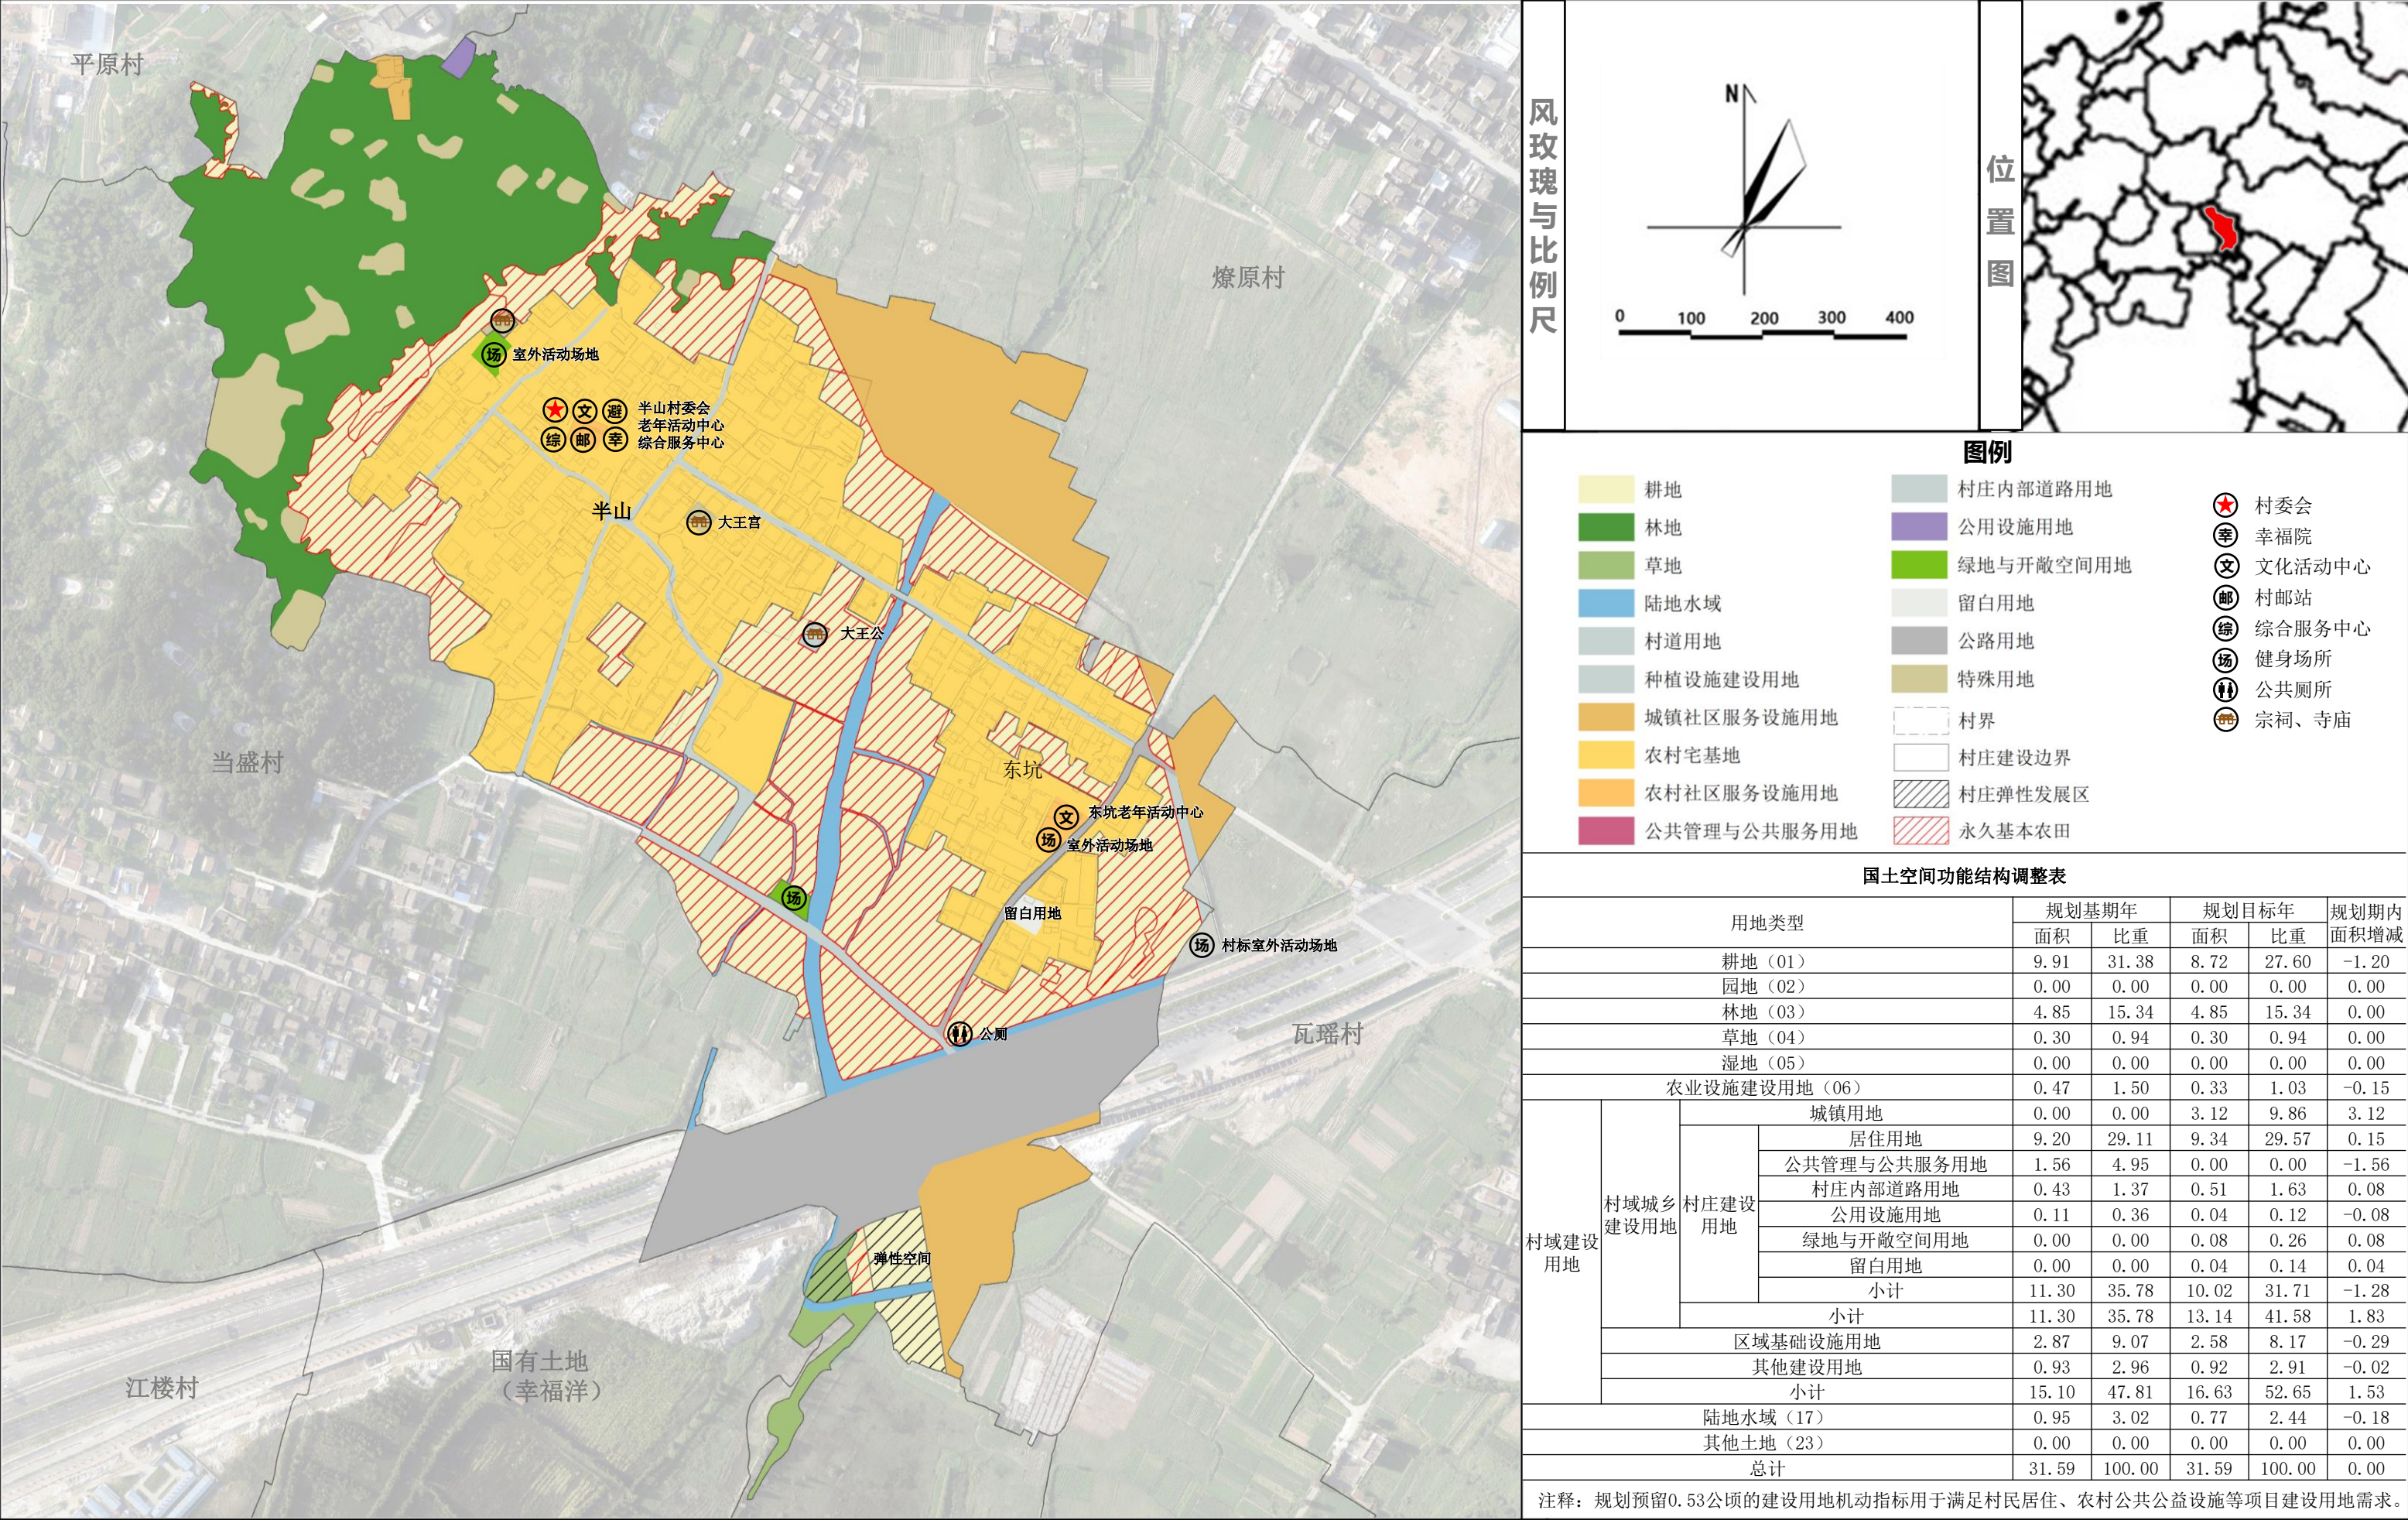


平潭综合实验区苏平镇半山村庄规划(2022-2035)


农村居民点规划布局图

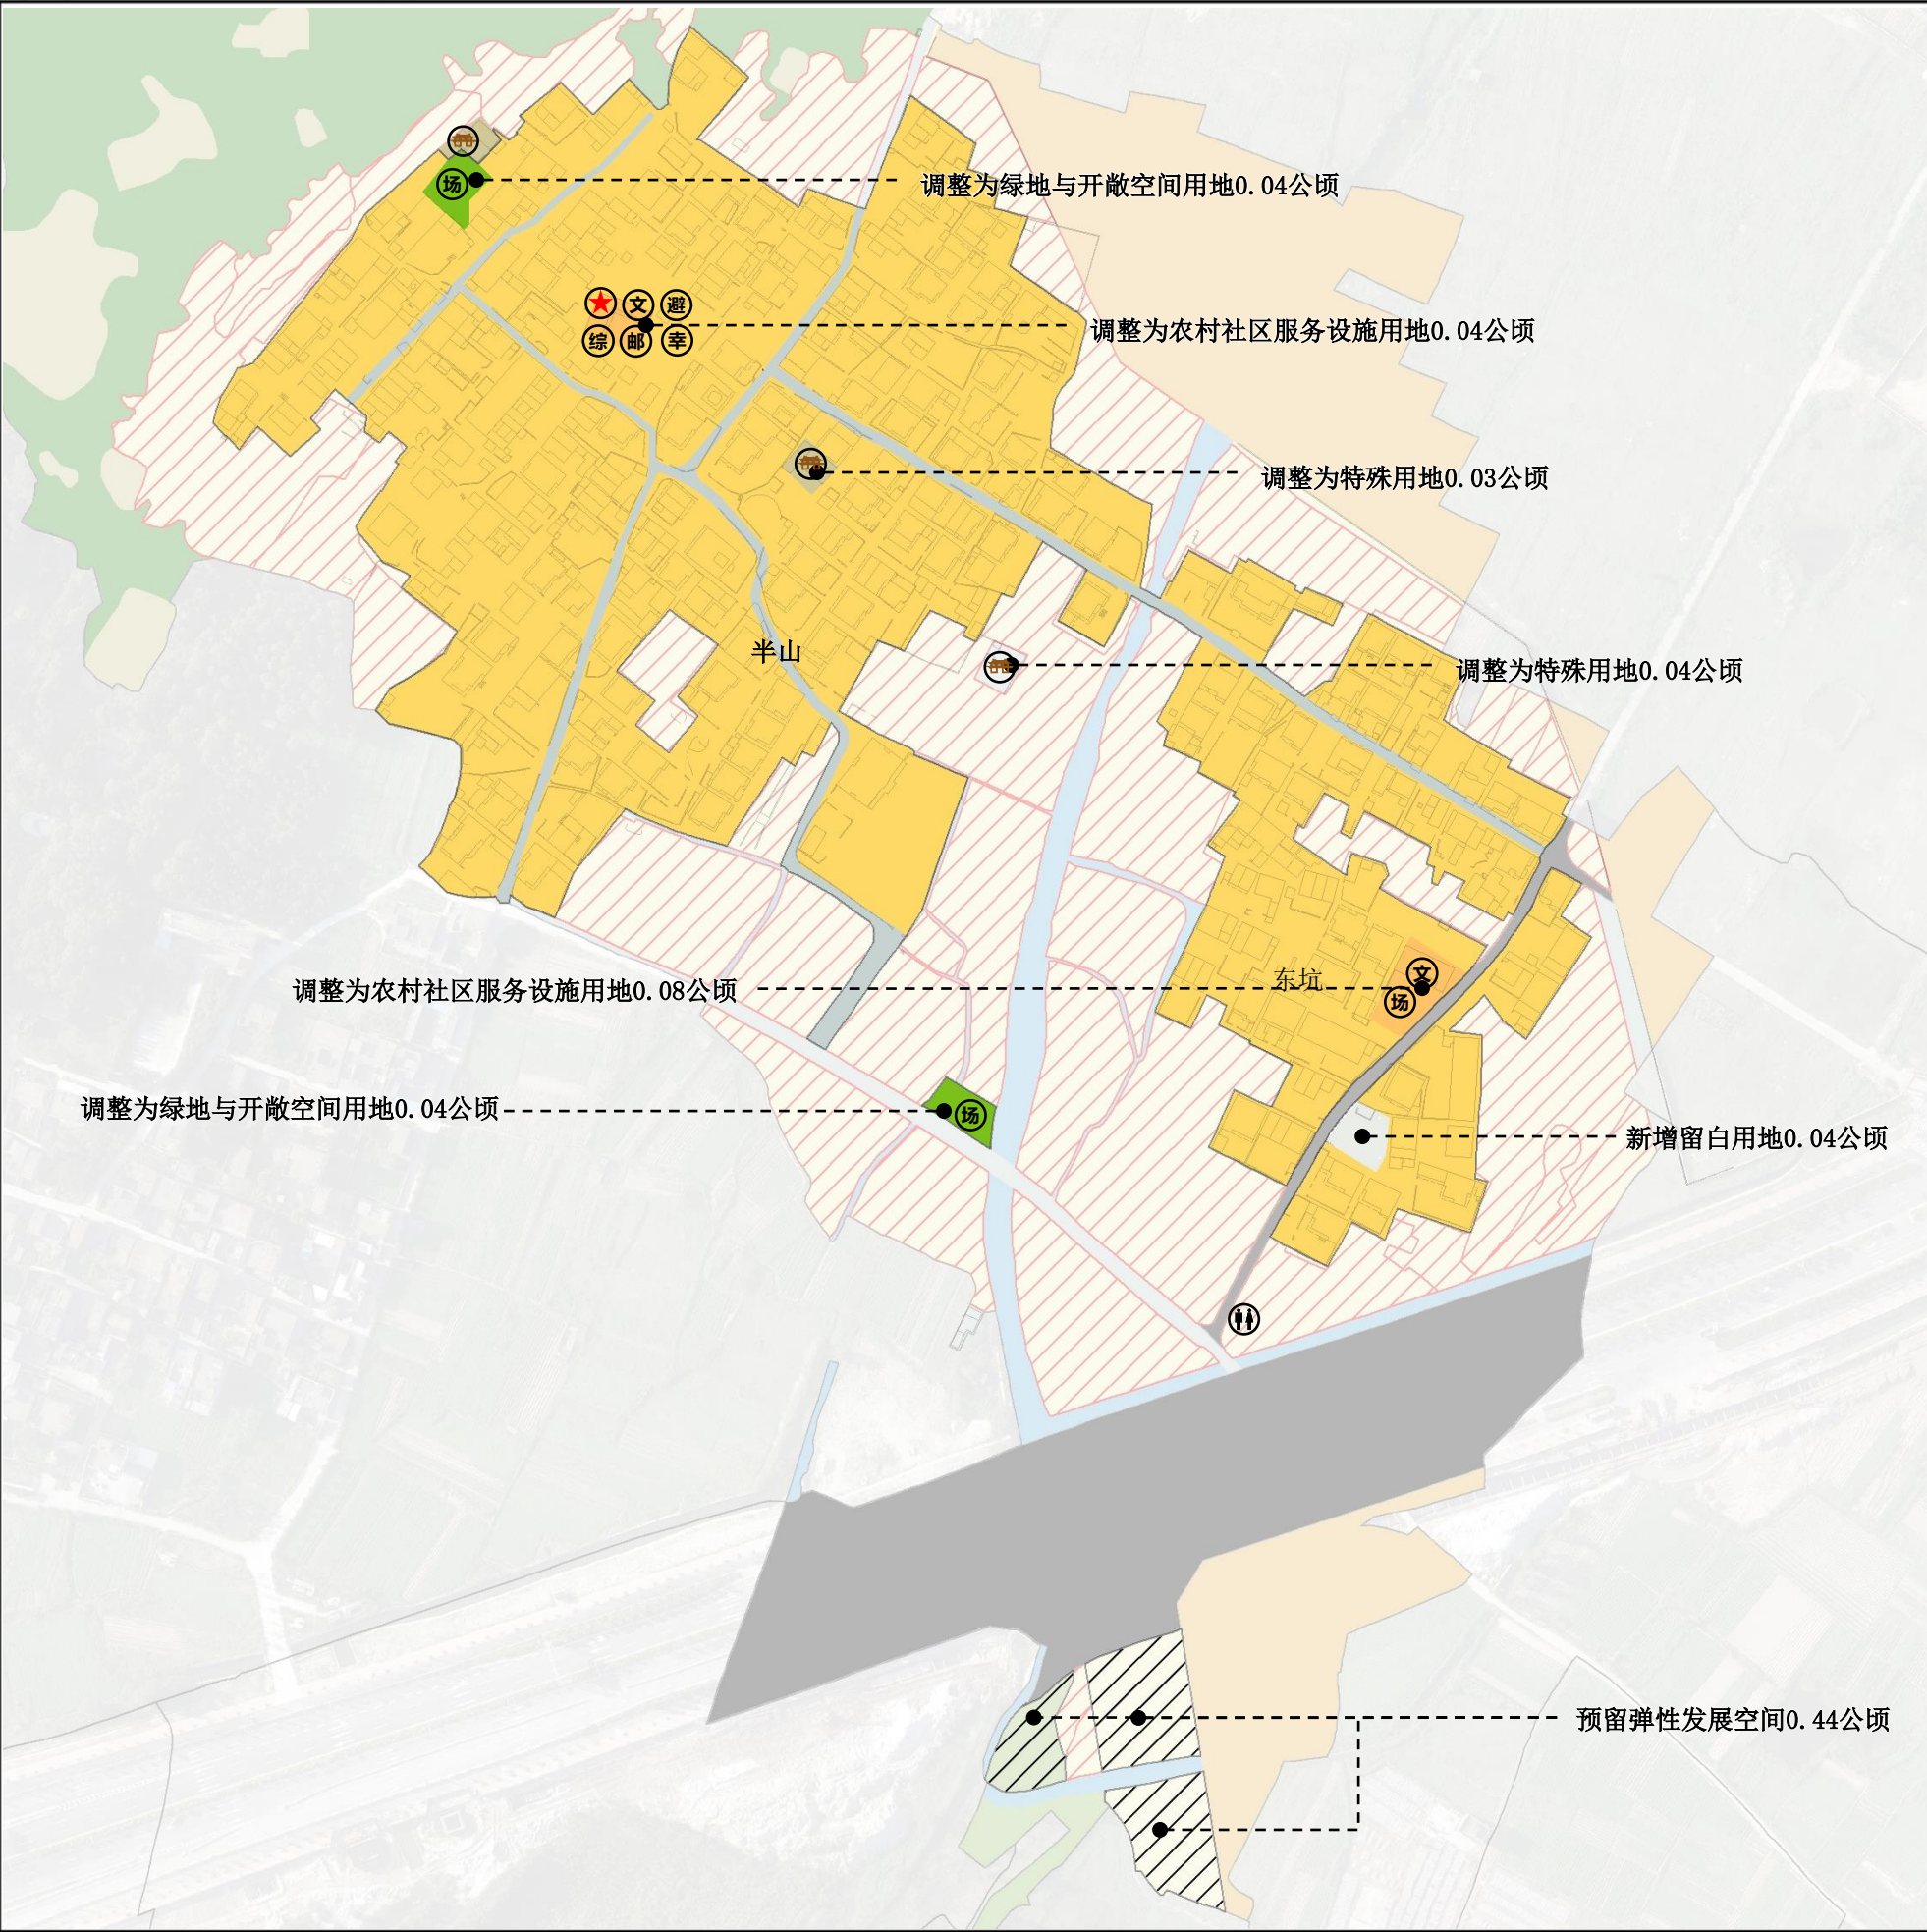

风玫瑰与比例尺

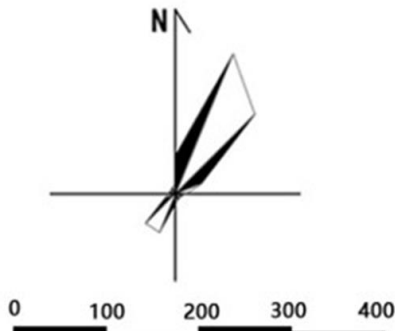

位置图

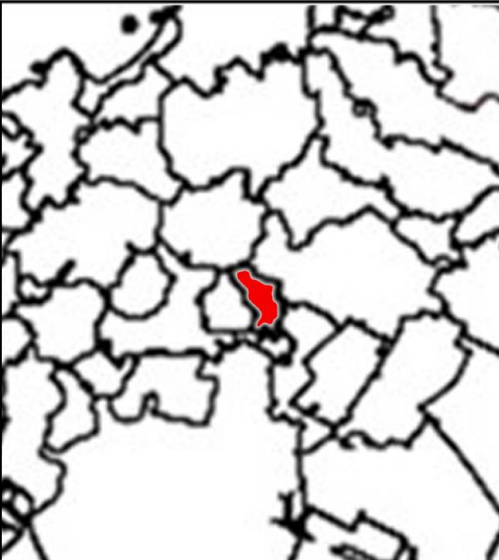

图例

- | | | |
|------------|-----------|--------|
| 村庄建设边界 | 绿地与开敞空间用地 | 村委会 |
| 村庄弹性发展区 | 留白用地 | 幸福院 |
| 农村宅基地 | 公路用地 | 文化活动中心 |
| 农村社区服务设施用地 | 特殊用地 | 村邮站 |
| 村庄内部道路用地 | | 综合服务中心 |
| | | 健身场所 |
| | | 公共厕所 |
| | | 宗祠、寺庙 |

建设空间管控图则

宅基地管制要求

宅基地需严格遵守“一户一宅”政策，村民在原宅基地之外申请新建住宅的，其原有宅基地由村委会收回，村委会制定依法收回村民旧宅基地的经 济补偿。宅基地控制面积在120m²以内，建筑层数控制在3层以内，建筑面积控制在300m²以内。

住房布局控制要求

建筑退距要求

- 1) 新（改）建建筑后退对外交通20米以上、村庄干路3米以上、支路1米以上。
- 2)) 高度大于2米小于6米的挡土墙和护坡，其上缘与同水平面建筑间水平距离不应小于3米，其下缘与同水平面建筑间的水平距离不应小于2米； 高度大于等于6米的挡土墙和护坡，其上下缘与同水平面建筑间的水平距离不应小于6米。
- 3) 溪流两侧宜布置滨水、连续的步行系统或绿化等公共空间，保障滨水空间的共享性。溪流两侧新建建筑退距最小宽度不小于8米。

建筑间距要求

建筑间距应满足日照间距要求，南北向平行布置的建筑其建筑间距不小于南侧建筑高度的1.0倍，低层建筑相邻房屋山墙之间（外墙至外墙）的间 距为4米，设置消防通道的多次建筑山墙最小距离不小于6米。

新建建筑与市政公用设施、工业企业之间的间距应预留5米以上；除此之外东西方向应预留3.5米，南北向方向应满足各类建筑日照要求。

人口规模


半山村现状人口：1092人；远期2035年：1110人。

用地规模


村庄建设用地规模：10.55公顷，人均建设用地面积：95.02m²/人。



风玫瑰与比例尺

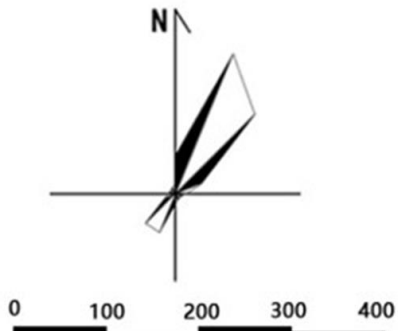

位置图

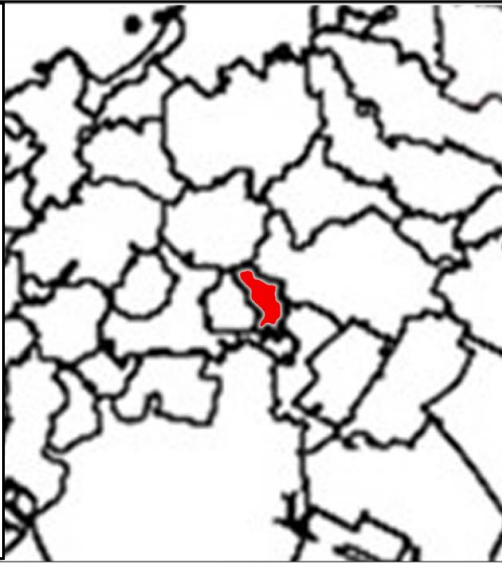

图例

- 公服建筑
- 原址翻建建筑
- 保留建筑
- 弹性用地
- 规划范围

- ① 村委会、半山老年活动中心、综合服务中心
- ② 大公公庙
- ③ 大王公
- ④ 大王宫
- ⑤ 半山村标公园
- ⑥ 东坑老年活动中心
- ⑦ 东坑村标公园
- ⑧ 公厕