



暖通
电气
给排水
结构
建筑

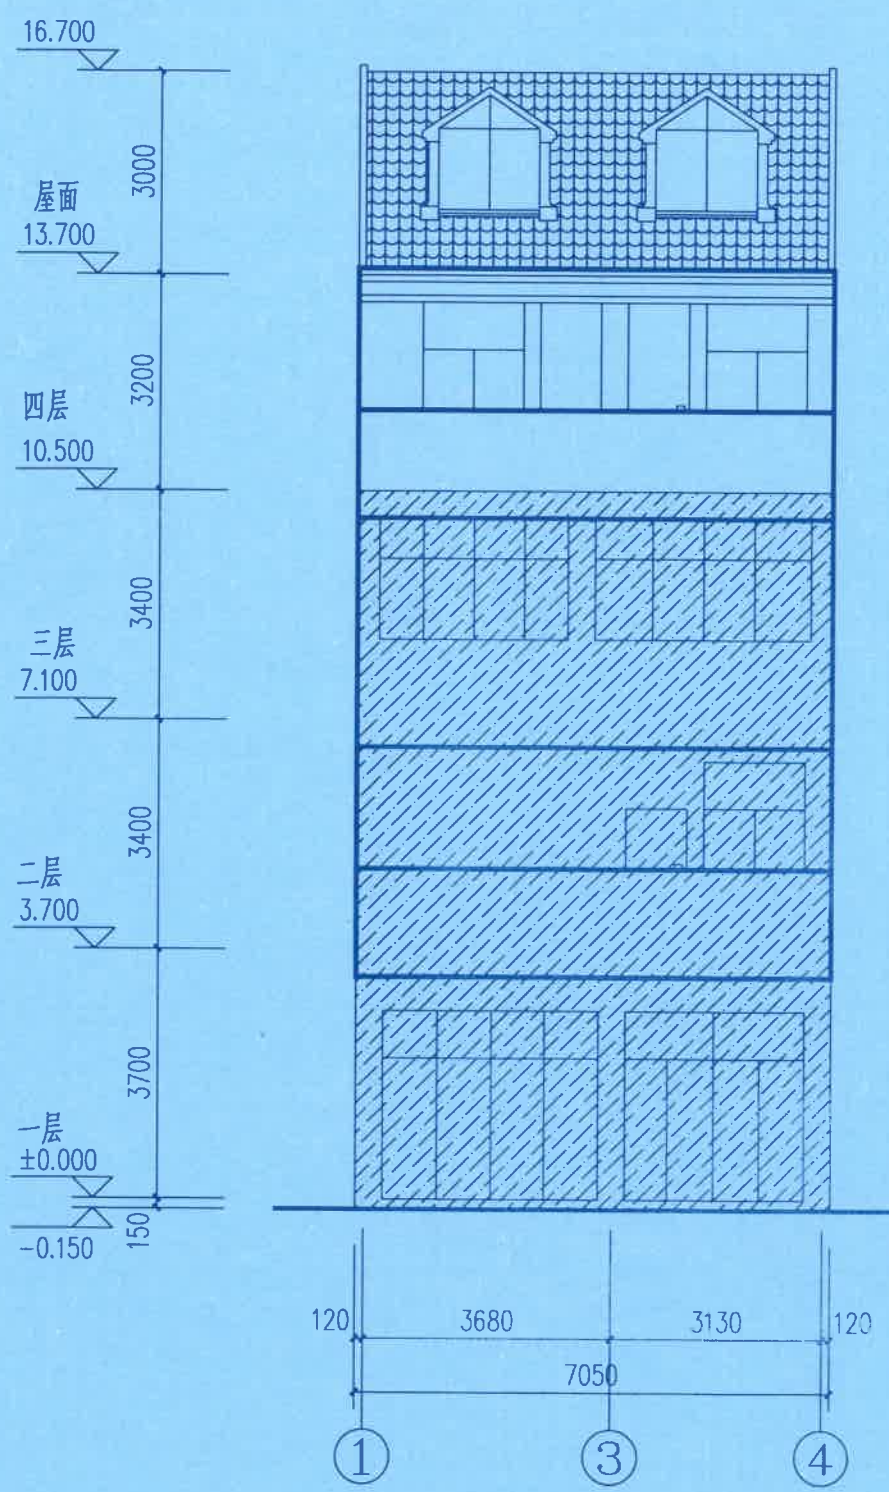

①~④轴立面图 1:100
(沿街面)

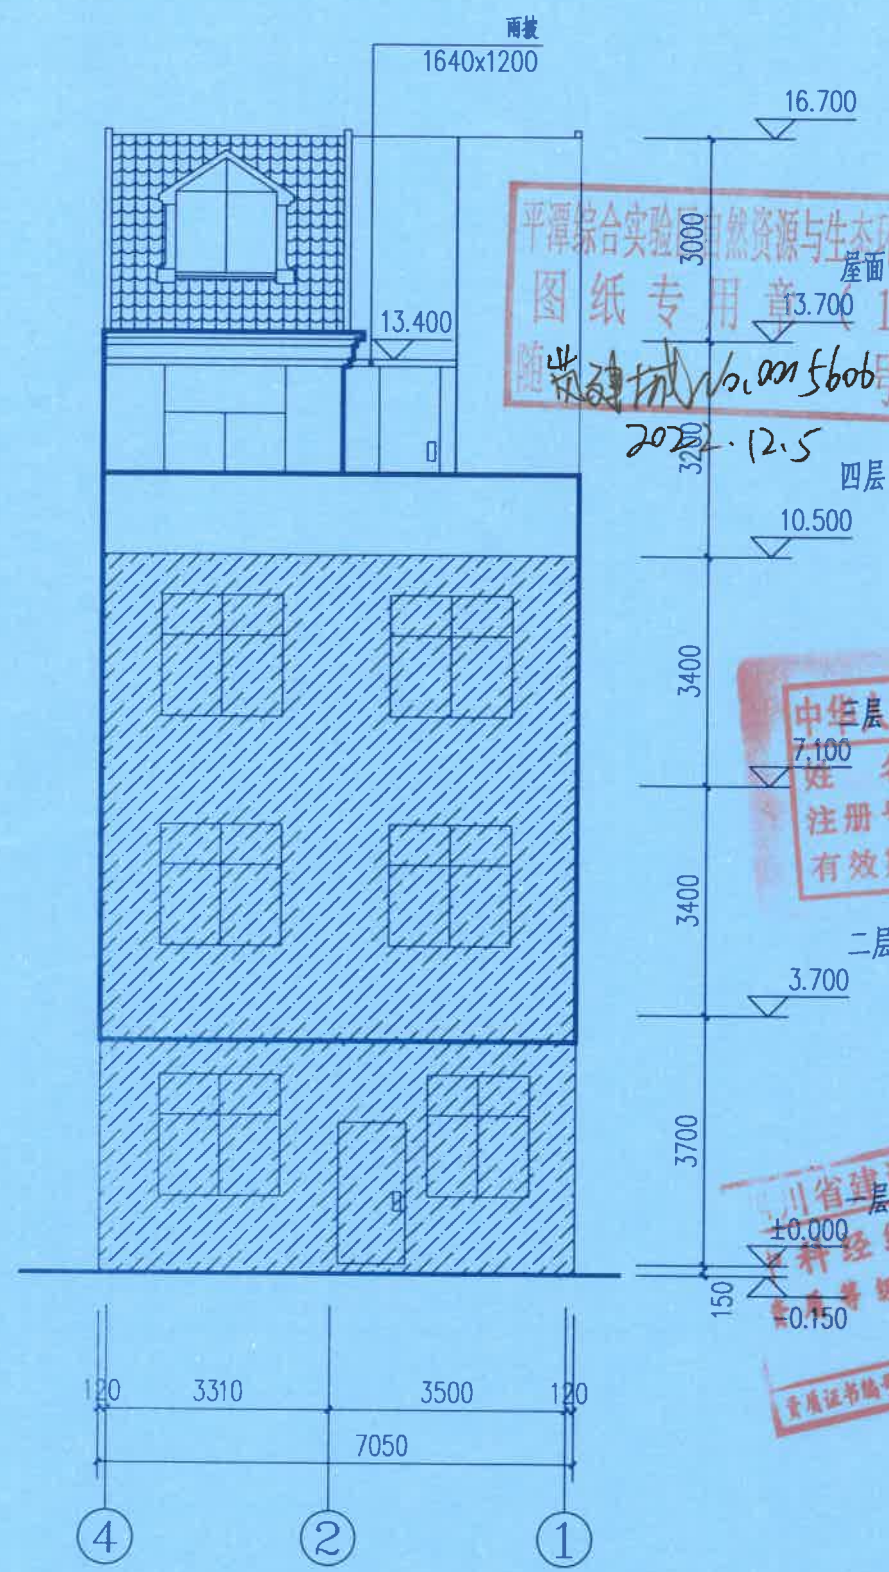

④~①轴立面图 1:100

注: 1. 现状层高应以现场实际高度为准。
2. 阴影部分表示现场已建。
3. 本项目现场已建3层, 本次拟建1层



中科经纬
ZHONGKE JINGWEI

中华人民共和国建设工程设计证书
行业乙级 A251034247
地址: 中国·成都·高新区东虹湾中心2栋7楼
电话: 028-67775960
传真: 028-67775920
E-mail: 3211911868@qq.com
网址: www.zkjwgcjs.com
邮编: 610041

注册执业章

REGISTERED PRACTICE SIGNET

姓名	曹雯
注册印章号	5103424-002
注册证书号	151400588
设计总负责人	曹雯
专业负责人	魏建英
设计	王嘉辉
校对	魏建英
审核	曹雯
审定	曹雯

设计单位 DESIGNER

中科经纬工程技术有限公司

建设单位 CLIENT

四川省建设工程勘察设计研究院有限公司

工程名称 PROJECT

子项名称 SUB PROJECT

图名 TITLE

①~④轴立面图 (拟建)

④~①轴立面图 (拟建)

设计号 PROJECT NO.

图别 DWG TYPE

版本号 Ver.

所有设计图以最新版本为有效版本
本图若未盖本单位出图章则无效