




工程名称	海坛片区黄楼福050 个人住宅
建设单位	
设计单位	平潭综合实验区规划设计研究院
项目负责人	陈明建
专业负责人	陈春
审核人	陈英
制图人	
日期	2021.09

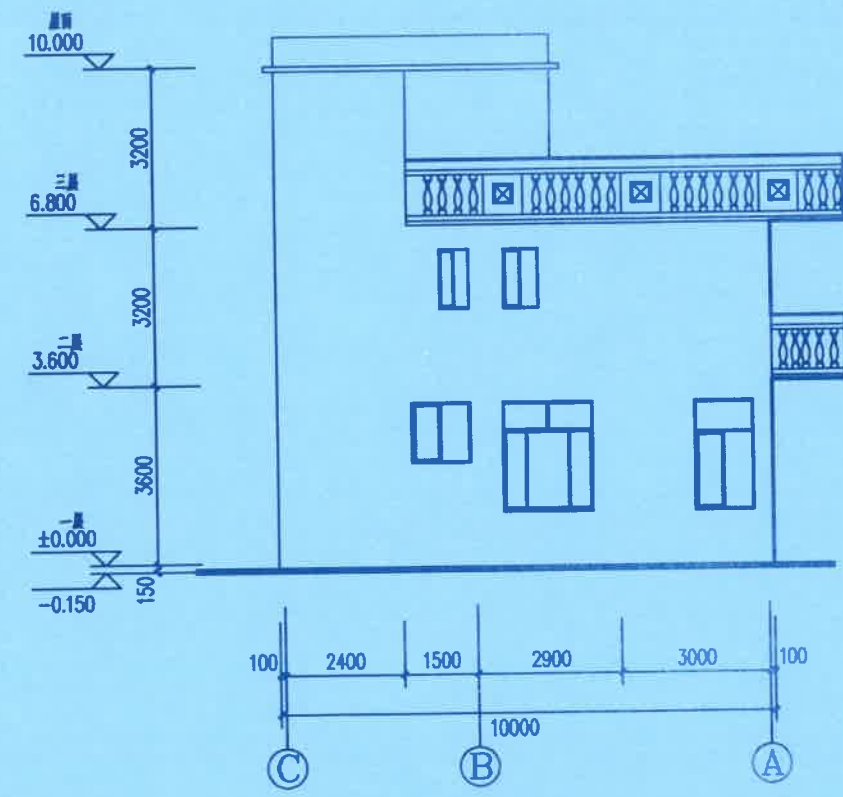

C - A 轴立面图 1:100

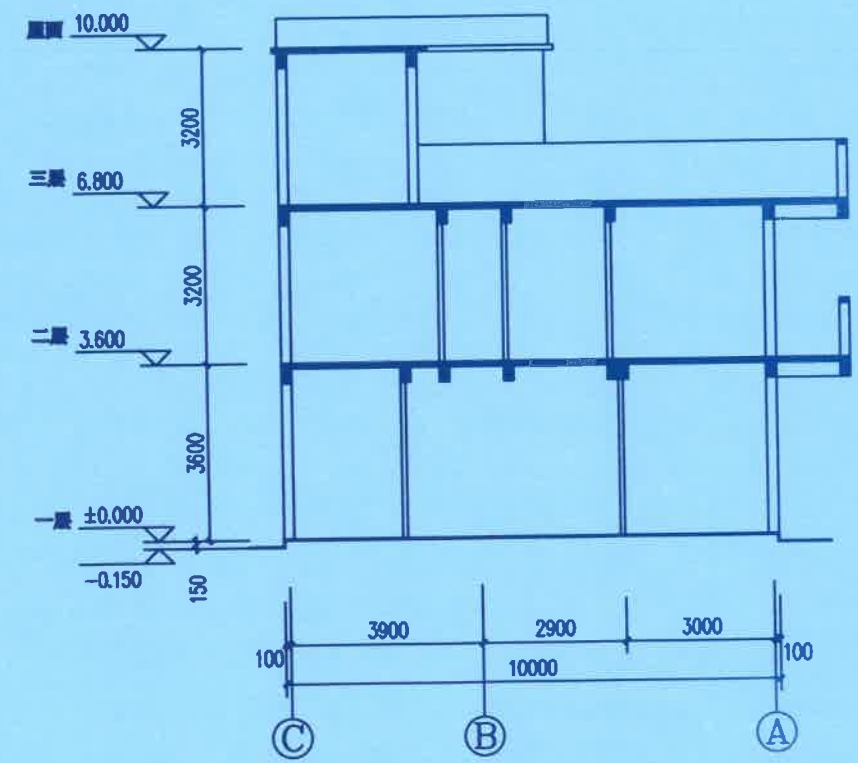

1-1 剖面图 1:100

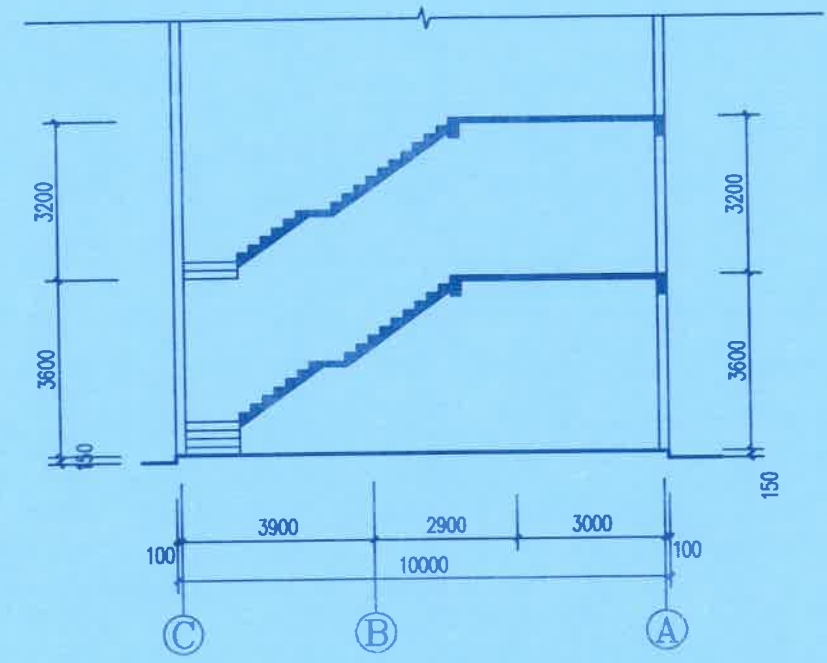

楼梯间剖面图 1:100

平潭综合实验区自然资源局与生态环境局
图纸专用章(1)
随 35012820210919 号有效

平潭综合实验区规划设计研究院
(平潭县建筑勘察设计院)
Pingtan Comprehensive Experimentation Zone
Planning Programming Institute
(Pingtan Architectural Design Institute)
设计证书编号: A235005610
ARCHITECTURAL DESIGN LICENSE No. A235005610

备注:
图章专用章
注册建筑师执业章
注册结构师执业章

施工图审查批准单位
施工图审查批准书证号

工程名称
海坛片区黄楼福050 个人住宅

建设单位	
审定	
工程负责人	陈明建
专业负责人	陈春
审核	陈英
校对	
设计	
制图	

图名
C~A轴立面图
1-1剖面图

工程编号	WFPJ4-海坛片050
图别	方案
图号	08
日期	2021.09