


平潭综合实验区苏平片区 江楼村 村庄规划（2021-2035）修编 —— 公示文件

■ 村域综合规划图

规划必备指标一览表					
序号	指标	属性	单位	现状基期年	规划目标年
一、村庄发展性指标					
1	村域建设用地总面积	约束性	公顷	75.15	80.33
2	村域城乡建设用地面积	约束性	公顷	26.76	32.79
3	村庄建设用地规模	预期性	公顷	26.76	32.37
4	公共管理与公共服务用地规模	预期性	公顷	0.23	1.11
5	公用设施用地规模	预期性	公顷	—	0.06
6	人均村庄建设用地面积	预期性	平方米/人	72.61	81.91
二、村庄保护性指标					
7	生态保护红线面积	约束性	公顷	—	—
8	永久基本农田保护面积	约束性	公顷	43.01	43.01
9	耕地保有量	约束性	公顷	46.54	49.87
10	林地保有量	约束性	公顷	12.54	7.86
11	湿地面积	约束性	公顷	—	—
12	大陆自然海岸线保有率	预期性	%	—	—
13	自然和文化遗产	预期性	处	1	1

国土空间功能结构调整表						单位：公顷、%
用地类型名称及编码		规划基期年		规划目标年		规划期内面积增减
		面积	比重	面积	比重	
耕地 (01)		46.54	24.13	49.87	25.86	3.34
园地 (02)		0.31	0.16	0.20	0.10	-0.11
林地 (03)		12.54	6.50	7.86	4.07	-4.68
草地 (04)		—	—	—	—	—
湿地 (05)		—	—	—	—	—
农业设施建设用地 (06)		1.95	1.01	1.78	0.92	-0.17
村域建设用地	城镇用地	—	—	0.42	0.22	0.42
	居住用地 (0703-0704)	24.33	12.61	25.08	13.00	0.75
	公共管理与公共服务用地 (08)	0.23	0.12	0.21	0.11	-0.02
	商业服务业用地 (09)	0.32	0.17	0.21	0.11	-0.12
	工业用地 (1001)	0.04	0.02	0.04	0.02	0.00
	仓储用地 (11)	—	—	—	—	—
	村庄内部道路用地 (060102)	1.63	0.85	1.92	1.00	0.29
	交通场站用地 (1208)	0.02	0.01	0.03	0.01	0.01
	其他交通设施用地 (1209)	—	—	—	—	—
	公用设施用地 (1301-1310,1313)	—	—	0.06	0.03	0.06
	绿地与开敞空间用地 (14)	—	—	0.14	0.07	0.14
	留白用地 (16)	—	—	4.68	2.42	4.68
	空闲地 (2301)	0.18	0.09	—	—	-0.18
小计		26.76	13.87	32.37	16.78	5.61
小计		26.76	13.87	32.79	17.00	6.03
区域基础设施用地(1201-1206,1311,1312)		46.33	24.02	45.46	23.57	-0.87
其他建设用地(15,1002,1003)		2.07	1.07	2.09	1.08	0.02
小计		75.15	38.96	80.33	41.64	5.17
陆地水域 (17)		56.41	29.24	52.85	27.40	-3.55
总计		192.89	100.00	192.89	100.00	0.00

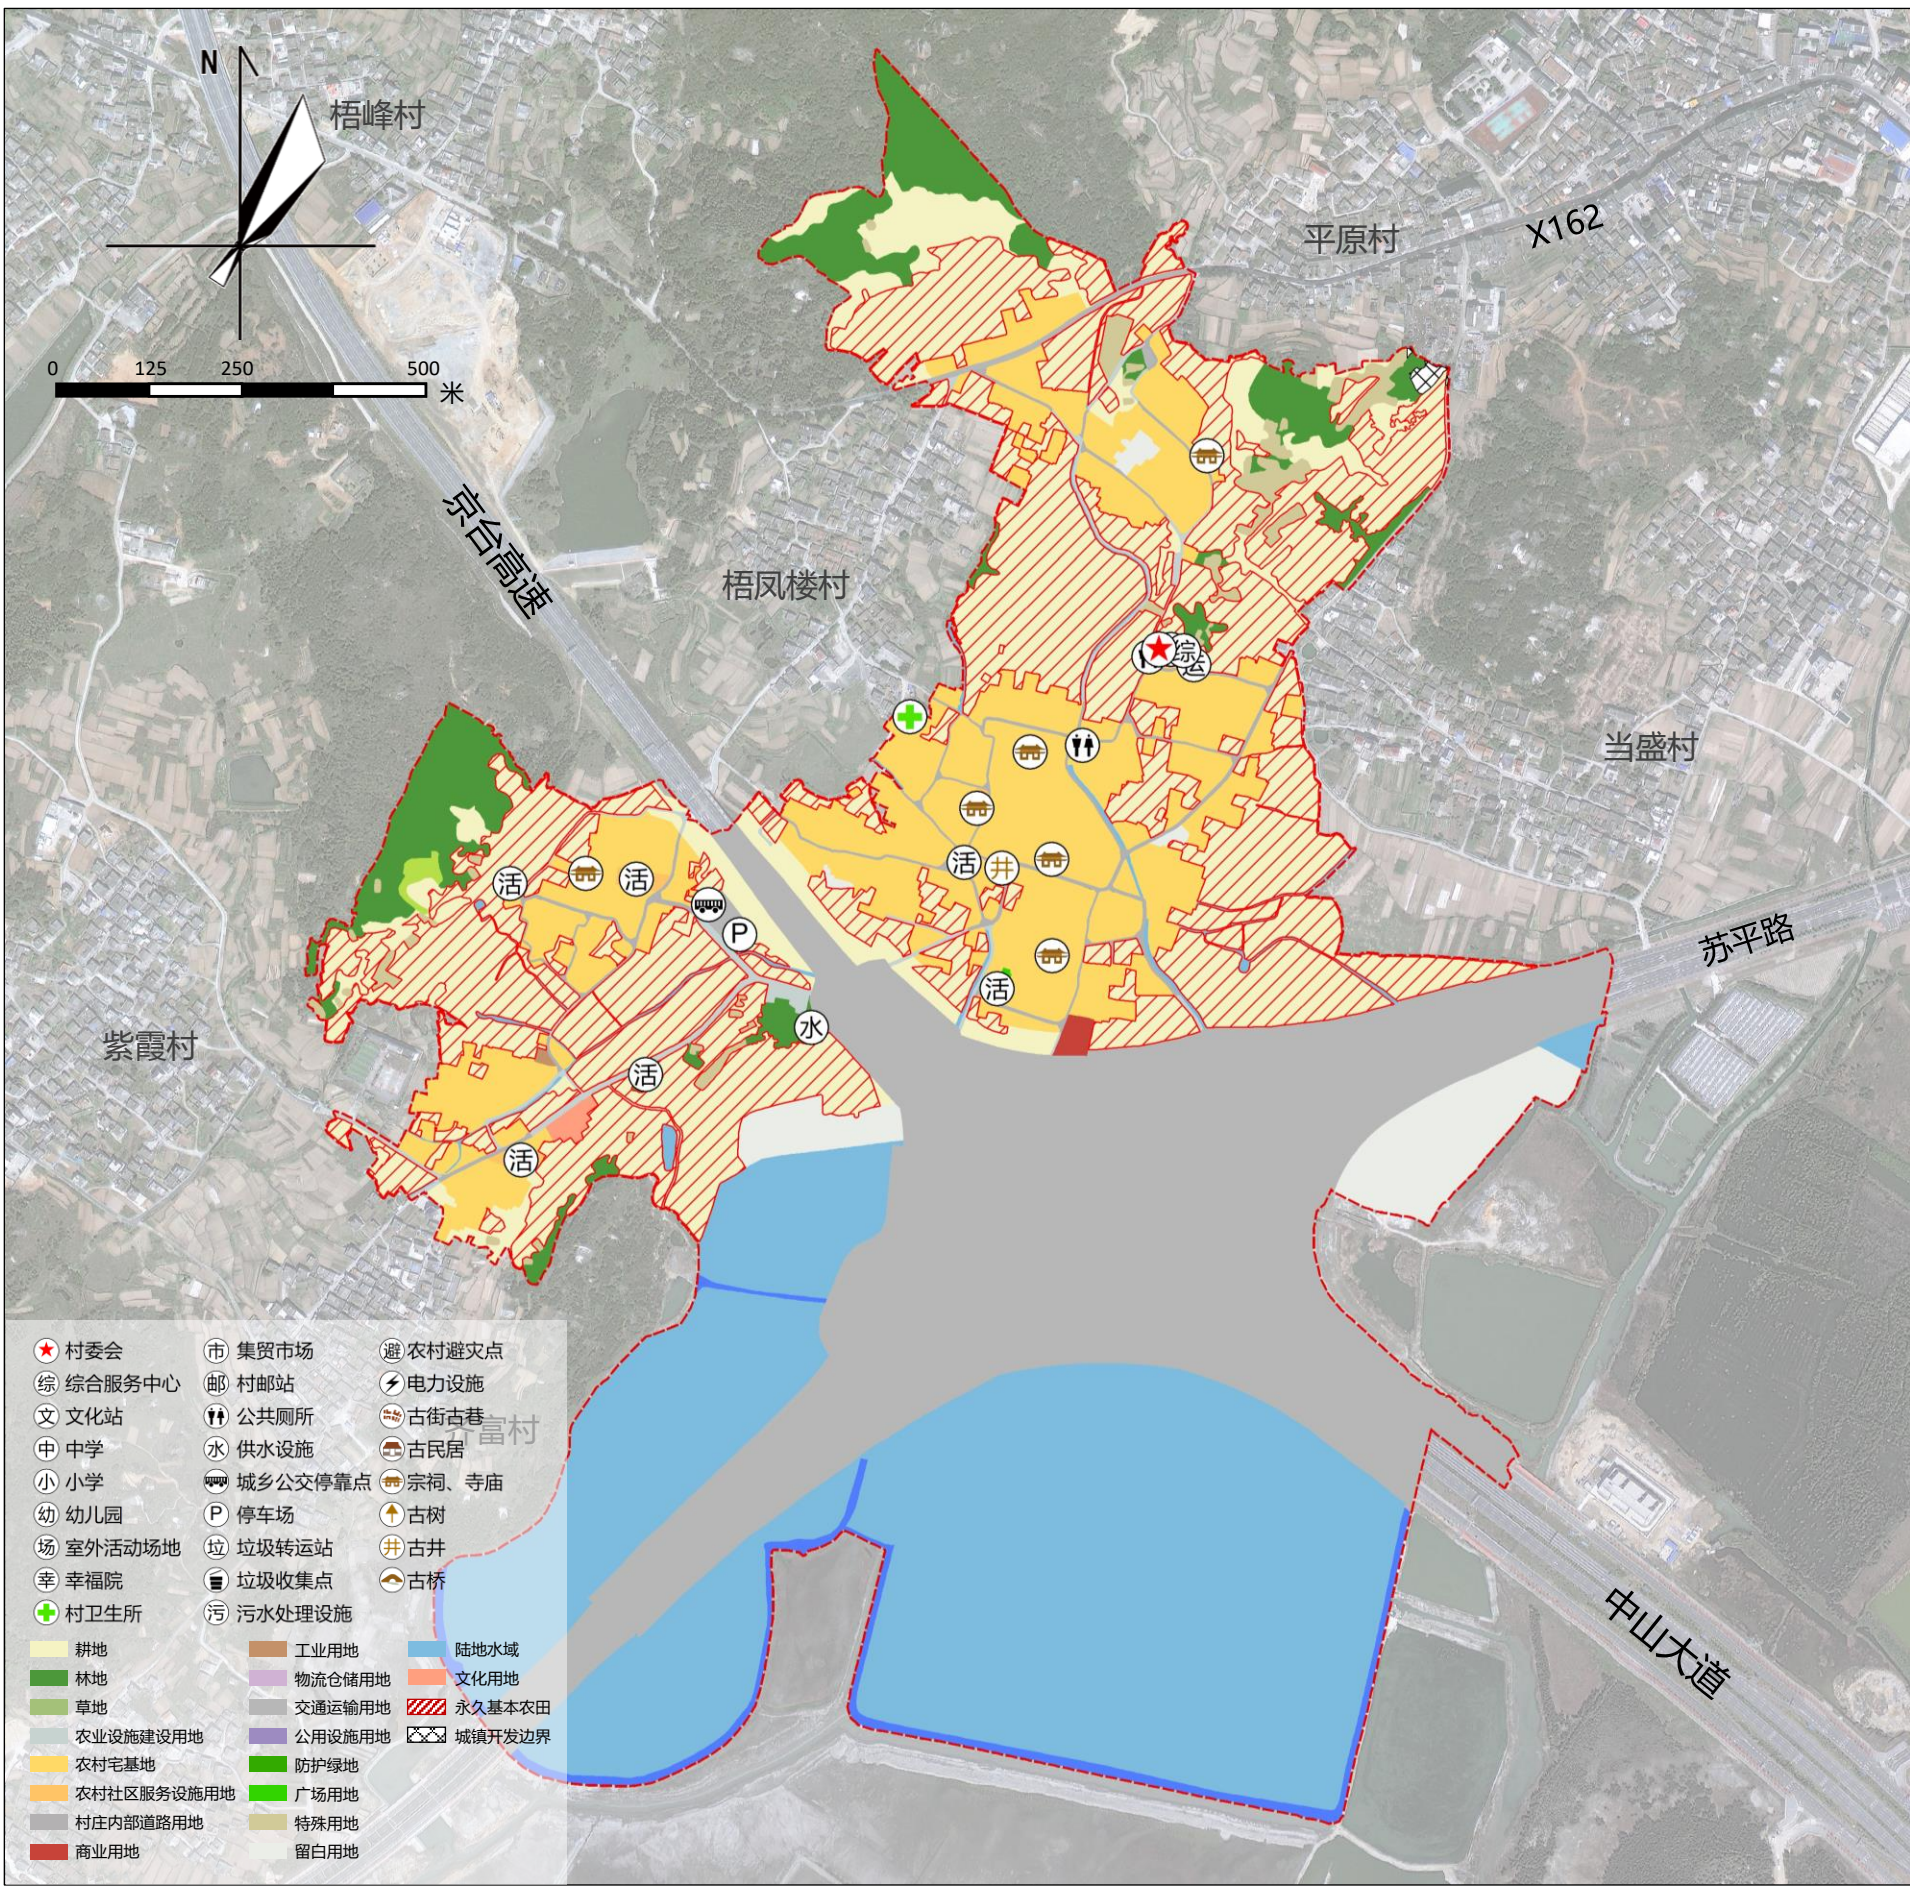

■ 总平面图




■ 居民点规划布局图

通过建设用地占用基本农田调整、用地结构优化等，在不与永久基本农田冲突的前提下，结合建设用地总量、村庄产业发展和公共服务设施配套等需求，对江楼村民居点进行综合布局。最终划定：

规划期末江楼村村域建设用地为32.37公顷，人均农村居民点建设用地面积为81.91平方米。

村庄新增建设用地规划控制内容及要求					
用地性质	地块编号	规划内容	要求		管控方式
			总体要求	说明	
留白用地	ZA-01 ZA-02 ZA-04 ZA-07 ZA-09	—	用地面积：46751.65㎡	预留留白用地，应对未来发展的不确定性，增加规划弹性，暂不明确规划用地。	实位刚性控制
广场用地	ZA-03 ZA-06	休闲广场	用地面积：1497.26㎡	规划建设休闲广场作为村庄文化活动场所，可配备一定的健身器材	实位刚性控制
供水用地	ZA-05	泵站	用地面积：503.88㎡	近期建设供水泵站。	实位刚性控制
文化用地	ZA-08	博物馆	用地面积：2095.63㎡	规划建设苏平畚文化博物馆。	实位刚性管控
弹性发展区			用地面积：5606.36㎡	划定弹性发展区，为应对村庄发展不确定性。	实位刚性控制

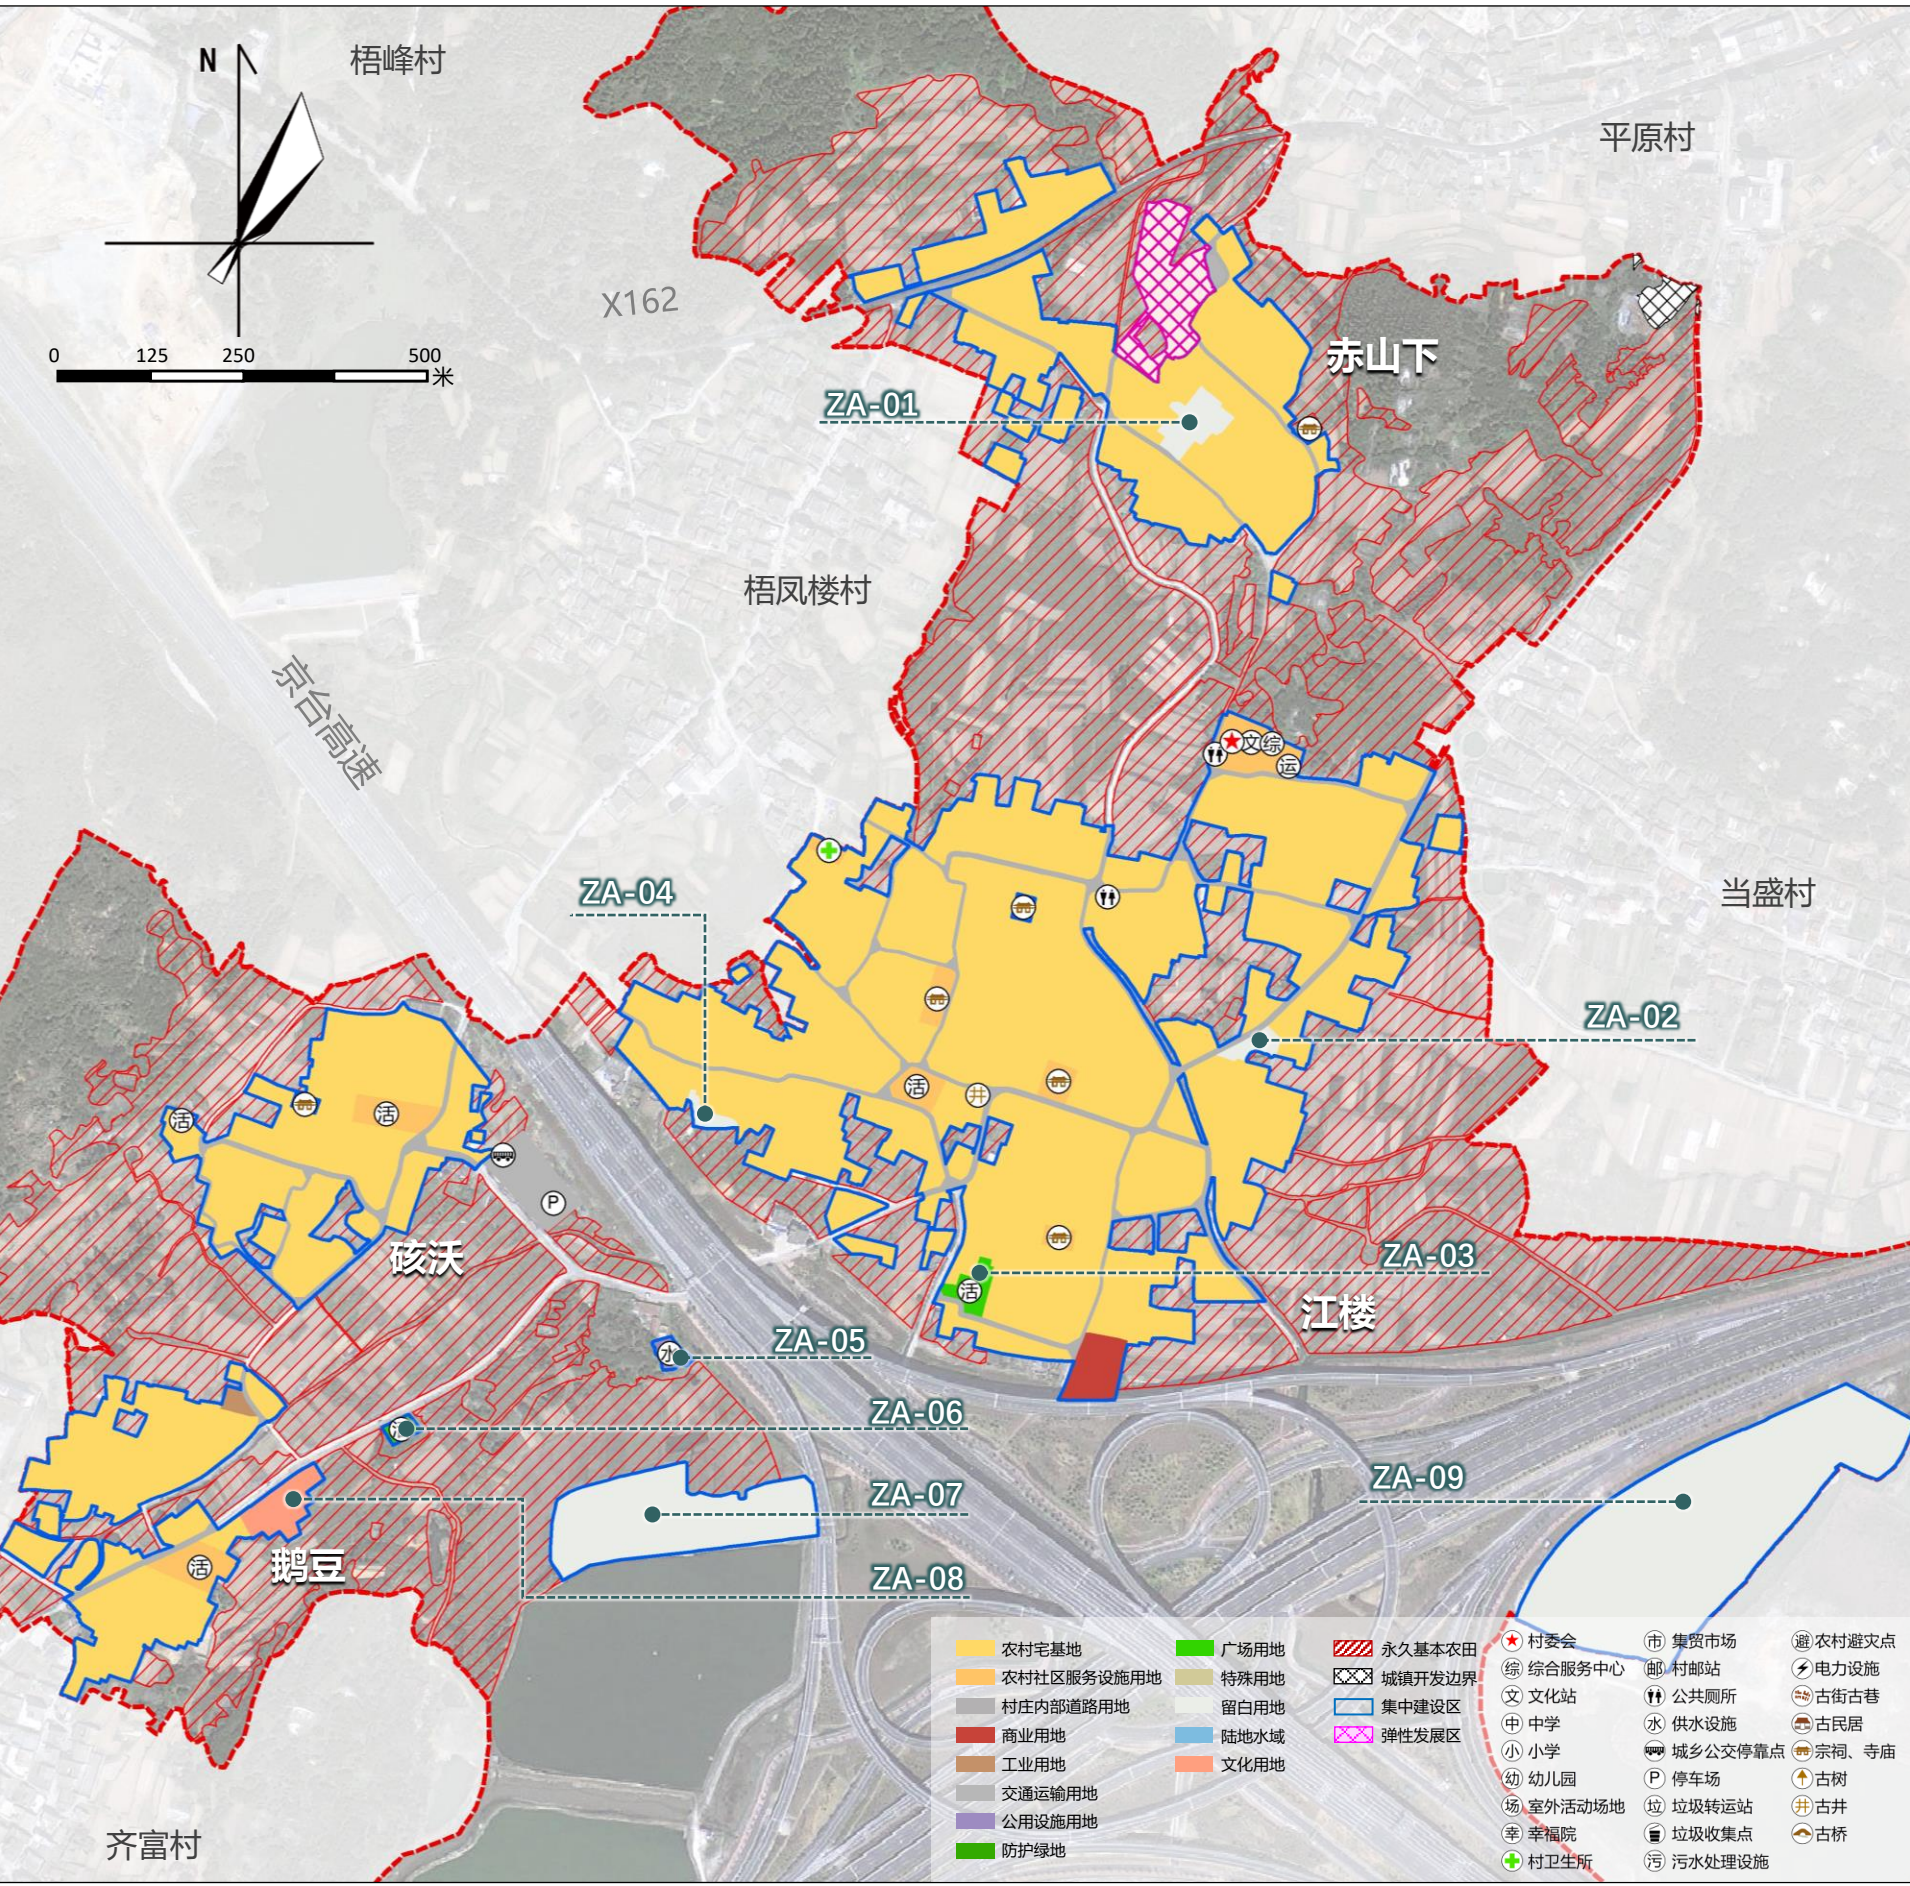

■ 近期建设项目表

近期建设项目一览表						
序号	工程类型	项目名称	项目规模	建设年限	投资总额 (万元)	资金来源 (万元)
					财政	社会 专项
1	新增道路	新增主路，道路长度为120m，宽度为3m。	2023-2025	10.8	10.8	—
2	新增道路	新增主路，道路长度为120m，宽度为3m。	2023-2025	10.8	10.8	—
3	道路交通	新增主路，道路长度为80m，宽度为3m。	2023-2025	7.2	7.2	—
4	新增道路	新增主路，道路长度为100m，宽度为3m。	2023-2025	9	9	—
5	新增道路	新增主路，道路长度为70m，宽度为6.5m。	2023-2025	13.7	13.7	—
6	新增停车场	碓沃新建公交场站，规模为1800㎡。	2023-2025	36	36	—
7	市政公用设施	新建江楼给水泵站，规模为500㎡。	2023-2025	13	13	—
8	公共服务设施	新增广场江楼居民点新增一处广场绿地，规模为1100平方米。	2023-2025	22	5	17
9	土地综合整治	高标准农田建设 赤山南山侧耕地建设高标准农田，规模为50000㎡。	2023-2025	15	—	—
合计				137.5	120.5	17

