



平潭综合实验区苏平片区 围东村 村庄规划（2021-2035）修编 —— 公示文件

■ 国土空间规划

规划必选指标一览表						
序号	指标	属性	单位	现状基期年	规划目标年	
一、村庄发展性指标						
1	村域建设用地总面积	约束性	公顷	11.76	14.26	
2	村域城乡建设用地面积	约束性	公顷	7.88	9.83	
3	村庄建设用地规模	预期性	公顷	7.88	9.83	
4	公共管理与公共服务用地规模	预期性	公顷	0.21	0.13	
5	公用设施用地规模	预期性	公顷	—	0.10	
6	人均村庄建设用地面积	预期性	平方米/人	40.80	47.70	
二、村庄保障性指标						
7	生态保护红线面积	约束性	公顷	—	—	
8	永久基本农田保护面积	约束性	公顷	18.89	18.89	
9	耕地保有量	约束性	公顷	20.55	20.15	
10	林地保有量	约束性	公顷	179.04	176.83	
11	湿地面积	约束性	公顷	0.00	0.00	
12	大陆自然海岸线保有率	约束性	%	87.51	87.51	
13	自然和文化遗产	预期性	处	—	—	
空间功能结构调整表						
单位：公顷、%						
用地类型名称及代码		规划基期年		规划目标年		规划期内面积增减
		面积	比重	面积	比重	
耕地 (01)		20.55	9.58	20.15	9.39	-0.40
园地 (02)		—	—	—	—	—
林地 (03)		179.04	83.45	176.83	82.42	-2.20
草地 (04)		0.32	0.15	0.32	0.15	-0.00
湿地 (05)		—	—	—	—	—
农业设施建设用地 (06)		0.09	0.04	0.25	0.11	0.15
村域城乡建设用地	城镇用地	—	—	—	—	—
	居住用地 (0703-0704)	7.52	3.51	7.21	3.36	-0.31
	公共管理与公共服务设施用地 (08)	0.21	0.10	—	—	-0.21
	商业服务业用地 (09)	—	—	0.43	0.20	0.43
	工业用地 (1001)	—	—	—	—	—
	仓储用地 (11)	—	—	—	—	—
	村庄内部道路用地 (060102)	0.14	0.07	0.64	0.30	0.50
	交通场站用地 (1208)	—	—	0.23	0.11	0.23
	其他交通设施用地 (1209)	—	—	—	—	—
	公用设施用地 (1301-1310,1313)	—	—	0.10	0.05	0.10
	绿地与开敞空间用地 (14)	—	—	0.48	0.22	0.48
	留白用地 (16)	—	—	0.73	0.34	0.73
	空闲地 (2301)	—	—	—	—	—
	小计	7.88	3.67	9.83	4.58	1.95
	小计	7.88	3.67	9.83	4.58	1.95
区域基础设施用地(1201-1206,1311,1312)		2.94	1.37	3.19	1.49	0.25
其他建设用地(15,1002,1003)		0.95	0.44	1.24	0.58	0.29
小计		11.76	5.48	14.26	6.65	2.50
陆地水域 (17)		0.59	0.27	0.55	0.25	-0.04
其他土地 (23)		2.20	1.02	2.20	1.02	0.00
总计		214.54	100.00	214.54	100.00	0.00

■ 村庄居民点布局规划

村庄新增建设用地规划控制内容及要求					
用地性质	地块编号	规划内容	要求		管控方式
			总体要求	说明	
社会停车场用地	ZA-01 ZA-11	停车场	用地面积：1602.76㎡	近期建设生态停车场。	实位刚性控制
宅基地用地	ZA-03 ZA-07 ZA-08	村民宅基地	用地面积：3536.21㎡ 建筑限高：≤12m 容积率：1-1.5	应符合《福建省农村村民住宅建设管理办法》的有关要求。	实位刚性控制
环卫用地	ZA-05	公共厕所	用地面积：61.37㎡	—	实位刚性控制
公园绿地	ZA-02	健身场地	用地面积：408.67㎡	应符合《福建省村庄规划编制指南》（试行）和福建省地方标准《村庄规划编制规程》（DB35/T 2061-2022）相关要求的有关要求。	实位刚性控制
	ZA-04	小游园	用地面积：447.80㎡		实位刚性控制
	ZA-10	观景平台	用地面积：657.01㎡		实位刚性控制
供水用地	ZA-12	供水泵站	用地面积：108.20㎡	纳入平潭供水一体化。	实位刚性控制
留白用地	ZA-06 ZA-09	—	用地面积：7313.75㎡	预留留白用地，应对未来发展的不确定性，增加规划弹性，暂不明确规划用地。	实位刚性控制
弹性发展区			用地面积：1382.07㎡	划定弹性发展区，为应对村庄发展不确定性。	点位弹性控制

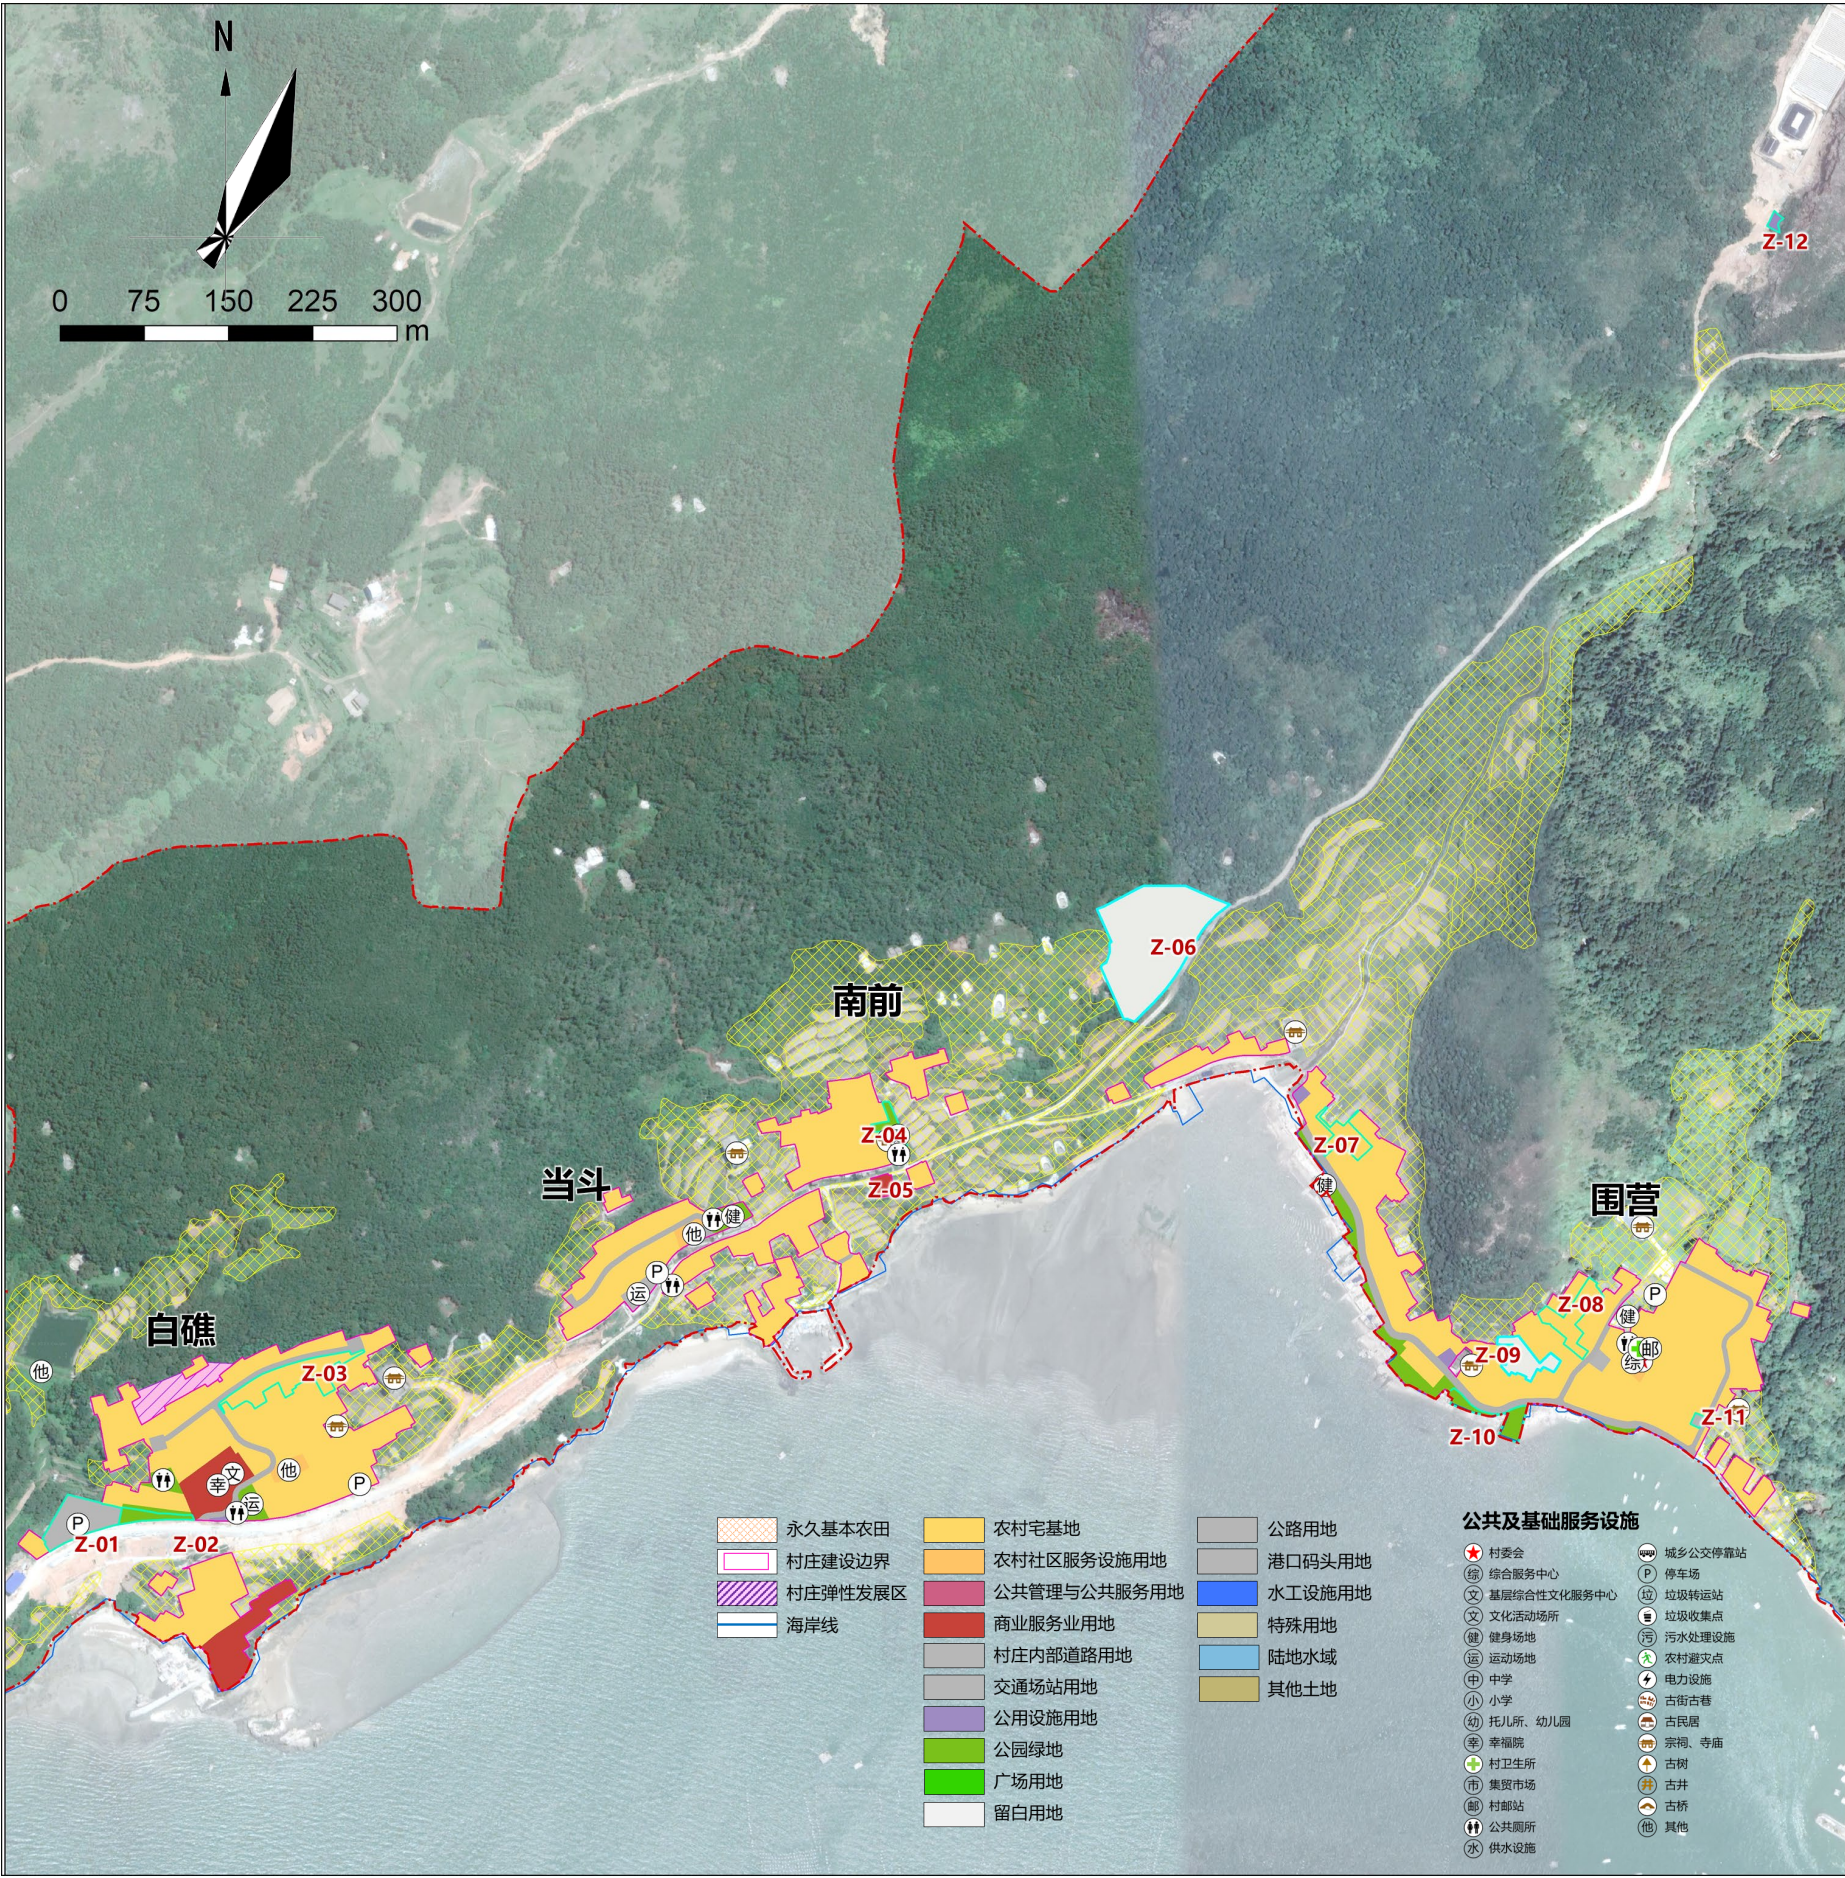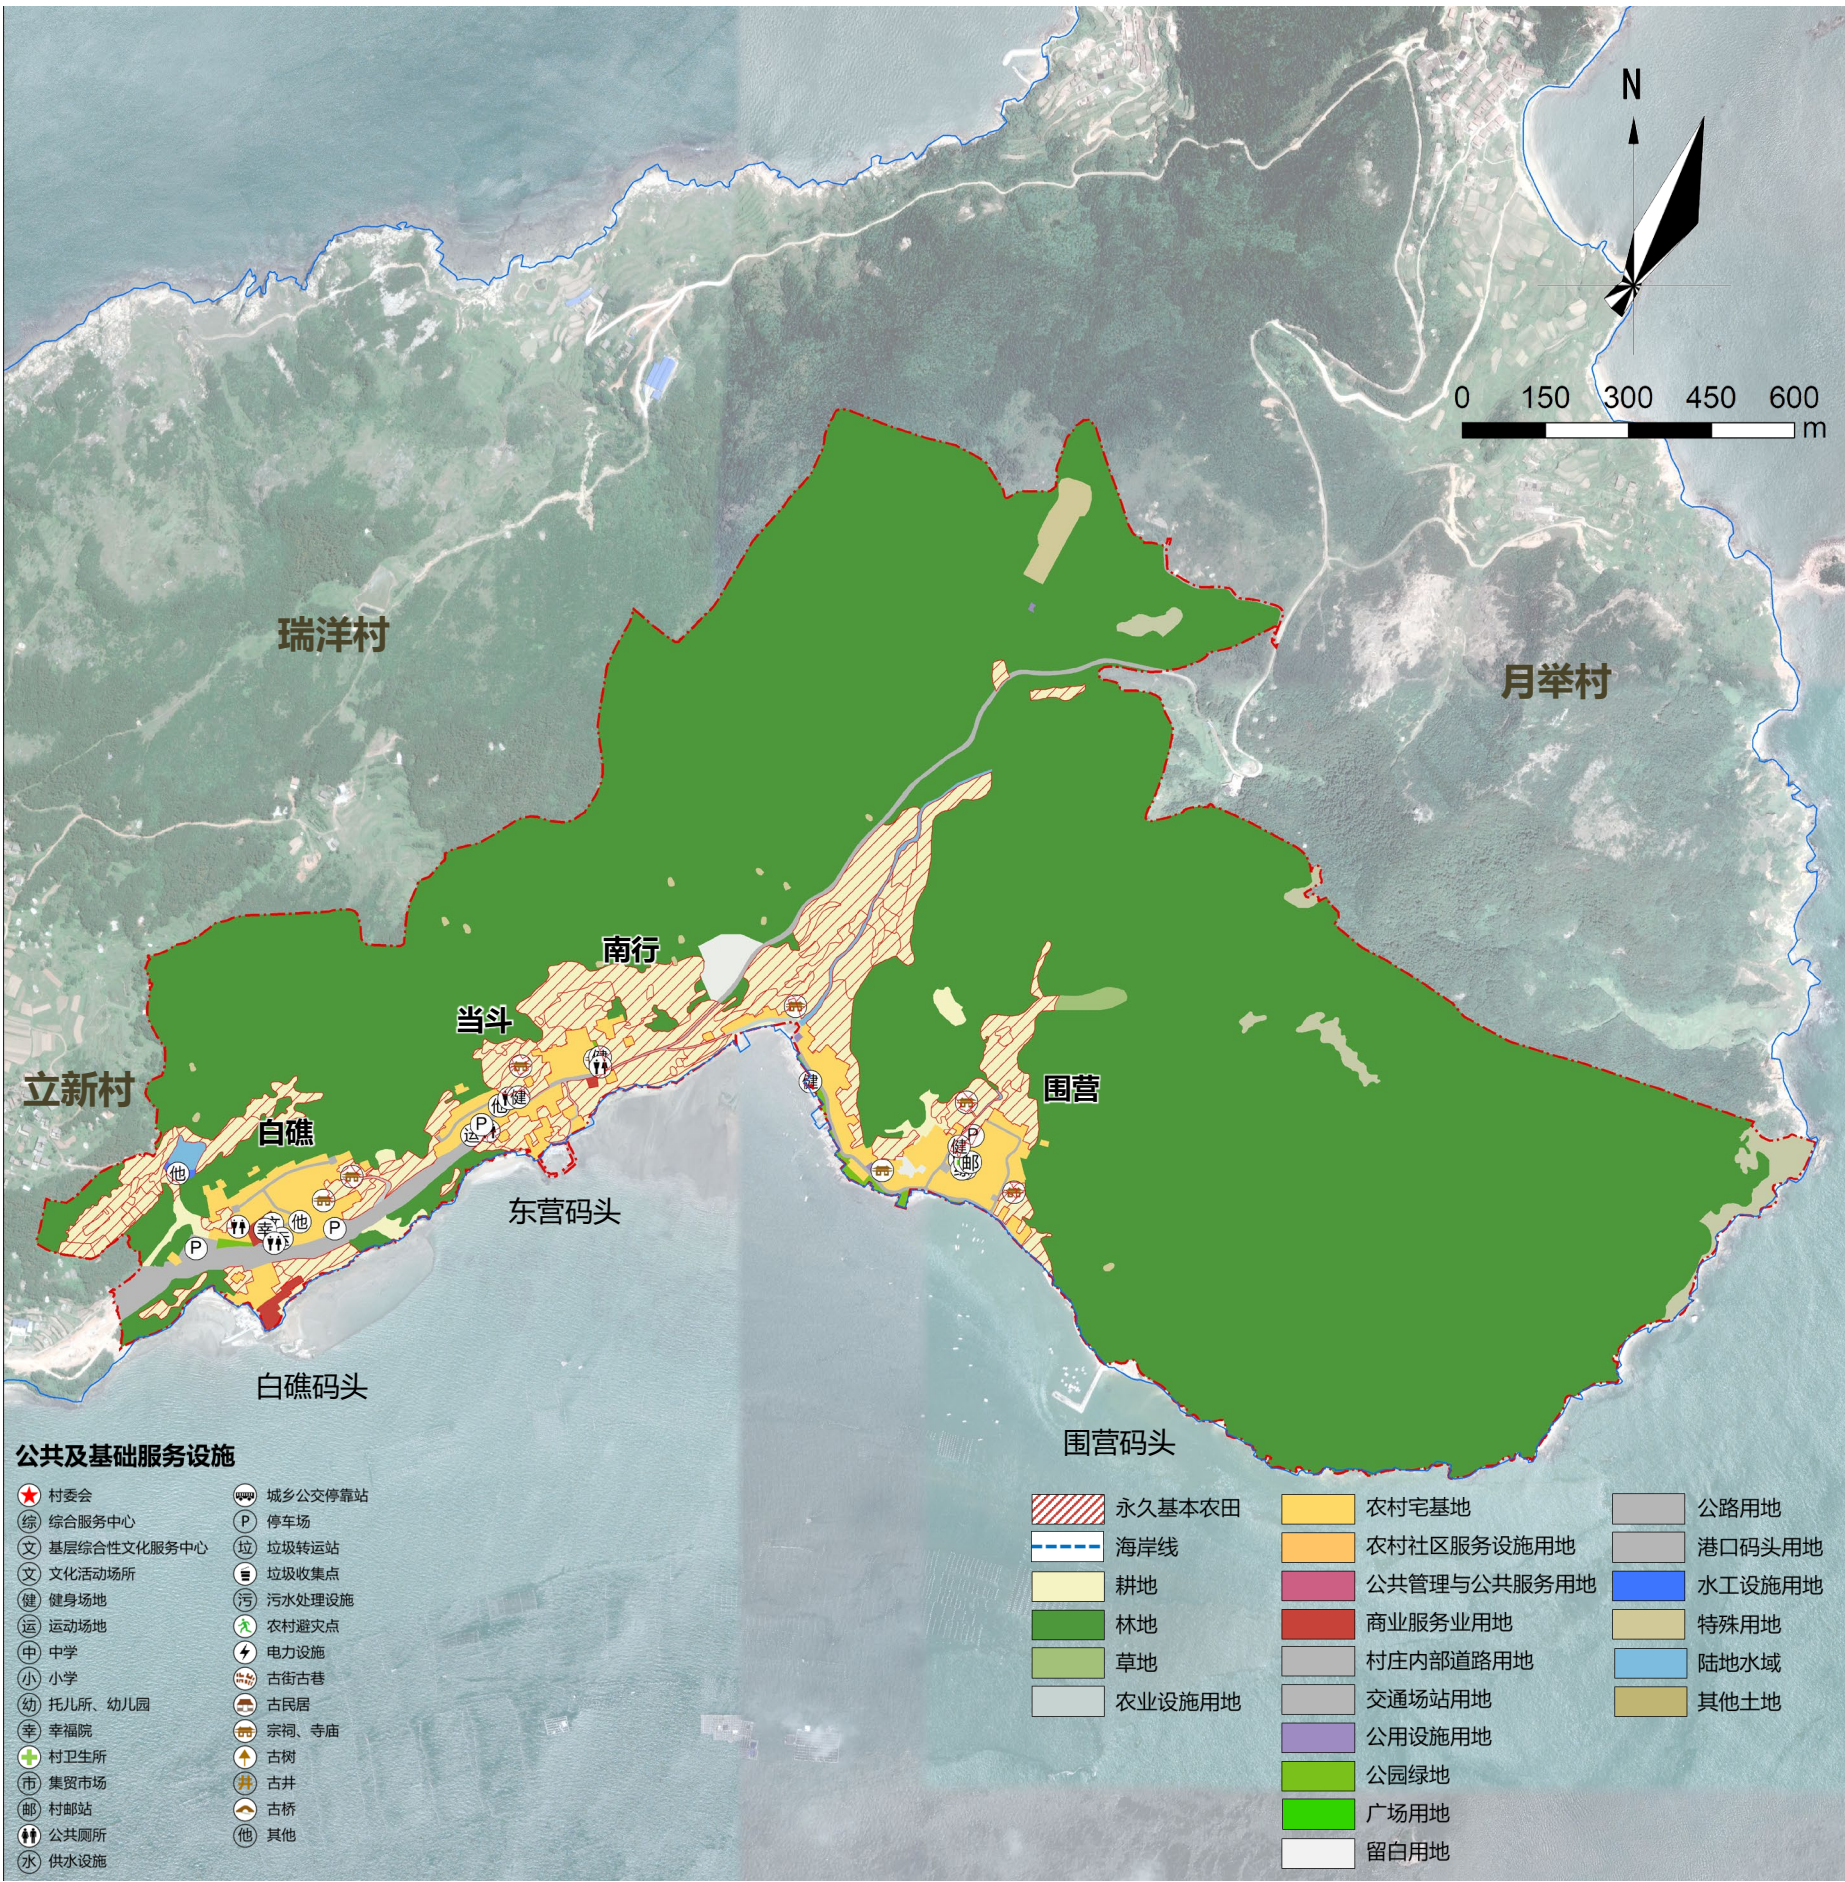

■ 农村居民点总平面布置图



■ 近期实施项目

近期建设项目一览表							
序号	工程类型	项目名称	项目内容和规模	建设年限	投资总额 (万元)	资金来源 (万元)	
1	土地综合整治	村庄耕地和土壤改良	对村庄无灌溉条件，碱解氮和速效钾缺乏，质地过于紧实的耕地进行改良，约10公顷。	2023-2025	15	15	—
2	生态保护与修复	侵蚀海岸线修复	1700米海岸线防护修复工程。	2023-2025	100	100	—
3	绿化美化	环岛路周边景观和建筑整治	对环岛路周边的景观环境进行统一整治。	2023-2025	50	50	—
4	绿化美化	村庄建筑风貌整治	对村庄不协调的建筑进行改造整治。	2023-2025	60	60	—
5	白礁“观海”温泉民宿建设	白礁道路南侧破旧石头厝改建为民宿。	2023-2025	200	—	200	—
6	国营带状观景平台建设	道路南侧带状观景平台建设，约3100㎡。	2023-2025	93	93	—	—
7	休闲餐饮购物一条街	环岛路沿线集中打造休闲餐饮购物一条街。	2023-2025	150	—	150	—
8	产业发展	环岛路旅游观光项目	沿路设置单车和电瓶车租借和休憩驿站。	2023-2025	20	20	—
9	国营山观景台及登山步道项目	国营山观景台建设，同时建设登山步道，约2550㎡。	2023-2025	76.5	76.5	—	—
10	沙滩主题	优质的沙滩打造露营、音乐活动打造沙滩、球类活动等主题活动。	2023-2025	20	—	20	—
11	码头拓展	提供近海观光、远海洋钓等旅游服务，拓展旅游体验项目。	2023-2025	15	—	15	—
12	道路拓宽	环岛路进行拓宽和延伸，道和新建设体系完善，约44800㎡。	2023-2025	896	896	—	—
13	停车场建设	新增三处停车场，约2800㎡。	2023-2025	56	—	56	—
14	沿海步道打造	新建沿海步道	2023-2025	25	25	—	—
合计					1776.5	1335.5	441

