

中华人民共和国一级注册建筑师

福建平潭岚海加油站 鸟瞰图



四川盛创石油天然气工程勘察设计有限公司
Sichuan Shengchuang Oil&Gas Engineering Survey and Design Co.,Ltd

中华人民共和国一级注册建筑师
姓名：魏云峰
注册号：5101070-002
有效期：至2024年6月



四川省建设工程设计出图专用章
四川盛创石油天然气工程勘察设计有限公司
资质等级范围：电力行业(新能源发电)专业乙级；石油天然气(海洋石油)行业
(气田地面、管道输送、油气库)专业乙级；建筑行业(建筑工程)乙级
可承担建筑装饰工程设计、建筑幕墙工程设计、轻型钢结构工程设计、建筑智能化系统设计、照明工程设计和消防设施工程设计相应范围的乙级专项工程设计业务。
资质证书编号：A251010700 有效期至：2025年09月23日



中华人民共和国一级注册建筑师
姓名：魏云峰
注册号：5101070-002
有效期：至2003年6月



平潭综合实验区自然资源与生态环境局
图纸专用章 (1)
随 号有效



中华人民共和国注册建筑师
姓名：魏云峰
注册号：5101070-002
有效期：至2024年6月

四川省建设工程设计出图专用章
四川盛创石油天然气工程勘察设计有限公司
资质等级范围：电力行业（新能源发电）专业乙级；石油天然气（海洋石油）行业
可承担建筑装饰工程设计、建筑幕墙工程设计、轻型钢结构工程设计、建筑智能化系统设计、照明工程设计和
消防设施工程设计相应范围的乙级专项工程设计业务。
资质证书编号：A251010700 有效期至：2025年06月22日



有效期：至2024年6月



资质证书编号：A251010700



中华人民共和国一级注册建筑师
姓名：魏云峰
注册号：5101070-002

四川省建设工程设计出图专用章
四川盛创石油天然气工程勘察设计有限公司
资质等级范围：电力行业（新能源发电）专业乙级；石油天然气（海洋石油）行业
可承担建筑装饰工程设计、建筑幕墙工程设计、轻型钢结构工程设计、建筑智能化系统设计、照明工程设计和消防设施工程设计相应范围的乙级专项工程设计业务。
资质证书编号：A251010700 有效期至：2025年09月23日




 岚海能源 >>

四川省建设工程设计出图专用章



平潭综合实验区自然资源与生态环境局
图纸专用章(1)
号有效

中华人民共和国一级注册建筑师
姓名: 魏云峰
注册号: 5101070-002
有效期至: 2024年6月

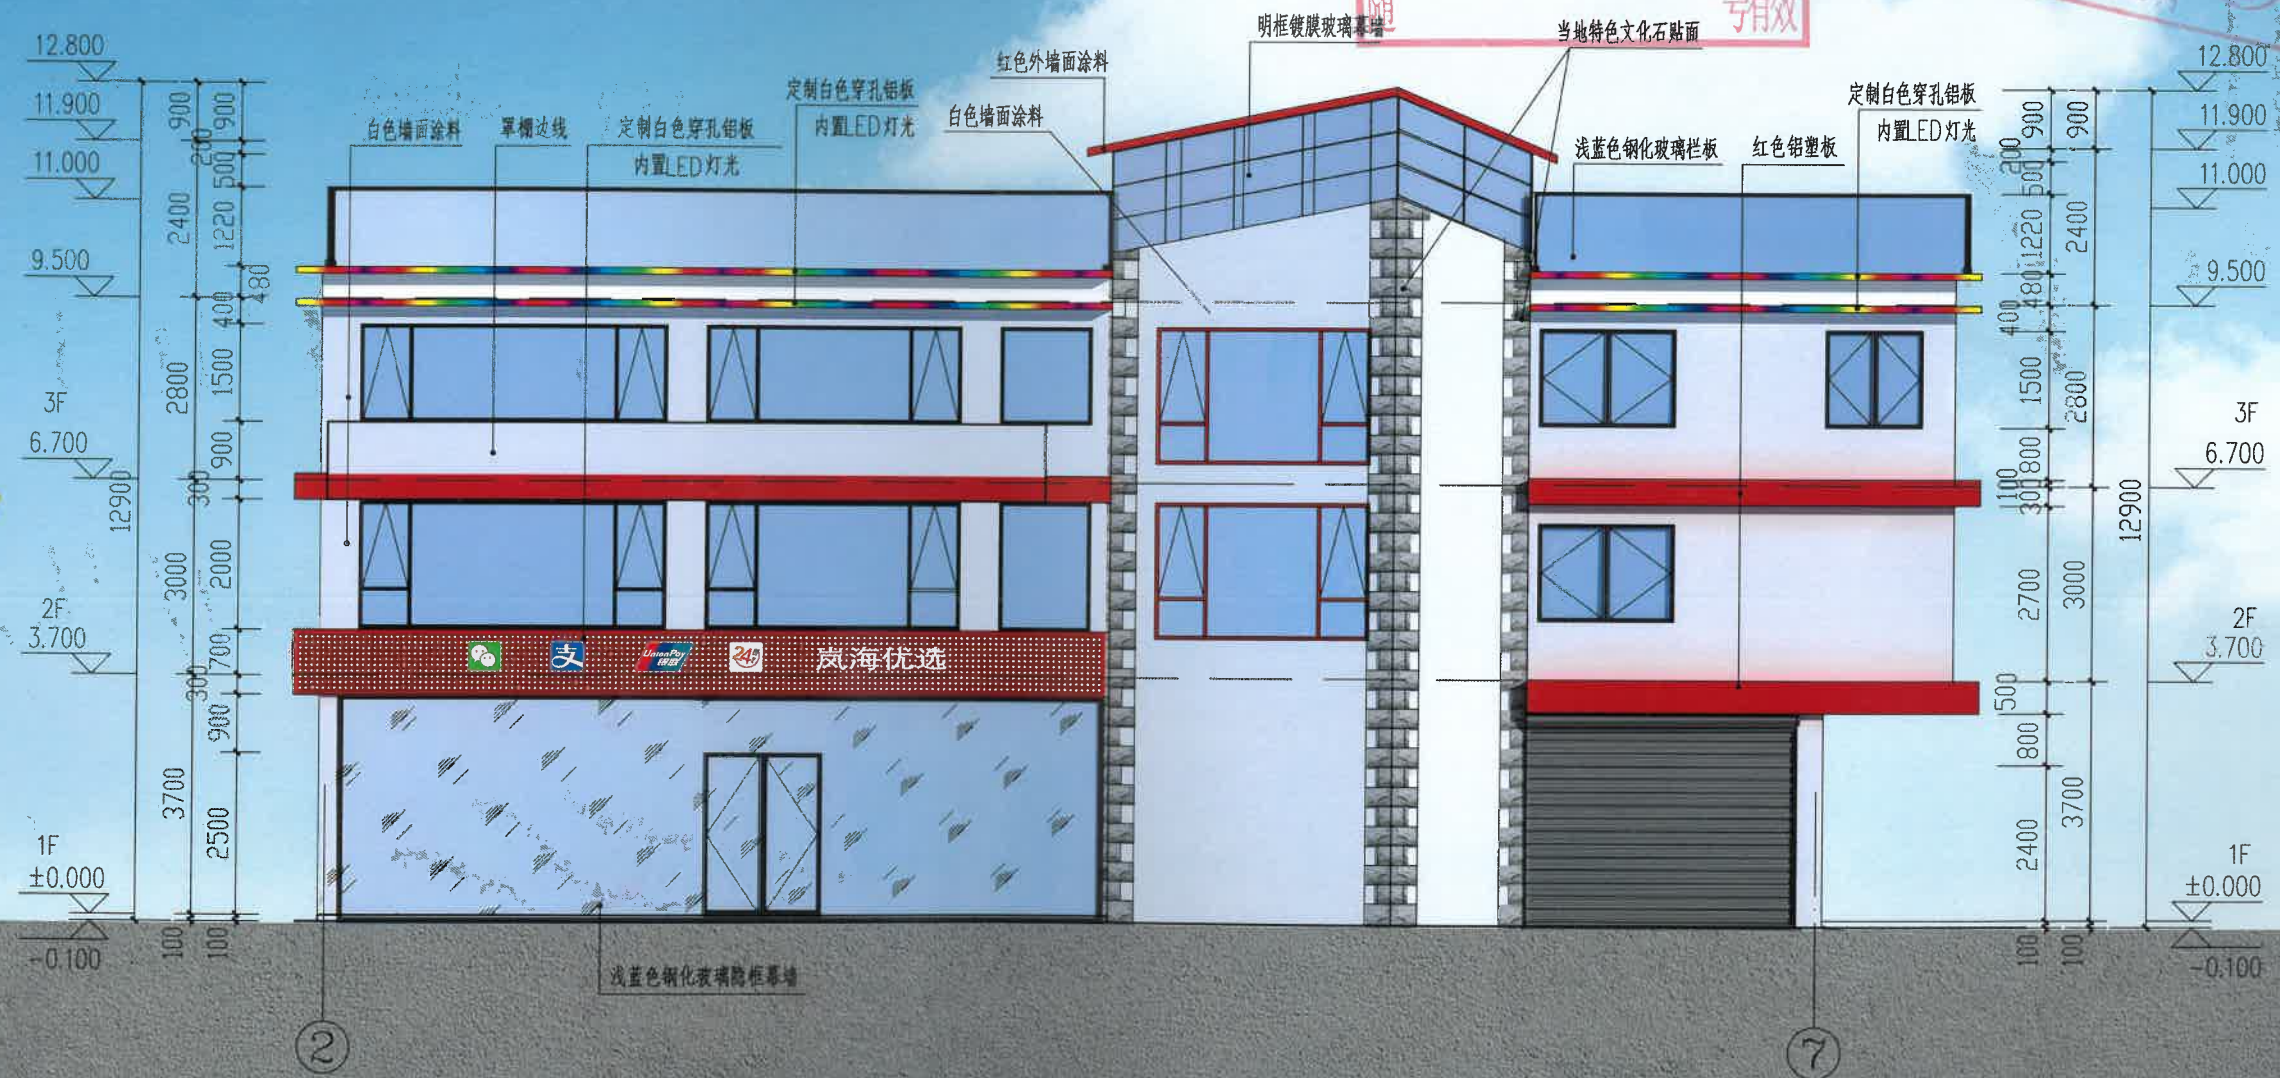


站房②-⑦展开立面图 1:100

四川省建设工程设计出图专用章




中华人民共和国一级注册建筑师
姓名：魏云峰
注册号：5101070-002
有效期：至2024年6月

平潭综合实验区自然资源与生态环境局
图纸专用章(1)
随号有效

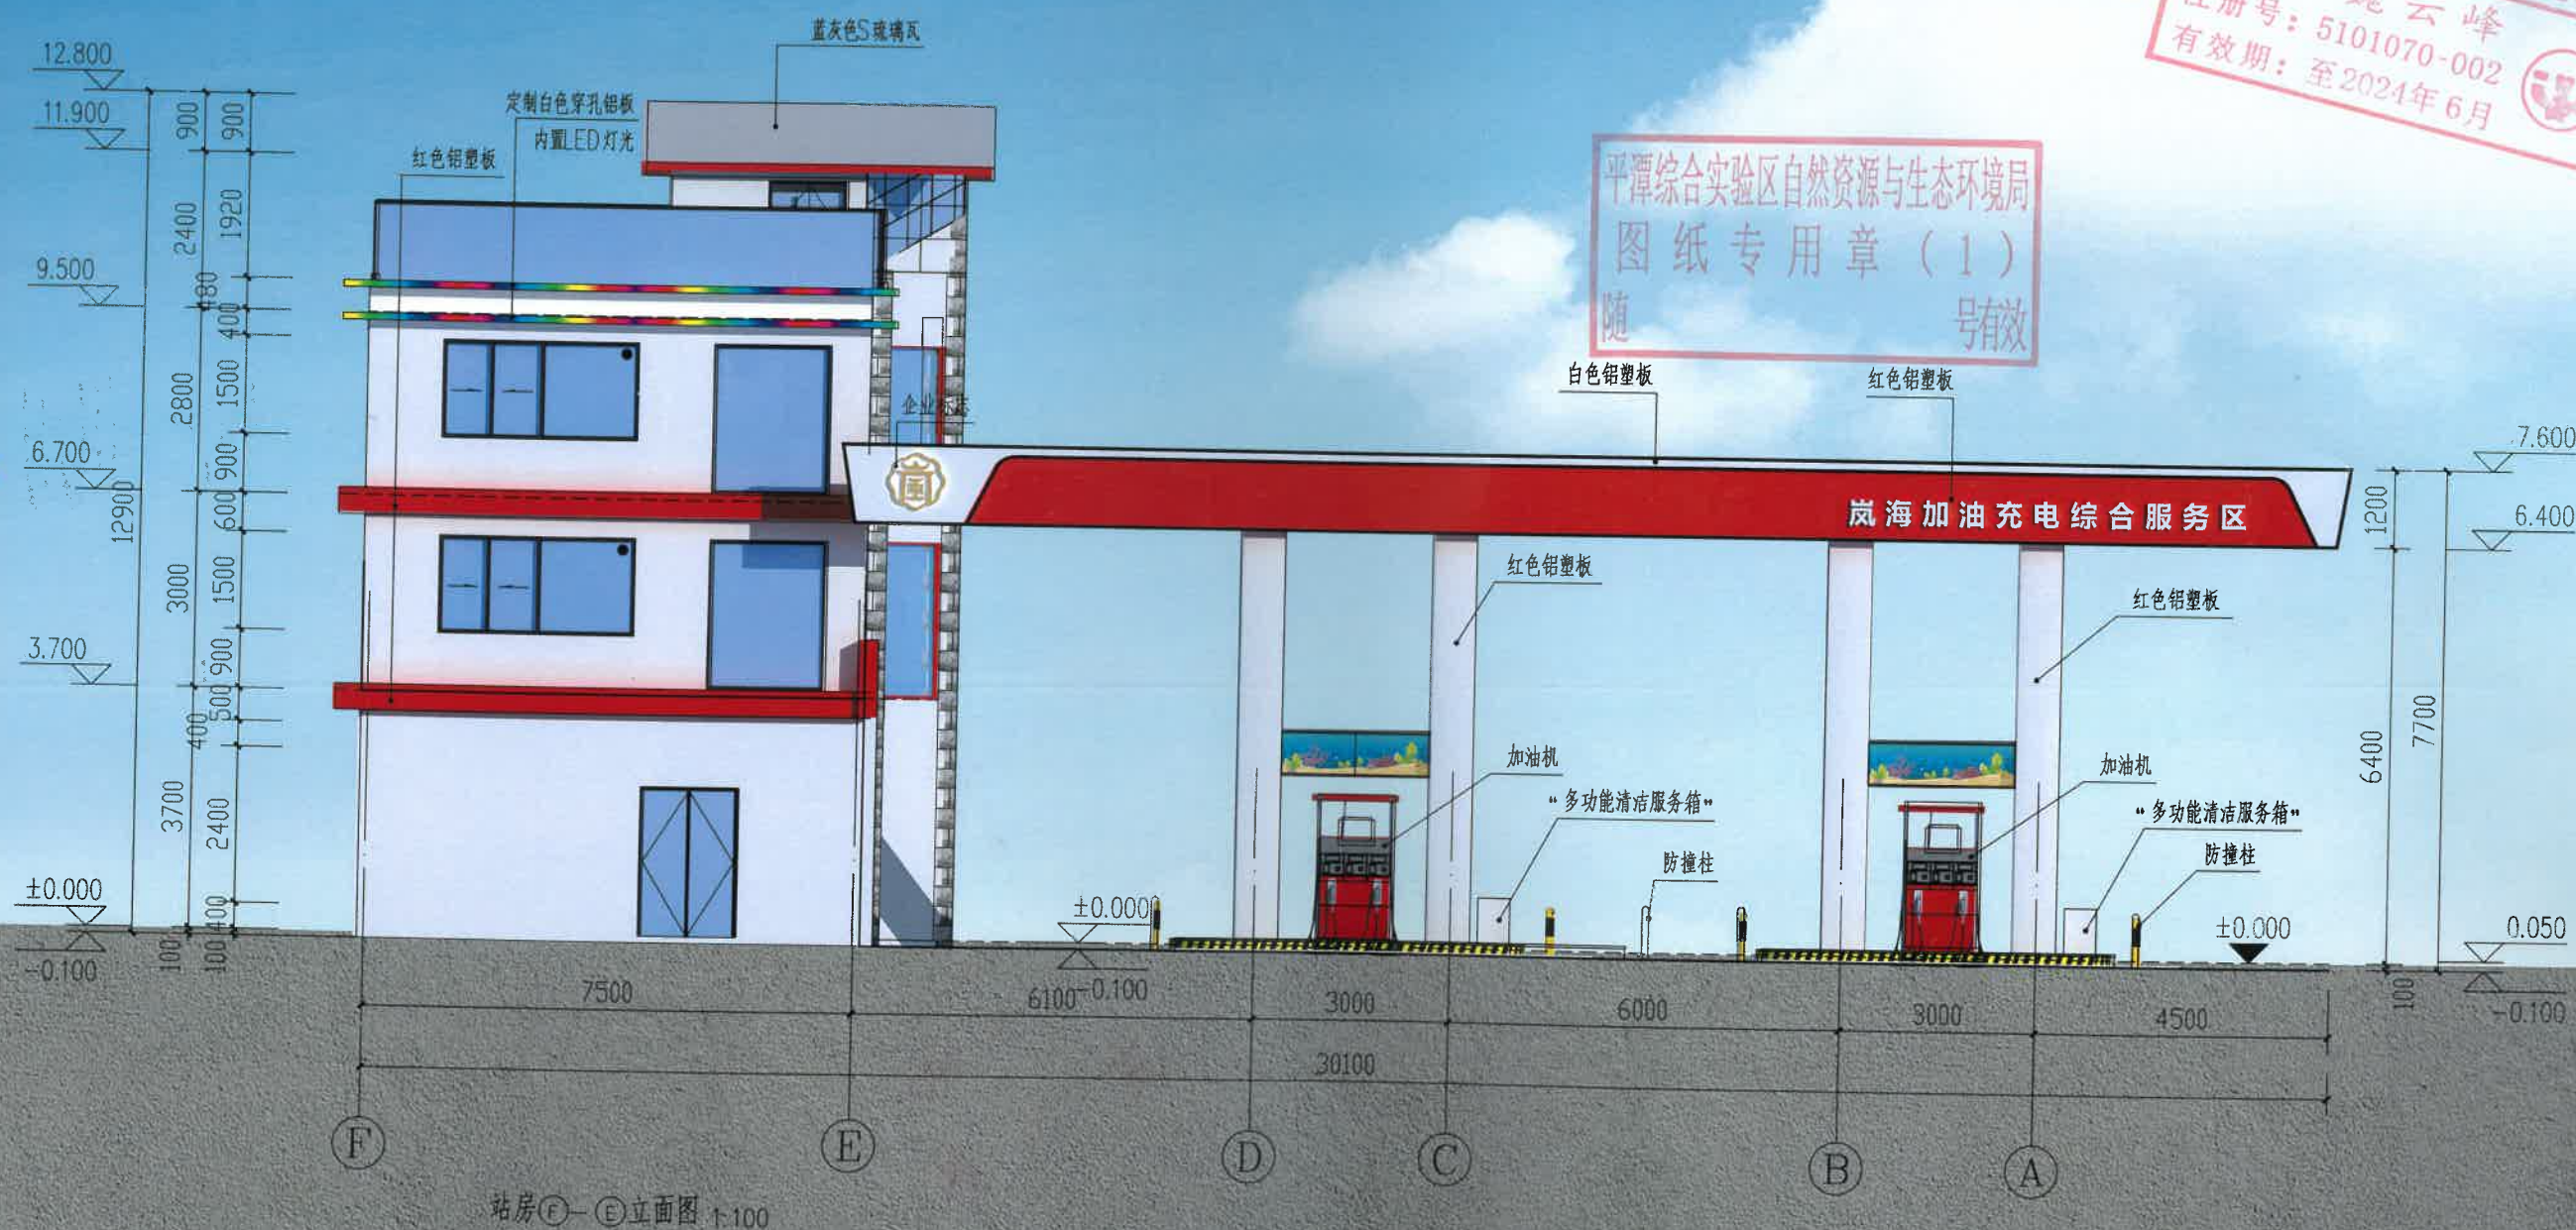

[illegible]

平潭综合实验区自然资源与生态环境
图 纸 专 用 章 (1)
随 蓝灰色S琉璃瓦 号有效

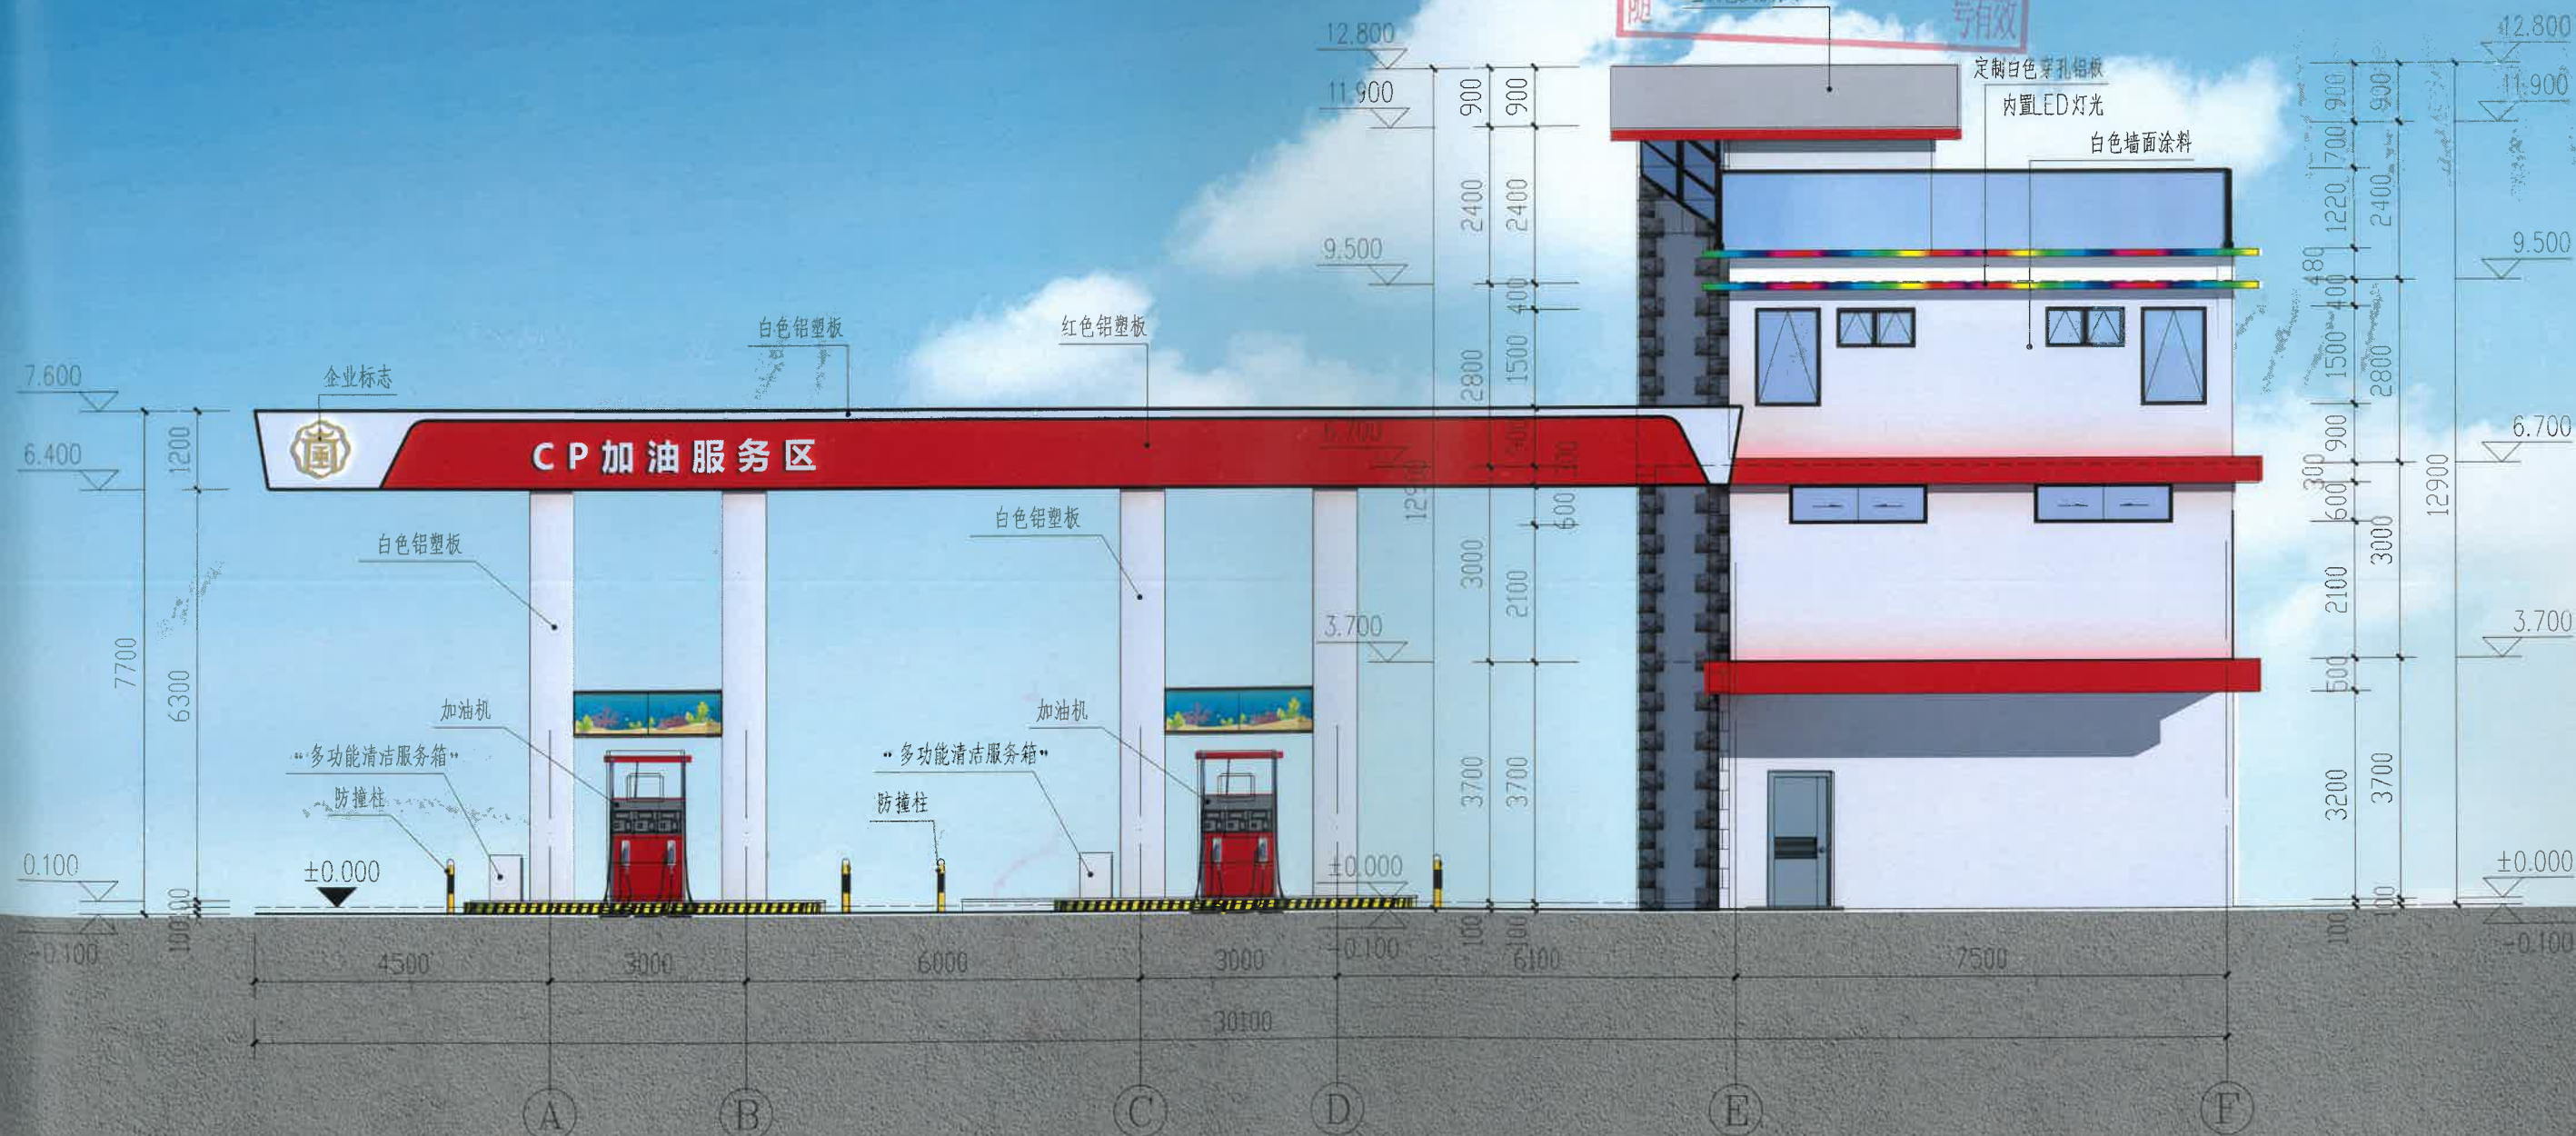

罩棚④—⑤立面图 1:100

站房⑤—⑥立面图 1:100

四川盛创石油天然气工程勘察设计有限公司

蓝灰色S琉璃瓦

窗户玻璃采用易碎玻璃并设置可在室外易于识别的明显标志

定制白色穿孔铝板

内置LED灯光

红色铝塑板

平潭综合实验区自然资源与生态环境局

图 纸 专 用 章 (1)

随 号有效

站房(F) — (E) 立面图 1:100

F

Ⓔ