

162县道至底井孟段村道硬化项目 施工图

 中城恒业设计集团有限公司
2025年7月



资质证书编号: A3520112676

市政行业乙级: 电力行业(变电工程、新能源发电、送电工程)专业乙级; 公路行业(公路)专业丙级; 农林行业(农林综合开发生态工程)专业乙级; 水利行业丙级; 建筑行业乙级; 风景园林工程设计专项乙级; 环境工程(固体废物处理处置工程、水污染防治工程)专项乙级。

[illegible]

日期													
签名													
专业													
日期													
签名													
专业													

一、概述

本项目位于平潭县君山镇中楼村

本工程为现状土路硬化项目，具体详见设计图。

(一) 任务依据

1、相关行业有关法规、规范、规程等。

(二) 设计概况

本道路按照市政性质将现状土坯道路硬化，

道路宽度具体详见设计图。

(三) 采用的主要规范、规程

1、《城市道路工程设计规范》（CJJ37-2012）

2、《城市道路路线设计规范》（CJJ 193-2012）

3、《城镇道路路面设计规范》(CJJ 169-2012)

4、《公路路基设计规范》（JTG D30-2015）

5、《城镇道路工程施工与质量验收规范》（CJJ1-2008）部颁

《公路桥涵地基与基础设计规范》（JTJ024—2007）

6、部颁《公路工程基本建设项目设计文件编制办法》（2015）

7、国标《工程建设标准强制性条文》公路工程部分

二、路基

(一) 一般路基设计

1、路基

本项目现状土路硬化，沿用现状道路路基。

2、路拱横坡

行车道采用1.5%的单向坡。

三、路面

本项目路面为水泥混凝土路面。

(一) 技术标准

行车道采用水泥混凝土路面。水泥路面设计采用以双轮组单轴轴载100KN为标准轴载，双圆

均布垂直荷载作用下的弹性层状连续体系理论进行计算，设计使用年限为20年，交通等级为轻

级。

1、 接缝设计

横向接缝

横向缩缝：采用假缝。

胀缝：项目在平交口处设置胀缝，胀缝宽20mm，。

横向施工缝：宜设在胀缝或缩缝处。


(二) 施工注意事项

1、施工中应严格按照现行的《公路水泥混凝土路面施工技术规范》JTGF30-2003、

《公路路面基层施工技术规范》（JTJ034-2000）等有关规程规范中所规定的施工工艺及质量检查验收标准进行施工。

5未尽事宜请严格参照国家相关法规、规范办理。


中城恒业设计集团有限公司 ZHONGCHENG HENGYE DESIGN GROUP LIMITED 资质证书编号：A352012676	工程名称	162县道至底井孟段村道硬化项目	项目负责人	王敏文	设计	陈奇	图名	总说明		建设单位	平潭县君山镇中楼村村民委员会	
	单项名称		专业负责人	张云堂	审核	张云堂	复核	程刚	日期		图号	DL-01

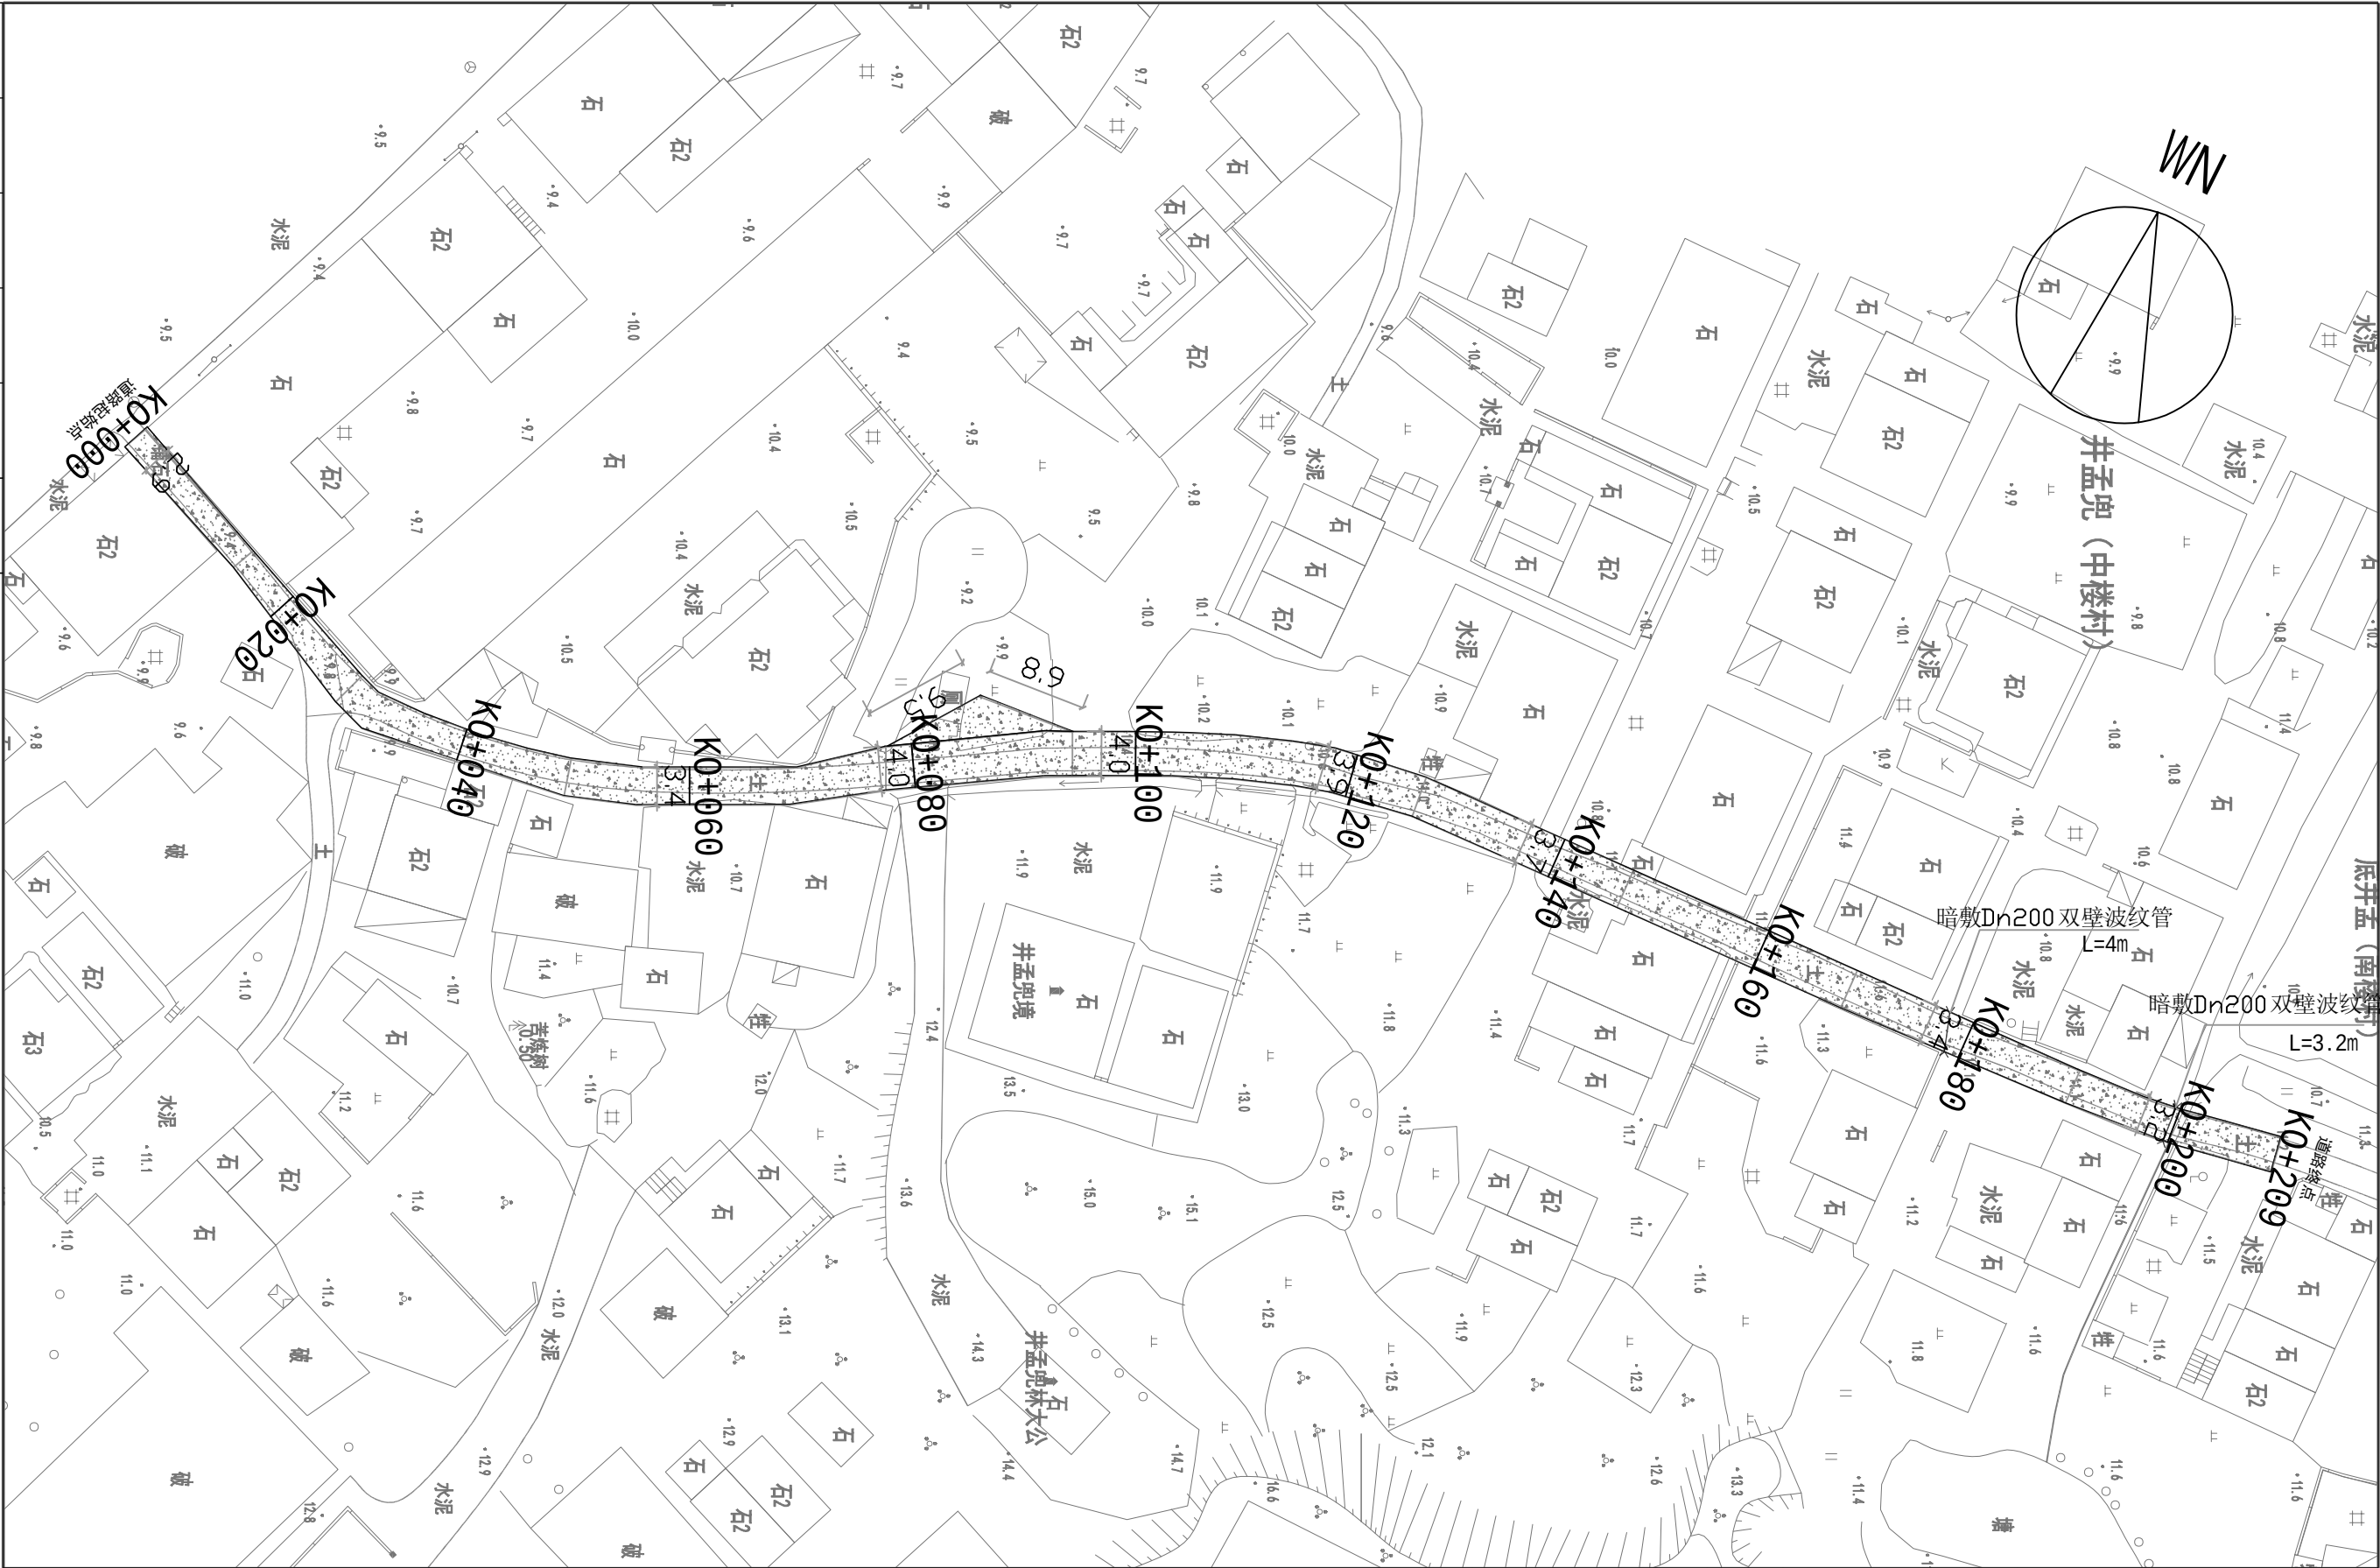

中城恒业设计集团有限公司 ZHONGCHENG HENGYE DESIGN GROUP LIMITED 资质证书编号: A352012676	工程名称	162县道至底井孟段村道硬化项目	项目负责人	王敏上	设计	王敏上	图名	总平面图		建设单位	平潭县君山镇中楼村村民委员会	
	单项名称		专业负责人	王敏上	审核	王敏上	复核	程刚	日期		图号	DL-02

设计	审核	审核	审核	审核	审核
日期	日期	日期	日期	日期	日期

图	
名	
号	
图	
名	
号	

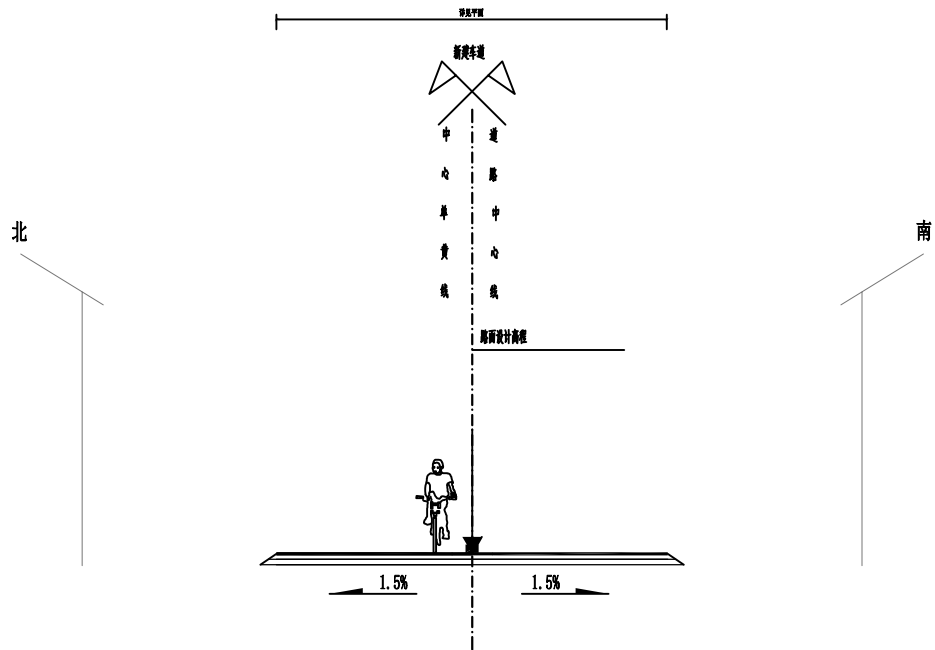


旧路环境提升标准横断面设计图



中城恒业设计集团有限公司 ZHONGCHENG HENGYE DESIGN GROUP LIMITED 资质等级: 甲级	工程名称	162县道至底井孟段村道硬化项目	项目负责人	王斌文	设计	陈博	图名	道路标横断面图		建设单位	平潭县崑山镇中樓村村民委员会	
	单项名称		专业负责人	陈博	审核	陈博	复核	程刚	日期		图号	DL-03

图例	
说明	
备注	
图例	
说明	
备注	

路面类型		水泥混凝土路面		
路面结构		土路		
路面厚度		少地注意		
图例	面层	K0+000~K0+005水泥混凝土路面	水泥混凝土路面	K0+120~K0+140水泥混凝土路面
	基层	15cm厚C25混凝土 基层厚度不小于15cm	15cm厚C25混凝土 基层厚度不小于15cm	15cm厚C25混凝土 基层厚度不小于15cm 20cm厚2.5%水泥砂浆找平层 厚度不小于15cm
备注				

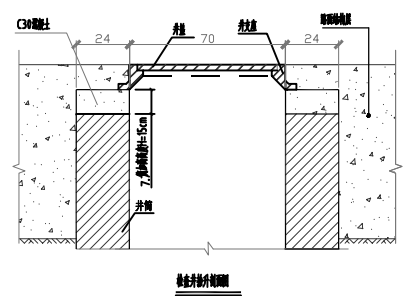


- 备注
1. 本图仅供参考，具体施工时应根据实际情况进行设计，并经审批后方可施工。
 2. 本图仅供参考，具体施工时应根据实际情况进行设计，并经审批后方可施工。
 3. 本图仅供参考，具体施工时应根据实际情况进行设计，并经审批后方可施工。

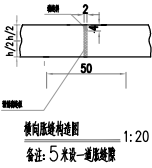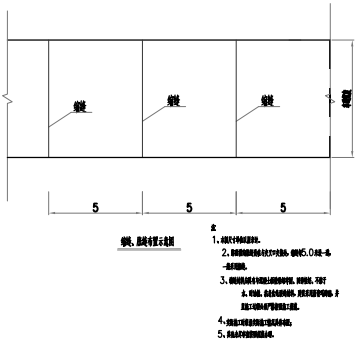

中城恒业设计集团有限公司 ZHONGCHENG HENGYE DESIGN GROUP LIMITED 资质等级：甲级 13011301	工程名称	162县道至底井孟段村道硬化项目	项目负责人	王斌立	设计	陈静	图名	道路做法详图	建设单位	平潭县崑山镇中樓村村委会
	单项名称		专业负责人	王斌立	审核	王斌立	复核	王斌立	日期	图号 DL-04

日期	
姓名	
专业	
日期	
姓名	
专业	

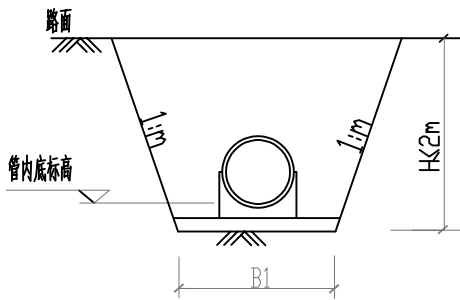


单槽开挖断面

挖槽放坡(m值)

h或H(M)		$h \leq 1$	$1 < h \leq 2$	$2 < h \leq 3$	$3 < h \leq 4$
m	无淤泥时	0.2	0.2	0.2	0.2
	有淤泥时	0.3	0.33	0.4	0.5

原地面

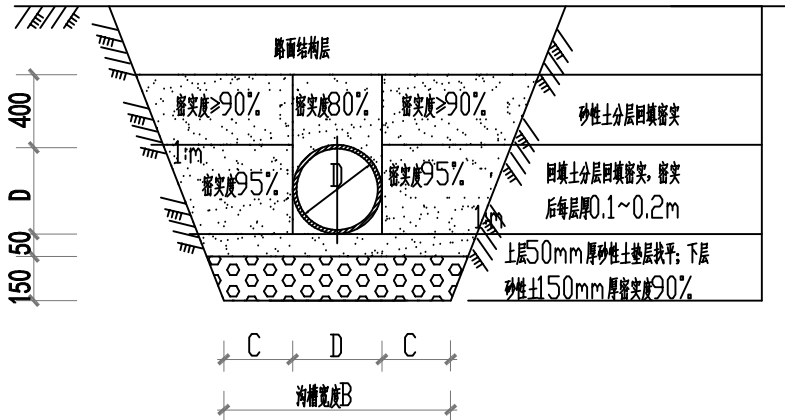

排水管道基础图

① 双壁波纹管 $\phi 200$, 埋深小于2.5米

说明

1. 本图尺寸单位为毫米。
2. 管道基础中碎石粒径为 $5 \sim 40\text{mm}$ 。管道基础碎石垫层上铺 50mm 中粗砂层找平。
3. 管道与检查井的连接采用短管，管道承口应落在检查井的进水方向，插口应落在检查井的出水方向。
4. 管道开挖放坡、支撑方式依据现场土质情况和开挖深度按《给水排水管道工程施工及验收规范》要求实施。
5. 管道基础为淤泥时，若淤泥层 $< 80\text{cm}$ ，可将淤泥层清除，用块石替换，然后在块石上用碎石垫层 30cm 。

作为管道基础处理；若淤泥层较厚，采用块石替换，块石替换厚度按 80cm 考虑，实际发生工程量实际
发生工程量由现场确定，并由监理确认。确保管道基础稳定。发生工程量由现场确定，并由监理确认。确保管道基础稳定。

中城恒业设计集团有限公司 ZHONGCHENG HENGYE DESIGN GROUP LIMITED 资质等级: 甲级	工程名称	162县道至底井孟段村道硬化项目	项目负责人	王斌文	设计	陈静	图名	排水做法详图		建设单位	平潭县碧山镇中楼村村民委员会	
	单项名称		专业负责人	王斌文	审核	王斌文	复核	王斌文	日期		图号	DL-05