

后池路东段（翠园北路至038乡道段）
水泥路面浇筑沥青路面项目
施工图



中科经纬
ZHONGKE JINGWEI

中华人民共和国建设工程设计证书
行业乙级 A251034247

会 签 栏		暖通
	电气	
	给排水	
	结构	
		建筑

图纸目录									
子项		专业	建筑	版本号	A	总张数		日期	
序号	图纸名称						图号	图 幅	
00	图纸目录						00	A3	
01	施工范围影像示意图						01	A3	
02	现状总平面图一						02	A3	
03	现状总平面图二						03	A3	
04	改造后总平面图一						04	A3	
05	改造后总平面图二						05	A3	
06	建筑设计说明						06	A3	
07	大样详图1						07	A3	
08	大样详图2						08	A3	
09	大样详图3						09	A3	
10							10	A3	
11							11	A3	
12							12	A3	
13							13	A3	
14							14	A3	
15							15	A3	
16							16	A3	



中科经纬

ZHONGKE JINGWEI


中华人民共和国建设部工程设计证书

建筑行业乙级 A251034247

地址:中国·成都·成都市青羊区敬业路218号15栋1楼1号
电话: 028-67775960 网址: www.zkjwgc.js.com
传真: 028-67775920 E-mail: zkjwgc.js@163.com 邮编: 610041

注 册 执 业 章 REGISTERED PRACTICE SIGNET			
姓 名 NAME		明 侨	
注册印章号 REGISTERED SIGNET NO.		5100235-006	
注册证书号 REGISTERED CERTIFICATE NO.		20215102475	
设计总负责人 PROJECT LEADER	明 侨	明 侨	
专业负责人 DIVISION CHIEF	陈丽	陈丽	
设 计 DESIGNED BY	林亮	林亮	
校 对 PROCESSED BY	陈丽	陈丽	
审 核 CHECHED BY	明 侨	明 侨	
审 定 APPROVED BY	明 侨	明 侨	
设计单位 DESIGNER			
中科经纬工程技术有限公司			
建设单位 CLIENT			
平潭君山镇松南村村民委员会			
工程名称 PROJECT			
后池路东段（翠园北路至038乡道段） 水泥路面浇筑沥青路面项目			
图 名 TITLE			
图纸目录			
设计号 PROJECT NO.			
图 别 DWG TYPE	建施	图 号 DWG TYPE	00
版本号 Ver.	A	日 期 DATE	
所有设计图以最新版本为有效版本			
本图若未盖本单位出图章则无效			

会 签 栏				
暖通		电气		给排水
结构		建筑		

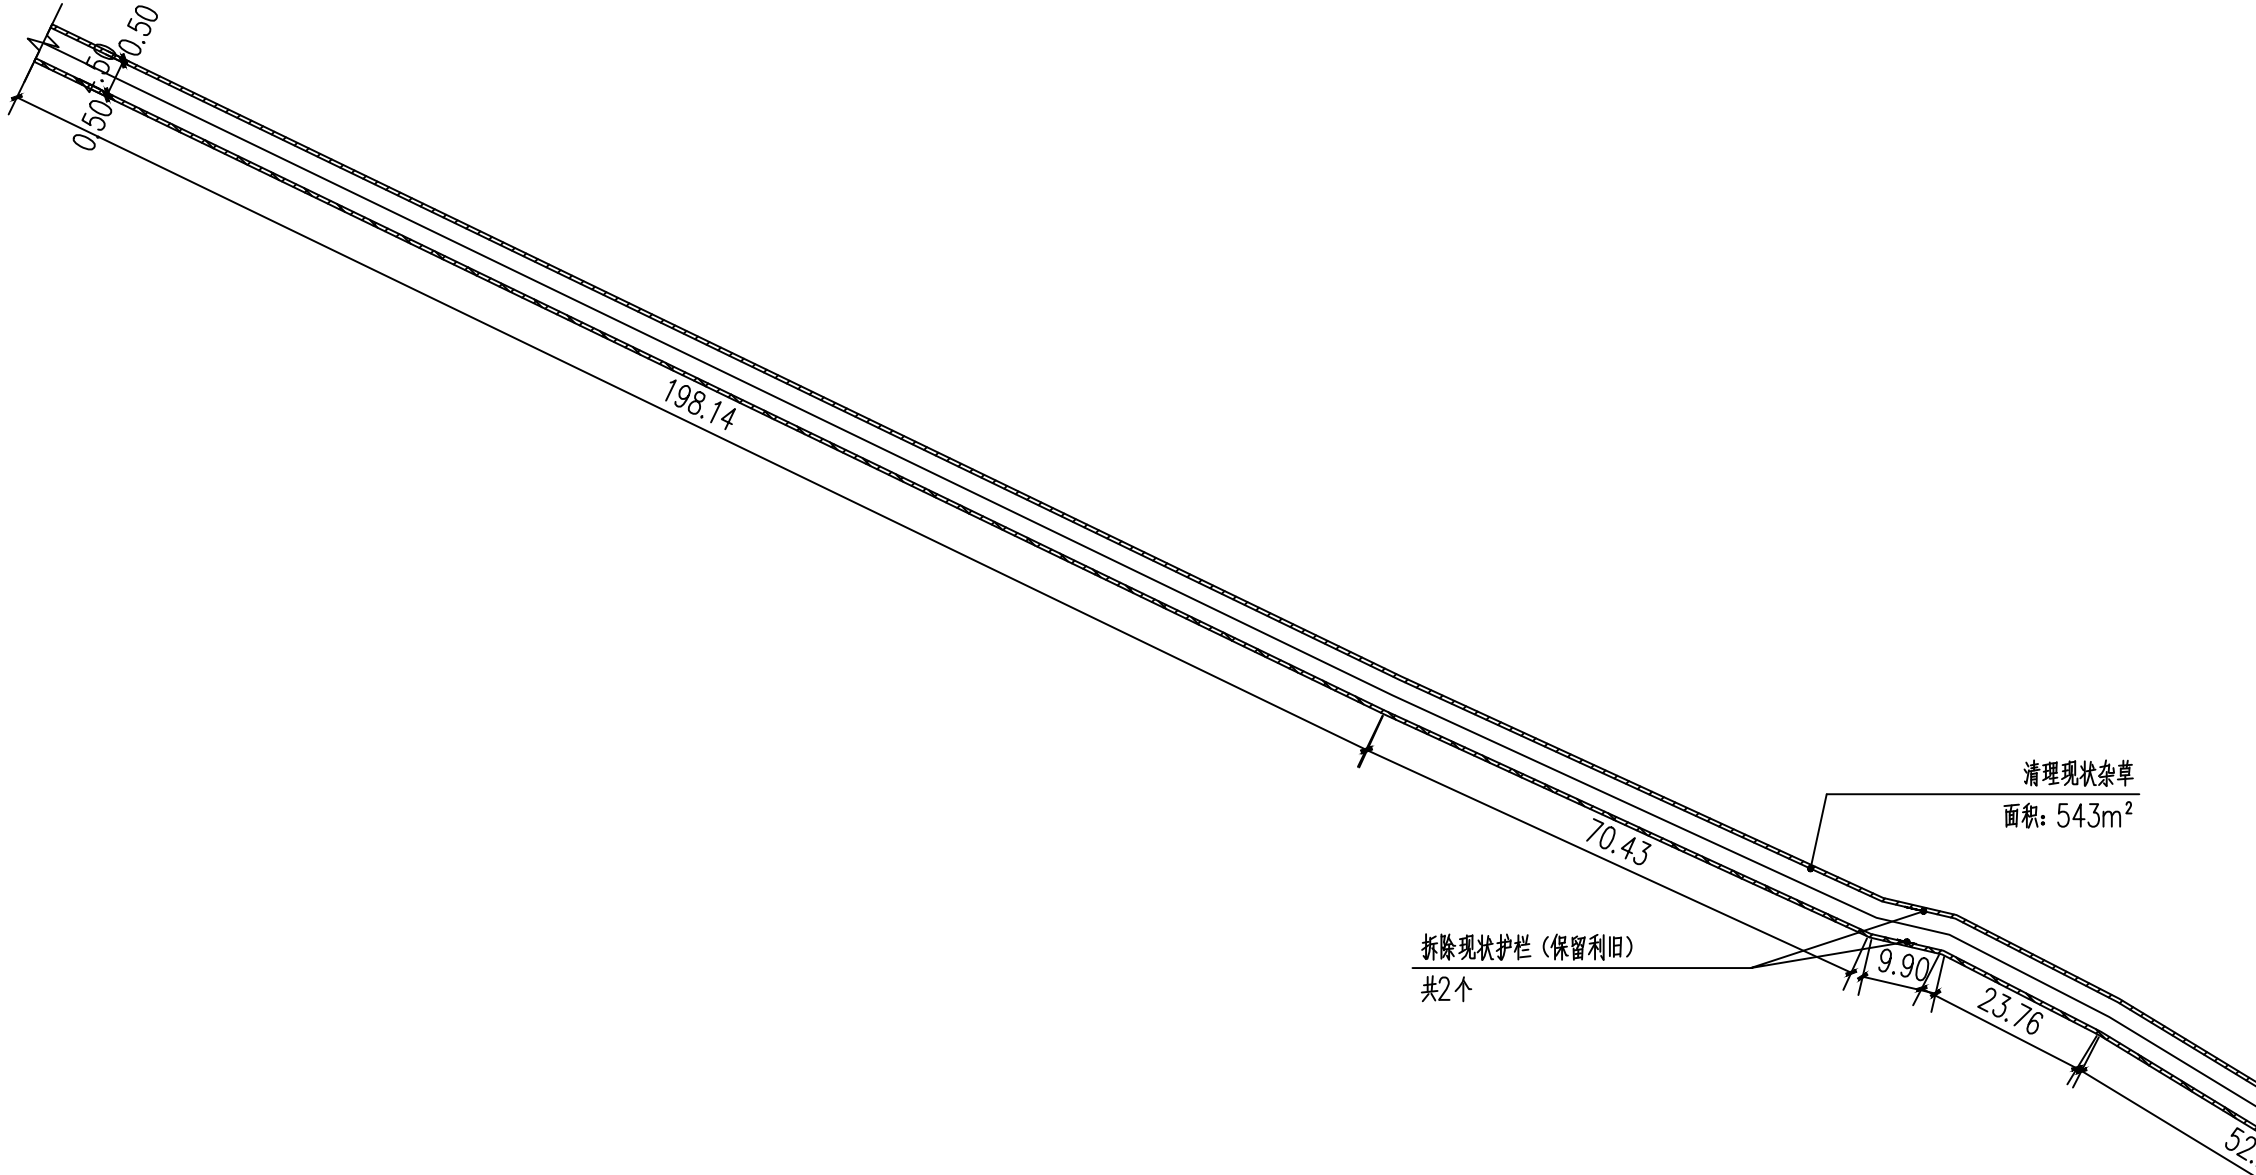

现状总平面图一

注: 1.本图尺寸单位为“m”
2.现状路段宽度4.5米,长度54.4米



中科经纬


ZHONGKE JINGWEI

中华人民共和国建设部工程设计证书
建筑行业乙级 A251034247

地址:中国·成都·成都市青羊区敬业路218号15栋1楼1号
电话: 028-67775960 网址: www.zkjwgcjs.com
传真: 028-67775920 E-mail: zkjwgcjs@163.com 邮编: 610041

注册执业章 REGISTERED PRACTICE SIGNET			
姓名 NAME		明 桥	
注册印章号 REGISTERED SIGNET NO.		5100235-006	
注册证书号 REGISTERED CERTIFICATE NO.		20215102475	
设计总负责人 PROJECT LEADER	明 桥	明 桥	
专业负责人 DIVISION CHIEF	陈丽	陈丽	
设 计 DESIGNED BY	林亮	林亮	
校 对 PROCESSED BY	陈丽	陈丽	
审 核 CHECKED BY	明 桥	明 桥	
审 定 APPROVED BY	明 桥	明 桥	
设计单位 DESIGNER			
中科经纬工程技术有限公司			
建设单位 CLIENT			
平潭君山镇松南村村民委员会			
工程名称 PROJECT			
后池路东段（翠园北路至038乡道段） 水泥路面浇筑沥青路面项目			
图 名 TITLE			
现状总平面图一			
设计号 PROJECT NO.			
图 别 DWG TYPE	建施	图 号 DWG TYPE	02
版本号 Ver.	A	日 期 DATE	
所有设计图以最新版本为有效版本			
本图若未盖本单位出图章则无效			

会 签 栏	
	暖通
	电气
	给排水
	结构
	建筑

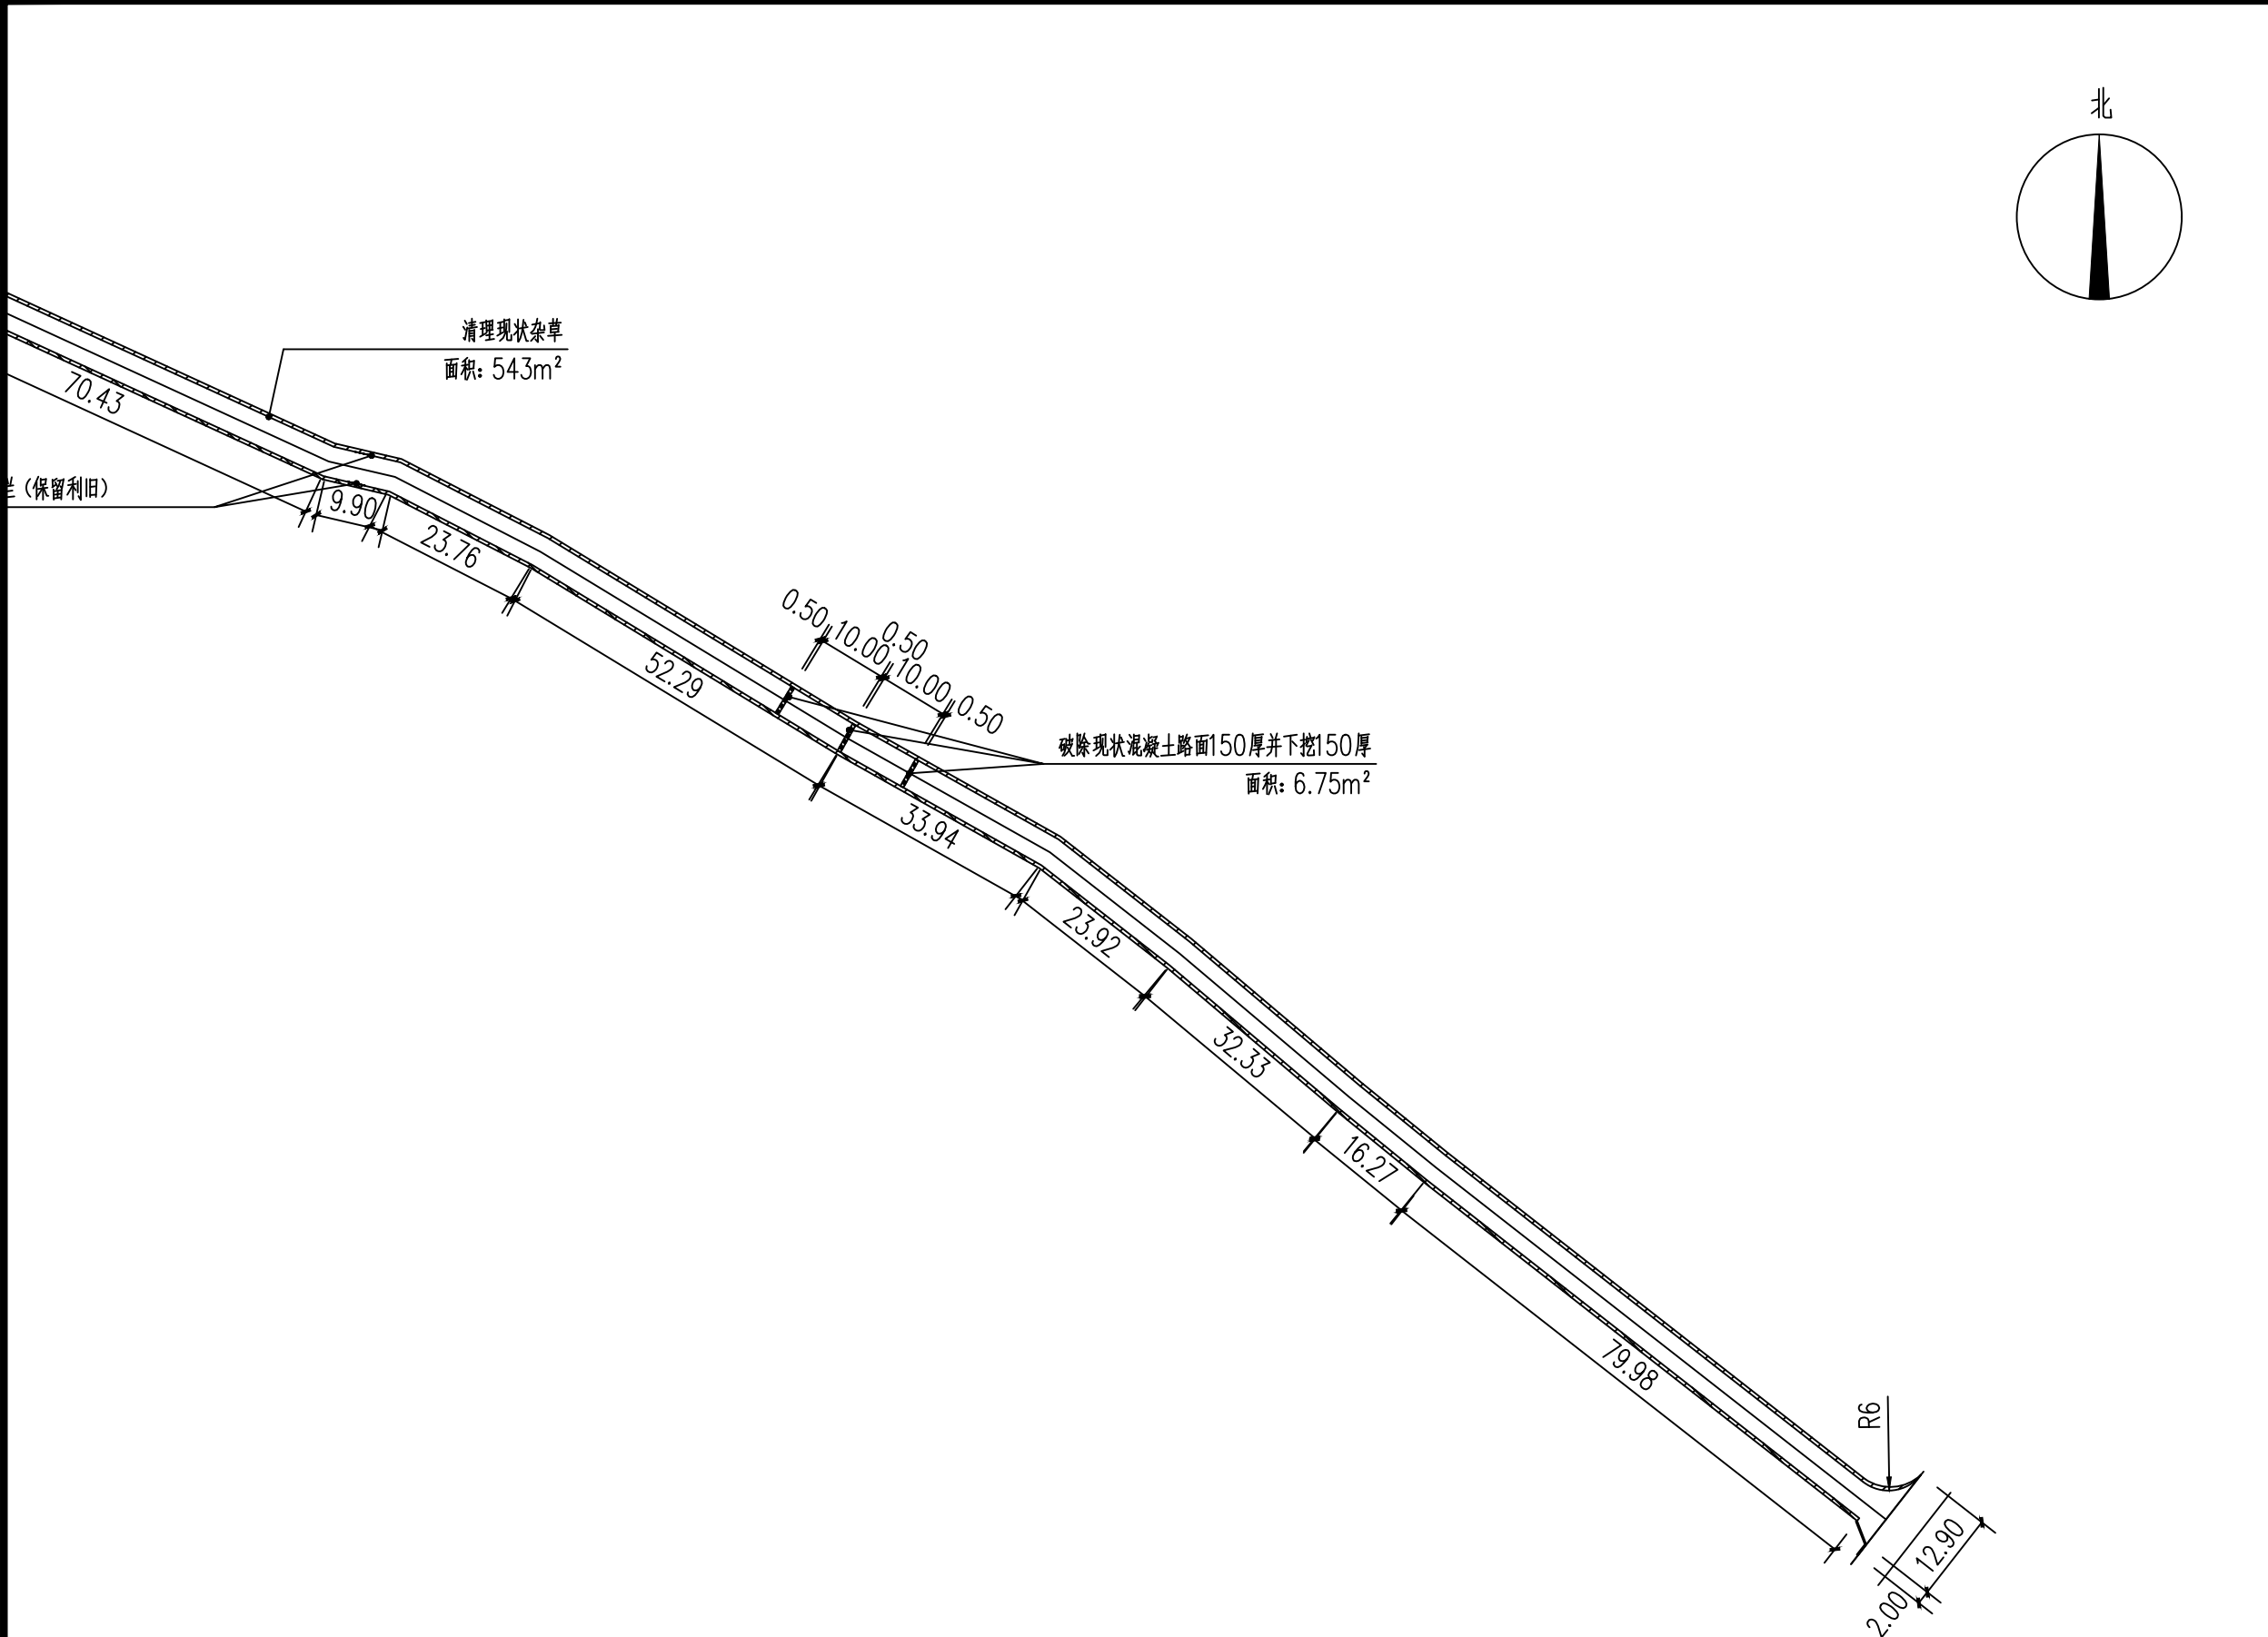

现状总平面图二

注：1.本图尺寸单位为“m”
2.现状路段宽度4.5米，长度544米



中科经纬


ZHONGKE JINGWEI

中华人民共和国建设部工程设计证书
建筑行业乙级 A251034247

地址:中国·成都·成都市青羊区敬业路218号15栋1楼1号
电话: 028-67775960 网址: www.zkjwgcjs.com
传真: 028-67775920 E-mail: zkjwgcjs@163.com 邮编: 610041

注册执业章 REGISTERED PRACTICE SIGNET			
姓名 NAME	明 桥		
注册印章号 REGISTERED SIGNET NO.	5100235-006		
注册证书号 REGISTERED CERTIFICATE NO.	20215102475		
设计总负责人 PROJECT LEADER	明 桥	明 桥	
专业负责人 DIVISION CHIEF	陈丽	陈丽	
设计 DESIGNED BY	林亮	林亮	
校对 PROCESSED BY	陈丽	陈丽	
审核 CHECKED BY	明 桥	明 桥	
审定 APPROVED BY	明 桥	明 桥	
设计单位 DESIGNER			
中科经纬工程技术有限公司			
建设单位 CLIENT			
平潭君山镇松南村村民委员会			
工程名称 PROJECT			
后池路东段（翠园北路至038乡道段） 水泥路面浇筑沥青路面项目			
图 名 TITLE			
现状总平面图二			
设计号 PROJECT NO.			
图 别 DWG TYPE	建施	图 号 DWG TYPE	03
版本号 Ver.	A	日 期 DATE	
所有设计图以最新版本为有效版本			
本图若未盖本单位出图章则无效			

会 签 栏		暖通
电气	给排水	
结构		
建筑		

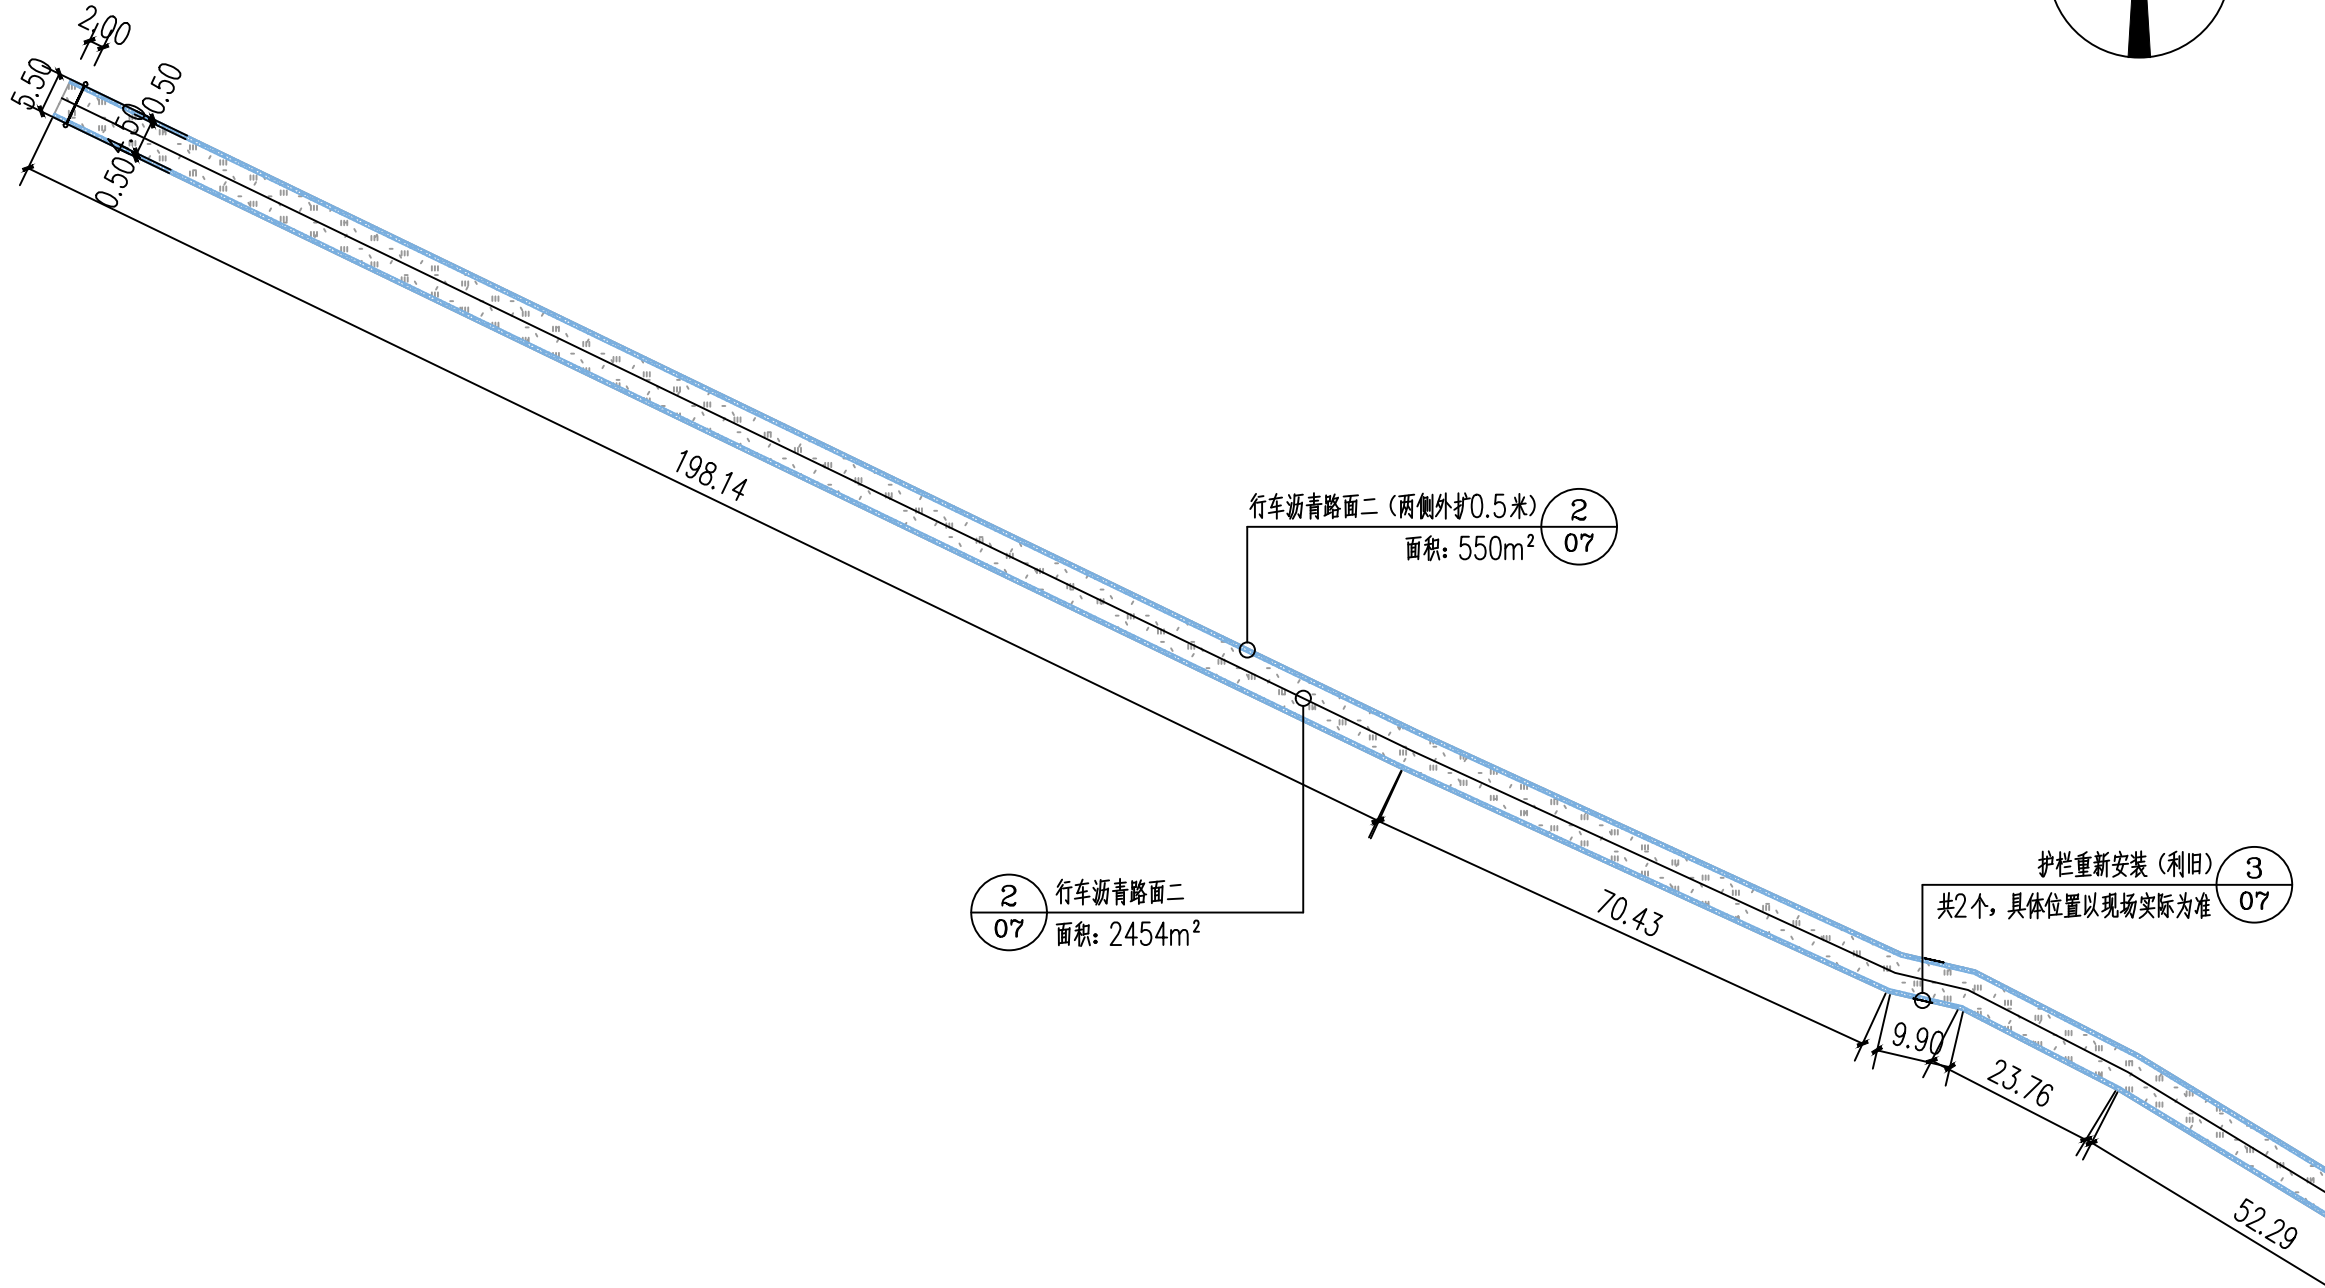

改造后总平面图一

注: 1.本图尺寸单位为“m”
2.改造后路段宽度5.5米, 长度544米




中科经纬
ZHONGKE JINGWEI

中华人民共和国建设部工程设计证书
建筑行业乙级 A251034247

地址: 中国·成都·成都市青羊区敬业路218号15栋1楼1号
电话: 028-67775960 网址: www.zkjwgcjs.com
传真: 028-67775920 E-mail: zkjwgcjs@163.com 邮编: 610041

注册 执 业 章 REGISTERED PRACTICE SIGNET			
姓 名 NAME		明 桥	
注册印章号 REGISTERED SIGNET NO.		5100235-006	
注册证书号 REGISTERED CERTIFICATE NO.		20215102475	
设计总负责人 PROJECT LEADER	明 桥	明 桥	
专业负责人 DIVISION CHIEF	陈丽	陈丽	
设 计 DESIGNED BY	林亮	林亮	
校 对 PROCESSED BY	陈丽	陈丽	
审 核 CHECKED BY	明 桥	明 桥	
审 定 APPROVED BY	明 桥	明 桥	
设计单位 DESIGNER			
中科经纬工程技术有限公司			
建设单位 CLIENT			
平潭君山镇松南村村民委员会			
工程名称 PROJECT			
后池路东段（翠园北路至038乡道段） 水泥路面浇筑沥青路面项目			
图 名 TITLE			
改造后总平面图一			
设计号 PROJECT NO.			
图 别 DWG TYPE	建施	图 号 DWG TYPE	04
版本号 Ver.	A	日 期 DATE	
所有设计图以最新版本为有效版本			


暖通
电气
给排水
结构
建筑

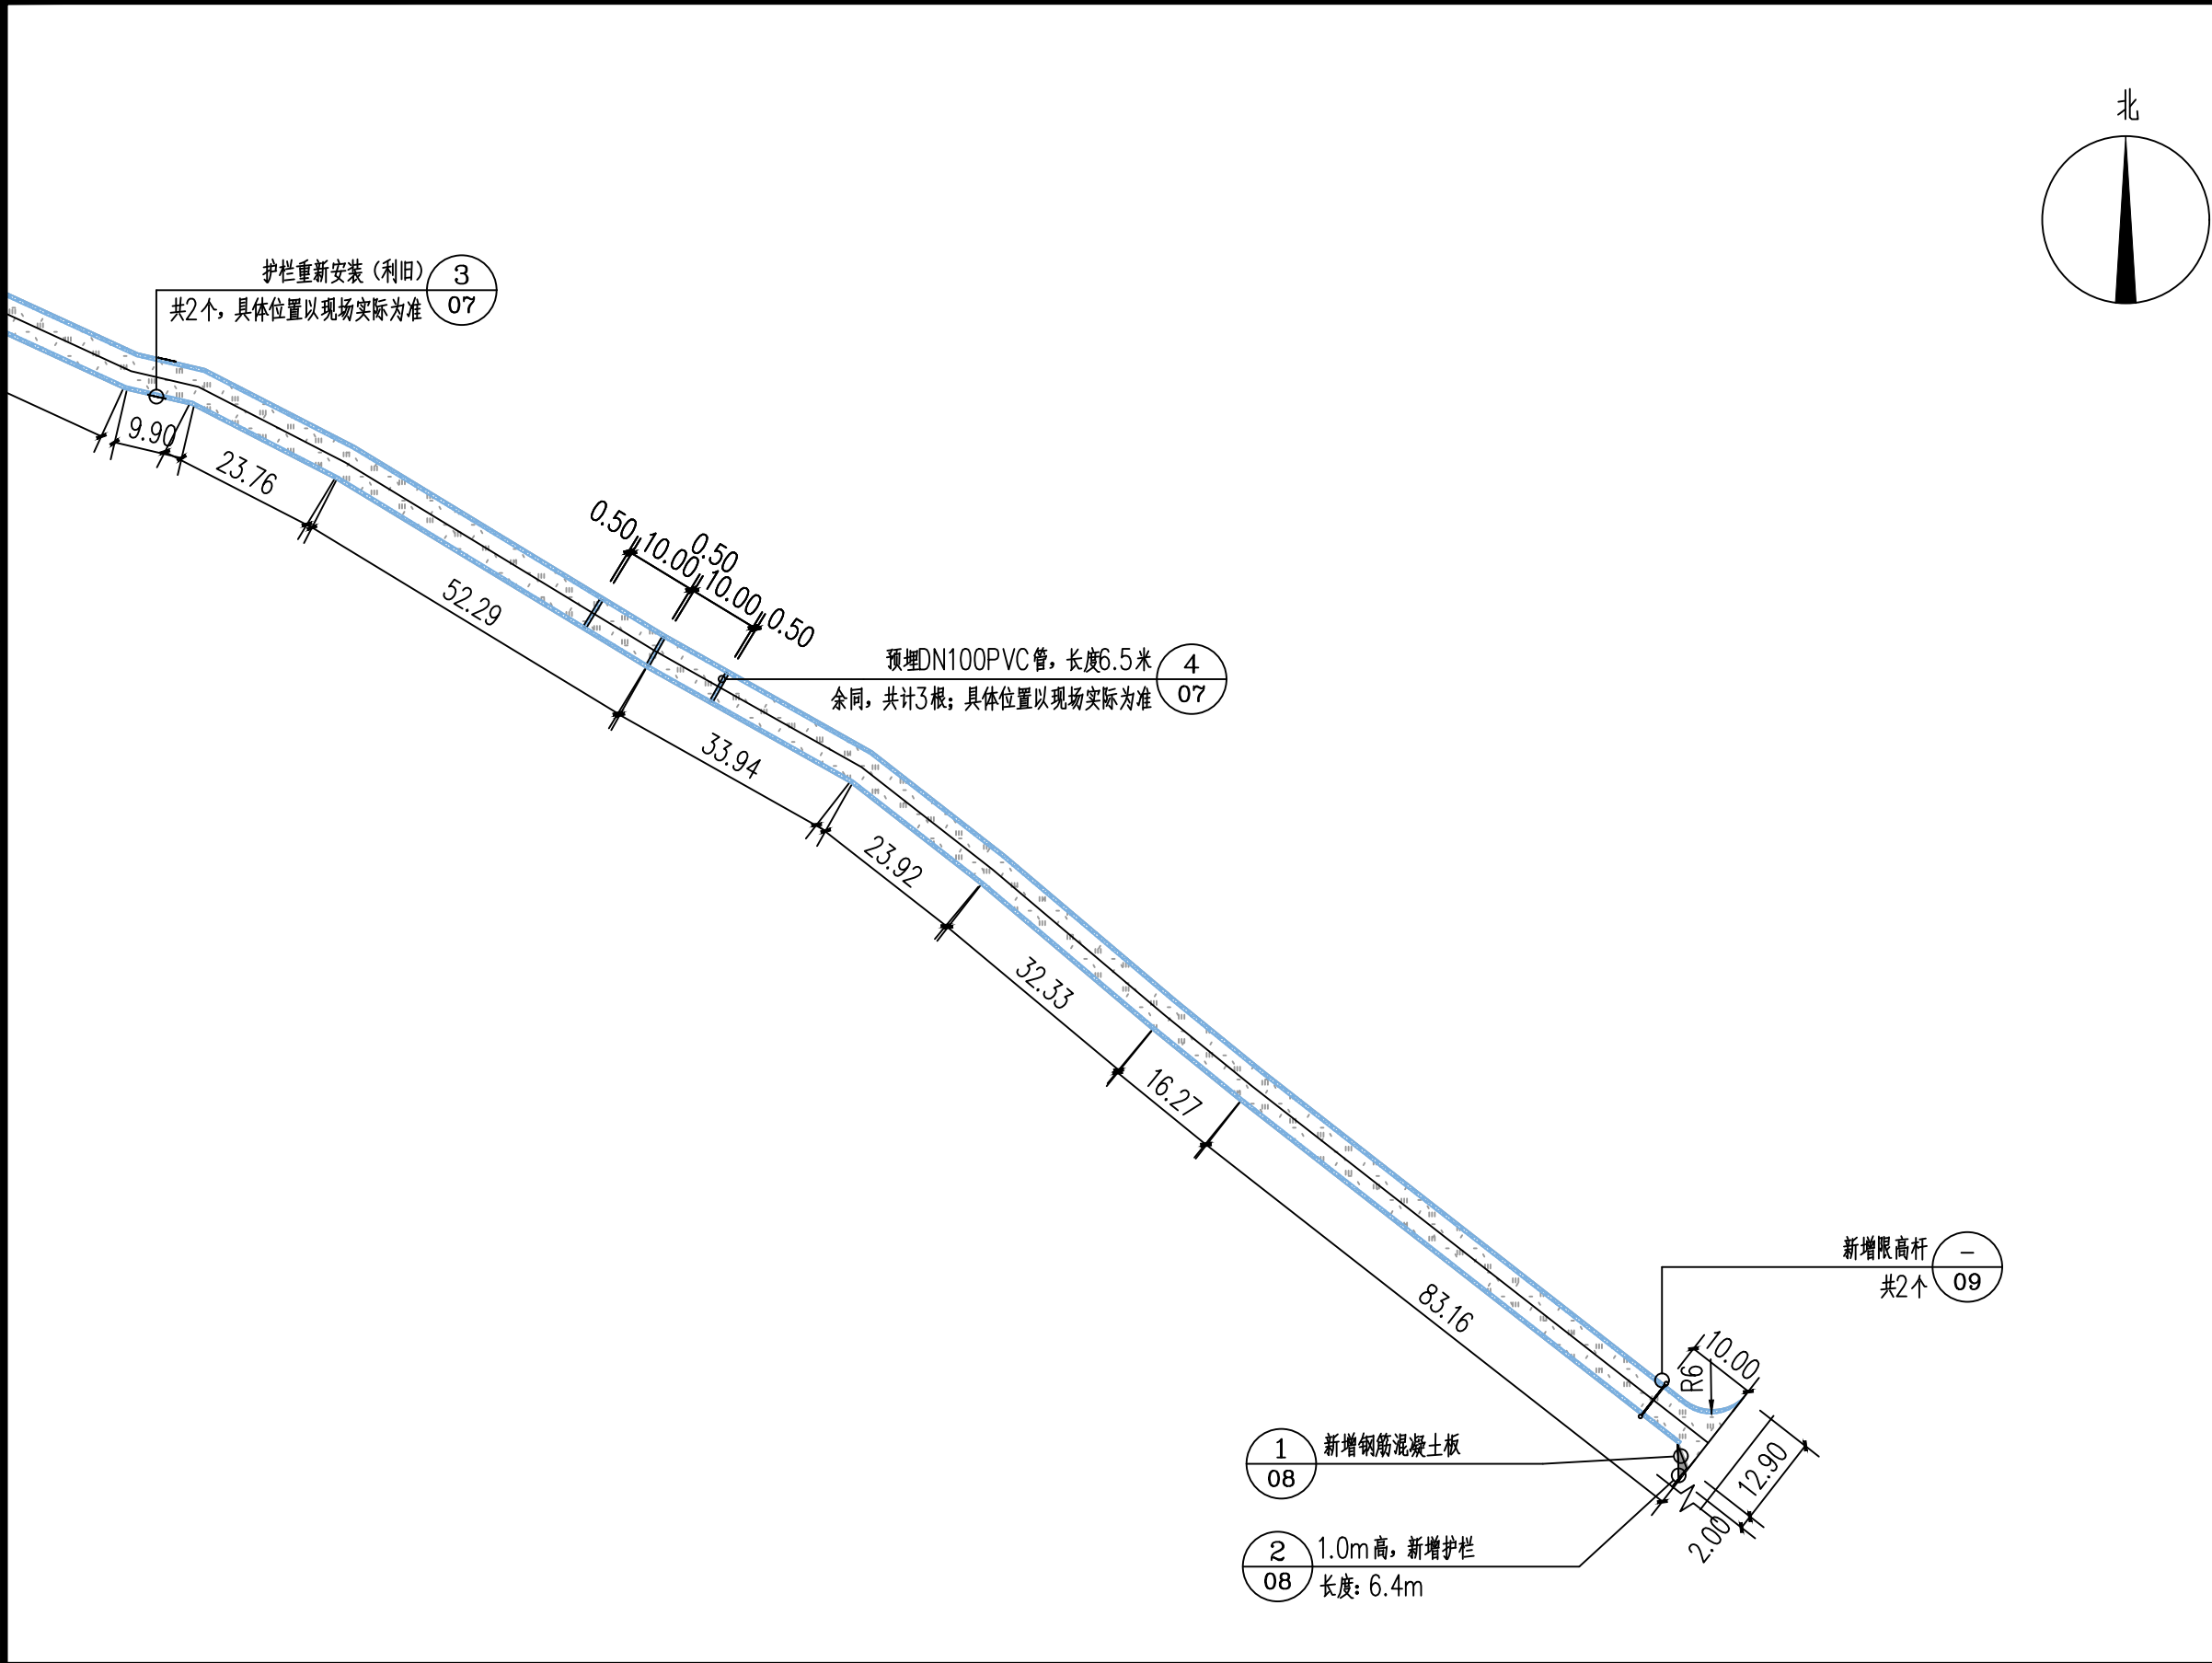

改造后总平面图二


注: 1.本图尺寸单位为“m”
2.改造后路段宽度5.5米, 长度54.4米

 中科经纬 ZHONGKE JINGWEI 中华人民共和国建设部工程设计证书 建筑行业乙级 A251034247 地址:中国·成都·成都市青羊区敬业路218号15栋1楼1号 电话: 028-67775960 传真: 028-67775920 网址: www.zkjwgcjs.com E-mail: zkjwgcjs@163.com 邮编: 610041			
注册执业章 REGISTERED PRACTICE SIGNET			
姓 名 NAME		明 侨	
注册印章号 REGISTERED SIGNET NO.		5100235-006	
注册证书号 REGISTERED CERTIFICATE NO.		20215102475	
设计总负责人 PROJECT LEADER		明 侨	明 侨
专业负责人 DIVISION CHIEF		陈丽	陈丽
设 计 DESIGNED BY		林亮	林亮
校 对 PROCESSED BY		陈丽	陈丽
审 核 CHECKED BY		明 侨	明 侨
审 定 APPROVED BY		明 侨	明 侨
设计单位 DESIGNER			
中科经纬工程技术有限公司			
建设单位 CLIENT			
平潭君山镇松南村村民委员会			
工程名称 PROJECT			
后池路东段（翠园北路至038乡道段） 水泥路面浇筑沥青路面项目			
图 名 TITLE			
改造后总平面图二			
设计号 PROJECT NO.			
图 别 DWG TYPE	建施	图 号 DWG TYPE	05
版本号 Ver.	A	日 期 DATE	
所有设计图以最新版本为有效版本			
本图若未盖本单位出图章则无效			

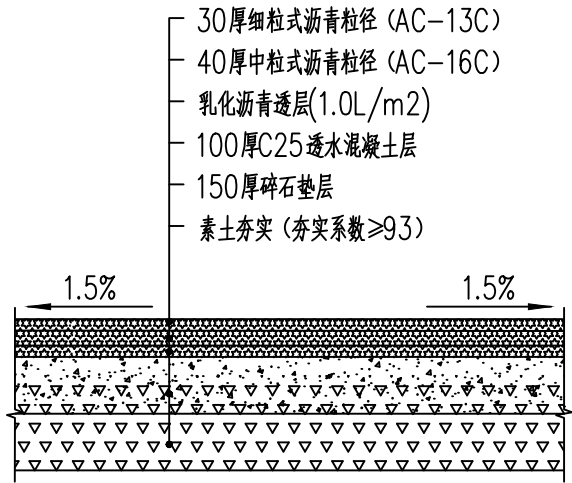


1 车行透水沥青道路做法一
1:20

注：1.因道路两侧均为碎毛石，施工时因设置相应挡板等防护措施
2.该做法仅适用于路面恢复（详管道预埋大样）

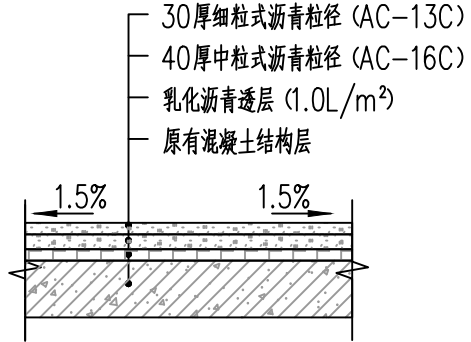


2 车行透水沥青道路做法二
1:20

注：因道路两侧均为碎毛石，施工时因设置相应挡板等防护措施

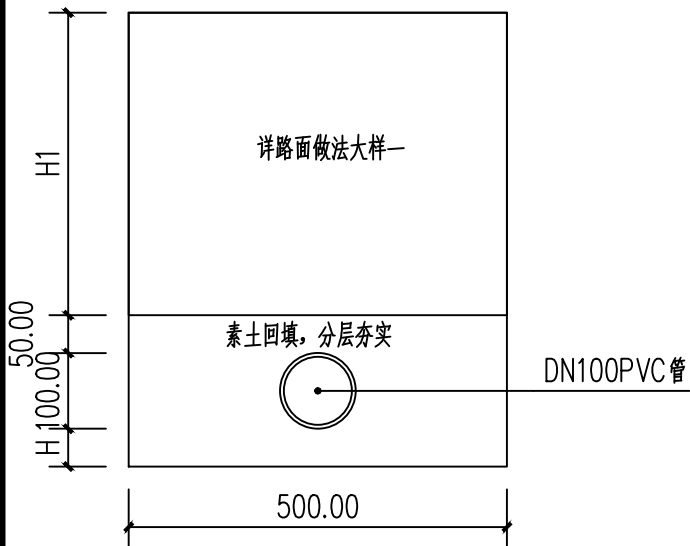

4 管道预埋断面
1:10

注：1.本工程需预埋3根DN100PVC管；具体位置以现场实际为准
2.单根PVC管长度为6.5米，两端各超出路段0.5米

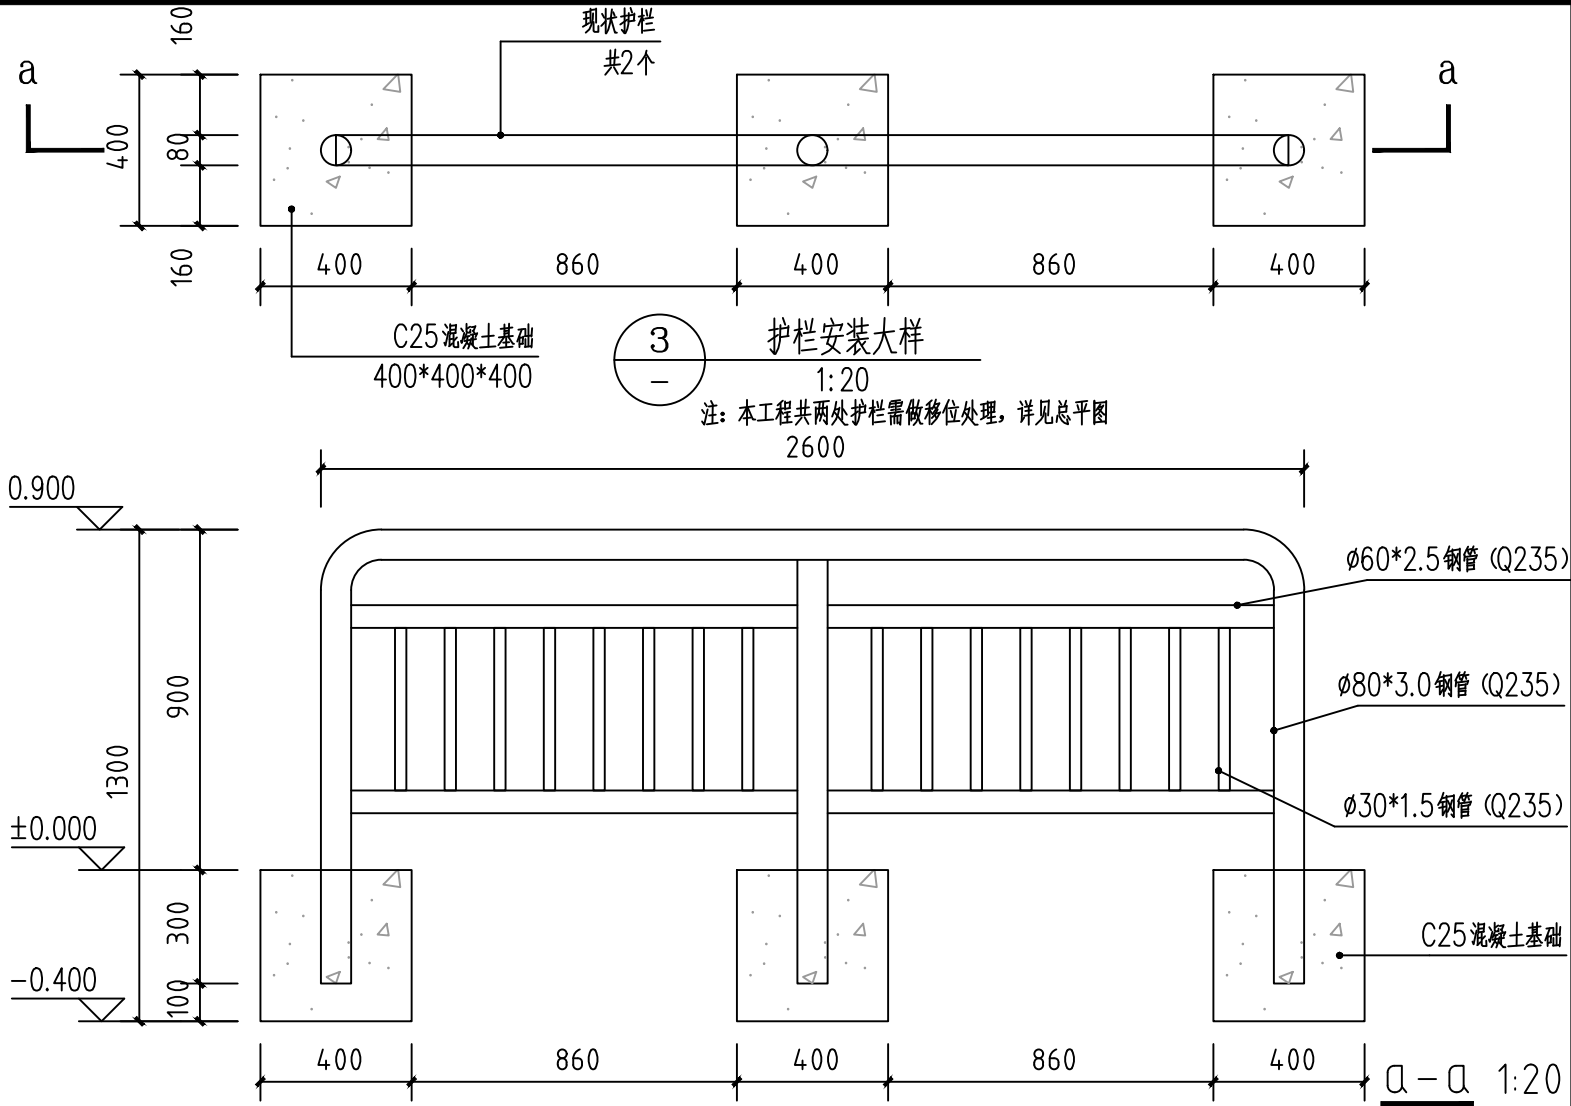









中科经纬


ZHONGKE JINGWEI

中华人民共和国建设部工程设计证书
建筑行业乙级 A251034247

地址:中国·成都·成都市青羊区敬业路218号15栋1楼1号
电话: 028-67775960
传真: 028-67775920 网址: www.zkjwgcjs.com
E-mail: zkjwgcjs@163.com 邮编: 610041

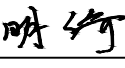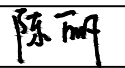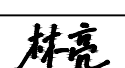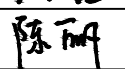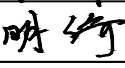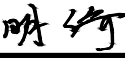
注册执业章 REGISTERED PRACTICE SIGNET		
姓名 NAME	明 桥	
注册印章号 REGISTERED SIGNET NO.	5100235-006	
注册证书号 REGISTERED CERTIFICATE NO.	20215102475	
设计总负责人 PROJECT LEADER	明 桥	
专业负责人 DIVISION CHIEF	陈丽	
设 计 DESIGNED BY	林亮	
校 对 PROCESSED BY	陈丽	
审 核 CHECKED BY	明 桥	
审 定 APPROVED BY	明 桥	

设计单位		DESIGNER	
中科经纬工程技术有限公司			
建设单位		CLIENT	
平潭君山镇松南村村民委员会			
工程名称		PROJECT	
后池路东段（翠园北路至038乡道段） 水泥路面浇筑沥青路面项目			
图 名		TITLE	
大样详图1			
设计号 PROJECT NO.			
图 别 DWG TYPE	建施	图 号 DWG TYPE	07
版本号 Ver.	A	日 期 DATE	
所有设计图以最新版本为有效版本			

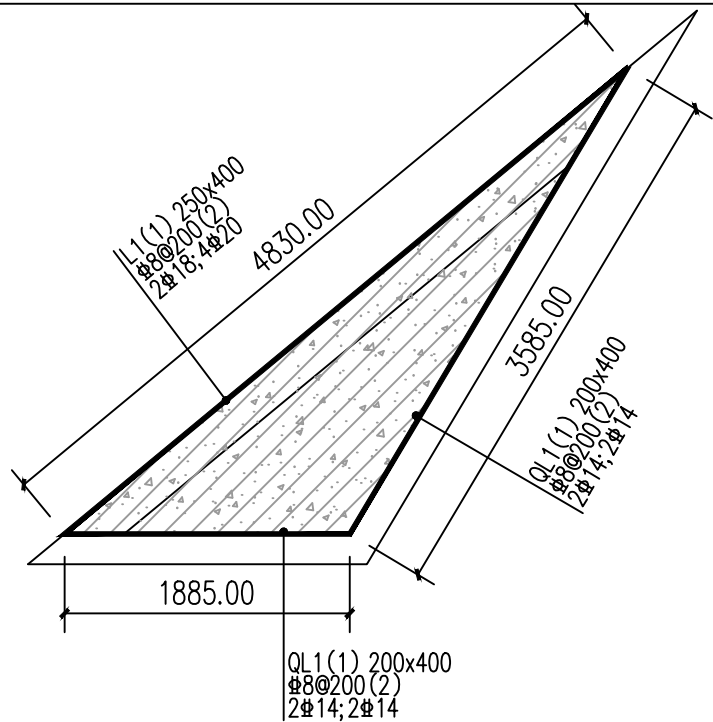


1
—
混凝土板配筋大样
1:50

- 说明:
- 混凝土强度等级C25, 钢筋采用HRB400(Φ)。
 - 图中未注明的板厚均为150mm, 板筋双层双向布置, 板底: Φ10@150, 板面: Φ10@150。

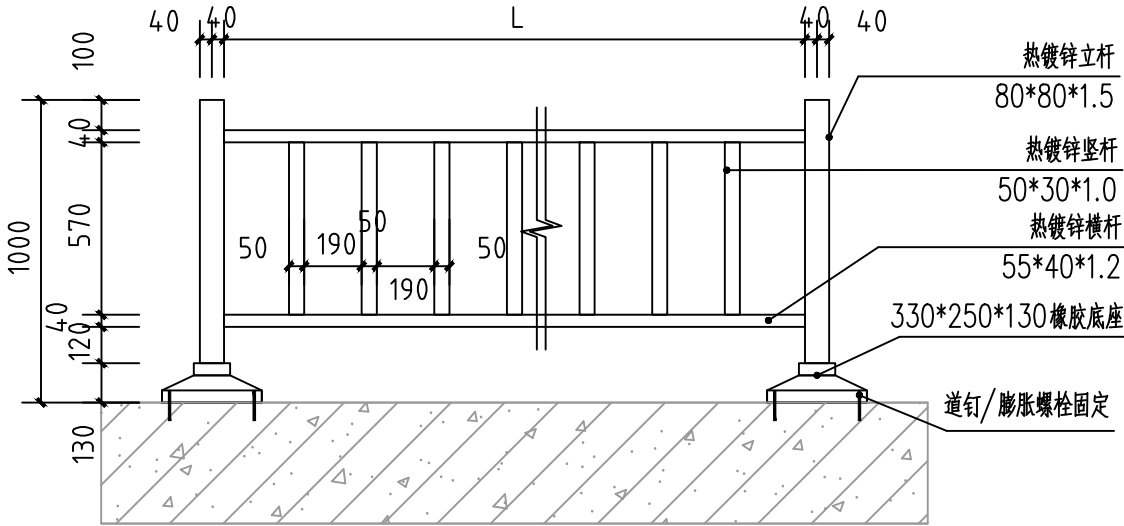

2
—
行车道路护栏大样
1:25

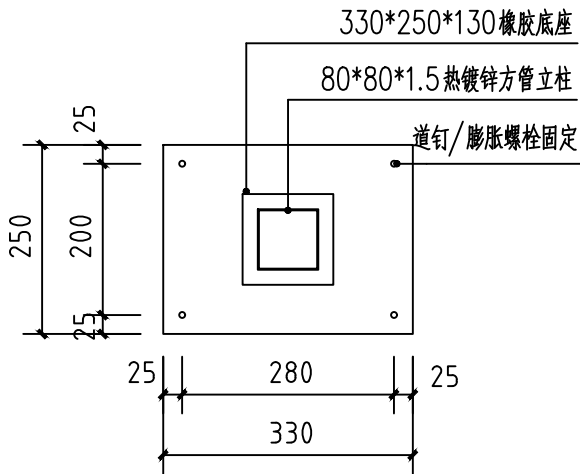

橡胶底座示意图 1:5



行车道路护栏意向图

注: 本图仅供前期预算编制参考, 具体样式由业主选择专业厂家制作施工



中科经纬
ZHONGKE JINGWEI

中华人民共和国建设部工程设计证书
建筑行业乙级 A251034247

地址: 中国·成都·成都市青羊区敬业路218号15栋1楼1号
电话: 028-67775960 网址: www.zkjwgcjs.com
传真: 028-67775920 E-mail: zkjwgcjs@163.com 邮编: 610041


注册执业章 REGISTERED PRACTICE SIGNET	
姓名 NAME	明 桥
注册印章号 REGISTERED SIGNET NO.	5100235-006
注册证书号 REGISTERED CERTIFICATE NO.	20215102475

设计总负责人 PROJECT LEADER	明 桥	明 桥
专业负责人 DIVISION CHIEF	陈丽	陈丽
设计 DESIGNED BY	林亮	林亮
校对 PROCESSED BY	陈丽	陈丽
审核 CHECKED BY	明 桥	明 桥
审定 APPROVED BY	明 桥	明 桥



设计单位 DESIGNER			
中科经纬工程技术有限公司			
建设单位 CLIENT			
平潭君山镇松南村村民委员会			
工程名称 PROJECT			
后池路东段(翠园北路至038乡道段) 水泥路面浇筑沥青路面项目			
图 名 TITLE			
大样详图2			
设计号 PROJECT NO.			
图 别 DWG TYPE	建施	图 号 DWG TYPE	08
版本号 Ver.	A	日 期 DATE	

所有设计图以最新版本为有效版本
本图若未盖本单位出图章则无效

暖通
电气
给排水
结构
建筑

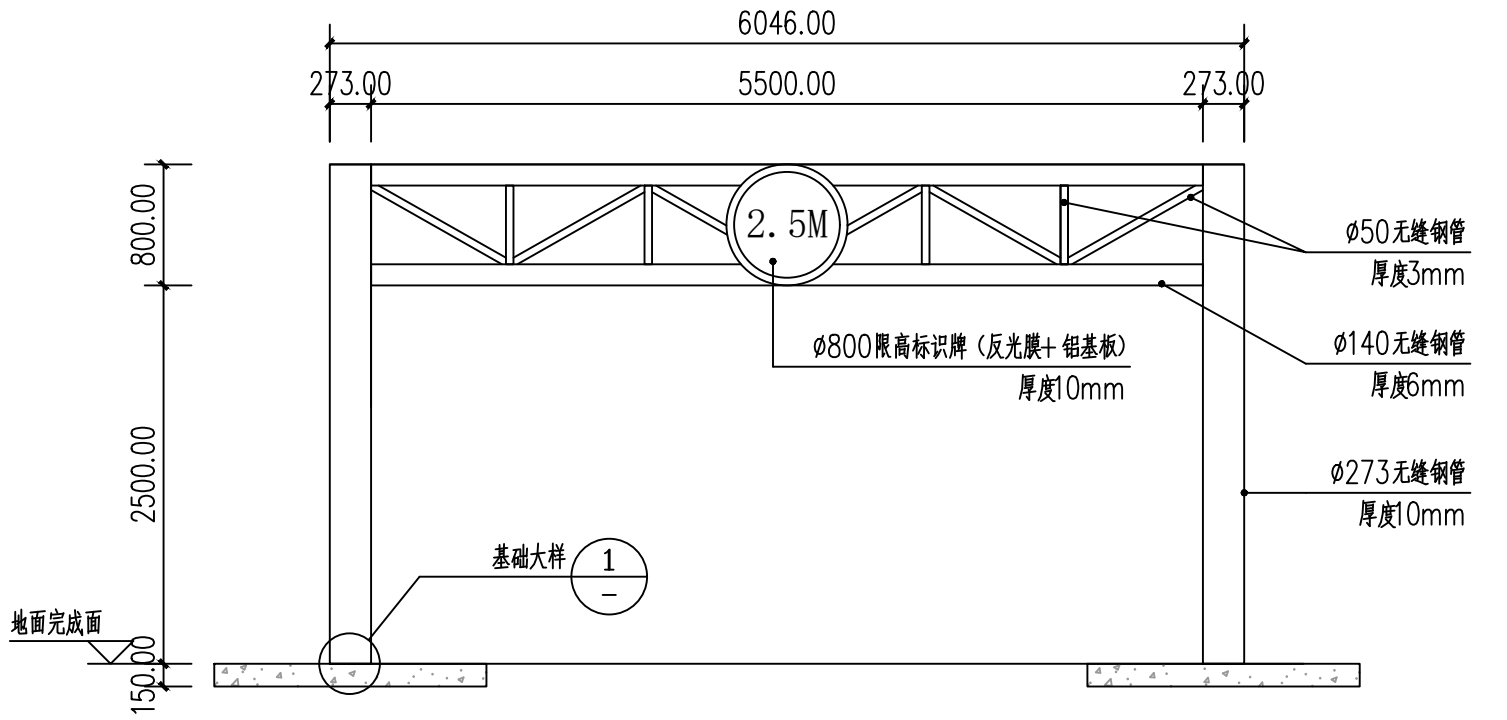

限高杆示意图 1:50

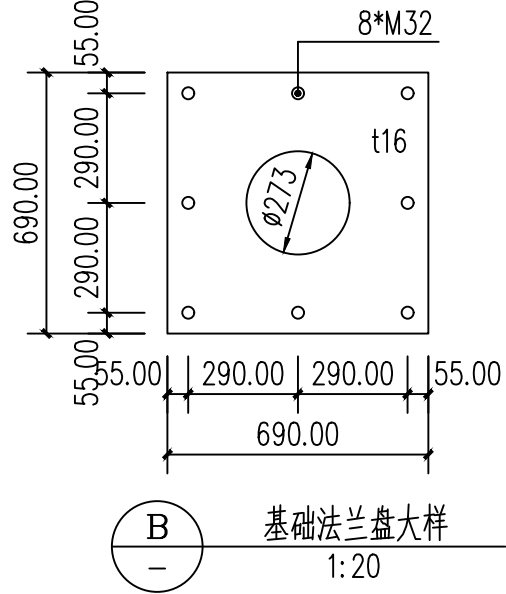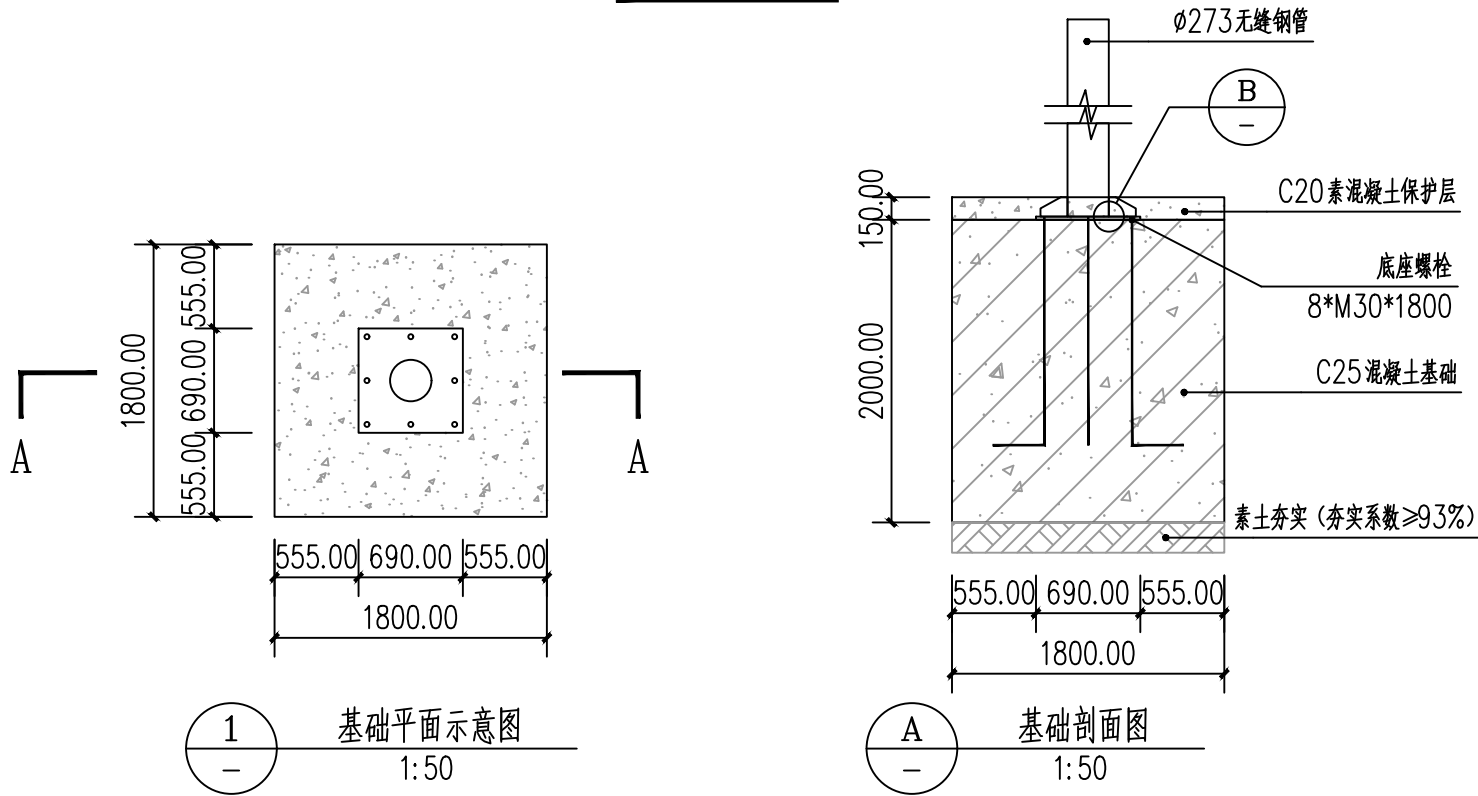

说明:

1. 本图除特殊说明外, 尺寸均以毫米计
2. 限高杆钢材均使用304无缝钢管, 连接方式为焊接
3. 混凝土均采用C25砼基础现浇, 浇筑混凝土之前需预埋基础法兰盘, 基础下土基要求压实度93%以上
4. 限高杆本工程共计1个, 该大样图仅供参考, 具体有专业厂家制作施工



中科经纬
ZHONGKE JINGWEI

中华人民共和国建设部工程设计证书
建筑行业乙级 A251034247

地址: 中国·成都·成都市青羊区敬业路218号15栋1楼1号
电话: 028-67775960
传真: 028-67775920 网址: www.zkjwgcjs.com
E-mail: zkjwgcjs@163.com 邮编: 610041

注册执业章 REGISTERED PRACTICE SIGNET	
姓名 NAME	明 侨
注册印章号 REGISTERED SIGNET NO.	5100235-006
注册证书号 REGISTERED CERTIFICATE NO.	20215102475

设计总负责人 PROJECT LEADER	明 侨	明 侨
专业负责人 DIVISION CHIEF	陈丽	陈丽
设 计 DESIGNED BY	林亮	林亮
校 对 PROCESSED BY	陈丽	陈丽
审 核 CHECKED BY	明 侨	明 侨
审 定 APPROVED BY	明 侨	明 侨

设计单位 DESIGNER

中科经纬工程技术有限公司

建设单位 CLIENT

平潭君山镇松南村村民委员会

工程名称 PROJECT

后池路东段（翠园北路至038乡道段） 水泥路面浇筑沥青路面项目

图 名 TITLE

大样详图3

设计号 PROJECT NO.			
图 别 DWG TYPE	建施	图 号 DWG TYPE	09
版本号 Ver.	A	日 期 DATE	

所有设计图以最新版本为有效版本

本图若未盖本单位出图章则无效