


平潭综合实验区雨洪利用工程雨洪工程用地规划红线图（地块一）
2834.6-475.3

秘密

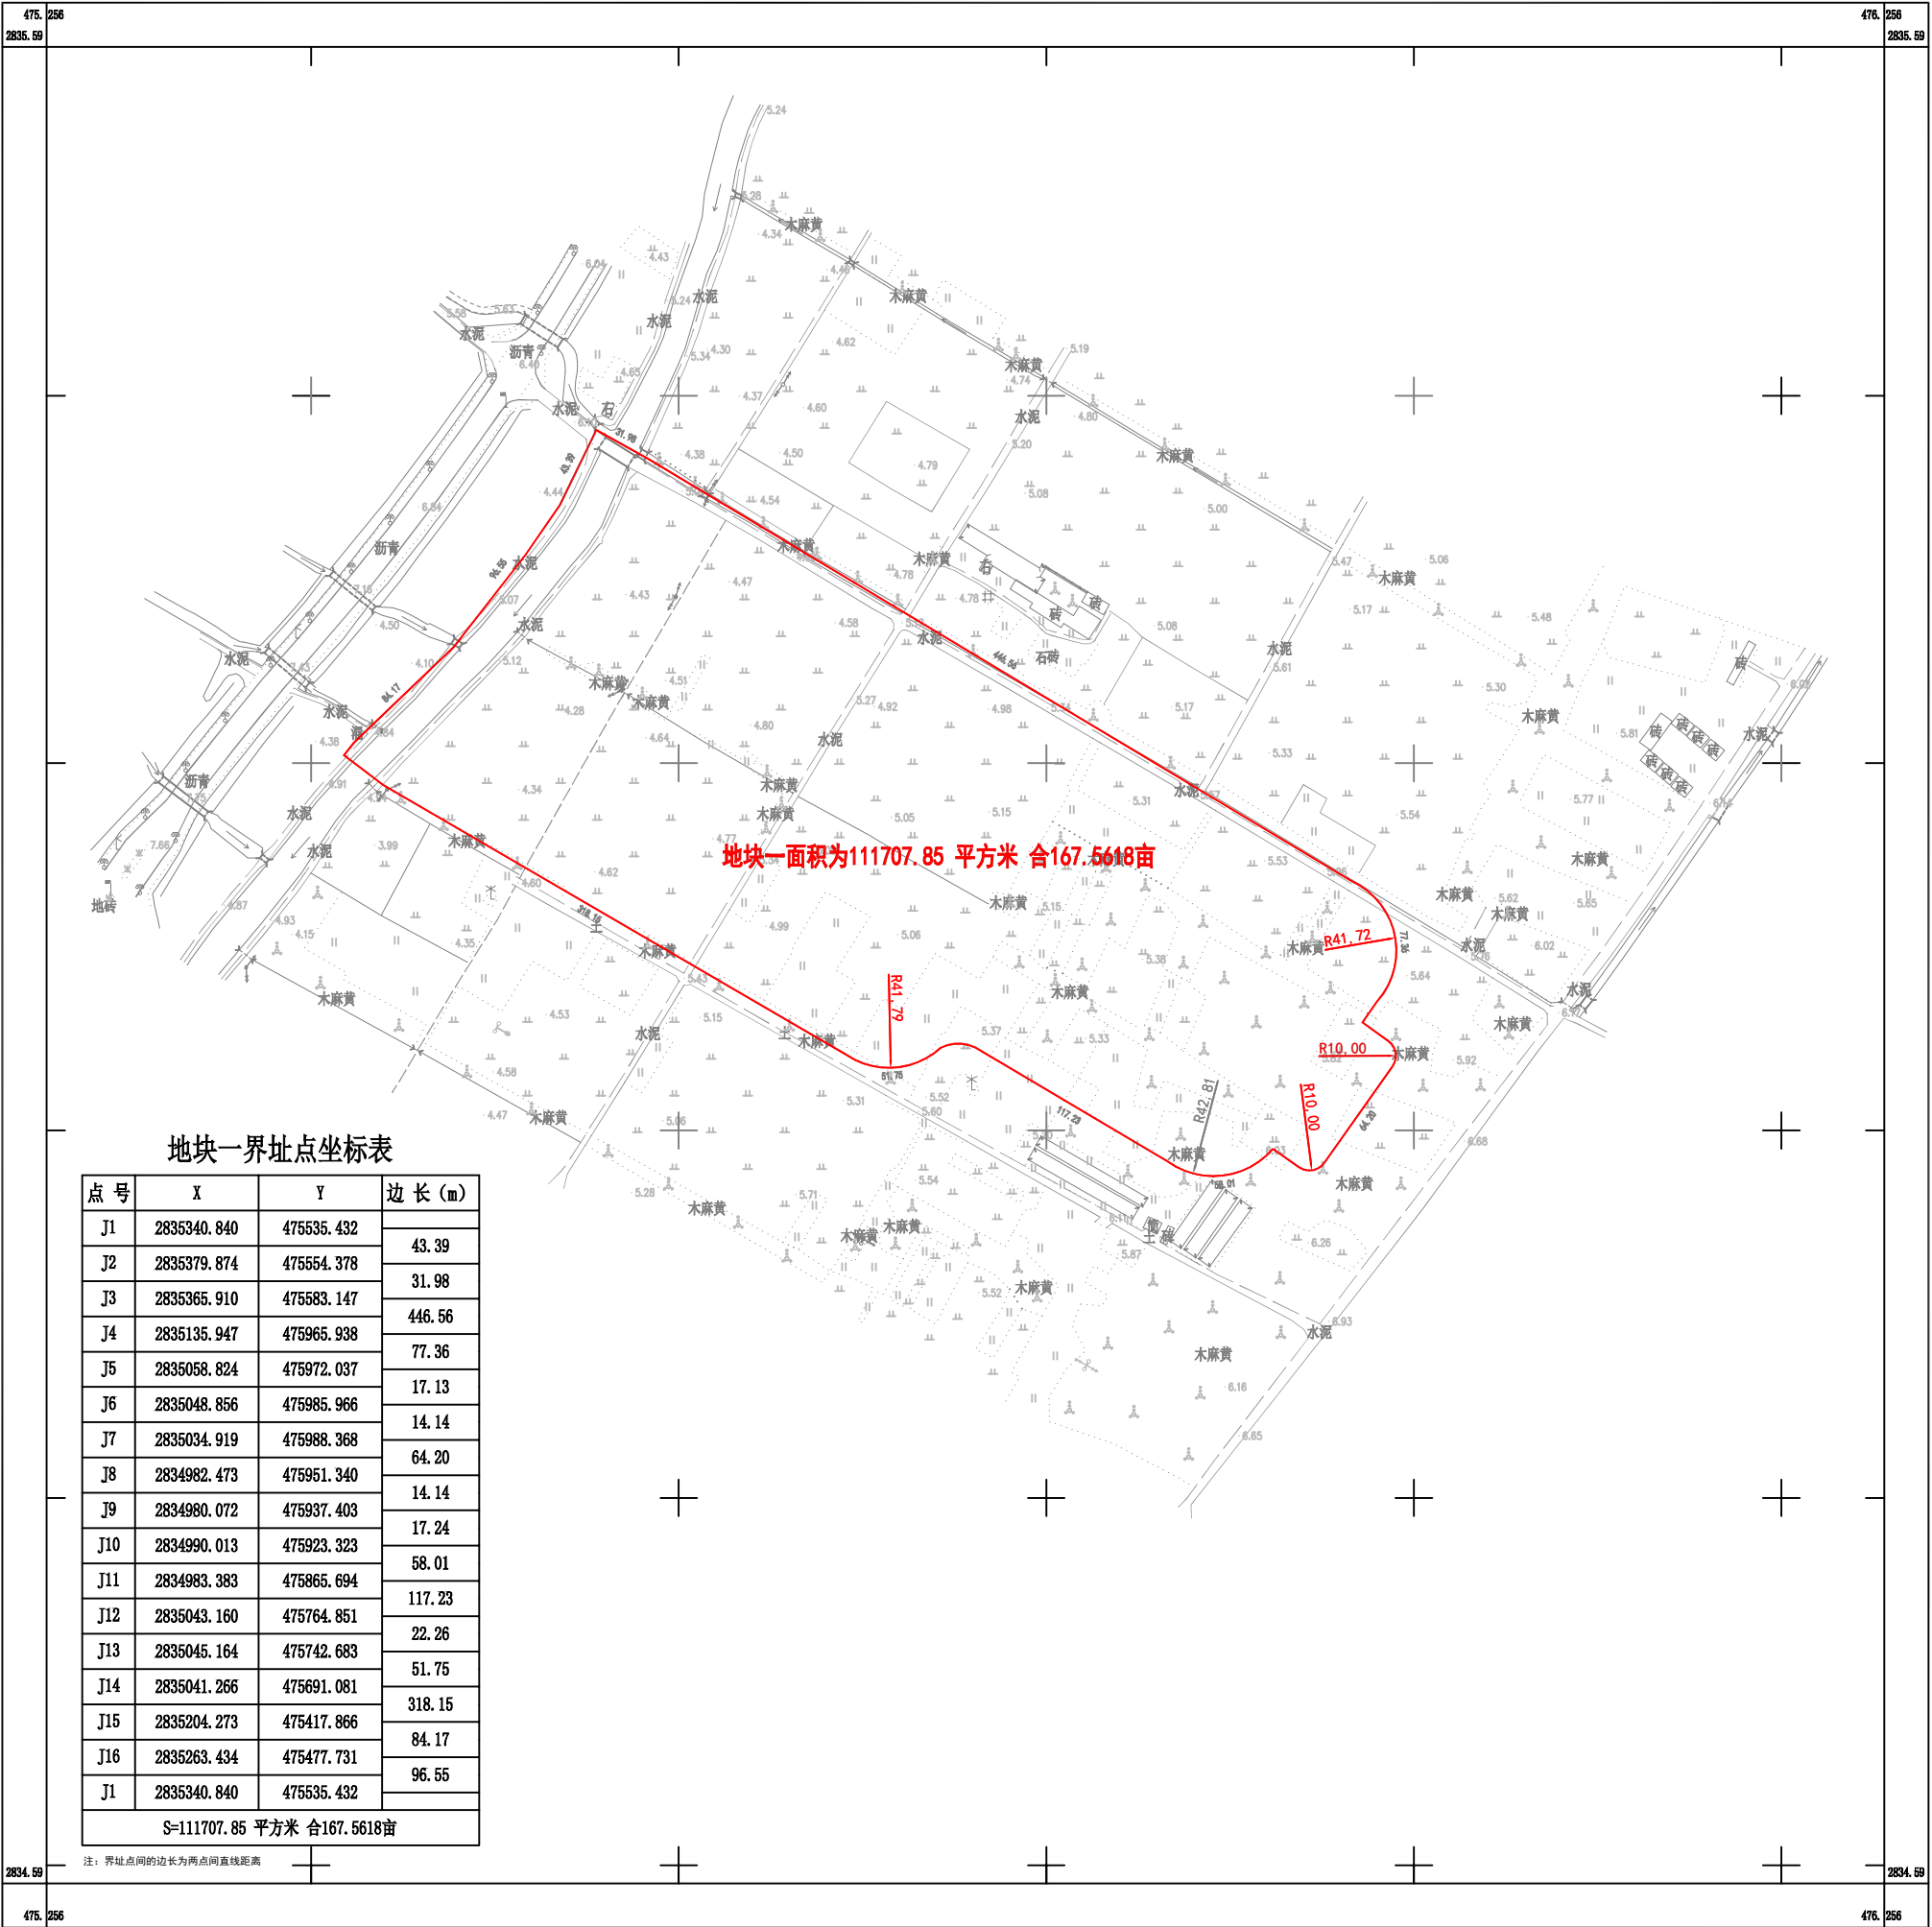

地块一界址点坐标表

点 号	X	Y	边 长 (m)
J1	2835340.840	475535.432	43.39
J2	2835379.874	475554.378	31.98
J3	2835365.910	475583.147	446.56
J4	2835135.947	475965.938	77.36
J5	2835058.824	475972.037	17.13
J6	2835048.856	475985.966	14.14
J7	2835034.919	475988.368	64.20
J8	2834982.473	475951.340	14.14
J9	2834980.072	475937.403	17.24
J10	2834990.013	475923.323	58.01
J11	2834983.383	475865.694	117.23
J12	2835043.160	475764.851	22.26
J13	2835045.164	475742.683	51.75
J14	2835041.266	475691.081	318.15
J15	2835204.273	475417.866	84.17
J16	2835263.434	475477.731	96.55
J1	2835340.840	475535.432	
S=111707.85 平方米 合167.5618亩			

注：界址点间的边长为两点间直线距离

2020年4月数字化制图。
CGCS2000国家大地坐标系，中央子午线120度。
1985国家高程基准，等高距为0.5米。
2007年版图式。

1:2000

测量员：黄 顺
绘图员：许青山
检查员：陈龙珍