


建筑产业化基地周边路网-芦洋北路（瑶竹北路-长盛路）红线图

475. 102		475. 682
2831. 698		2831. 698

地块一至地块二总面积为7985. 43 平方米 合11. 9781亩

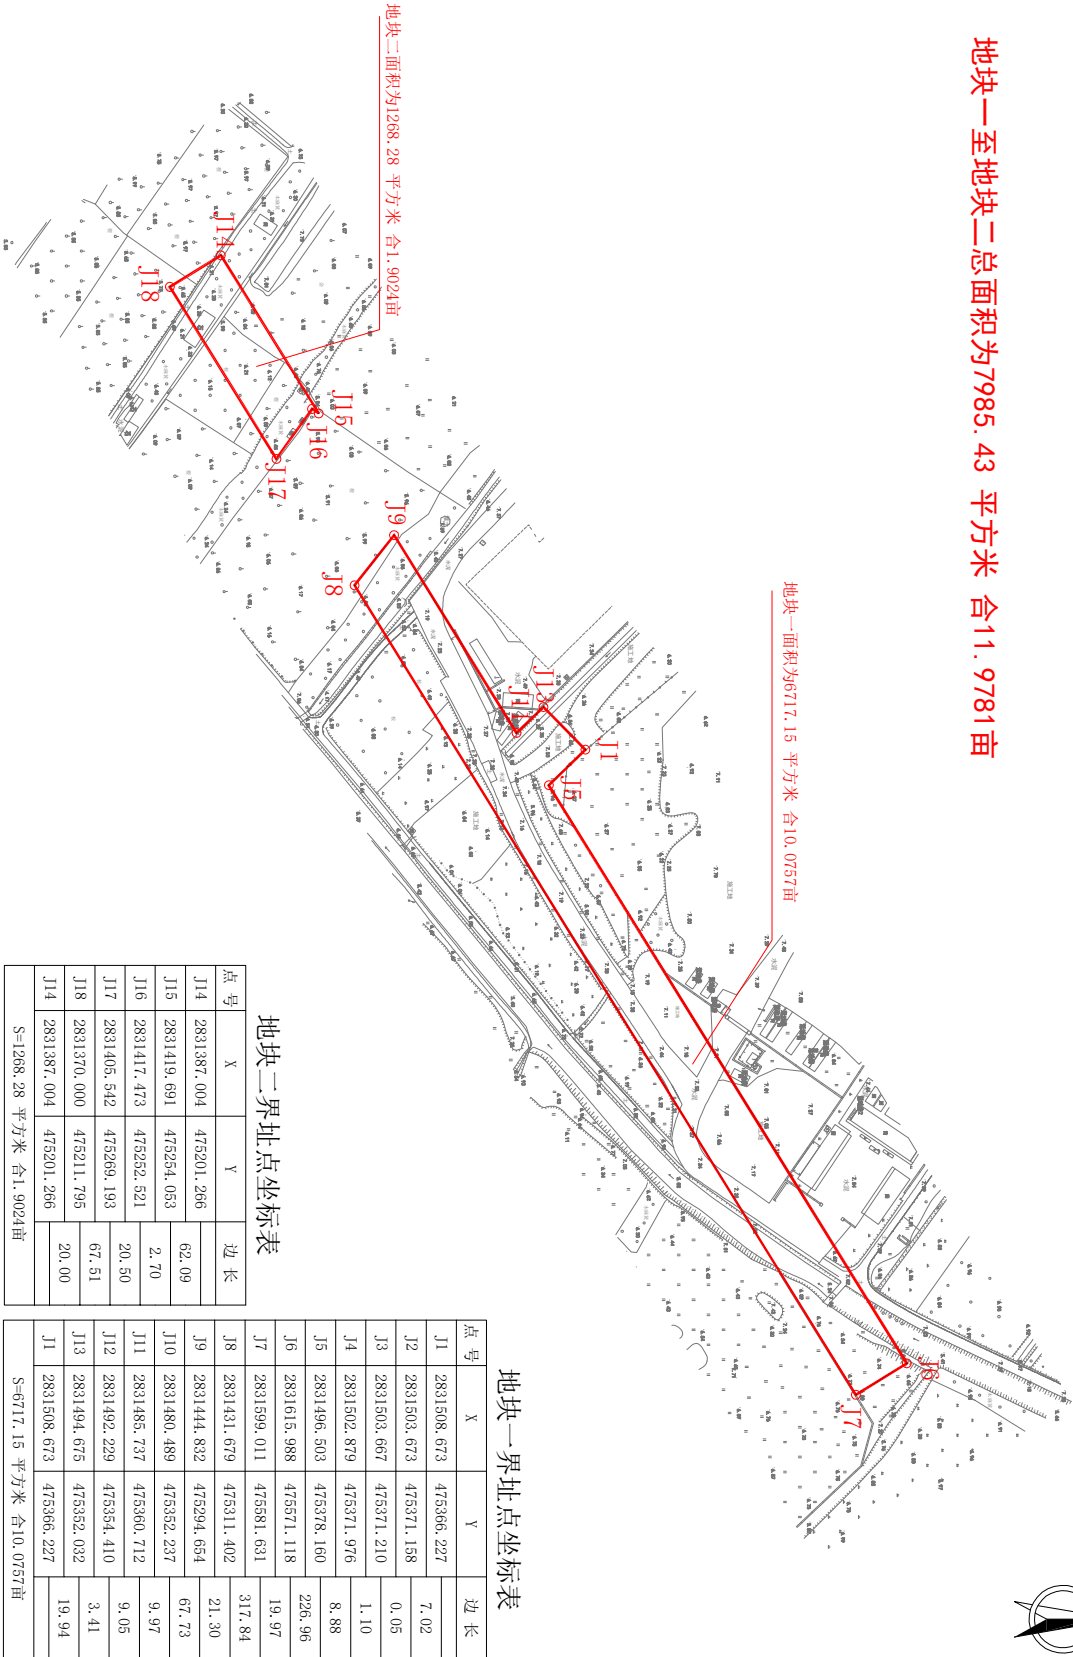

地块一界址点坐标表

点号	X	Y	边长
J1	2831508. 673	475366. 227	7. 02
J2	2831503. 673	475371. 158	0. 05
J3	2831503. 667	475371. 210	1. 10
J4	2831502. 879	475371. 976	8. 88
J5	2831496. 503	475378. 160	226. 96
J6	2831615. 988	475571. 118	19. 97
J7	2831599. 011	475581. 631	317. 84
J8	2831431. 679	475311. 402	21. 30
J9	2831444. 832	475294. 654	67. 73
J10	2831480. 489	475352. 237	9. 97
J11	2831485. 737	475360. 712	9. 05
J12	2831492. 229	475354. 410	3. 41
J13	2831494. 675	475352. 032	19. 94
J14	2831508. 673	475366. 227	
S=6717. 15 平方米 合10. 0757亩			

点号	X	Y	边长
J14	2831387. 004	475201. 266	62. 09
J15	2831419. 691	475254. 053	2. 70
J16	2831417. 473	475252. 521	20. 50
J17	2831405. 542	475269. 193	67. 51
J18	2831370. 000	475211. 795	20. 00
J14	2831387. 004	475201. 266	
S=1268. 28 平方米 合1. 9024亩			

地块二界址点坐标表

注：界址点间的边长为两点间直线距离

2831. 298		2831. 298
475. 102		475. 682

2000国家大地坐标系，中央子午线120°
1985国家高程基准，等高距为1米

1：2500