


平潭北部自来水厂工程红线图（一）

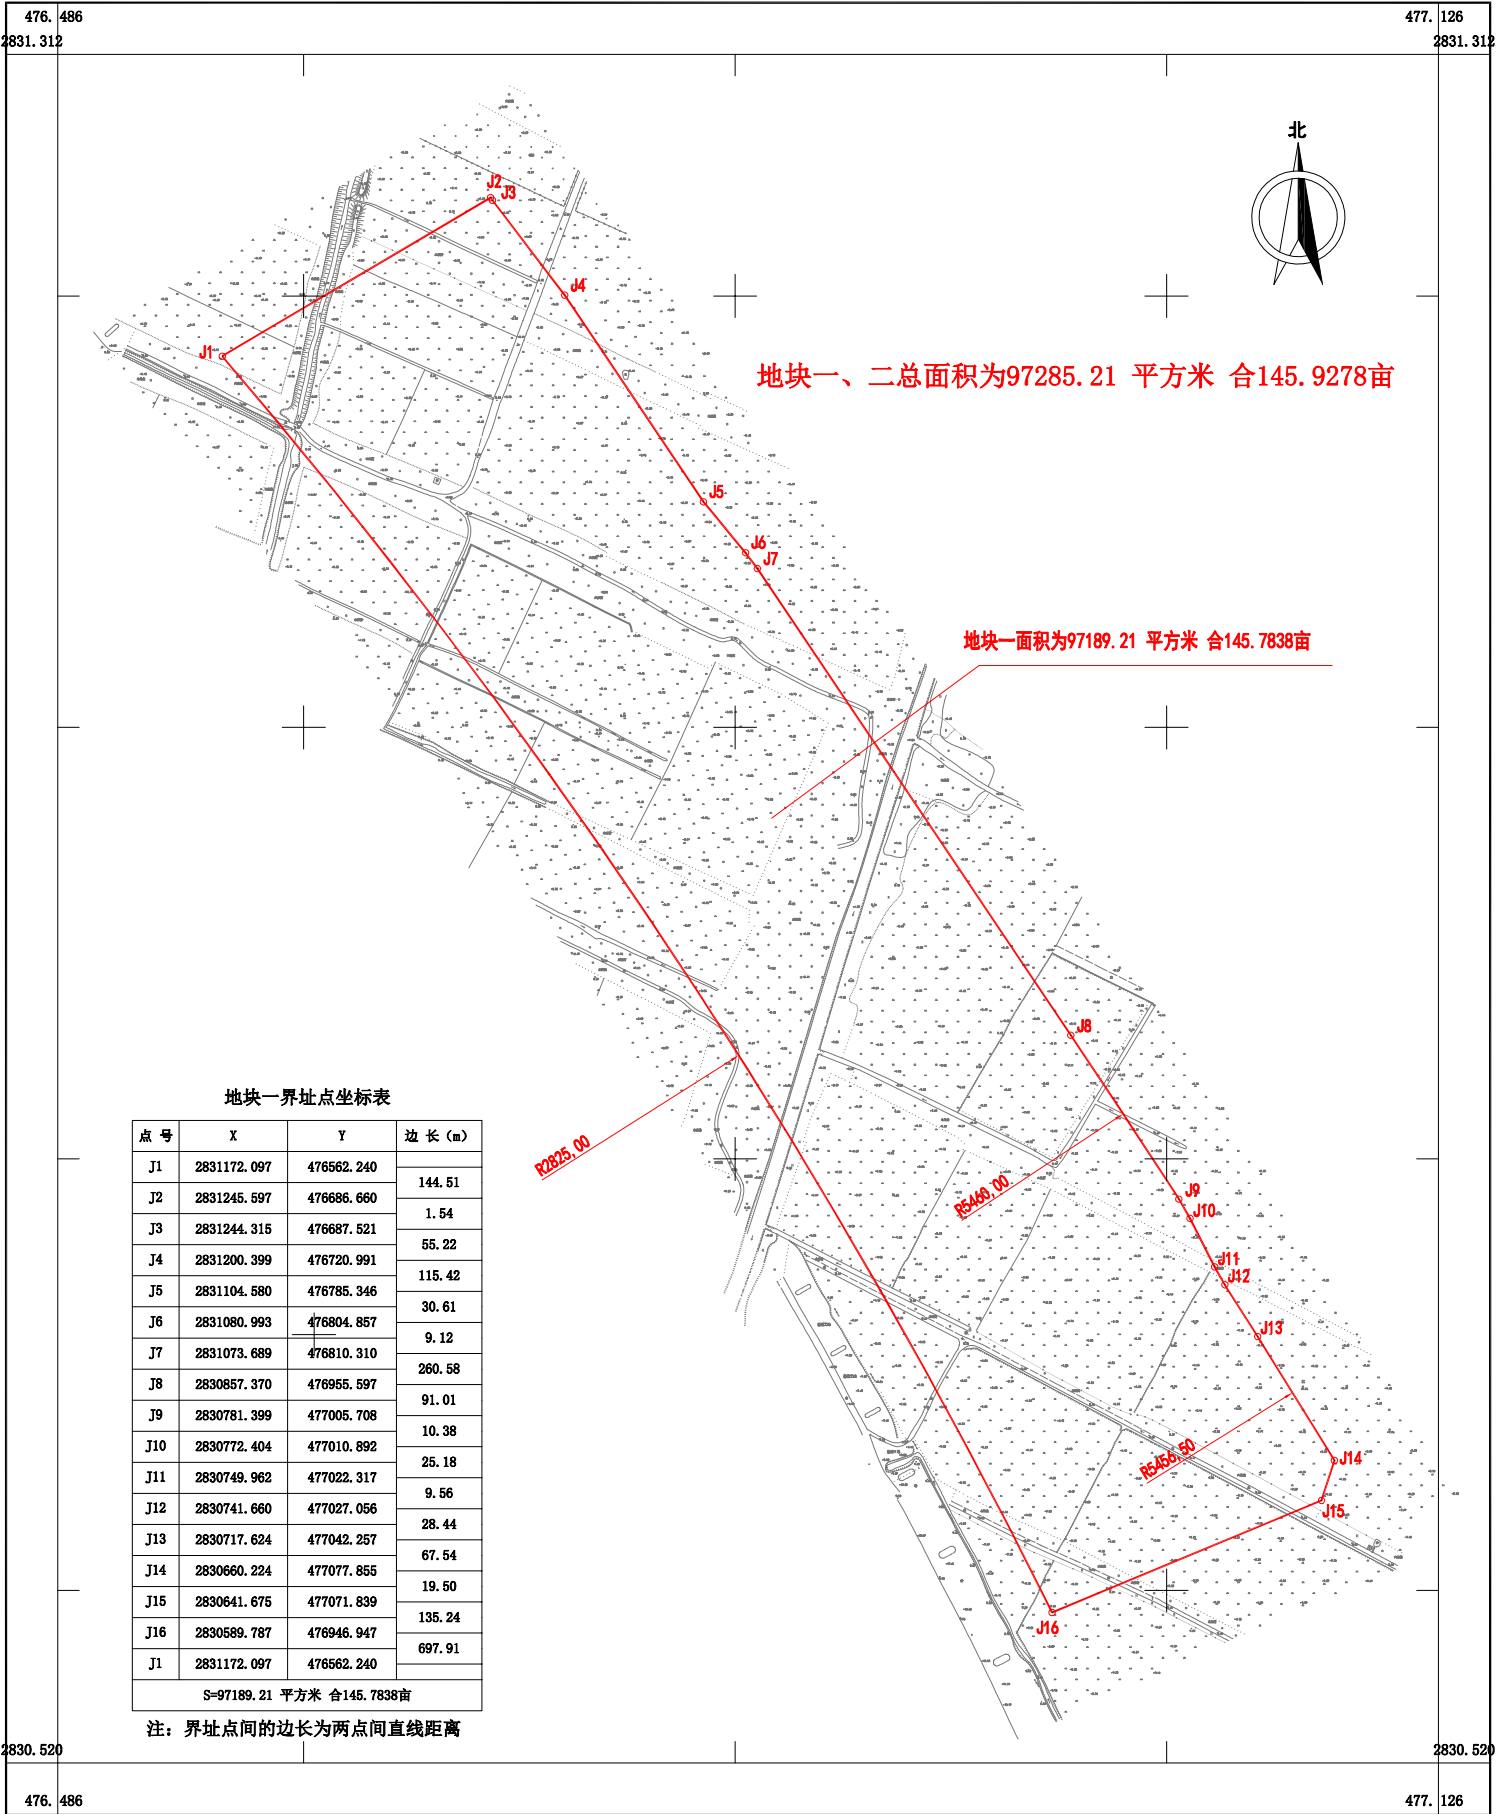

2000国家大地坐标系，中央子午线120°
1985国家高程基准，等高距为1米。

1:3500