


君山路（中山大道-长盛路）选址红线图

福州市勘测院有限公司
内部资料 严禁复制

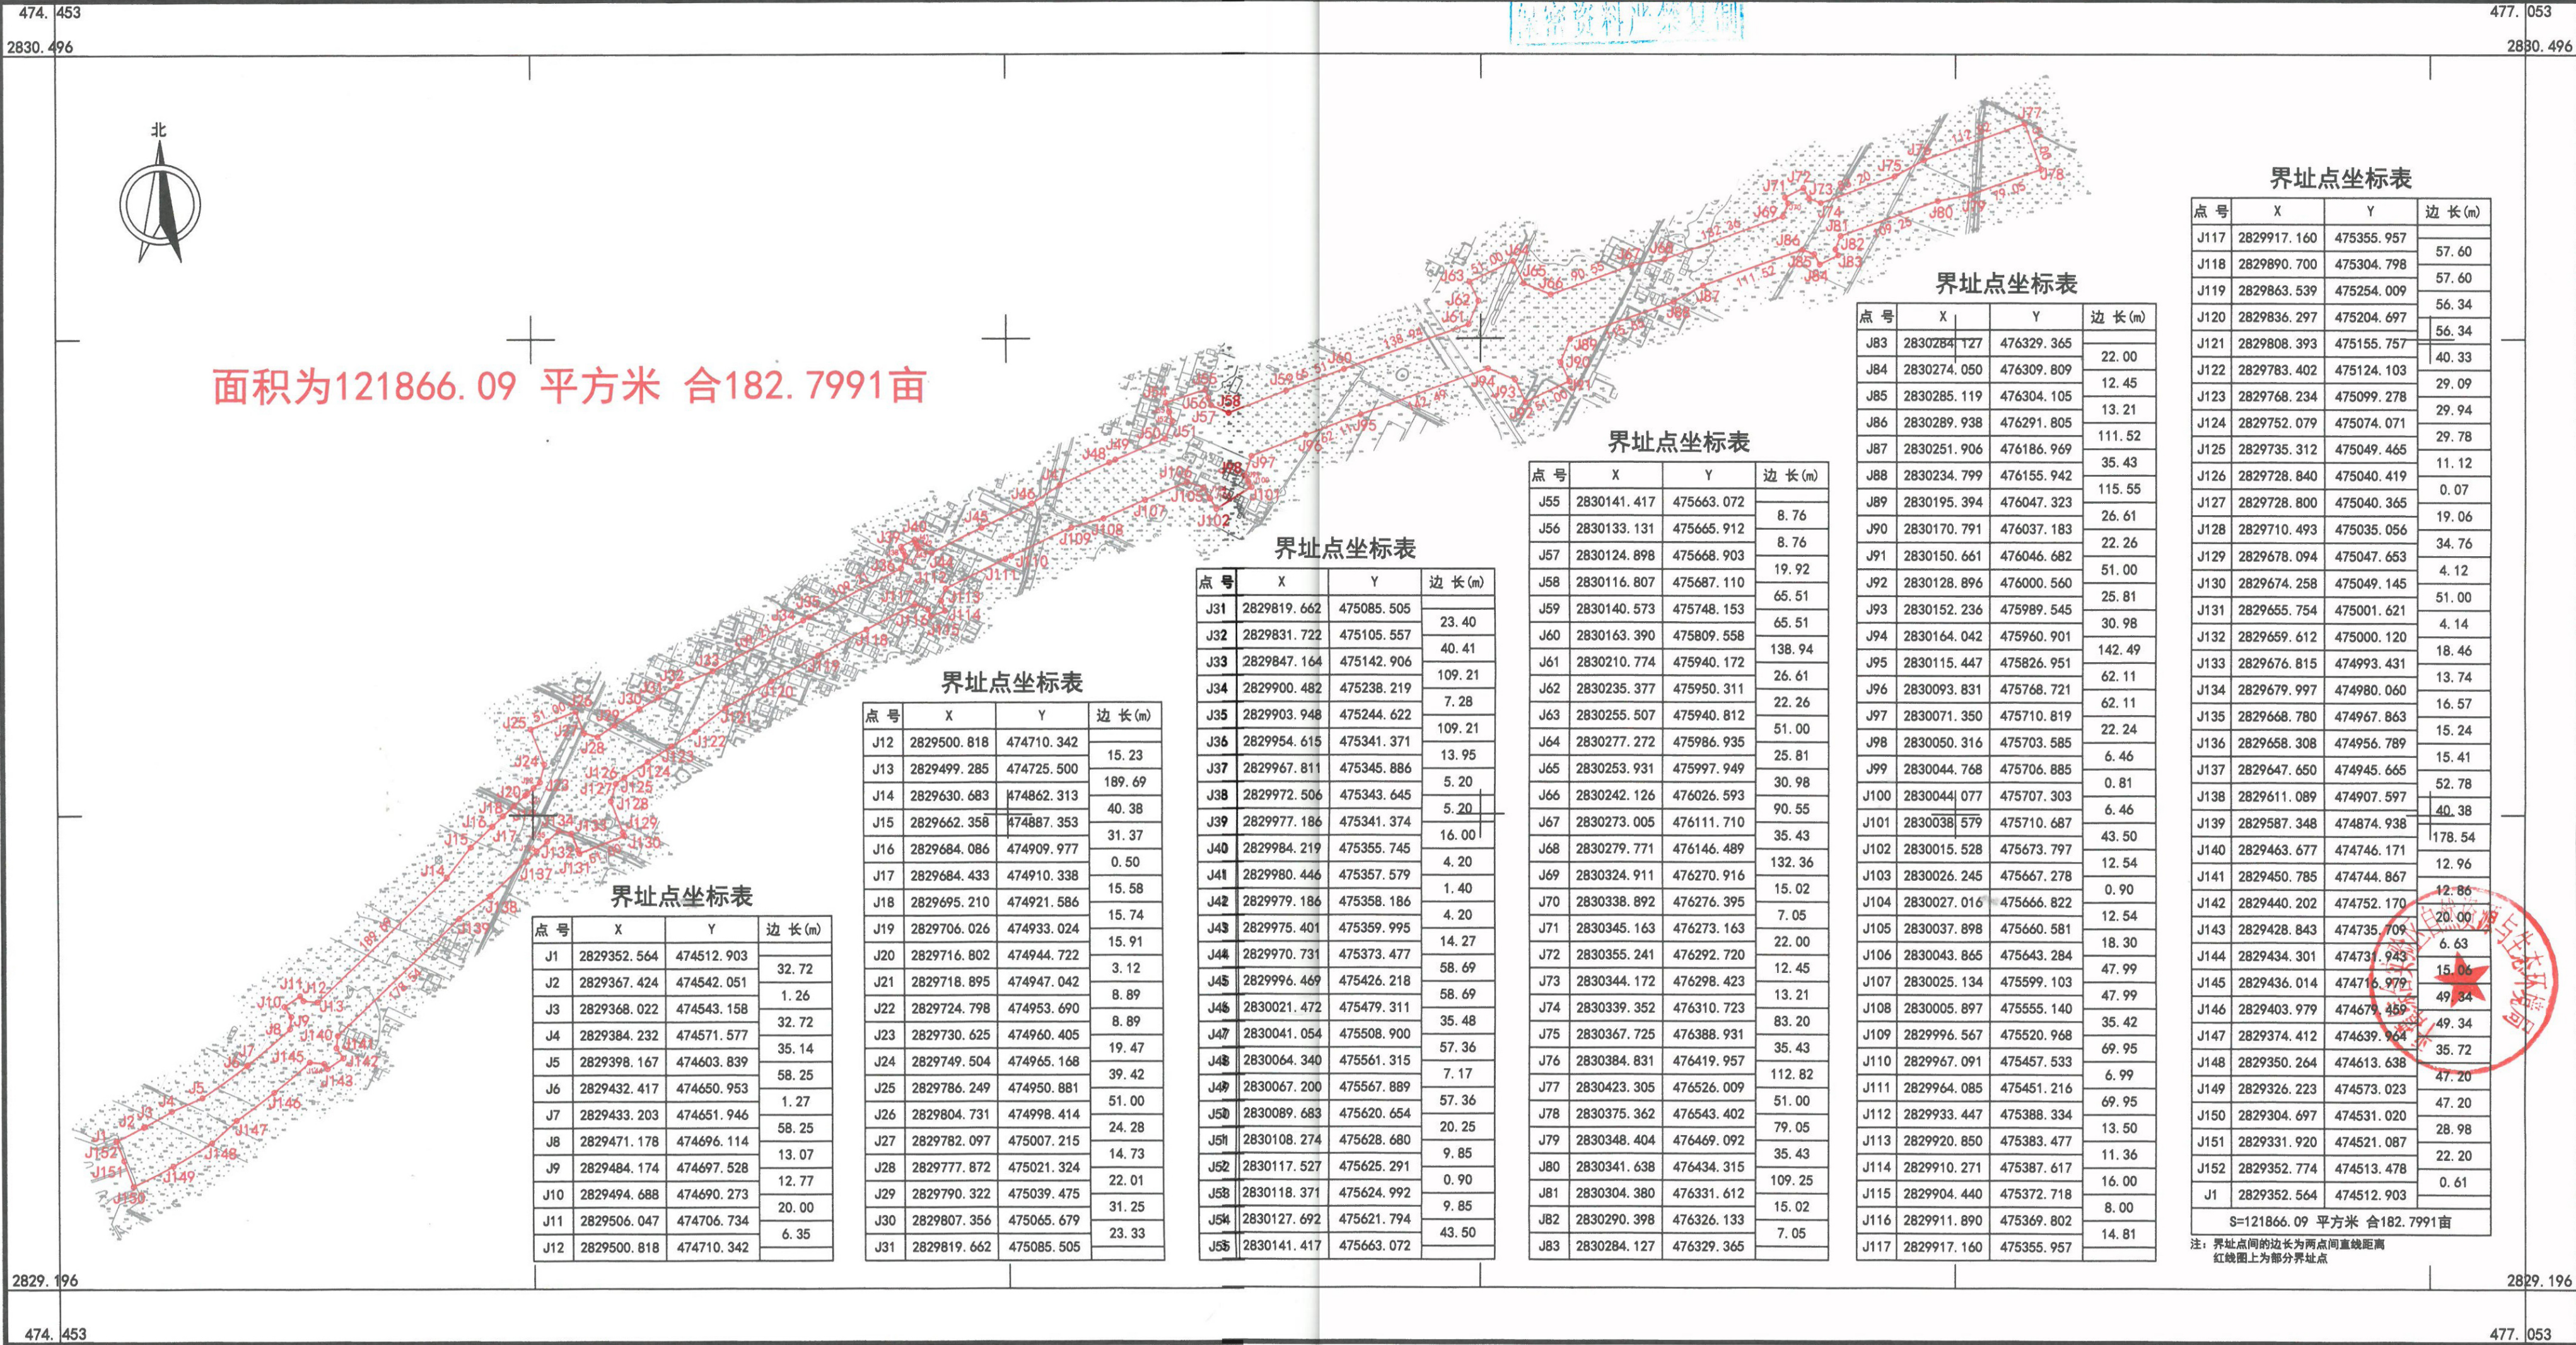

面积为121866.09 平方米 合182.7991亩

界址点坐标表

点号	X	Y	边长(m)
J117	2829917.160	475355.957	57.60
J118	2829890.700	475304.798	57.60
J119	2829863.539	475254.009	56.34
J120	2829836.297	475204.697	56.34
J121	2829808.393	475155.757	40.33
J122	2829783.402	475124.103	29.09
J123	2829768.234	475099.278	29.94
J124	2829752.079	475074.071	29.78
J125	2829735.312	475049.465	11.12
J126	2829728.840	475040.419	0.07
J127	2829728.800	475040.365	19.06
J128	2829710.493	475035.056	34.76
J129	2829678.094	475047.653	4.12
J130	2829674.258	475049.145	51.00
J131	2829655.754	475001.621	4.14
J132	2829659.612	475000.120	18.46
J133	2829676.815	474993.431	13.74
J134	2829679.997	474980.060	16.57
J135	2829668.780	474967.863	15.24
J136	2829658.308	474956.789	15.41
J137	2829647.650	474945.665	52.78
J138	2829611.089	474907.597	40.38
J139	2829587.348	474874.938	178.54
J140	2829463.677	474746.171	12.96
J141	2829450.785	474744.867	12.86
J142	2829440.202	474752.170	20.00
J143	2829428.843	474735.709	6.63
J144	2829434.301	474731.943	15.06
J145	2829436.014	474716.979	49.34
J146	2829403.979	474679.459	49.34
J147	2829374.412	474639.964	35.72
J148	2829350.264	474613.638	47.20
J149	2829326.223	474573.023	47.20
J150	2829304.697	474531.020	28.98
J151	2829331.920	474521.087	22.20
J152	2829352.774	474513.478	0.61
J1	2829352.564	474512.903	

S=121866.09 平方米 合182.7991亩
注：界址点间的边长为两点间直线距离
红线图上为部分界址点

界址点坐标表

点号	X	Y	边长(m)
J31	2829819.662	475085.505	23.40
J32	2829831.722	475105.557	40.41
J33	2829847.164	475142.906	109.21
J34	2829900.482	475238.219	7.28
J35	2829903.948	475244.622	109.21
J36	2829954.615	475341.371	13.95
J37	2829967.811	475345.886	5.20
J38	2829972.506	475343.645	5.20
J39	2829977.186	475341.374	16.00
J40	2829984.219	475355.745	4.20
J41	2829980.446	475357.579	1.40
J42	2829979.186	475358.186	4.20
J43	2829975.401	475359.995	14.27
J44	2829970.731	475373.477	58.69
J45	2829996.469	475426.218	58.69
J46	2830021.472	475479.311	35.48
J47	2830041.054	475508.900	57.36
J48	2830064.340	475561.315	7.17
J49	2830067.200	475567.889	57.36
J50	2830089.683	475620.654	20.25
J51	2830108.274	475628.680	9.85
J52	2830117.527	475625.291	0.90
J53	2830118.371	475624.992	9.85
J54	2830127.692	475621.794	43.50
J55	2830141.417	475663.072	

界址点坐标表

点号	X	Y	边长(m)
J55	2830141.417	475663.072	8.76
J56	2830133.131	475665.912	8.76
J57	2830124.898	475668.903	19.92
J58	2830116.807	475687.110	65.51
J59	2830140.573	475748.153	65.51
J60	2830163.390	475809.558	138.94
J61	2830210.774	475940.172	26.61
J62	2830235.377	475950.311	22.26
J63	2830255.507	475940.812	51.00
J64	2830277.272	475986.935	25.81
J65	2830253.931	475997.949	30.98
J66	2830242.126	476026.593	90.55
J67	2830273.005	476111.710	35.43
J68	2830279.771	476146.489	132.36
J69	2830324.911	476270.916	15.02
J70	2830338.892	476276.395	7.05
J71	2830345.163	476273.163	22.00
J72	2830355.241	476292.720	12.45
J73	2830344.172	476298.423	13.21
J74	2830339.352	476310.723	83.20
J75	2830367.725	476388.931	35.43
J76	2830384.831	476419.957	112.82
J77	2830423.305	476526.009	51.00
J78	2830375.362	476543.402	79.05
J79	2830348.404	476469.092	35.43
J80	2830341.638	476434.315	109.25
J81	2830304.380	476331.612	15.02
J82	2830290.398	476326.133	7.05
J83	2830284.127	476329.365	

界址点坐标表

点号	X	Y	边长(m)
J83	2830284.127	476329.365	22.00
J84	2830274.050	476309.809	12.45
J85	2830285.119	476304.105	13.21
J86	2830289.938	476291.805	111.52
J87	2830251.906	476186.969	35.43
J88	2830234.799	476155.942	115.55
J89	2830195.394	476047.323	26.61
J90	2830170.791	476037.183	22.26
J91	2830150.661	476046.682	51.00
J92	2830128.896	476000.560	25.81
J93	2830152.236	475989.545	30.98
J94	2830164.042	475960.901	142.49
J95	2830115.447	475826.951	62.11
J96	2830093.831	475768.721	62.11
J97	2830071.350	475710.819	22.24
J98	2830050.316	475703.585	6.46
J99	2830044.768	475706.885	0.81
J100	2830044.077	475707.303	6.46
J101	2830038.579	475710.687	43.50
J102	2830015.528	475673.797	12.54
J103	2830026.245	475667.278	0.90
J104	2830027.016	475666.822	12.54
J105	2830037.898	475660.581	18.30
J106	2830043.865	475643.284	47.99
J107	2830025.134	475599.103	47.99
J108	2830005.897	475555.140	35.42
J109	2829996.567	475520.968	69.95
J110	2829967.091	475457.533	6.99
J111	2829964.085	475451.216	69.95
J112	2829933.447	475388.334	13.50
J113	2829920.850	475383.477	11.36
J114	2829910.271	475387.617	16.00
J115	2829904.440	475372.718	8.00
J116	2829911.890	475369.802	14.81
J117	2829917.160	475355.957	

测绘单位：福州市勘测院平潭分院

2010年7月数字化成图
CGCS2000坐标系，3度分带高斯投影，中央经线120度
1985国家高程基准
2009年福州基础地理信息数据图式
加盖福州市勘测院地形图蓝章，方为正式材料

1:5000