


2022-07-11

鹿原北路（君山路-民主路）选址红线图

测绘单位：福州市勘测院平潭分院

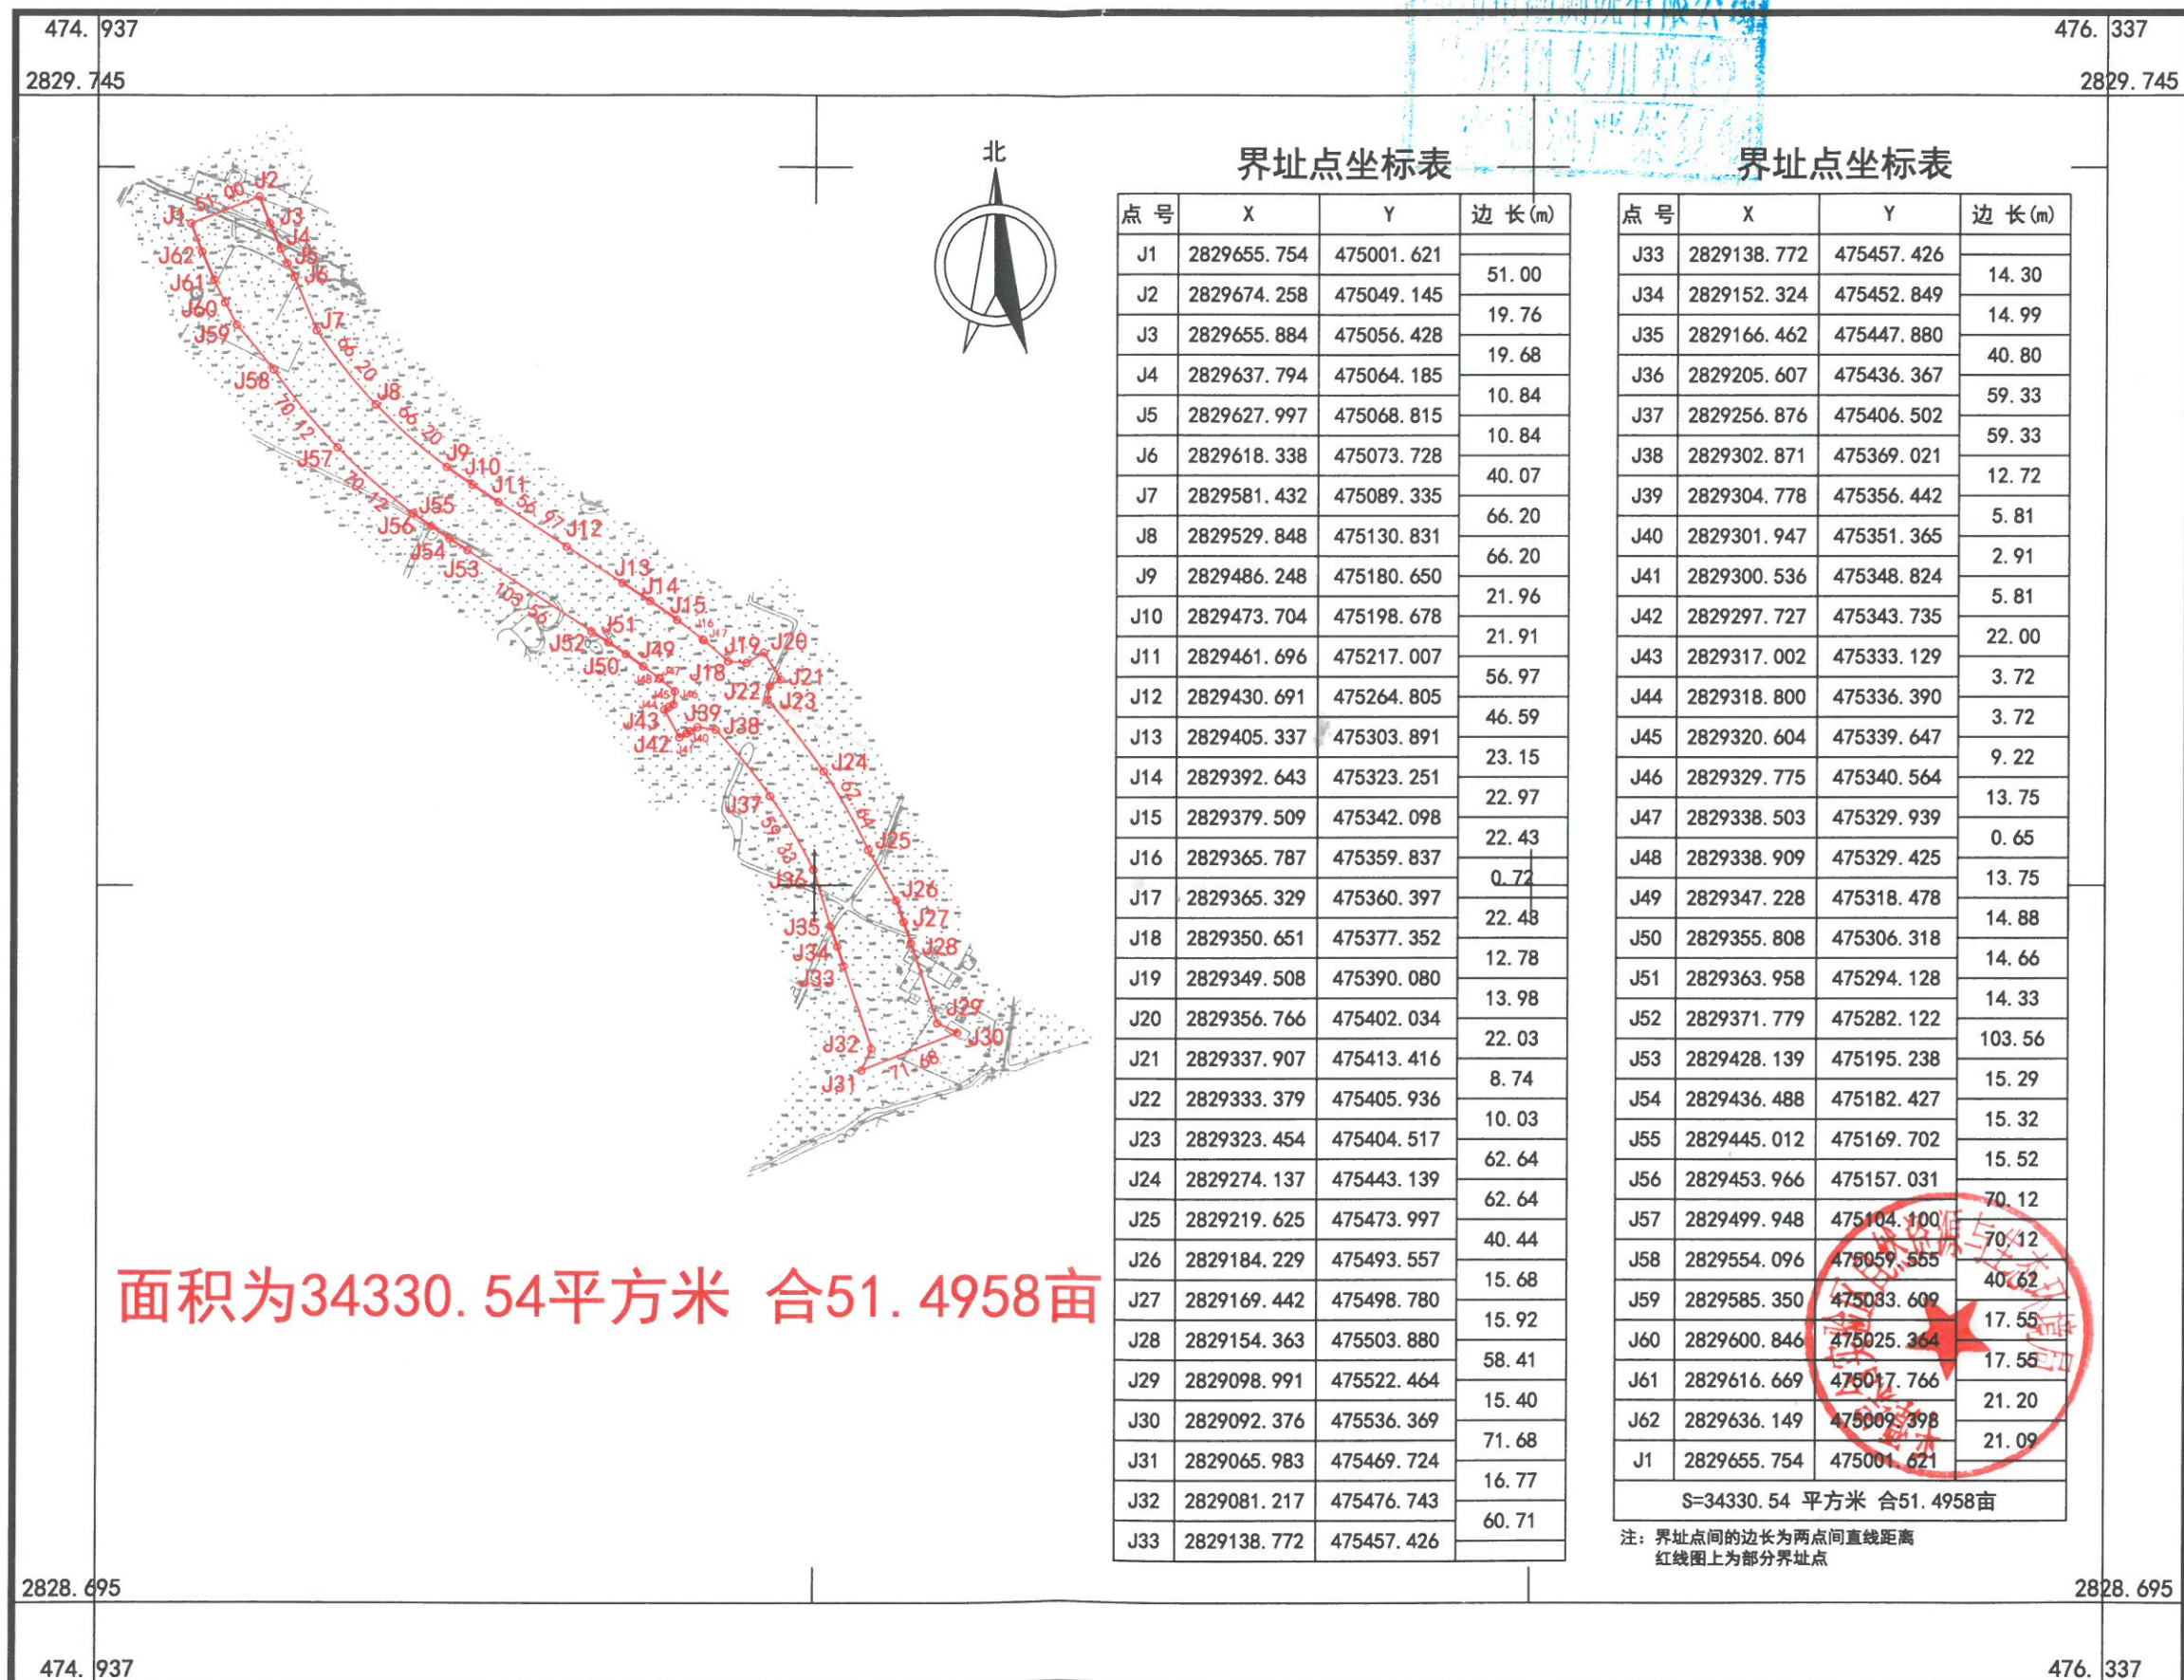

界址点坐标表

点号	X	Y	边长(m)
J1	2829655.754	475001.621	51.00
J2	2829674.258	475049.145	19.76
J3	2829655.884	475056.428	19.68
J4	2829637.794	475064.185	10.84
J5	2829627.997	475068.815	10.84
J6	2829618.338	475073.728	40.07
J7	2829581.432	475089.335	66.20
J8	2829529.848	475130.831	66.20
J9	2829486.248	475180.650	21.96
J10	2829473.704	475198.678	21.91
J11	2829461.696	475217.007	56.97
J12	2829430.691	475264.805	46.59
J13	2829405.337	475303.891	23.15
J14	2829392.643	475323.251	22.97
J15	2829379.509	475342.098	22.43
J16	2829365.787	475359.837	0.72
J17	2829365.329	475360.397	22.48
J18	2829350.651	475377.352	12.78
J19	2829349.508	475390.080	13.98
J20	2829356.766	475402.034	22.03
J21	2829337.907	475413.416	8.74
J22	2829333.379	475405.936	10.03
J23	2829323.454	475404.517	62.64
J24	2829274.137	475443.139	62.64
J25	2829219.625	475473.997	40.44
J26	2829184.229	475493.557	15.68
J27	2829169.442	475498.780	15.92
J28	2829154.363	475503.880	58.41
J29	2829098.991	475522.464	15.40
J30	2829092.376	475536.369	71.68
J31	2829065.983	475469.724	16.77
J32	2829081.217	475476.743	60.71
J33	2829138.772	475457.426	

界址点坐标表

点号	X	Y	边长(m)
J33	2829138.772	475457.426	14.30
J34	2829152.324	475452.849	14.99
J35	2829166.462	475447.880	40.80
J36	2829205.607	475436.367	59.33
J37	2829256.876	475406.502	59.33
J38	2829302.871	475369.021	12.72
J39	2829304.778	475356.442	5.81
J40	2829301.947	475351.365	2.91
J41	2829300.536	475348.824	5.81
J42	2829297.727	475343.735	22.00
J43	2829317.002	475333.129	3.72
J44	2829318.800	475336.390	3.72
J45	2829320.604	475339.647	9.22
J46	2829329.775	475340.564	13.75
J47	2829338.503	475329.939	0.65
J48	2829338.909	475329.425	13.75
J49	2829347.228	475318.478	14.88
J50	2829355.808	475306.318	14.66
J51	2829363.958	475294.128	14.33
J52	2829371.779	475282.122	103.56
J53	2829428.139	475195.238	15.29
J54	2829436.488	475182.427	15.32
J55	2829445.012	475169.702	15.52
J56	2829453.966	475157.031	70.12
J57	2829499.948	475104.100	70.12
J58	2829554.096	475059.555	40.62
J59	2829585.350	475033.609	17.55
J60	2829600.846	475025.364	17.55
J61	2829616.669	475017.766	21.20
J62	2829636.149	475009.398	21.09
J1	2829655.754	475001.621	

S=34330.54 平方米 合51.4958亩

注：界址点间的边长为两点间直线距离
红线图上为部分界址点

2010年7月数字化成图

CGCS2000坐标系，3度分带高斯投影，中央经线120度

1985国家高程基准

2009年福州基础地理信息数据图式

加盖福州市勘测院地形图蓝章，方为正式材料

1:5000