


➤ 管控边界划定

磹报村管控边界划定一览表


管控边界类型		面积 (公顷)	占村域面积比例 (%)
生态空间		0.28	1.69%
其中	生态保护红线	0	0
	一般生态空间	0.28	1.69%
农业空间		5.57	33.87%
其中	永久基本农田	5.08	30.90%
	一般农业空间	0.49	2.98%
建设空间		10.60	64.45%
其中	村庄集中建设区	7.59	46.14%
	村庄弹性发展区	0.27	1.46%
	其他（区域基础设施及其他建设用地）	1.82	11.04%
	城镇用地	1.19	7.26%

- 永久基本农田
- 生态保护红线
- 一般生态空间
- 一般农业空间
- 村庄集中建设区
- 村庄弹性发展区
- 城镇空间
- 其他
- 村庄建设边界

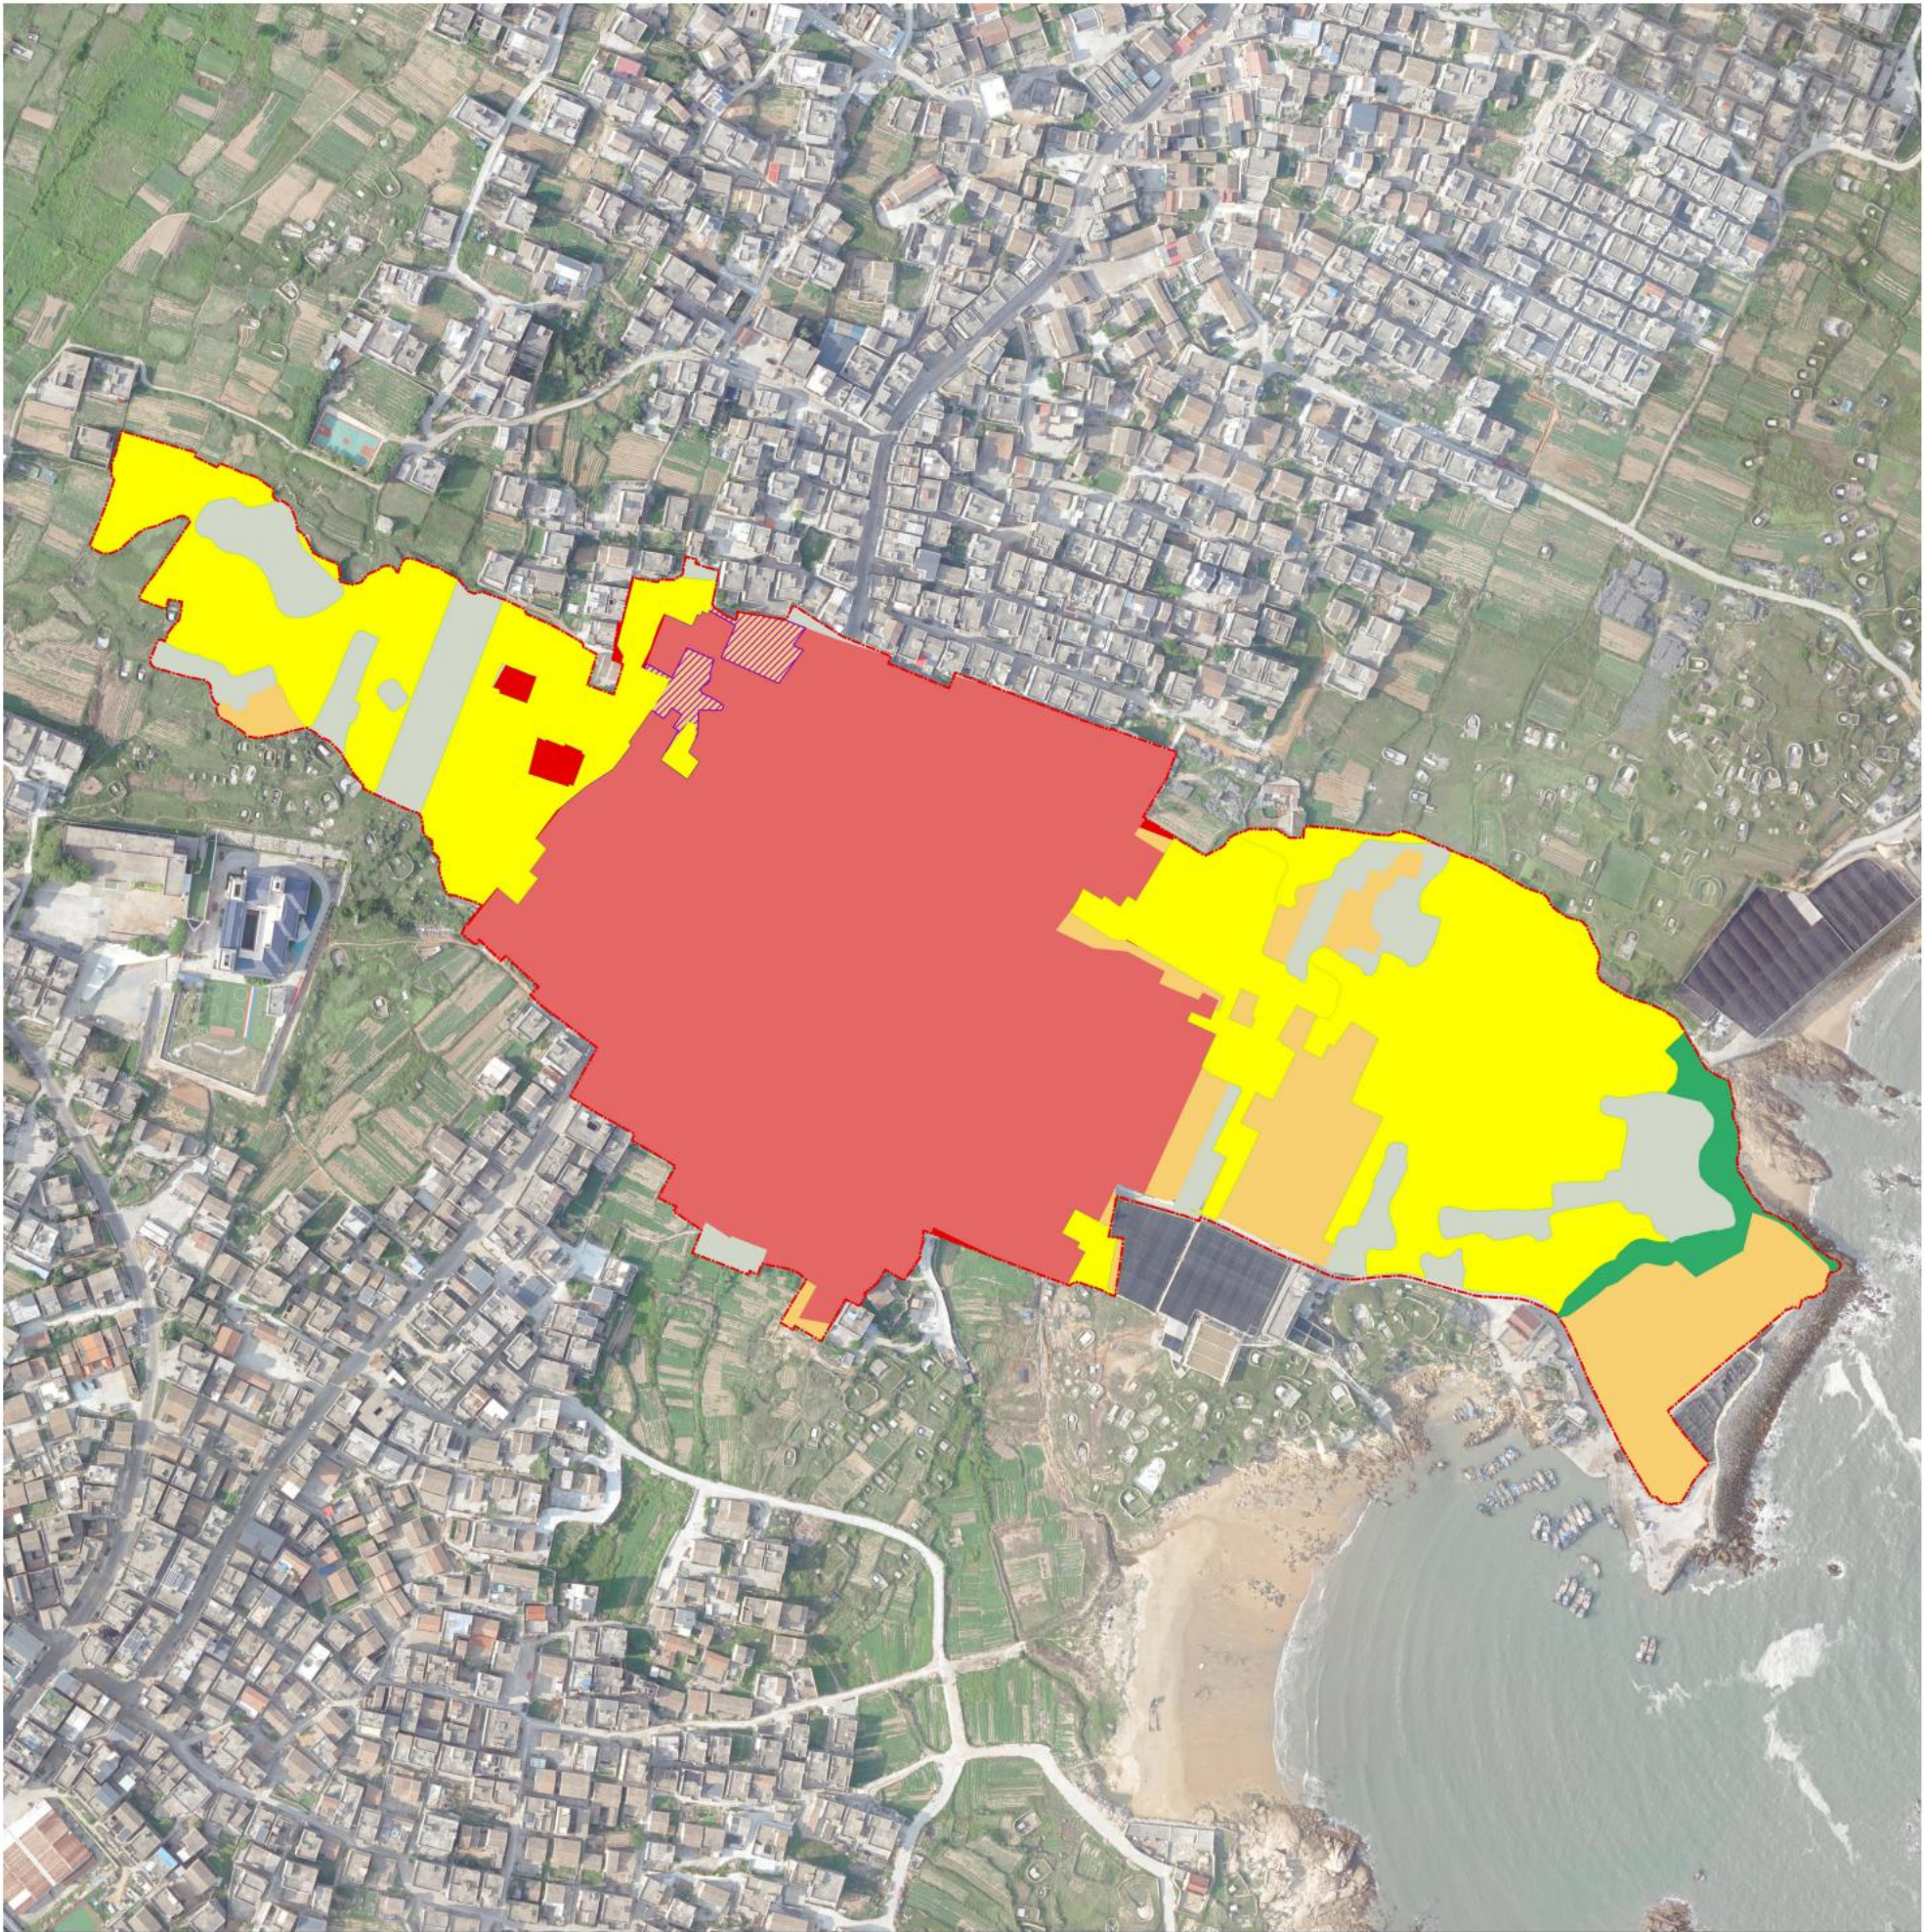


总体开发保护格局

村域综合规划

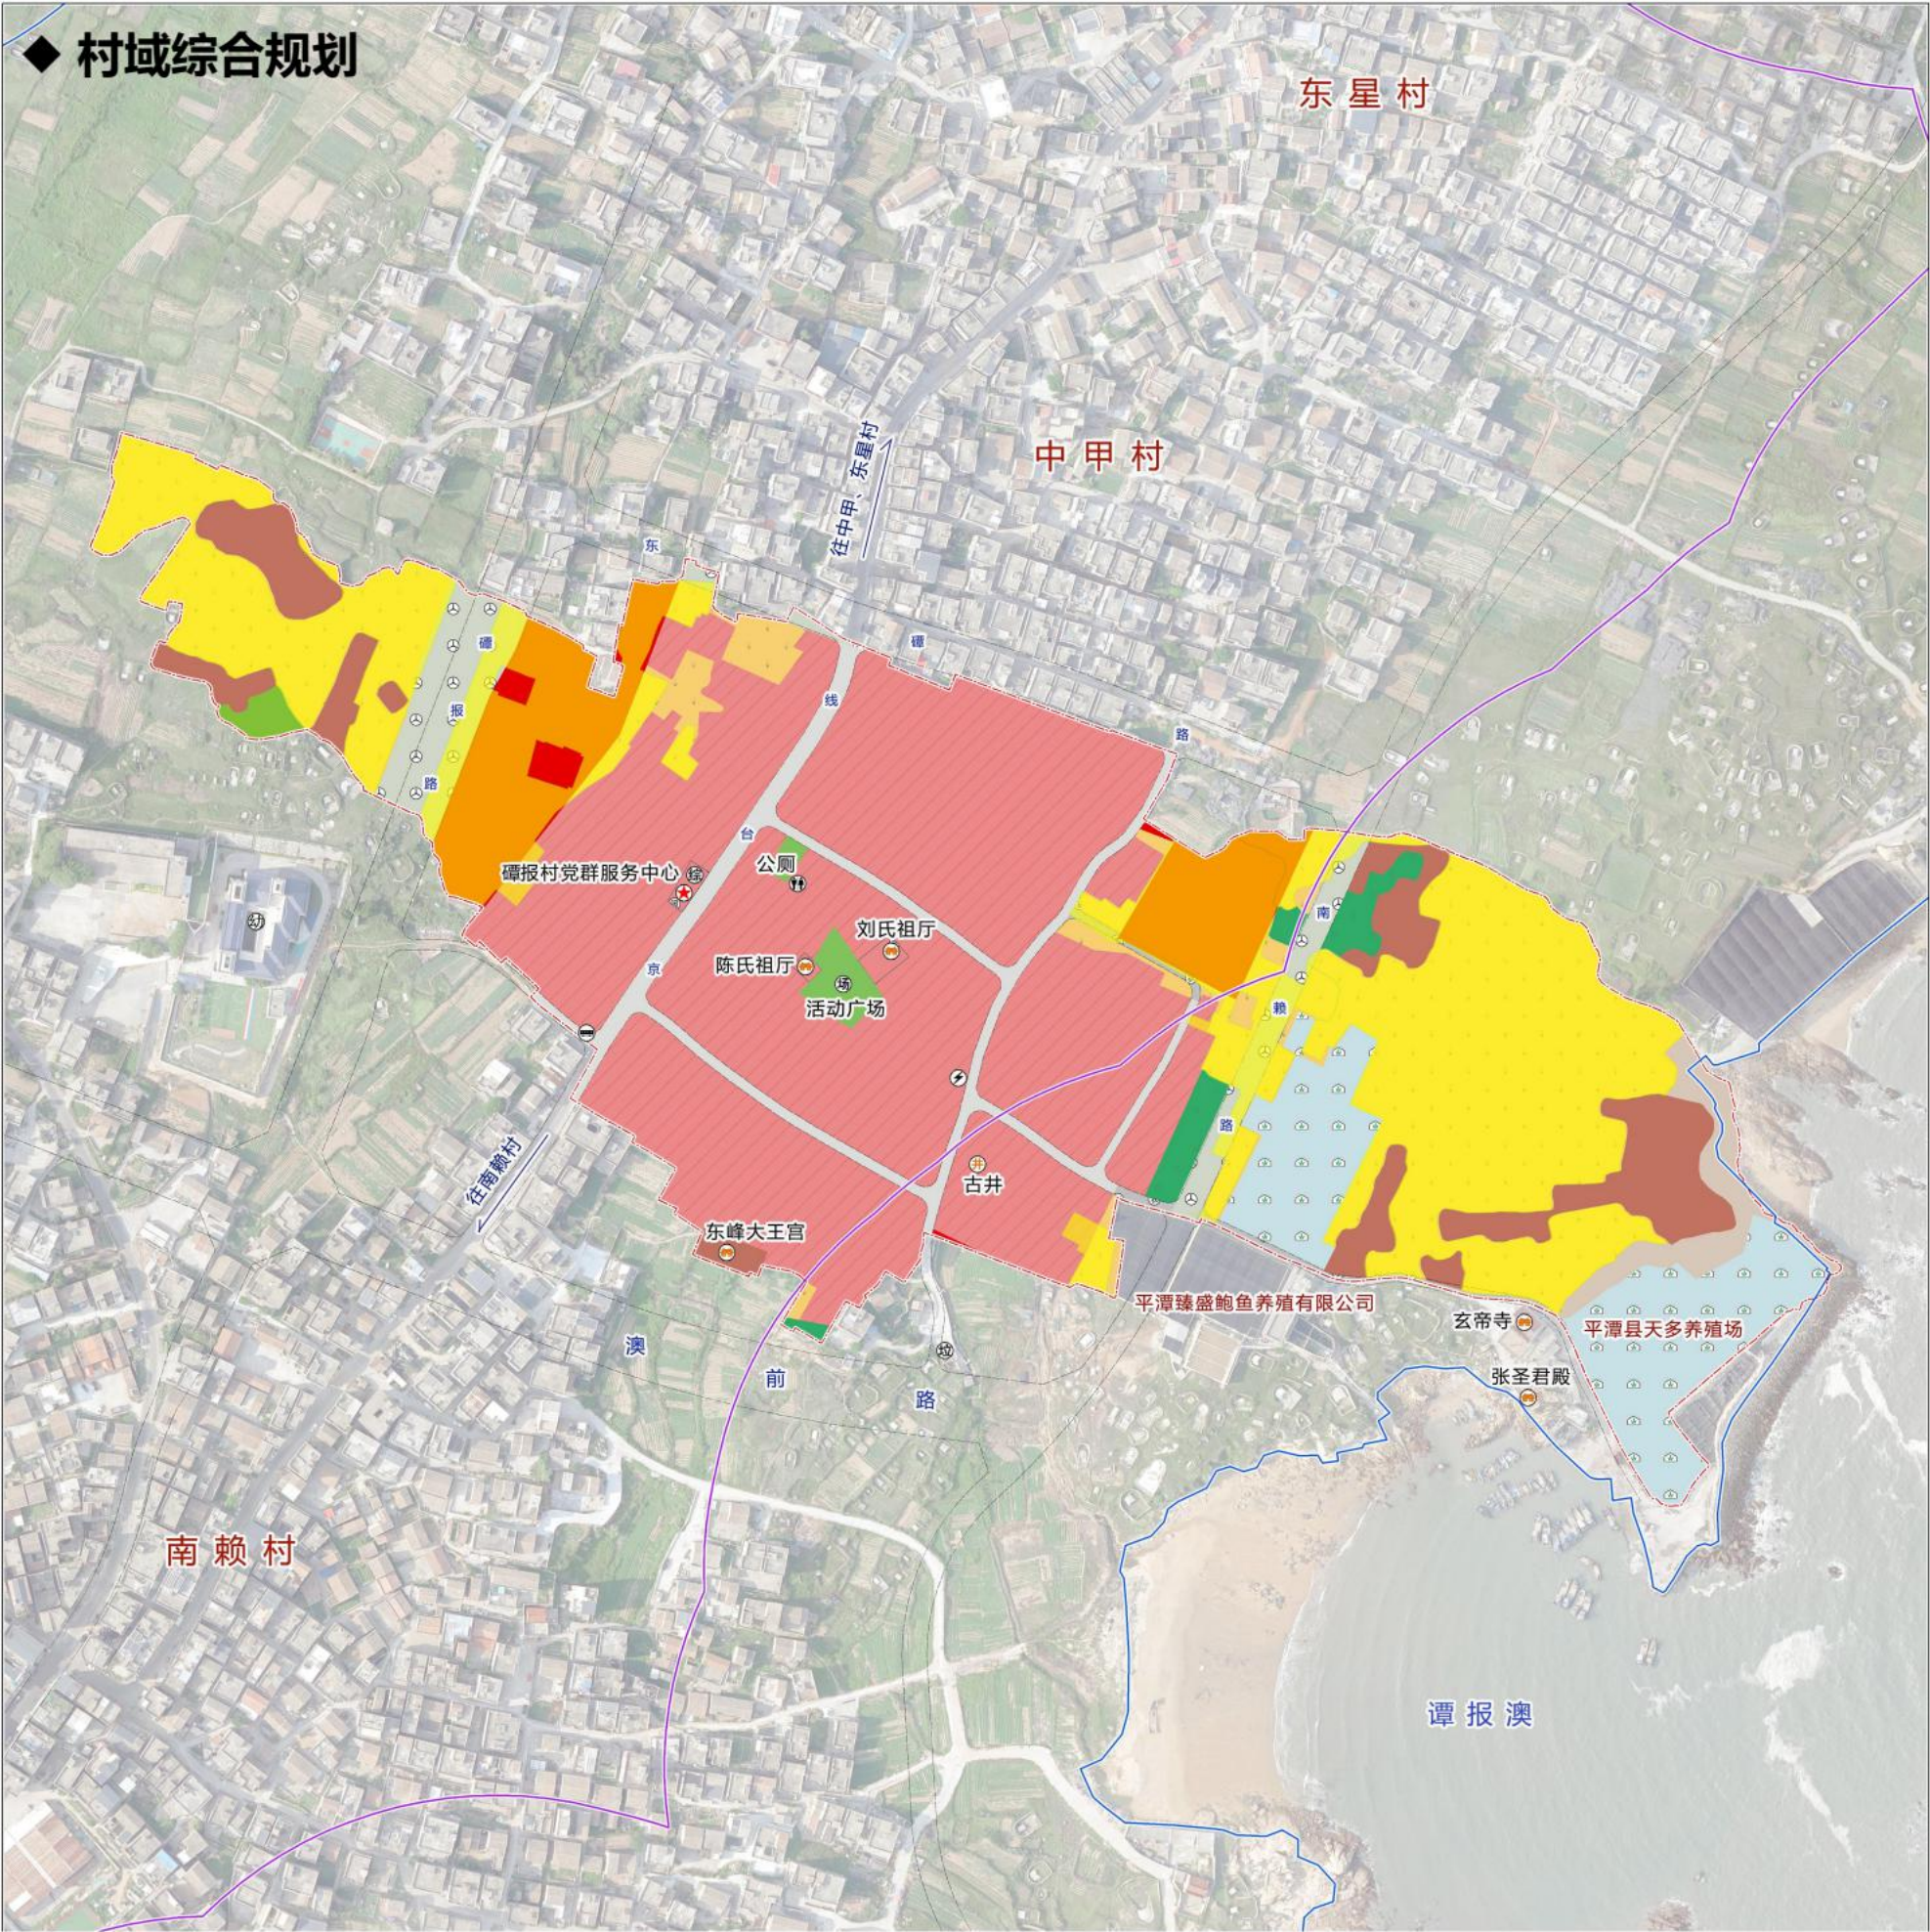


风玫瑰与比例尺

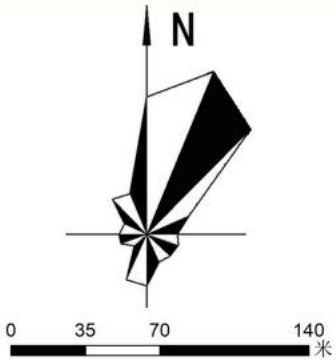

区位图



图例

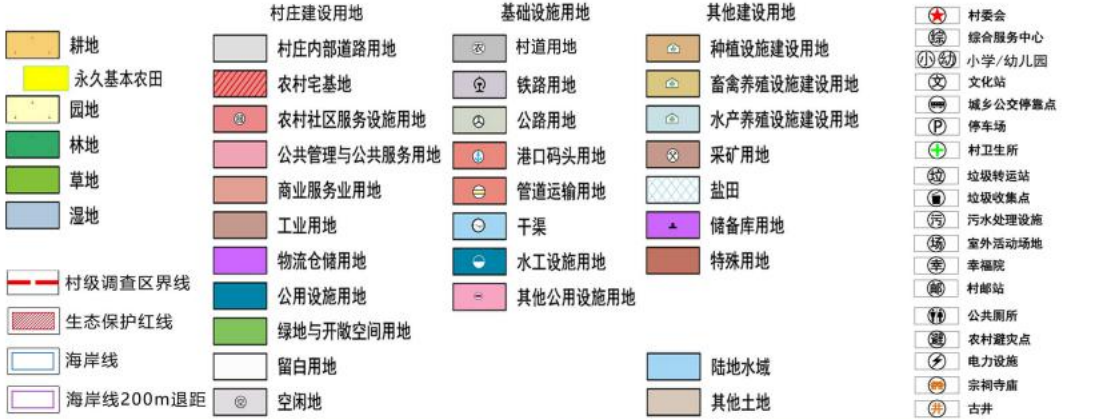

空间功能结构调整表

用地用海类型				规划基期年		规划目标年		用地调整（公顷）	
				面积（公顷）	比重（%）	面积（公顷）	比重（%）		
耕地（01）				5.70	34.66	3.94	23.98	-1.76	
园地（02）				0.00	0.00	0.00	0.00	0.00	
林地（03）				0.15	0.94	0.22	1.36	0.07	
草地（04）				0.06	0.37	0.06	0.37	0.00	
湿地（05）				0.00	0.00	0.00	0.00	0.00	
合计				5.91	35.97	4.23	25.71	-1.69	
农业设施建设用地	村道用地			0.05	0.31	0.08	0.51	0.03	
	种植设施建设用地			0.00	0.00	0.00	0.00	0.00	
	畜禽养殖设施建设用地			0.00	0.00	0.00	0.00	0.00	
	水产养殖设施建设用地			1.19	7.24	1.26	7.64	0.07	
合计				1.24	7.56	1.34	8.16	0.10	
村域建设用地	村域城乡建设用地	城镇用地		0.00	0.00	1.19	7.26	1.19	
		村庄建设用地	居住用地	农村社区服务设施用地	0.00	0.00	0.06	0.37	0.06
				农村宅基地	7.13	43.34	6.81	41.43	-0.31
				公共管理与公共服务用地	0.12	0.75	0.00	0.00	-0.12
			商业服务业用地	0.00	0.00	0.00	0.00	0.00	
			工业用地	0.00	0.00	0.00	0.00	0.00	
			仓储用地	0.00	0.00	0.00	0.00	0.00	
			村庄内部道路用地	0.51	3.12	0.60	3.62	0.08	
			交通场站用地	0.00	0.00	0.00	0.00	0.00	
			其他交通设施用地	0.00	0.00	0.00	0.00	0.00	
			公用设施用地	0.00	0.00	0.00	0.00	0.00	
			绿地与开敞空间用地	0.00	0.00	0.12	0.72	0.12	
			留白用地	0.00	0.00	0.00	0.00	0.00	
			空闲地	0.00	0.00	0.00	0.00	0.00	
	合计		7.76	47.20	7.59	46.14	-0.18		
	合计		7.76	47.20	8.78	53.40	1.02		
	区域基础设施用地		0.00	0.00	0.70	4.28	0.70		
	其他建设用地		1.18	7.16	1.11	6.76	-0.07		
	合计		8.94	54.37	10.60	64.45	1.66		
	陆地水域		0.00	0.00	0.00	0.00	0.00		
渔业用海		0.00	0.00	0.00	0.00	0.00			
工矿通信用海		0.00	0.00	0.00	0.00	0.00			
交通运输用海		0.00	0.00	0.00	0.00	0.00			
游憩用海		0.00	0.00	0.00	0.00	0.00			
特殊用海		0.00	0.00	0.00	0.00	0.00			
其他土地		0.35	2.11	0.28	1.69	-0.07			
其他海域		0.00	0.00	0.00	0.00	0.00			
总计		16.44	100.00	16.44	100.00	0.00			

指标一览表

用地用海类型				规划基期年		规划目标年		用地调整（公顷）
				面积（公顷）	比重（%）	面积（公顷）	比重（%）	
耕地（01）				5.70	34.66	3.94	23.98	-1.76
园地（02）				0.00	0.00	0.00	0.00	0.00
林地（03）				0.15	0.94	0.22	1.36	0.07
草地（04）				0.06	0.37	0.06	0.37	0.00
湿地（05）				0.00	0.00	0.00	0.00	0.00
合计				5.91	35.97	4.23	25.71	-1.69
农业设施建设用地	村道用地			0.05	0.31	0.08	0.51	0.03
	种植设施建设用地			0.00	0.00	0.00	0.00	0.00
	畜禽养殖设施建设用地			0.00	0.00	0.00	0.00	0.00
	水产养殖设施建设用地			1.19	7.24	1.26	7.64	0.07
合计				1.24	7.56	1.34	8.16	0.10
村域建设用地	村域城乡建设用地	城镇用地		0.00	0.00	1.19	7.26	1.19
		居住用地	农村社区服务设施用地	0.00	0.00	0.06	0.37	0.06
			农村宅基地	7.13	43.34	6.81	41.43	-0.31
		公共管理与公共服务用地		0.12	0.75	0.00	0.00	-0.12
		商业服务业用地		0.00	0.00	0.00	0.00	0.00
		工业用地		0.00	0.00	0.00	0.00	0.00
		仓储用地		0.00	0.00	0.00	0.00	0.00
		村庄内部道路用地		0.51	3.12	0.60	3.62	0.08
		交通场站用地		0.00	0.00	0.00	0.00	0.00
		其他交通设施用地		0.00	0.00	0.00	0.00	0.00
		公用设施用地		0.00	0.00	0.00	0.00	0.00
		绿地与开敞空间用地		0.00	0.00	0.12	0.72	0.12
		留白用地		0.00	0.00	0.00	0.00	0.00
		空闲地		0.00	0.00	0.00	0.00	0.00
		合计		7.76	47.20	7.59	46.14	-0.18
		合计		7.76	47.20	8.78	53.40	1.02
		区域基础设施用地		0.00	0.00	0.70	4.28	0.70
	其他建设用地		1.18	7.16	1.11	6.76	-0.07	
合计				8.94	54.37	10.60	64.45	1.66
陆地水域				0.00	0.00	0.00	0.00	0.00
渔业用海				0.00	0.00	0.00	0.00	0.00
工矿通信用海				0.00	0.00	0.00	0.00	0.00
交通运输用海				0.00	0.00	0.00	0.00	0.00
游憩用海				0.00	0.00	0.00	0.00	0.00
特殊用海				0.00	0.00	0.00	0.00	0.00
其他土地				0.35	2.11	0.28	1.69	-0.07
其他海域				0.00	0.00	0.00	0.00	0.00
总计				16.44	100.00	16.44	100.00	0.00

序号	指标	属性	单位	现状基期年	规划目标年	备注
一、村庄发展性指标						
1	村域建设用地总面积	约束性	公顷	8.94	10.60	
2	村域城乡建设用地面积	约束性	公顷	7.76	8.78	
3	村庄建设用地规模	预期性	公顷	7.76	7.59	
4	公共管理与公共服务用地规模	预期性	公顷	0.12	0.00	
5	公用设施用地规模	预期性	公顷	0.00	0.00	
6	人均村庄建设用地面积	预期性	平方米/人	57.20	65.97	
二、村庄保护性指标						
7	生态保护红线面积	约束性	公顷	0.00	0.00	
8	永久基本农田保护面积	约束性	公顷	5.08	5.08	
9	耕地保有量	约束性	公顷	5.70	3.94	
10	林地保有量	约束性	公顷	0.15	0.22	
11	湿地面积	约束性	公顷	0.00	0.00	
12	大陆自然海岸线保有率	约束性	%	85.00	95.00	
13	自然和文化遗产	预期性	处	0	0	

主要农村居民点总平面示意图



平潭综合实验区海坛片区磡报村村庄规划（2022-2035）
VILLAGE PLANNING OF TANBAO VILLAGE, PINGTAN TOWN



建设方案指引



村民建房应当遵守以下技术标准规定：

(一) 规划：村民建房要符合国土空间总体规划及各类专项规划，靠近城市、县城、乡镇所在地住宅小区，引导参照城市居住区规划设计相关标准，鼓励建设多层单元式住宅。

(二) 选址：村民建房选址应避免地质复杂、地基承载力差、地势低洼不易排涝以及易受风口、滑坡、雷电和洪水侵袭等自然灾害影响的地段，杜绝安全隐患问题。

(三) 层数和面积：农村独栋式、并联式或联排式自建住宅不得超过三层，每户住宅建筑面积控制在300平方米以内；多层单元式住宅的，每户住宅建筑面积控制在200平方米左右。

(四) 层高：一层层高控制在4.5米以内，二层以上层高控制在3.3米以内，建筑总高度不超过12米，建筑屋顶原则上应按坡屋顶设计。

(五) 间距和朝向：住宅建筑前后间距与建筑高度比一般不低于1:1，相邻房屋山墙之间（外墙至外墙）的间距不低于4米，建筑宜朝南、朝南偏东或偏西布置。新建建筑宜后退村庄干路红线3米以上，后退村庄支路红线1米以上。

因旧房改造、扩建等受用地条件限制的，根据实际情况由属地乡镇人民政府合理确定相邻距离。

(六) 抗震：新建住宅必须符合工程抗震设防要求，板、梁、柱不得采用石结构。


(七) 建筑单体：应满足村民生产生活需求，住宅平面布局应设有客厅、卧室、厨房、卫生间、储藏间（农具堆放间）应满足面积、通风、采光等要求。房屋造型简洁美观，宜采用坡屋面，符合地方建筑特色，外观应进行一次性装修。

(八) 配套：应同步配建化粪池等处理设施；集中建设住宅小区的，给排水、电力通信、道路、广电、绿化和社区服务等配套设施要同步规划建设，小区建筑密度控制在30%左右，绿地率不低于30%。


其他细则参考《福州市规范农村宅基地和建房管理实施细则（试行）》。

农村居民点规划布局图

平潭综合实验区海坛片区**磹报村**村庄规划（2022-2035）
VILLAGE PLANNING OF TANBAO VILLAGE, PINGTAN TOWN

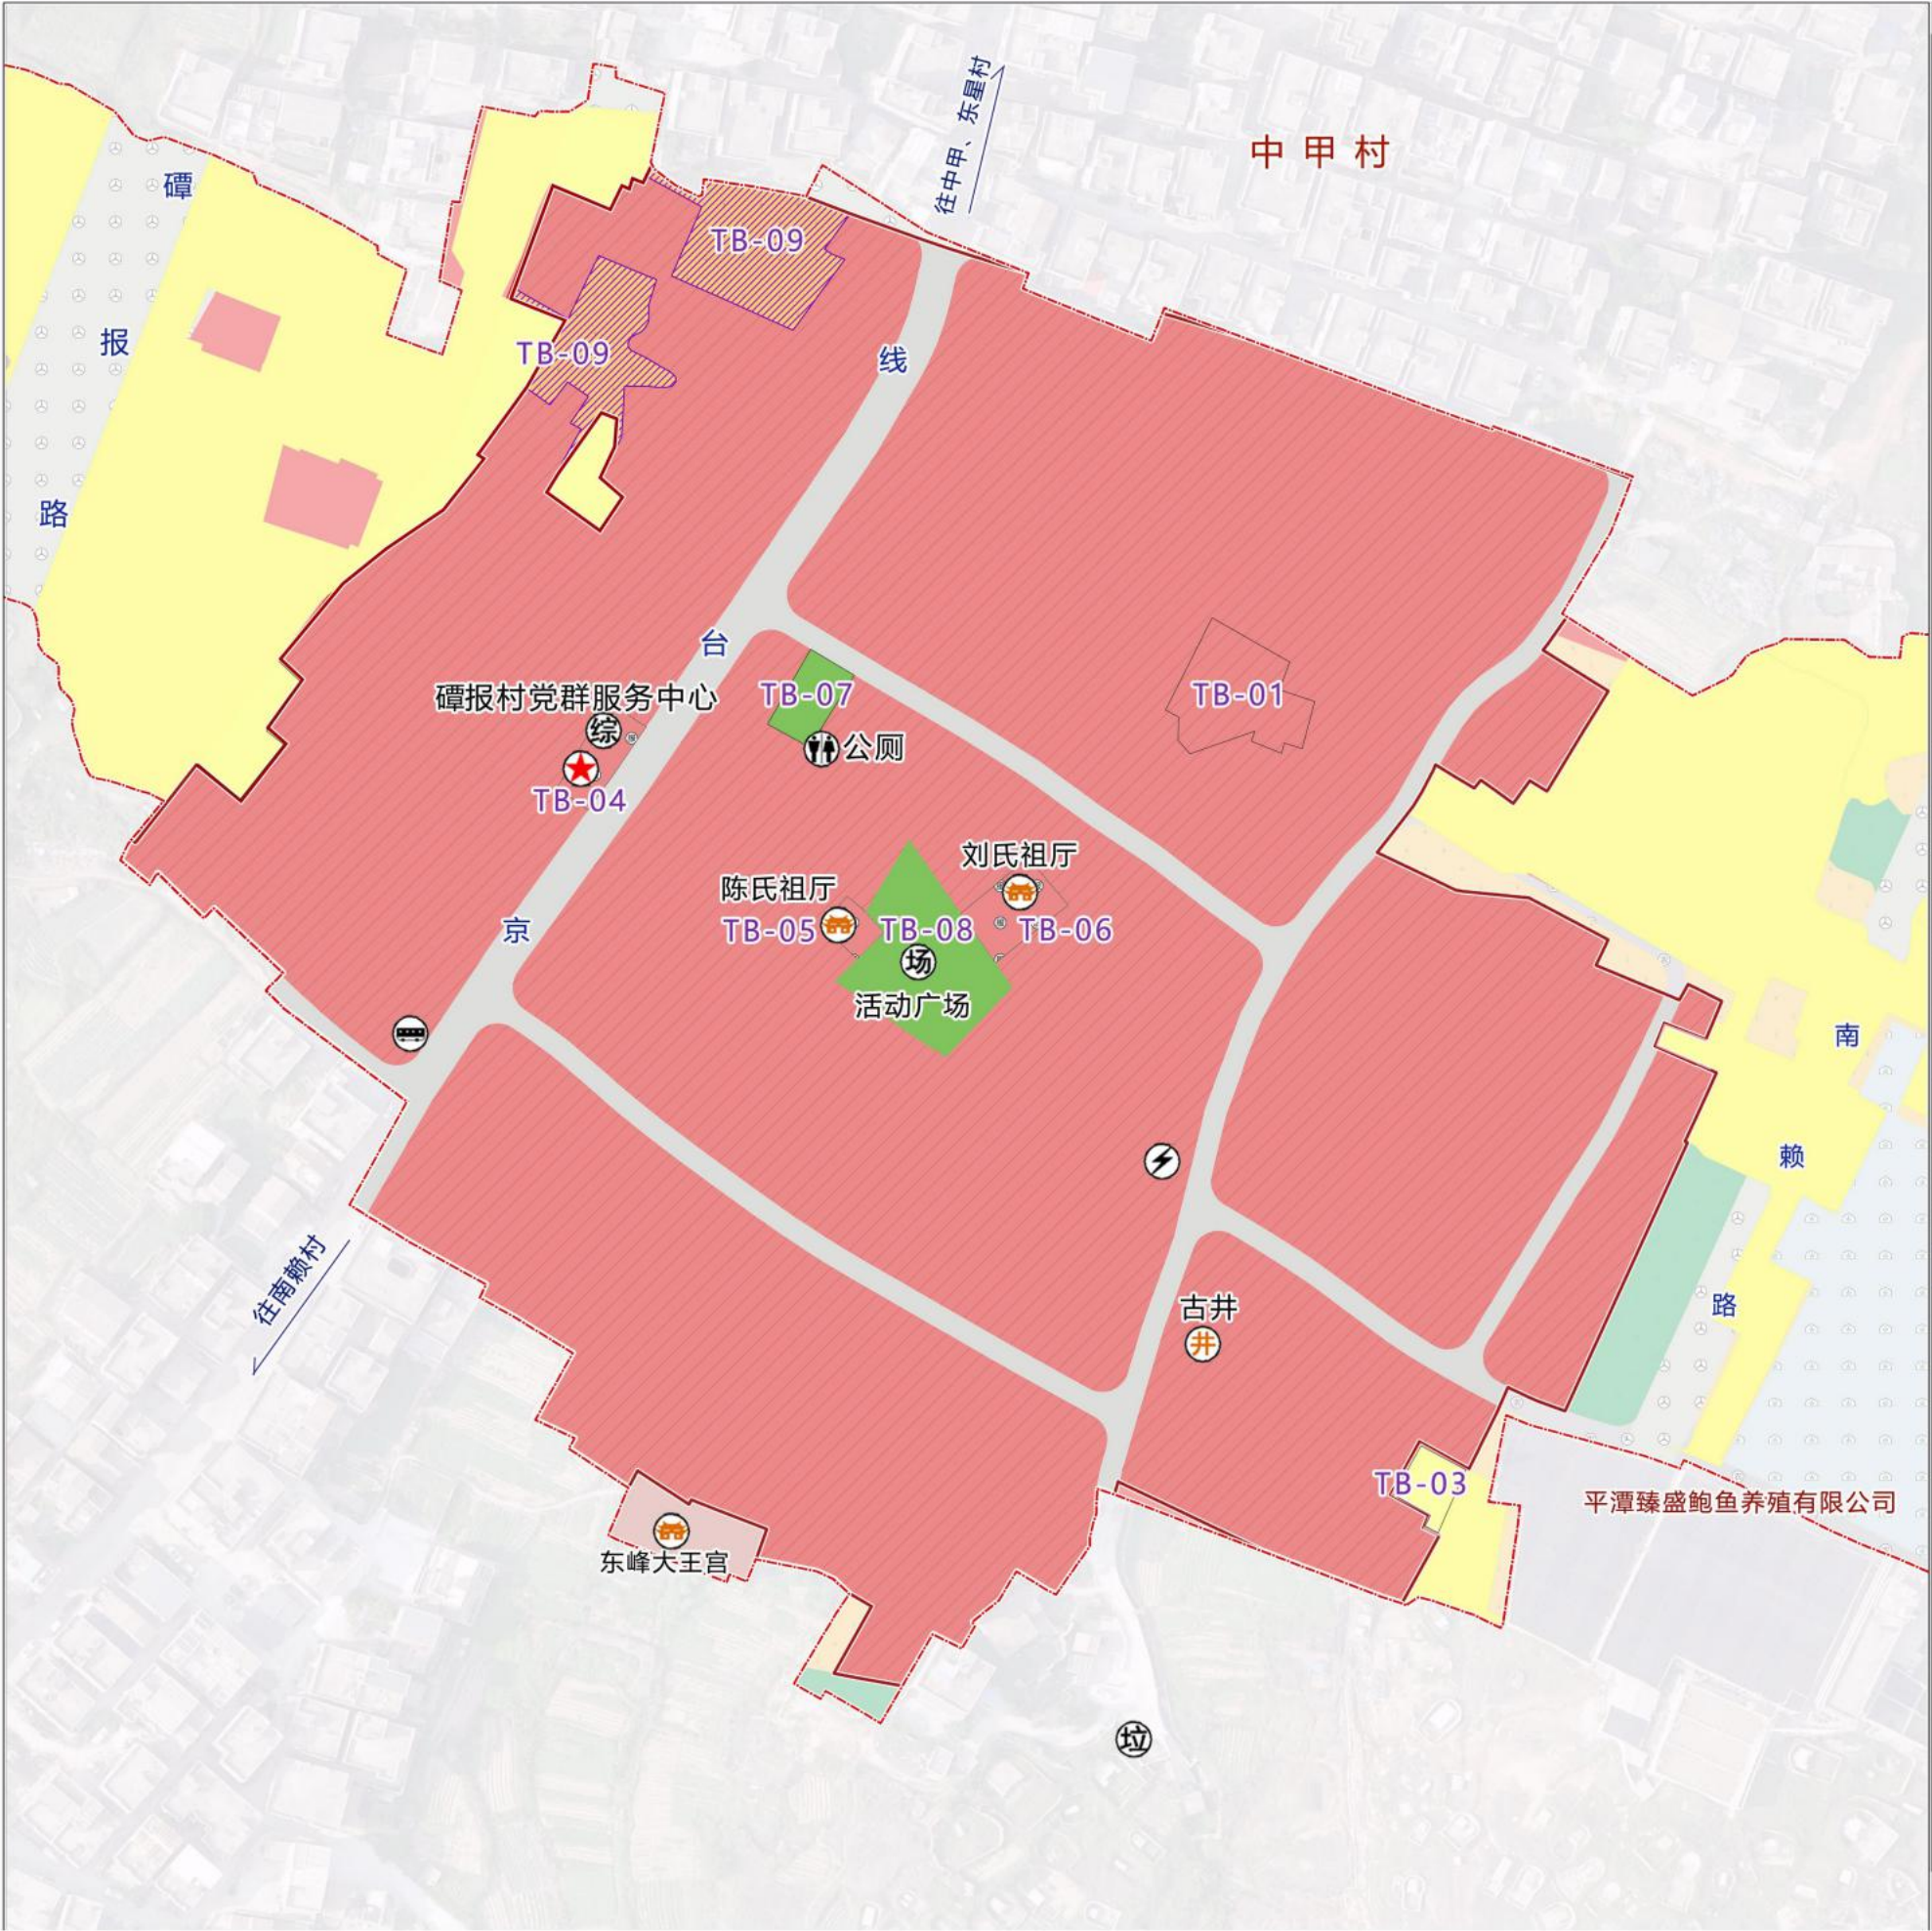

风玫瑰与比例尺

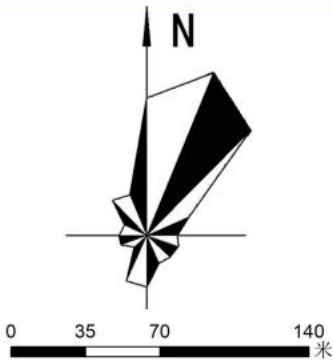

区位图



图例



指标一览表

地块编号	用地			户数		建筑高度 (m)	名称	备注
	用地代码	用地性质	地块面积 (m2)	现状户数	规划户数			
TB-01	0703	农村宅基地	600	0	3	3.0F, 14m以内	零星新建建筑	村庄居民点住宅建筑以保留及改造为主, 原则上不大量新增宅基地; 新建宅基地应优先利用村内空闲地、闲置宅基地和未利用地, 引导村民节约使用土地, 尽量不占耕地。村内零星新建建筑12户。
TB-02	0703	农村宅基地	200	0	1	3.0F, 14m以内		
TB-03	0703	农村宅基地	180	0	1	3.0F, 14m以内		
TB-04	0704	农村社区服务设施用地	220	0	0	3.0F, 12m以内	党群服务中心	依托现状村委大楼, 建成党群服务中心, 并配套相关基础设施; 如便民服务中心、警务室、小型卫生所、文化活动室、阅览室等;
TB-05	0704	农村社区服务设施用地	100	0	0	1.0F, 5m以内	陈氏祖厅	现状祖厅, 保留现状地类使用功能, 远期修缮或翻新祖厅, 统一以当地的建筑风貌为主; 并对周边的环境进行整治, 适当增加绿化种植, 提升村庄整体环境。
TB-06	0704	农村社区服务设施用地	280	0	0	1.0F, 5m以内	刘氏祖厅	
TB-07	14	绿地与开敞空间用地	220	0	0	限高9m	街角广场	现状为健身器材场地, 近期延续健身器材场地的功能, 对地面进行铺装, 并适当增加配套器材, 增加景观灯、石凳、垃圾桶, 广场四周可增设绿化种植。远期根据村里需求, 可新建老年人活动中心;
TB-08	14	绿地与开敞空间用地	1000	0	0	限高9m	休闲公园、篮球场	现状为篮球场, 但较为破旧, 规划腾退周边一处破旧建筑, 平整场地, 建设休闲凉亭; 并且对周边绿化环境进行提升改造;
TB-09	-	弹性发展空间	2700	0	0	未明确	机动指标	为满足村庄远期发展的不确定性, 预留不超过25%弹性发展空间;

居民点管控规则

村庄公共服务设施：完善党群服务中心、配建文化服务中心、室内活动场地，附设村邮所、幸福院、广播室等功能。维护现状文化活动中心并增设活动设施；远期可利用街角广场新建老年人活动中心或另外选址新建老年人活动中心；附设食堂餐厅、床位等功能。

道路交通设施：对外交通主要为现状村庄主干道，村庄内部道路交通沿用村中已有的道路，在原有的基础上维护；拆除部分质量较差建筑，优化道路线行，满足道路规范要求；利用街头空闲地改建停车场。局部村道未硬化，近期建议采用柏油硬化水泥路面，并提升两侧绿化环境；

市政设施：沿道路按30-50m距离设置垃圾收集点，按服务半径约300m配建公厕，服务游客和村民；完善村庄水电配套，远期采用雨污分离排放模式，按照不大于120m的距离配建消防栓，文保单位重点设置。

村庄住宅管制：村庄居民点住宅建筑以保留及改造为主，原则上不大量新增宅基地，严禁核心保护区内开发建设村民住宅，建设控制地带内严控建设高度、体量、色彩，严格按照本次设计户型建设，风貌与村落协调一致。建筑严格按照“一户一宅”政策，每户宅基地面积控制在120㎡以内，新建住宅高度不得超过14m，每户住宅面积控制在300㎡以内，住宅建筑间距与前建筑高度比不低于1:1，相邻建筑山墙间距不低于2m，建筑宜朝南、南偏东或偏西布置，建筑后退村庄道路不得少于1m。

村民建房应当遵守相关技术标准规定，若实验区未实施农村宅基地和建房审批相关规定，可参照《福州市规范农村宅基地和建房管理实施细则（试行）》。

近期建设项目分布



近期建设项目一览表						
序号	项目类型	项目名称	项目说明	建设年限	投资额(万元)	建议资金来源
1	村容村貌提升	整合用地，零星安置建设	整合用地，村域范围内零星新建10户，村内以挖掘存量建设用地为主，建议保留原有建筑风貌，部分建筑修缮改造成民宿；	2022-2027	——	村民自筹
2		村容村貌治理	村庄主干道沿线、次干道沿线垃圾整治，整治面积2000平方米	2022-2027	10	财政出资
3		日常环卫养护	村内日常环境卫生保养，在村域南侧配置垃圾分类收集点1个。垃圾桶沿主干道每100m设置一个；	——	10	村财、村民自筹
4	生态修复国土整治	低效建设用地整治	对村内现状存在的特殊用地进行整治，主要为坟墓用地征迁，远期由政府统筹安置。	2022-2027	——	专项资金
5	产业发展	渔业科技示范基地	对现状海边鲍鱼养殖厂进行产业升级改造，发展鲍鱼牧场，打造集鲍鱼培育、养殖、鲍鱼馆观光、鲍鱼文化研学、鲍鱼壳DIY亲子文创体验、加工销售于一体的综合型渔业示范基地	2023-2027	——	村民自筹 招商引资
6		滨海休闲观光旅游度假渔村	合理充分利用潭报澳海岸线资源，开发滨海景观步道，增设观景平台；依托现状沙滩，引进系列沙滩娱乐项目，如沙滩日光浴俱乐部、沙滩排球、沙滩摩托，海上冲浪运动，沙滩摄影等	2023-2027	——	招商引资
7	公共服务设施	党群服务中心提升	综合服务中心平台场所建设、志愿服务队伍建设，便民服务中心提升，规模220平方米；	2022-2025	20	村财、 村民自筹
8		日间照料中心及文化中心	规划选址新建老年人日间照料中心，并配套完善室内文化场地，面积约150平方米。	2022-2027	50	
9		街角公园、休闲广场	结合现状广场改造提升2处室外活动场地，提升绿化及相关健身器材设施，总面积约1200平方米；	2022-2027	50	
10	市政基础设施	实施厕所革命	现状村庄有一处公厕，规划拟建一处三类标准旅游公厕，并配建垃圾是分类收集站；面积100平方米；	2022-2027	30	村财
11		停车场建设	结合路边现状空闲地，平整土地，作为临时社会公共停车场地，供游客临时停车使用，面积约500平方米；	2022-2025	10	村财、村民自筹
12	历史文化保护	历史风貌建筑	村内部分传历史风貌建筑整治修缮，活化传统建筑改造成特色民宿；	2022-2025	——	招商引资
13		宗祠、寺庙	宗祠、祖厅、寺庙周边环境整治提升，增加绿植、健身器材设施、垃圾桶、民俗、宗教文化宣传栏等；	2022-2025	10	专项资金
合计					190	