


全域土地利用现状

人均农村居民点建设用地 68.84 m²/人

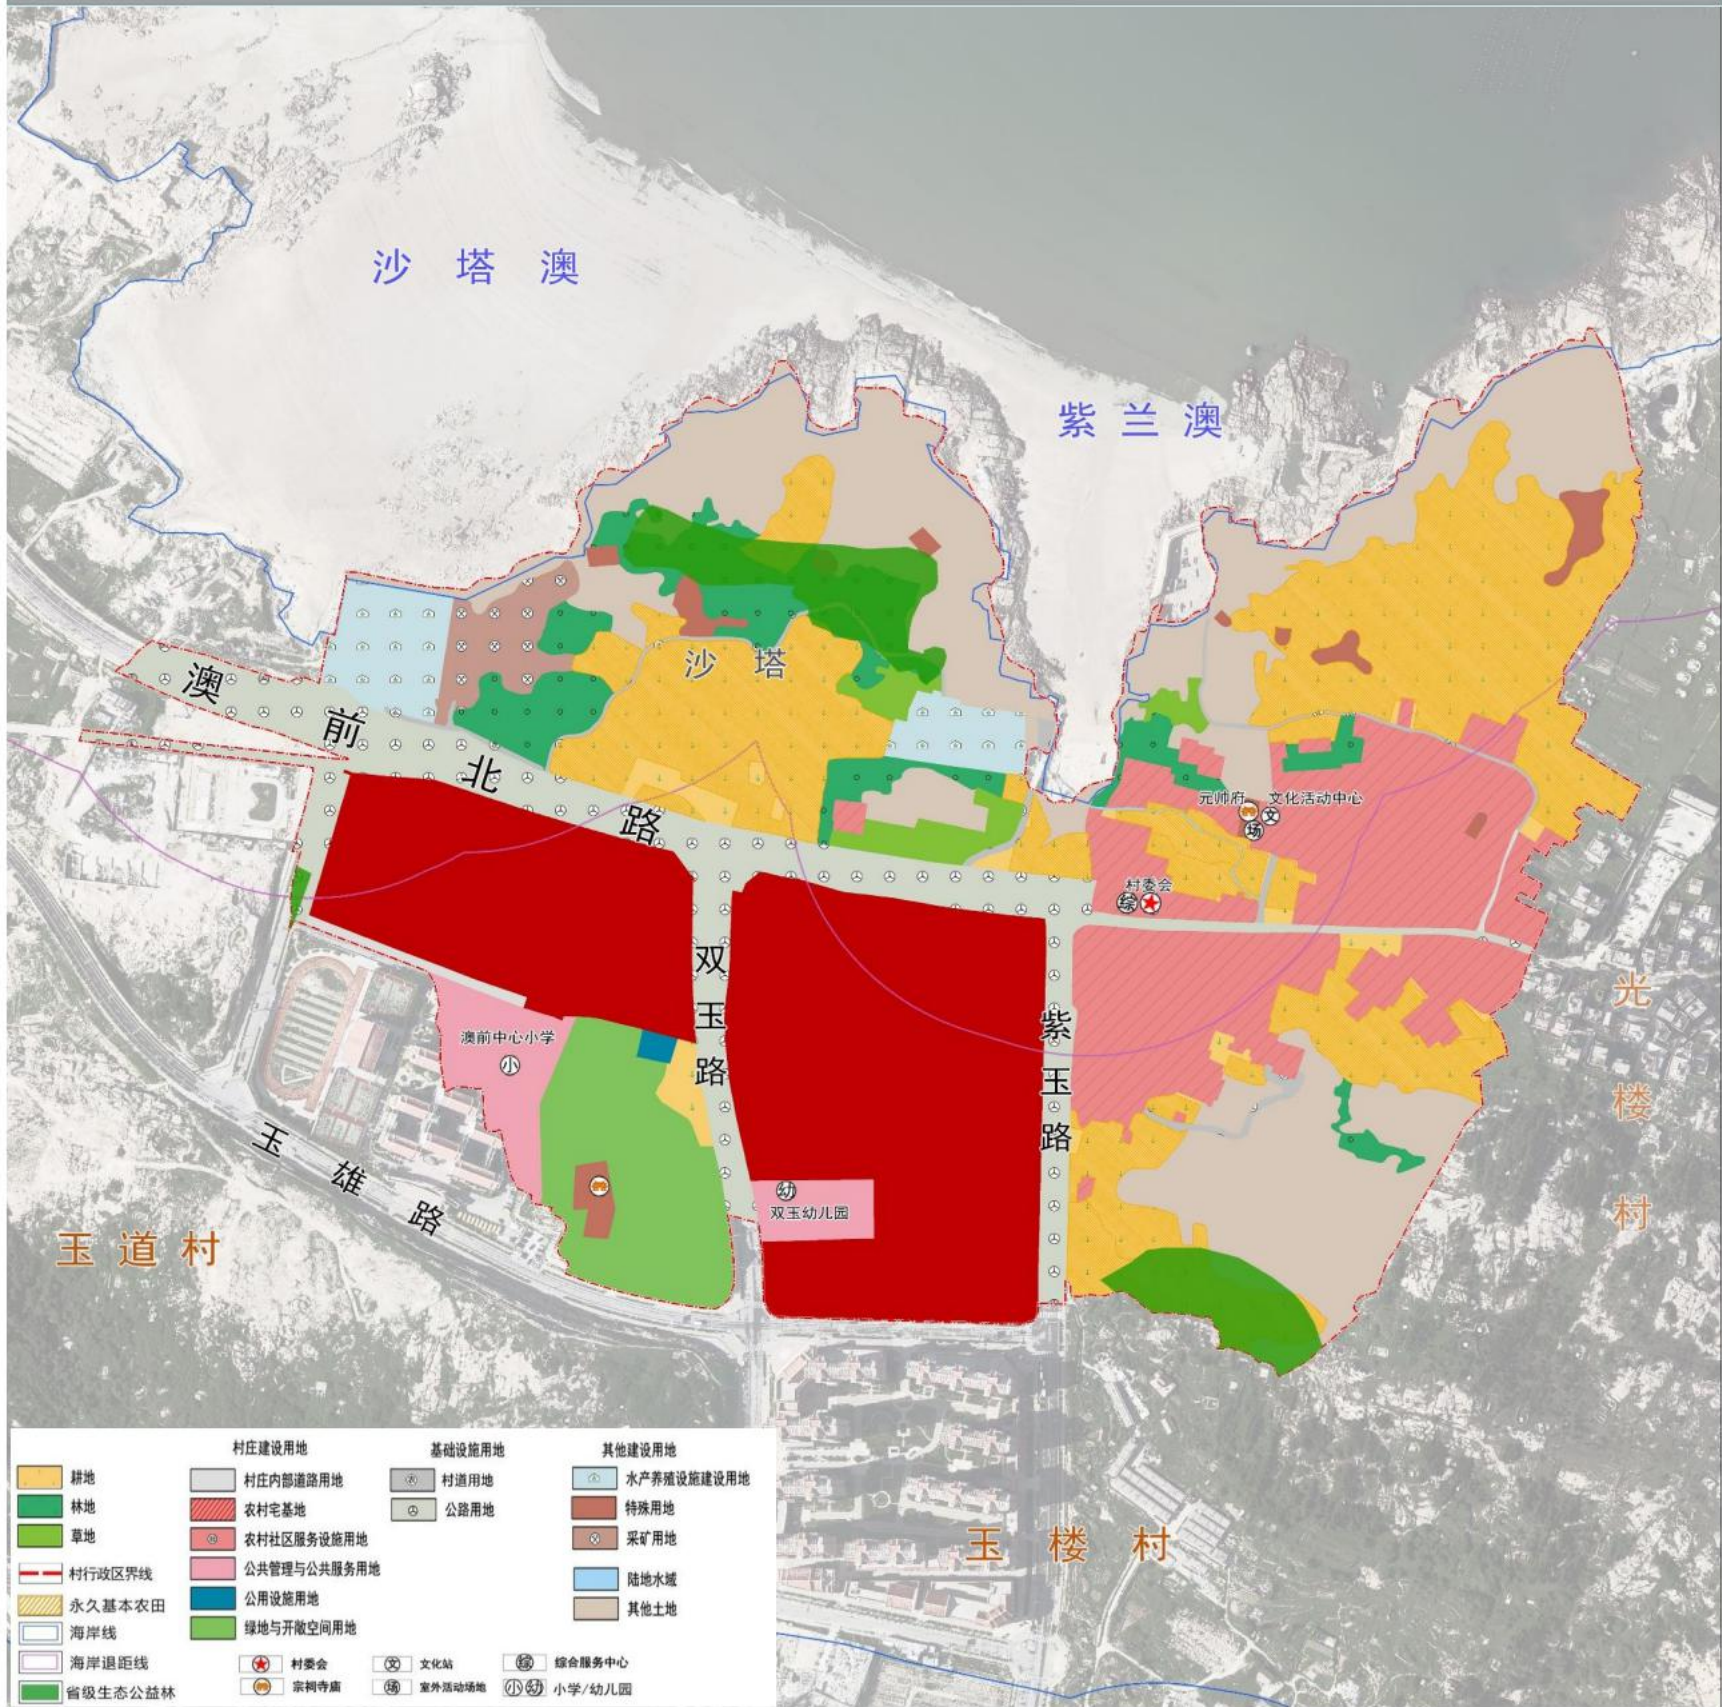


规划区内现有耕地12.05公顷、林地2.97公顷、草地0.7公顷、农业设施建设用地1.9公顷；村庄建设用地22.64公顷，其中农村宅基地面积7.01公顷；村域总建设用地29.09公顷；陆地水域0.03公顷，其他土地10.95公顷。

用地用海类型				规划基期年		
				面积（公顷）	比重（%）	
耕地（01）				12.05	20.89	
园地（02）				0.00	0.00	
林地（03）				2.97	5.14	
草地（04）				0.70	1.21	
湿地（05）				0.00	0.00	
合计				15.72	27.24	
农业设施建设用地	村道用地			0.53	0.91	
	种植设施建设用地			0.00	0.00	
	畜禽养殖设施建设用地			0.00	0.00	
	水产养殖设施建设用地			1.38	2.39	
合计				1.90	3.30	
村域建设用地	村域城乡建设用地	城镇用地			11.61	20.13
		居住用地	农村社区服务设施用地	0.06	0.10	
			农村宅基地	7.01	12.16	
		公共管理与公共服务用地			1.40	2.43
		商业服务业用地			0.00	0.00
		工业用地			0.00	0.00
		仓储用地			0.00	0.00
		村庄内部道路用地			0.17	0.29
		交通场站用地			0.00	0.00
		其他交通设施用地			0.00	0.00
		公用设施用地			0.06	0.10
		绿地与开敞空间用地			2.33	4.04
		留白用地			0.00	0.00
		空闲地			0.00	0.00
		合计			11.03	19.12
		合计			22.64	39.24
		区域基础设施用地			5.02	8.70
	其他建设用地			1.43	2.48	
	合计				29.09	50.42
陆地水域				0.03	0.06	
渔业用海				0.00	0.00	
工矿通信用海				0.00	0.00	
交通运输用海				0.00	0.00	
游憩用海				0.00	0.00	
特殊用海				0.00	0.00	
其他土地				10.95	18.98	
其他海域				0.00	0.00	
总计				57.69	100.00	


规划一张图

◆ 村域综合规划图

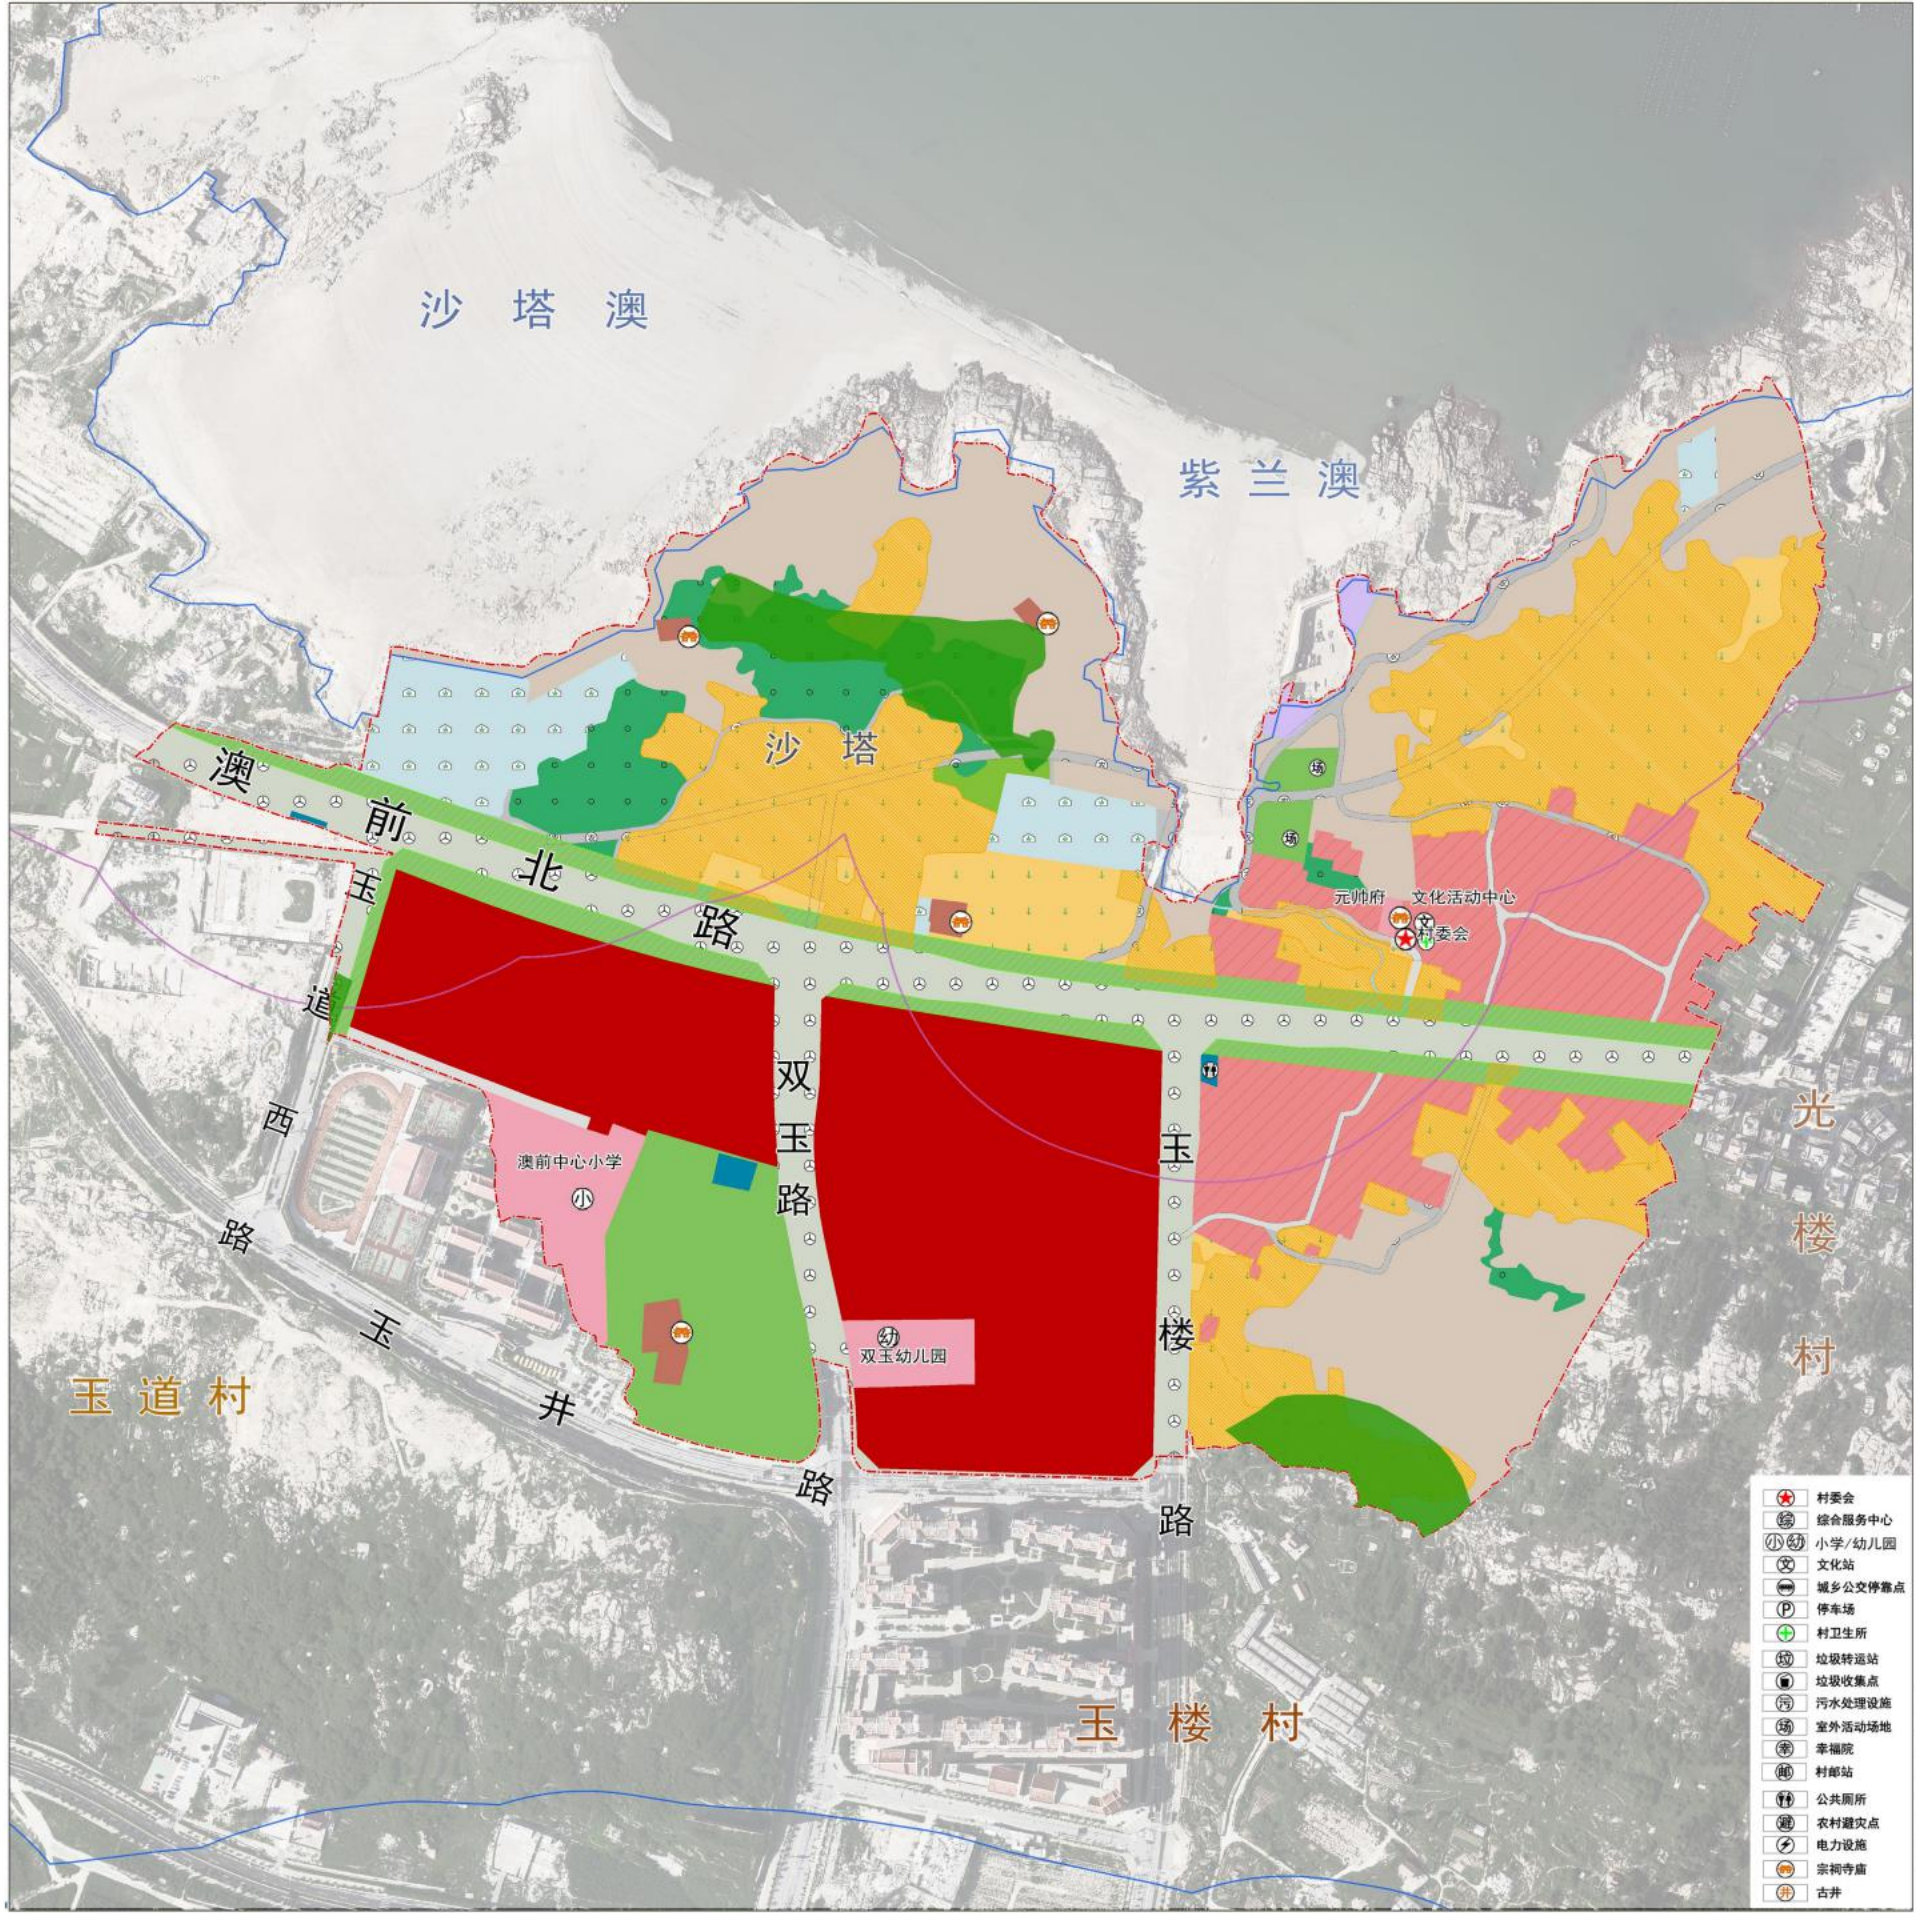

平潭综合实验区海坛片区紫兰村村庄规划 (2022-2035)

风玫瑰与比例尺

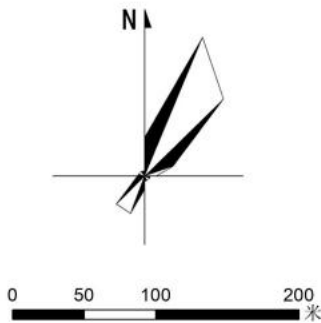

区位图



图例




村域国土空间功能结构调整表

用地用海类型				规划基期年		规划目标年		用地调整（公顷）	
				面积（公顷）	比重（%）	面积（公顷）	比重（%）		
耕地（01）				12.05	20.89	12.75	22.11	0.70	
园地（02）				0.00	0.00	0.00	0.00	0.00	
林地（03）				2.97	5.14	2.58	4.47	-0.39	
草地（04）				0.70	1.21	0.14	0.24	-0.56	
湿地（05）				0.00	0.00	0.00	0.00	0.00	
合计				15.72	27.24	15.47	26.81	-0.25	
农业设施建设用地	村道用地			0.53	0.91	1.04	1.80	0.51	
	种植设施建设用地			0.00	0.00	0.00	0.00	0.00	
	畜禽养殖设施建设用地			0.00	0.00	0.00	0.00	0.00	
	水产养殖设施建设用地			1.38	2.39	2.12	3.67	0.74	
	合计			1.90	3.30	3.16	5.47	1.25	
村域建设用地	村庄建设用地	城镇用地		11.61	20.13	20.09	34.82	8.48	
		居住用地	农村社区服务设施用地	0.06	0.10	0.00	0.00	-0.06	
			农村宅基地	7.01	12.16	5.63	9.77	-1.38	
		公共管理与公共服务用地		1.40	2.43	0.03	0.06	-1.37	
		商业服务业用地		0.00	0.00	0.00	0.00	0.00	
		工业用地		0.00	0.00	0.00	0.00	0.00	
		仓储用地		0.00	0.00	0.00	0.00	0.00	
		村庄内部道路用地		0.17	0.29	0.13	0.23	-0.03	
		交通场站用地		0.00	0.00	0.00	0.00	0.00	
		其他交通设施用地		0.00	0.00	0.00	0.00	0.00	
		公用设施用地		0.06	0.10	0.03	0.05	-0.03	
		绿地与开敞空间用地		2.33	4.04	0.30	0.52	-2.03	
		留白用地		0.00	0.00	0.00	0.00	0.00	
		空闲地		0.00	0.00	0.00	0.00	0.00	
	合计		11.03	19.12	6.12	10.62	-4.90		
	合计			22.64	39.24	26.22	45.44	3.57	
	区域基础设施用地			5.02	8.70	2.65	4.59	-2.37	
	其他建设用地			1.43	2.48	0.13	0.23	-1.30	
	合计			23.09	50.42	29.00	50.26	-0.09	
	陆地水域				0.03	0.06	0.02	0.03	-0.01
	渔业用海				0.00	0.00	0.17	0.29	0.17
	工矿通信用海				0.00	0.00	0.00	0.00	0.00
	交通运输用海				0.00	0.00	0.00	0.00	0.00
游憩用海				0.00	0.00	0.00	0.00	0.00	
特殊用海				0.00	0.00	0.00	0.00	0.00	
其他土地				10.95	18.98	9.88	17.13	-1.07	
其他海域				0.00	0.00	0.00	0.00	0.00	
总计				57.69	100.00	57.69	100.00	0.00	




用地用海类型			规划基期年		规划目标年		用地调整 (公顷)	
			面积（公 顷）	比重（%）	面积（公顷）	比重（%）		
耕地（01）			12.05	20.89	12.75	22.11	0.70	
园地（02）			0.00	0.00	0.00	0.00	0.00	
林地（03）			2.97	5.14	2.58	4.47	-0.39	
草地（04）			0.70	1.21	0.14	0.24	-0.56	
湿地（05）			0.00	0.00	0.00	0.00	0.00	
合计			15.72	27.24	15.47	26.81	-0.25	
农业设施建设用地	村道用地		0.53	0.91	1.04	1.80	0.51	
	种植设施建设用地		0.00	0.00	0.00	0.00	0.00	
	畜禽养殖设施建设用地		0.00	0.00	0.00	0.00	0.00	
	水产养殖设施建设用地		1.38	2.39	2.12	3.67	0.74	
合计			1.90	3.30	3.16	5.47	1.25	
村域建设用地	村域城 乡建设 用地	城镇用地		11.61	20.13	20.09	34.82	8.48
		居住用地	农村社区服务设 施用地	0.06	0.10	0.00	0.00	-0.06
			农村宅基地	7.01	12.16	5.63	9.77	-1.38
			公共管理与公共服务用地		1.40	2.43	0.03	0.06
		商业服务业用地		0.00	0.00	0.00	0.00	0.00
		工业用地		0.00	0.00	0.00	0.00	0.00
		仓储用地		0.00	0.00	0.00	0.00	0.00
		村庄内部道路用地		0.17	0.29	0.13	0.23	-0.03
		交通场站用地		0.00	0.00	0.00	0.00	0.00
		其他交通设施用地		0.00	0.00	0.00	0.00	0.00
		公用设施用地		0.06	0.10	0.03	0.05	-0.03
		绿地与开敞空间用地		2.33	4.04	0.30	0.52	-2.03
		留白用地		0.00	0.00	0.00	0.00	0.00
		空闲地		0.00	0.00	0.00	0.00	0.00
		合计		11.03	19.12	6.12	10.62	-4.90
		合计		22.64	39.24	26.22	45.44	3.57
		区域基础设施用地		5.02	8.70	2.65	4.59	-2.37
	其他建设用地		1.43	2.48	0.13	0.23	-1.30	
	合计			29.09	50.42	29.00	50.26	-0.09
陆地水域			0.03	0.06	0.02	0.03	-0.01	
渔业用海			0.00	0.00	0.17	0.29	0.17	
工矿通信用海			0.00	0.00	0.00	0.00	0.00	
交通运输用海			0.00	0.00	0.00	0.00	0.00	
游憩用海			0.00	0.00	0.00	0.00	0.00	
特殊用海			0.00	0.00	0.00	0.00	0.00	
其他土地			10.95	18.98	9.88	17.13	-1.07	
其他海域			0.00	0.00	0.00	0.00	0.00	
总计			57.69	100.00	57.69	100.00	0.00	

序号	指标	属性	单位	现状基期年	规划目标年	备注
一、村庄发展性指标						
1	村域建设用地总面积	约束性	公顷	29.09	29.00	
2	村域城乡建设用地面积	约束性	公顷	22.64	26.22	
3	村庄建设用地规模	预期性	公顷	11.03	6.12	
4	公共管理与公共服务用地规模	预期性	公顷	1.40	0.03	
5	公用设施用地规模	预期性	公顷	0.06	0.03	
6	人均村庄建设用地面积	预期性	平方米/人	68.84	76.49	
二、村庄保护性指标						
7	生态保护红线面积	约束性	公顷	0.00	0.00	
8	永久基本农田保护面积	约束性	公顷	11.35	11.35	
9	耕地保有量	约束性	公顷	12.05	12.75	
10	林地保有量	约束性	公顷	2.97	2.58	
11	湿地面积	约束性	公顷	0.00	0.00	
12	大陆自然海岸线保有率	约束性	%	88	96	
13	自然和文化遗产	预期性	处	0	0	

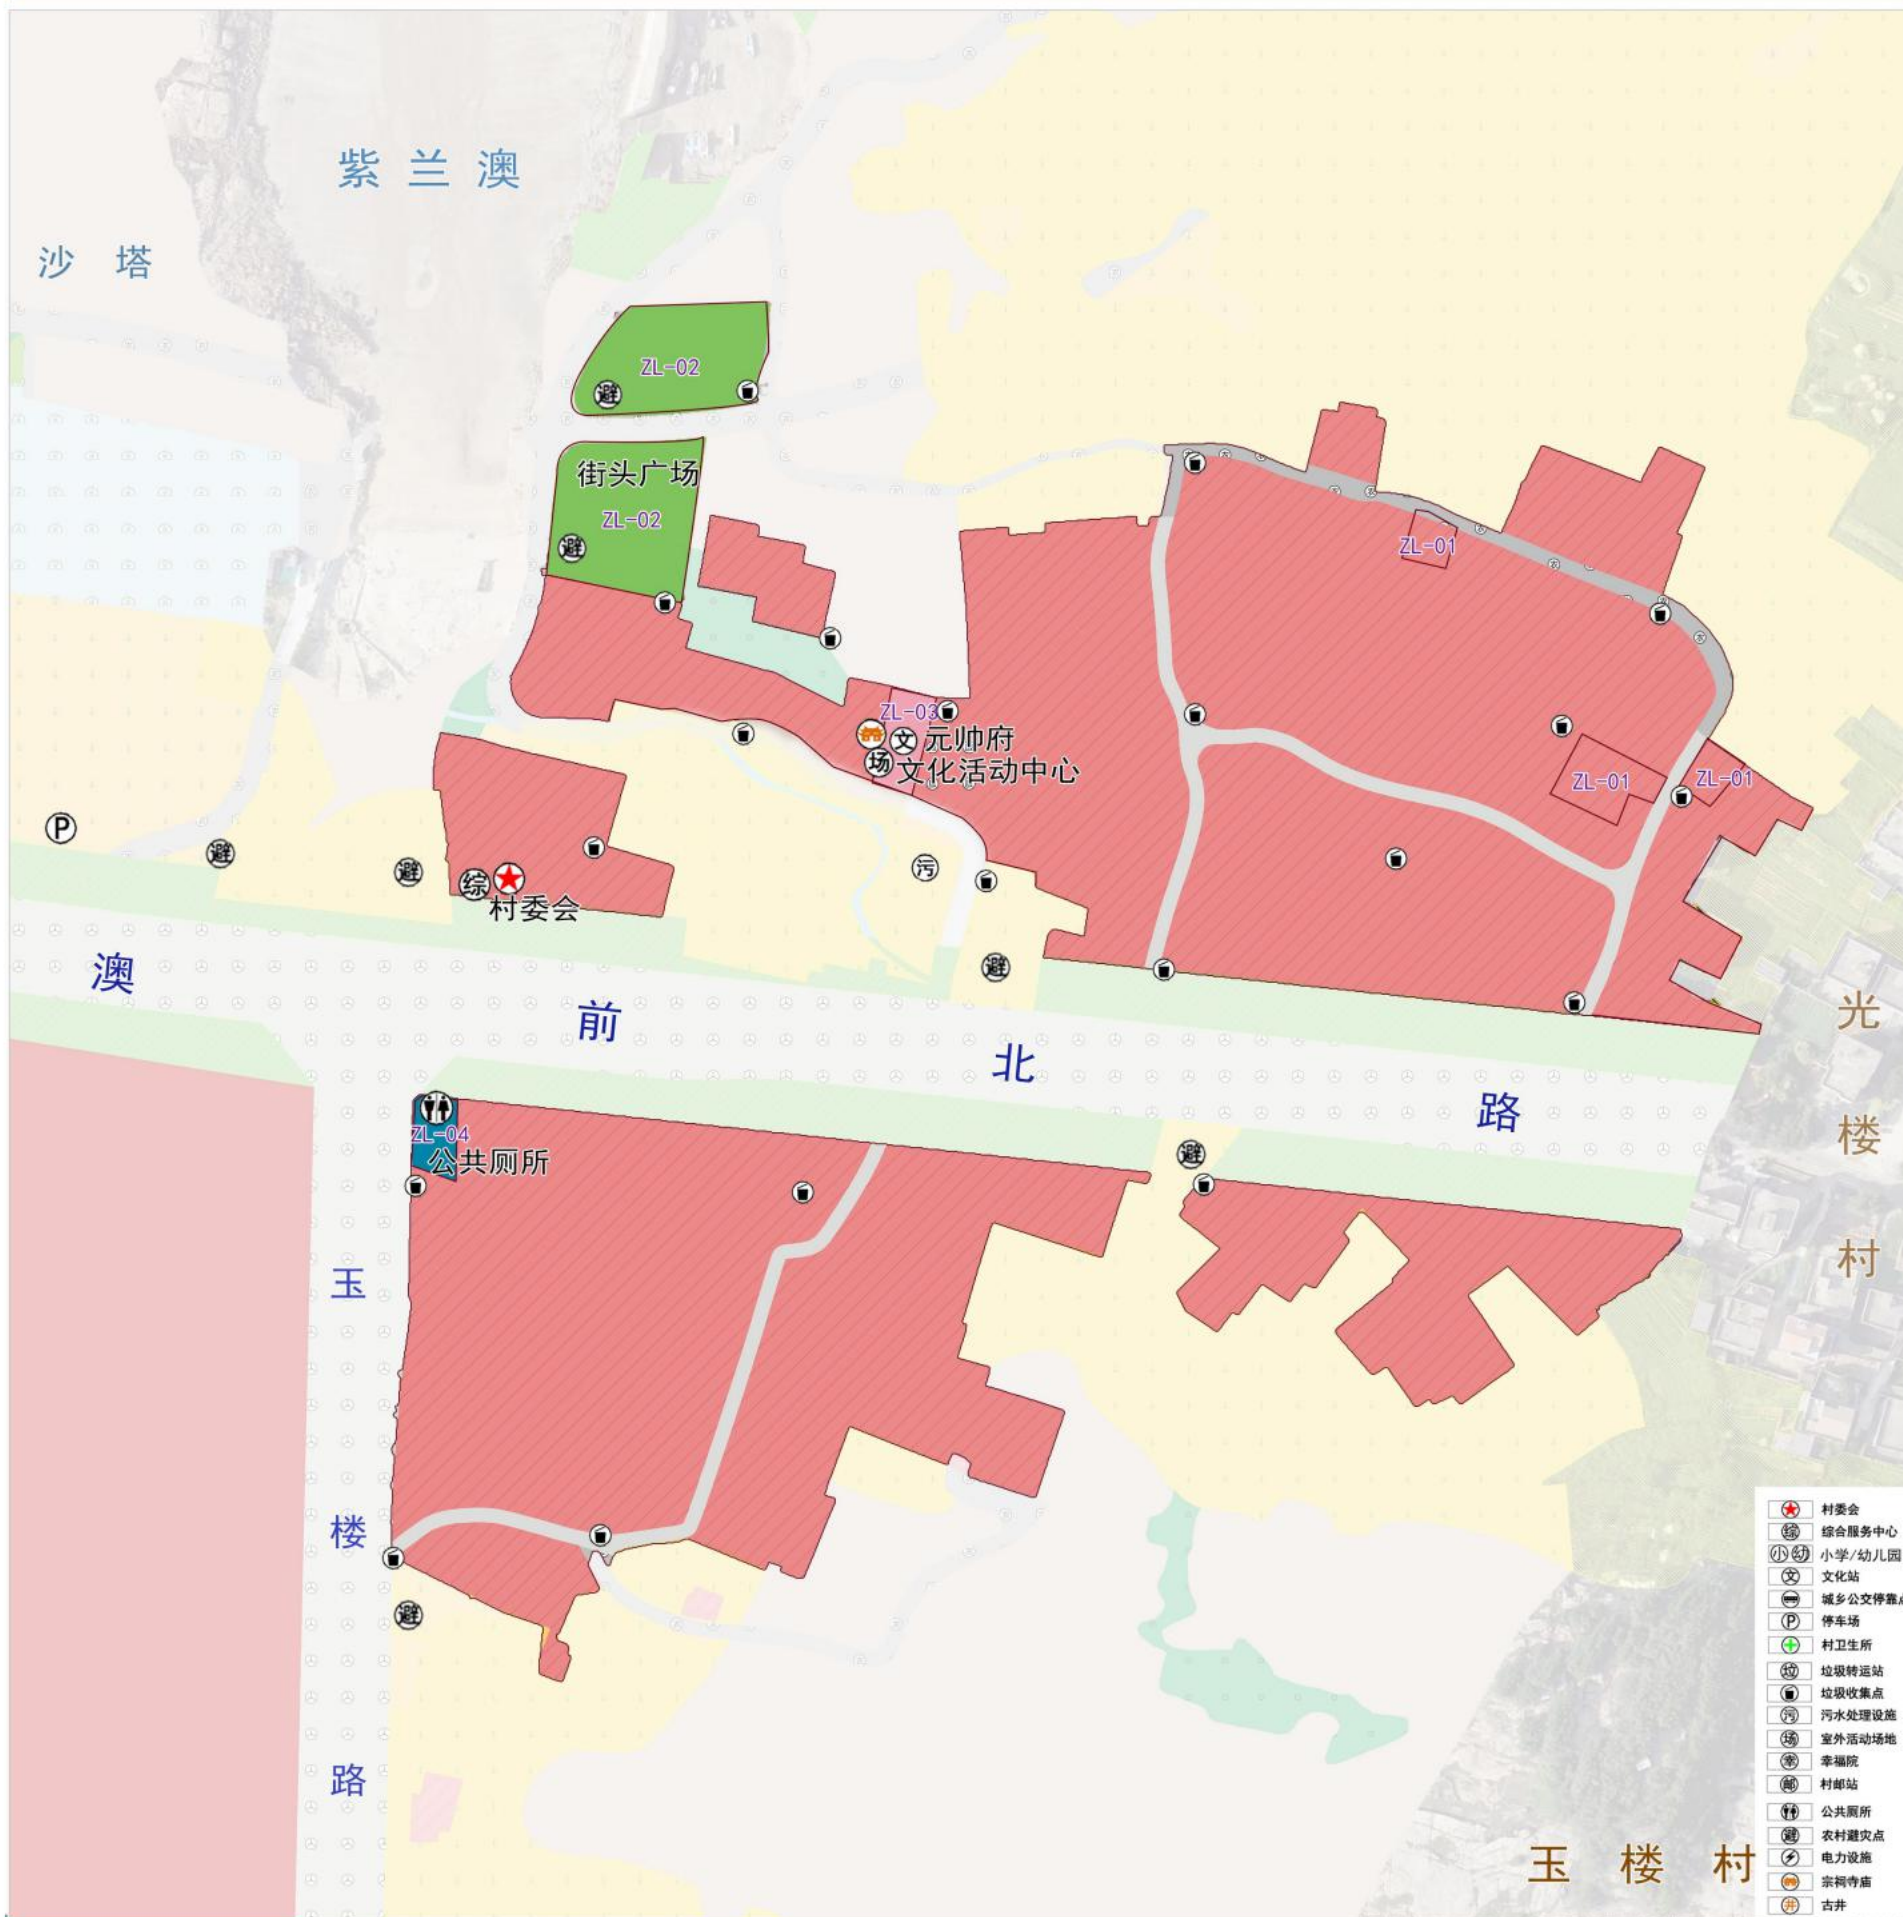


风玫瑰与比例尺

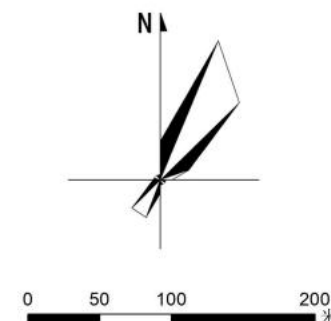

区位图



图例

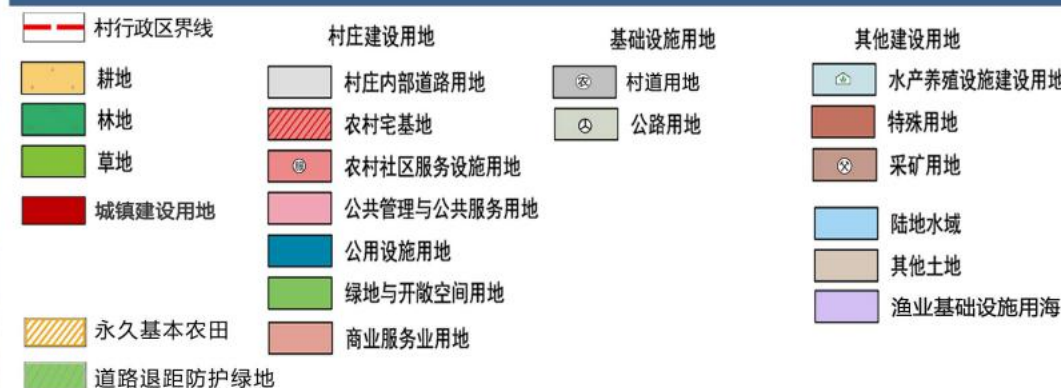

指标一览表

地块编号	用地			建筑高度	名称	地块指引
	用地代码	用地性质	地块面积			
ZL-01	0703	农村宅基地	2194	3层, 12m以内	零星新建	居民点住宅建筑以保留以及改造为主, 原则上不大量新增基地; 此地块拟用于破旧建筑新建以及满足村民建房需求
ZL-02	14	绿地与开敞空间用地	2988	12m以内	街头广场	结合村内空闲地, 提升环境, 改造篮球场, 足球场; 增设休闲配套设施, 供村民休闲娱乐
ZL-03	14	公共管理与公共服务用地	332	12m以内	文体活动中心	结合村内活动中心及宗祠前空地, 提升周边环境, 改造室外活动场地, 配置活动器材
ZL-04	13	公用设施用地	263	12m以内	公厕	结合村庄现状基础服务设施, 配置一处厕所并提升周边环境, 周围可设置临时休憩区

居民点管控规划


村庄公共设施: 提升党群服务中心、附设村邮所、卫生室、广播室等功能。增设并维护现状文化活动中心并增设活动设施; 将现状w活动中心改造成老年人活动中心及室外活动中心, 附设相关设施配套。

道路交通设施: 对外交通主要为上位澳前北路, 村内主干道拓宽并新增部分至海边码头道路, 村庄内部道路交通沿用村中已有的道路, 并在原有的基础上维护; 拆除部分质量较差建筑, 优化道路线行, 满足道路规范要求; 利用路旁空闲地改建临时停车场。局部村道路路面环境较差, 近期建议翻新路面, 并提升两侧绿化环境;

市政设施: 沿道路按30-50m距离设置垃圾收集点, 按服务半径约300m配建公厕, 服务游客和村民; 完善村庄水电配套, 远期采用雨污分离排放模式, 按照不大于120m的距离配建消防栓, 文保单位重点设置。

村庄住宅管制: 村庄居民点住宅建筑以保留及改造为主, 原则上不大量新增宅基地, 严禁核心保护区内开发建设村民住宅, 建设控制地带内严控建设高度、体量、色彩, 严格按照本次设计户型建设, 风貌与村落协调一致。建筑严格按照“一户一宅”政策, 每户宅基地面积控制在120m²以内, 新建住宅高度不得超过12m, 每户住宅面积控制在300m²以内, 住宅建筑间距与前建筑高度比不低于1:1, 相邻建筑山墙间距不低于2m, 建筑宜朝南、南偏东或偏西布置, 建筑后退村庄道路不得少于1m。

村民建房应当遵守相关技术标准规定, 详见《福州市规范农村宅基地和建房管理实施细则(试行)》。

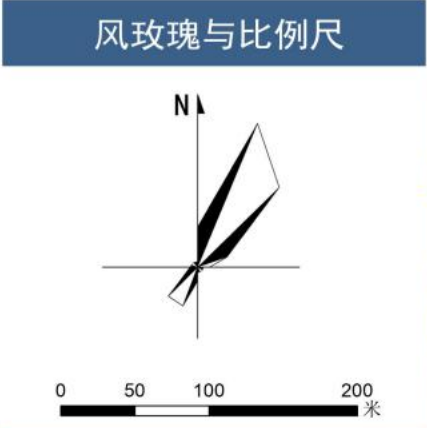

图例

村行政区界线	保留建筑	村委会	室外活动场地	城乡公交停靠点
海岸线	保留建筑	综合服务中	幸福院	停车场
省级生态公益林	新建建筑	文化站	村卫生所	垃圾转运站
道路退距防护绿地	公共建筑	中学	集贸市场	垃圾收集点
海岸退距线	改造建筑	小学	村邮站	污水处理设施
永久基本农田		幼儿园	公共厕所	农村避灾点
		宗祠寺庙	供水设施	电力设施

建设方案指引

9mX13m地块 (二层住宅模式)

村民建房应当遵守以下技术标准规定：

(一)规划：村民建房要符合国土空间总体规划及各类专项规划，靠近城市、县城、乡镇所在地住宅小区，引导参照城市居住区规划设计相关标准，鼓励建设多层单元式住宅。

(二)选址：村民建房选址应避开地质复杂、地基承载力差、地势低洼不易排涝以及易受风口、滑坡、雷电和洪水侵袭等自然灾害影响的地段，杜绝安全隐患问题。

(三)层数和面积：农村独栋式、并联式或联排式自建住宅不得超过三层，每户住宅建筑面积控制在300平方米以内；多层单元式住宅的，每户住宅建筑面积控制在200平方米左右。

(四)层高：一层层高控制在4.5米以内，二层以上层高控制在3.3米以内，建筑总高度不超过12米，建筑屋顶原则上应按坡屋顶设计。

(五)间距和朝向：住宅建筑前后间距与建筑高度比一般不低于1:1，相邻房屋山墙之间（外墙至外墙）的间距不低于4米，建筑宜朝南、朝南偏东或偏西布置。新建建筑宜后退村庄干路红线3米以上，后退村庄支路红线1米以上。因旧房改造、扩建等受用地条件限制的，根据实际情况由属地乡镇人民政府合理确定相邻距离。

(六)抗震：新建住宅必须符合工程抗震设防要求，板、梁、柱不得采用石结构。

(七)建筑单体：应满足村民生产生活需求，住宅平面布局应设有客厅、卧室、厨房、卫生间、储藏间（农具堆放间）应满足面积、通风、采光等要求。房屋造型简洁美观，宜采用坡屋面，符合地方建筑特色，外观应进行一次性装修。

(八)配套：应同步配建化粪池等处理设施；集中建设住宅小区的，给水排水、电力通信、道路、广电、绿化和社区服务等配套设施要同步规划建设，小区建筑密度控制在30%左右，绿地率不低于30%。

其他细则参考《福州市规范农村宅基地和建房管理实施细则(试行)》。