



◆ 国土空间管控边界

管控边界类型		面积 (公顷)	占村域面积比例 (%)
生态空间		1.22	3.63%
其中	生态保护红线	-	
	一般生态空间	1.22	3.63%
农业空间		17.42	51.81%
其中	永久基本农田	10.94	32.54%
	一般农业空间	6.47	19.24%
建设空间		14.84	44.16%
其中	村庄集中建设区	8.77	26.08%
	村庄弹性发展区	0.13	0.39%
	其他（区域基础设施）	3.32	9.87%
	城镇用地	2.76	8.21%

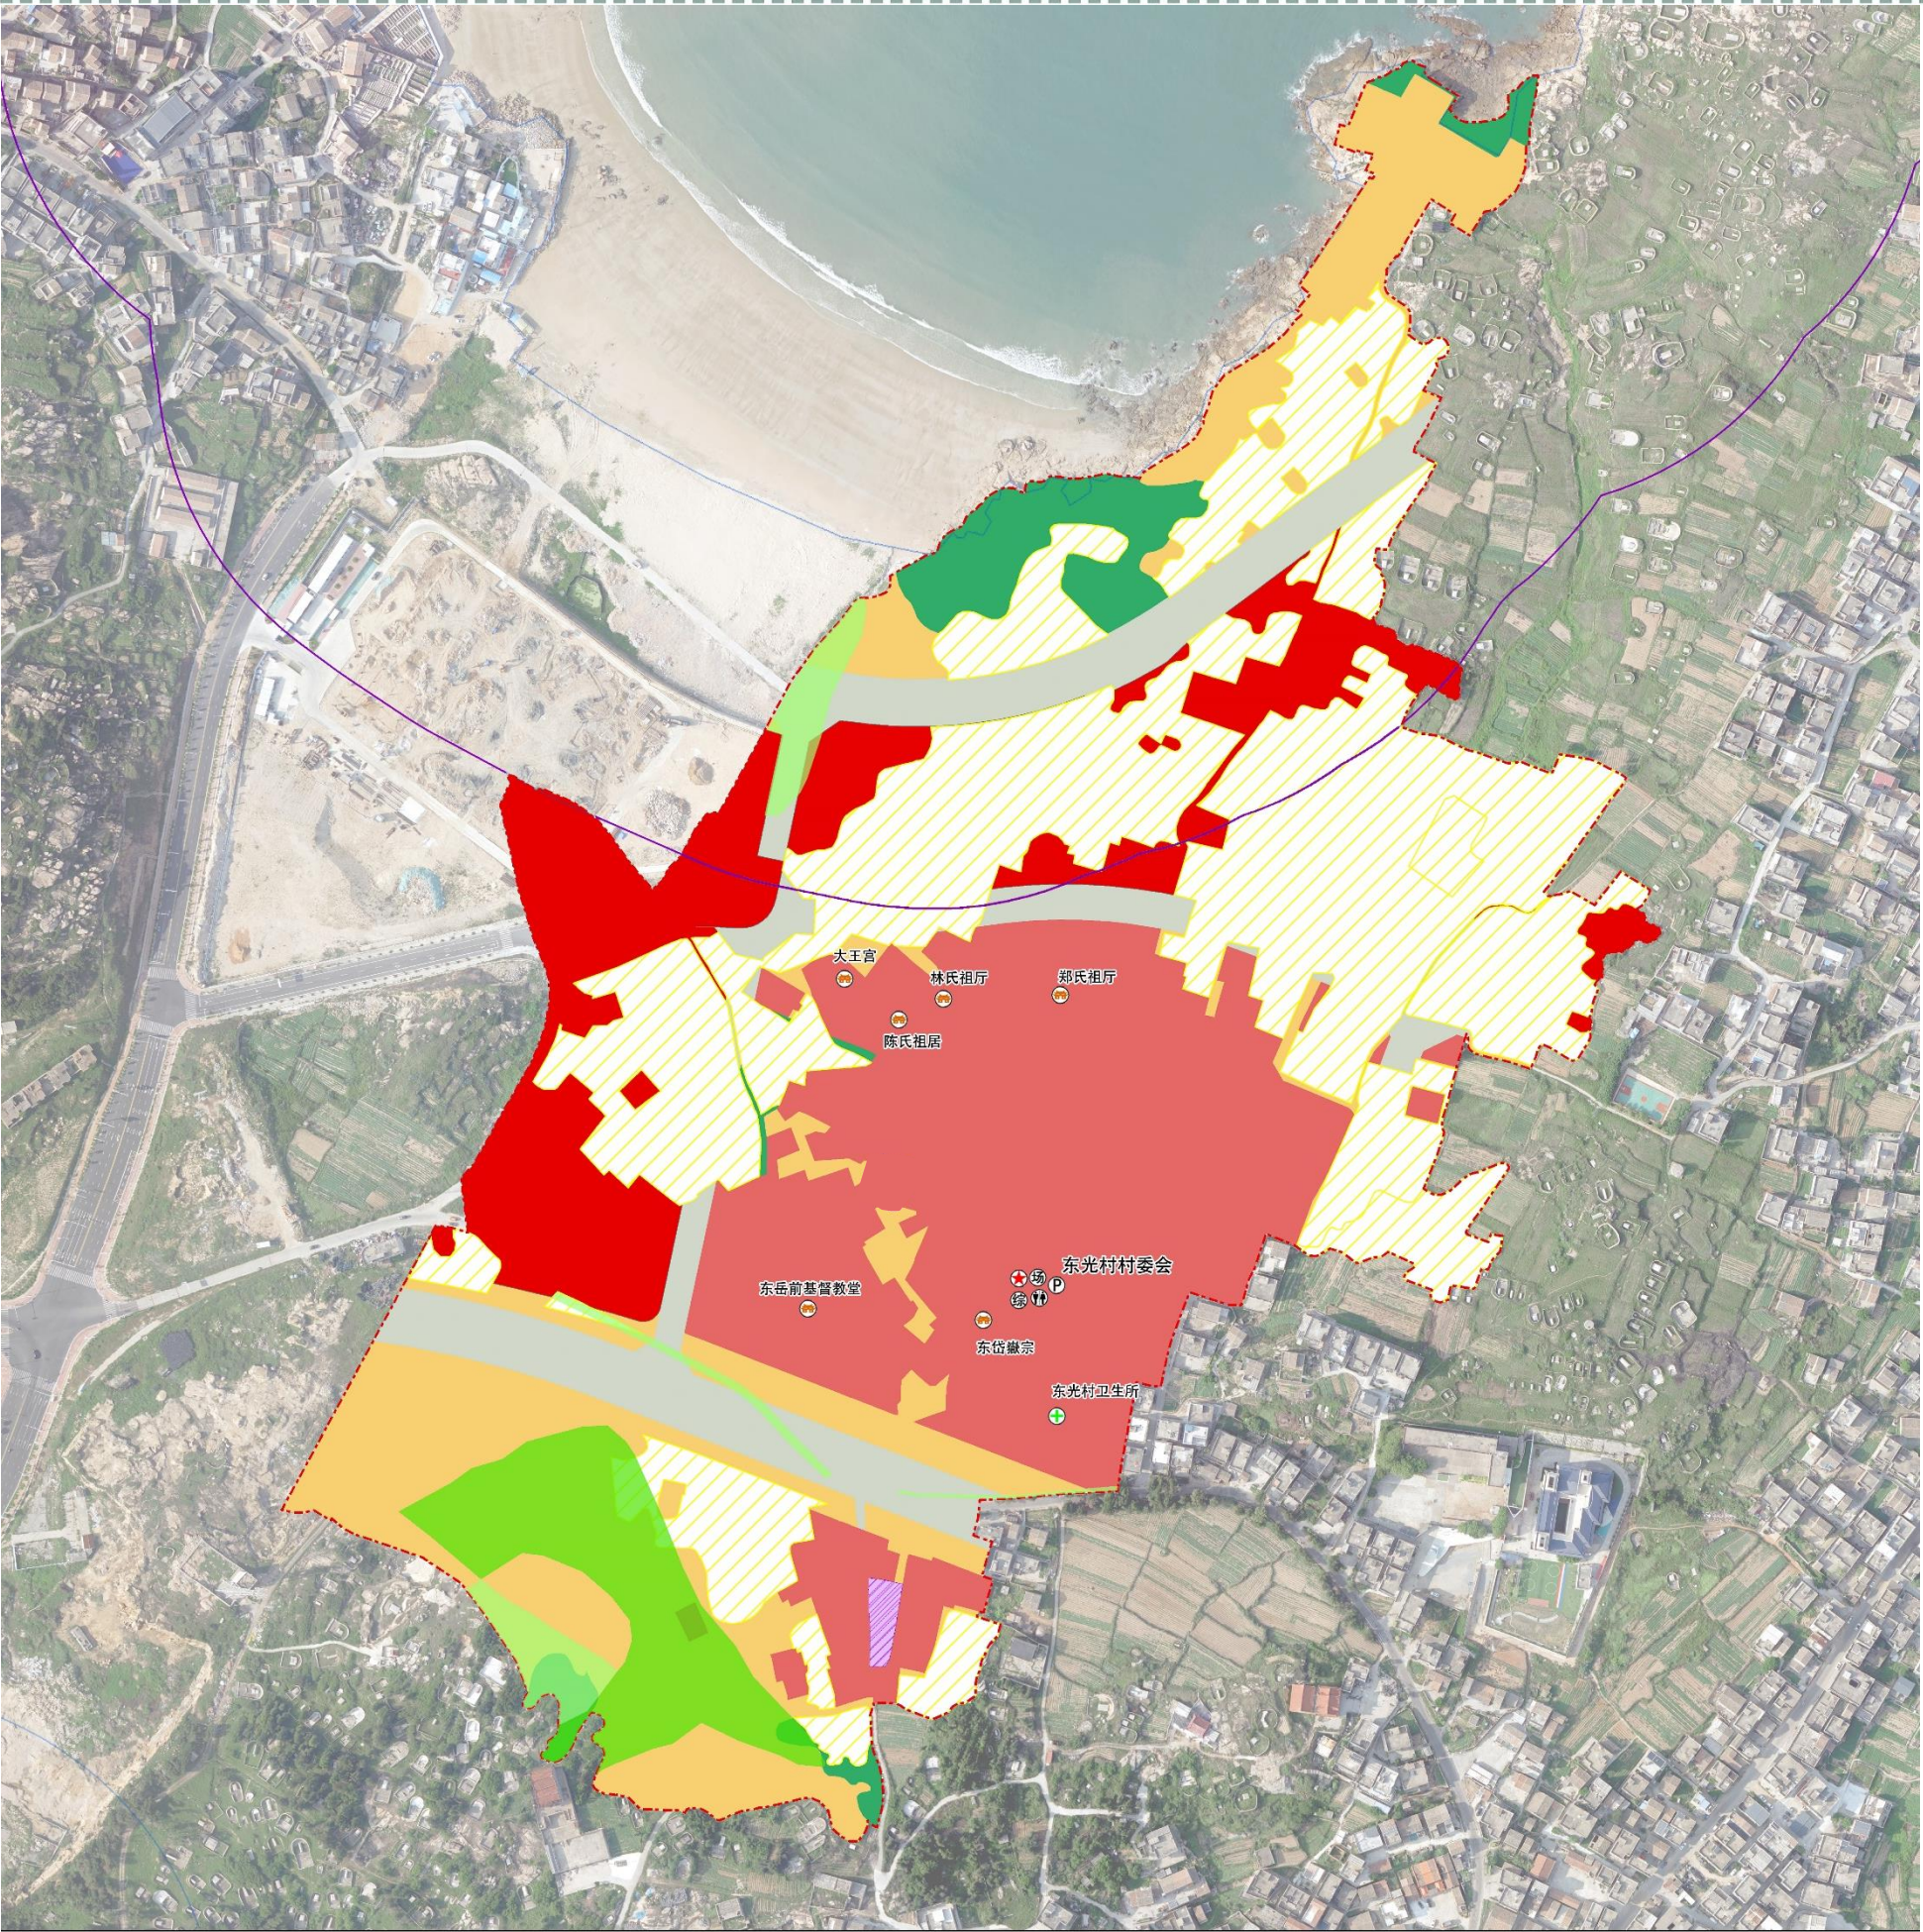

总体开发保护格局

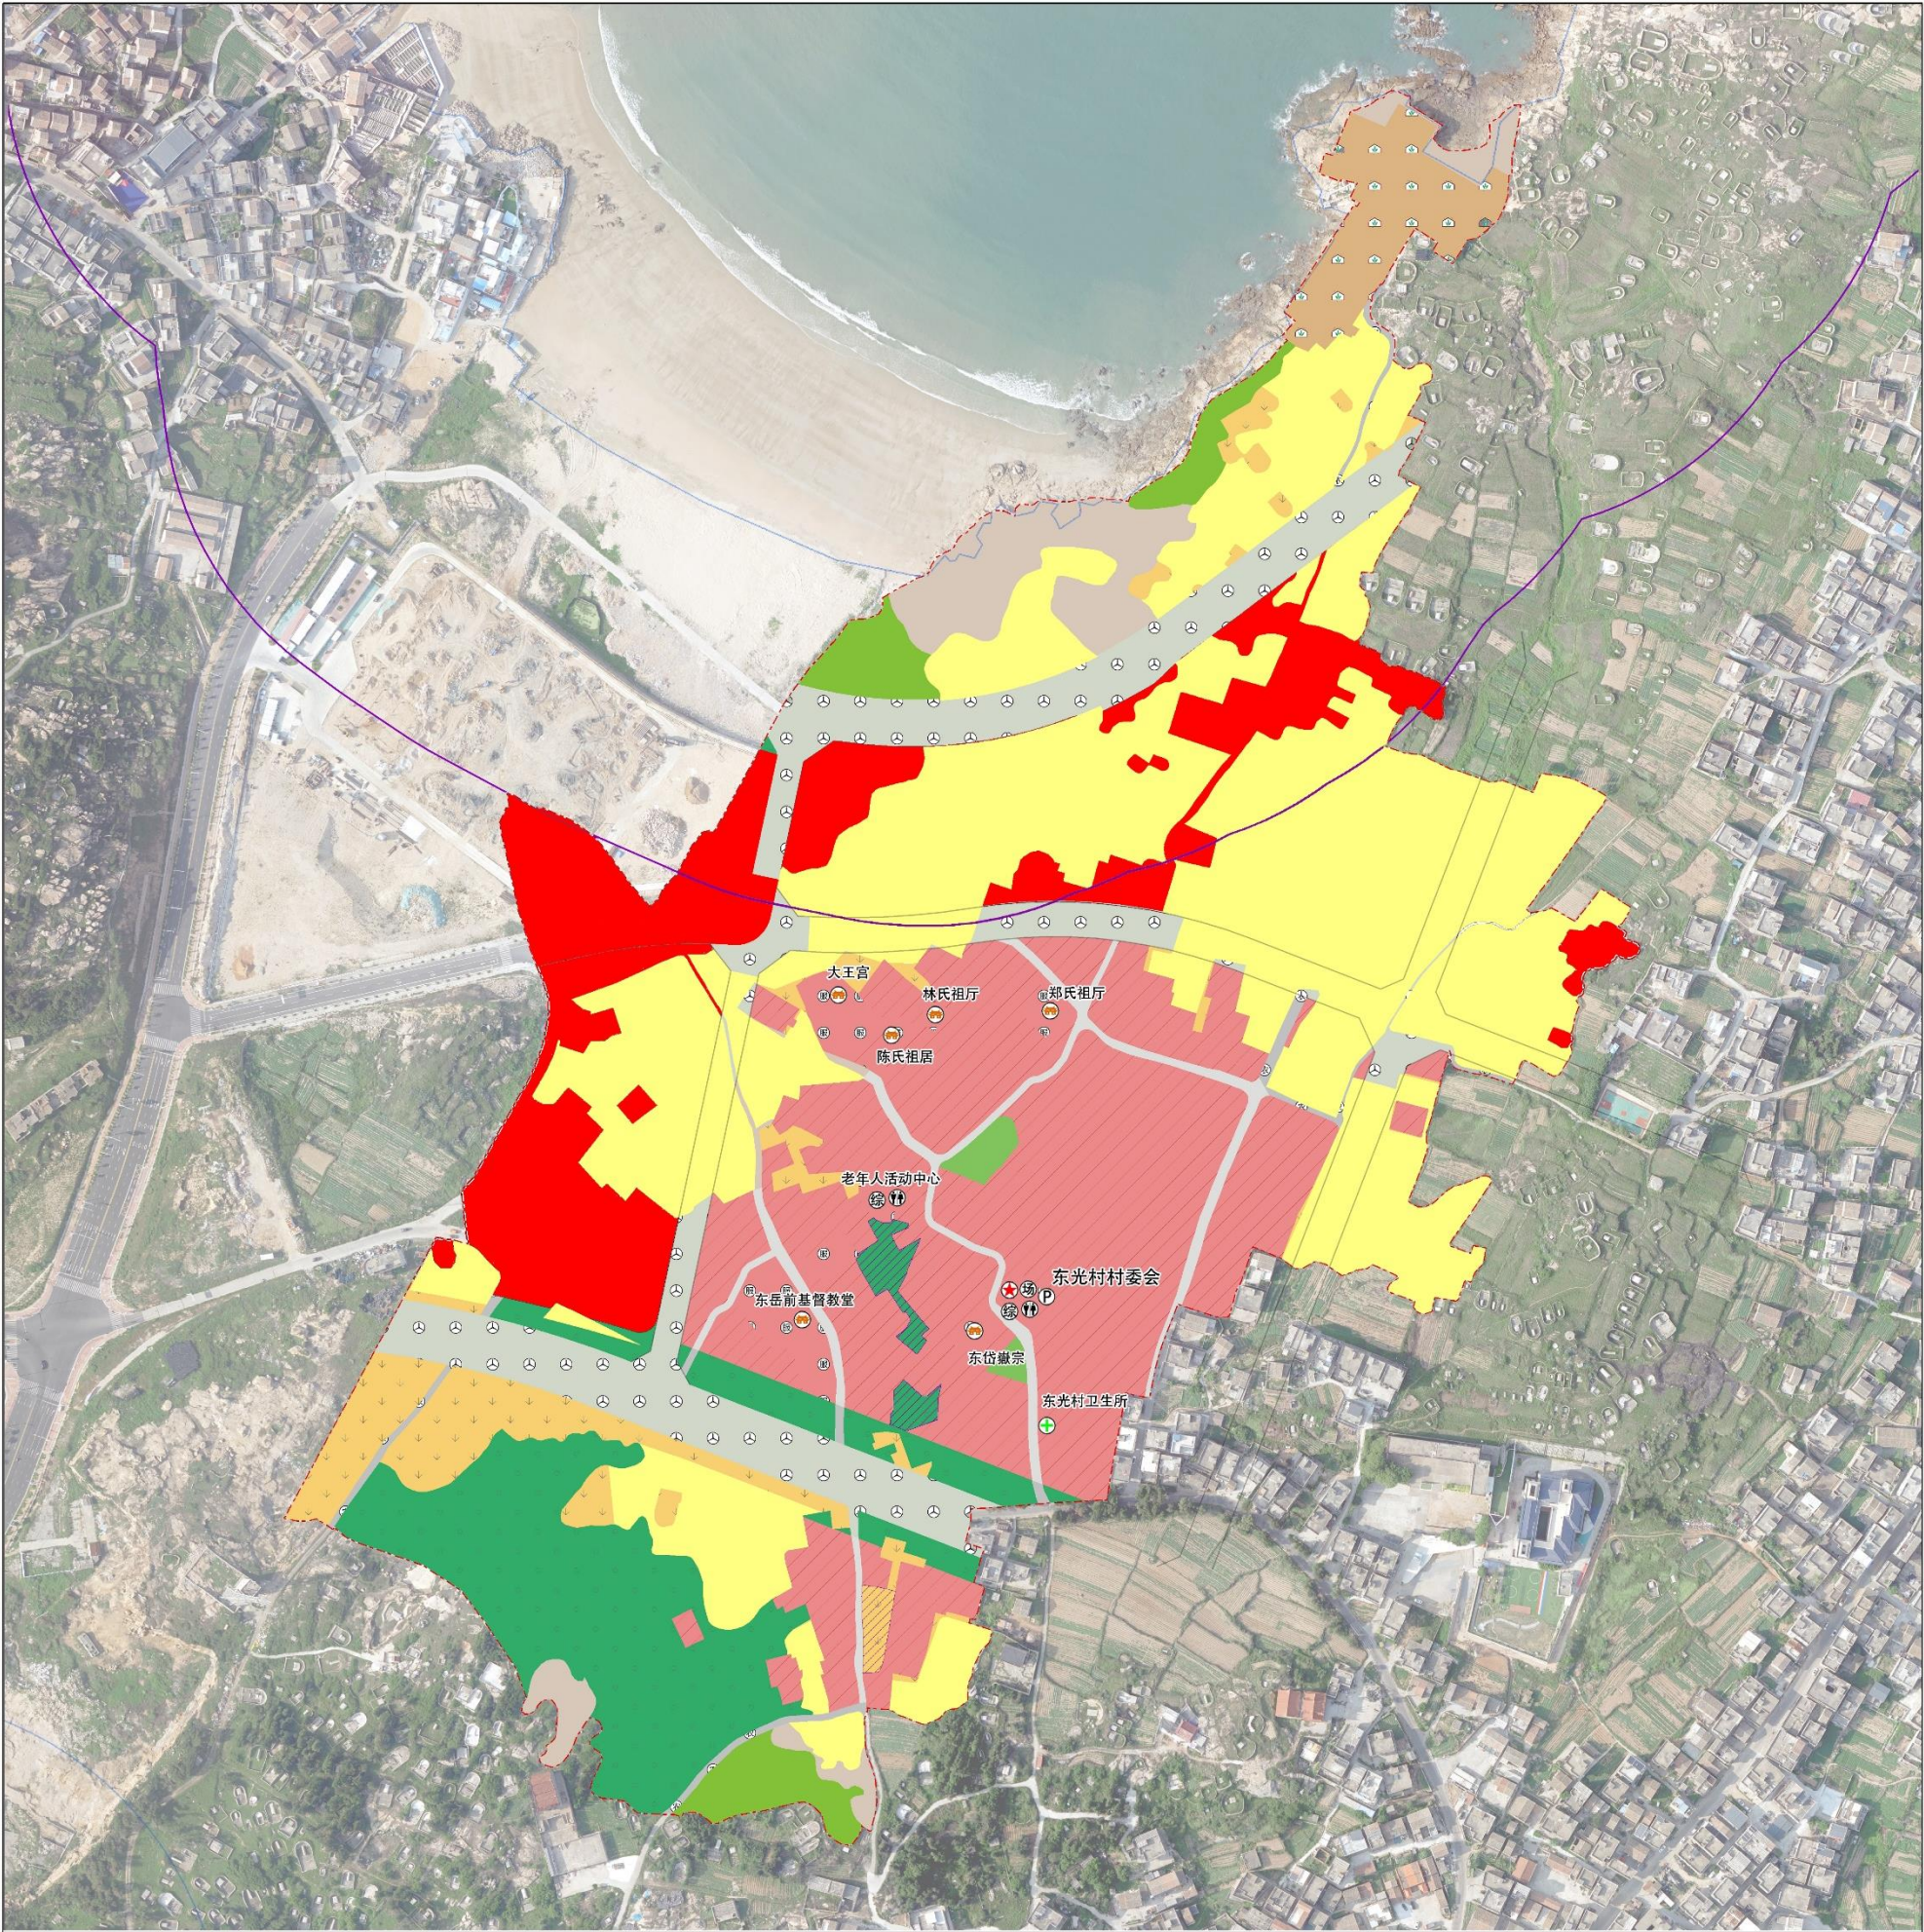

空间功能结构调整表								
用地用海类型			规划基期年		规划目标年			
			面积（公顷）	比重（%）	面积（公顷）	比重（%）		
耕地（01）			14.55	43.30	12.54	37.30		
园地（02）			0.00	0.00	0.00	0.00		
林地（03）			2.61	7.78	3.25	9.66		
草地（04）			1.34	3.98	0.77	2.28		
湿地（05）			0.00	0.00	0.00	0.00		
合计			18.51	55.06	16.55	49.23		
农业设施建设用地	村道用地		0.52	1.55	0.22	0.66		
	种植设施建设用地		0.00	0.00	0.00	0.00		
	畜禽养殖设施建设用地		0.00	0.00	0.00	0.00		
	水产养殖设施建设用地		0.77	2.30	0.77	2.30		
合计			1.29	3.85	0.99	2.96		
村域建设用地	村域城乡建设用地	城镇用地		0.00	0.00	2.76	8.21	
		村庄建设用地	居住用地	农村社区服务设施用地	0.00	0.00	0.63	1.87
			农村宅基地		10.19	30.30	6.83	20.32
			公共管理与公共服务用地		0.06	0.17	0.00	0.00
			商业服务业用地		0.00	0.00	0.00	0.00
			工业用地		0.00	0.00	0.00	0.00
			仓储用地		0.00	0.00	0.00	0.00
			村庄内部道路用地		0.31	0.92	0.54	1.60
			交通场站用地		0.00	0.00	0.00	0.00
			其他交通设施用地		0.00	0.00	0.00	0.00
			公用设施用地		0.01	0.03	0.65	1.92
			绿地与开敞空间用地		0.00	0.00	0.12	0.37
			留白用地		0.00	0.00	0.00	0.00
			空闲地		0.00	0.00	0.00	0.00
	合计		10.56	31.43	8.77	26.08		
	合计		10.56	31.43	11.53	34.29		
	区域基础设施用地		0.74	2.19	3.32	9.87		
	其他建设用地		1.30	3.86	0.00	0.00		
	合计			12.60	37.48	14.84	44.16	
陆地水域			0.00	0.00	0.00	0.00		
渔业用海			0.00	0.00	0.00	0.00		
工矿通信用海			0.00	0.00	0.00	0.00		
交通运输用海			0.00	0.00	0.00	0.00		
游憩用海			0.00	0.00	0.00	0.00		
特殊用海			0.00	0.00	0.00	0.00		
其他土地			1.21	3.61	1.23	3.65		
其他海域			0.00	0.00	0.00	0.00		
总计			33.62	100.00	33.62	100.00		

指标一览表

用地用海类型				规划基期年		规划目标年		用地调整（公顷）	
				面积（公顷）	比重（%）	面积（公顷）	比重（%）		
耕地（01）				14.55	43.30	12.54	37.30	-2.02	
园地（02）				0.00	0.00	0.00	0.00	0.00	
林地（03）				2.61	7.78	3.25	9.66	0.63	
草地（04）				1.34	3.98	0.77	2.28	-0.57	
湿地（05）				0.00	0.00	0.00	0.00	0.00	
合计				18.51	55.06	16.55	49.23	-1.96	
农业设施建设用地	村道用地			0.52	1.55	0.22	0.66	-0.30	
	种植设施建设用地			0.00	0.00	0.00	0.00	0.00	
	畜禽养殖设施建设用地			0.00	0.00	0.00	0.00	0.00	
	水产养殖设施建设用地			0.77	2.30	0.77	2.30	0.00	
	合计			1.29	3.85	0.99	2.96	-0.30	
村域建设用地	村域城乡建设用地	城镇用地			0.00	0.00	2.76	8.21	2.76
		居住用地	农村社区服务设施用地		0.00	0.00	0.63	1.87	0.63
			农村宅基地		10.19	30.30	6.83	20.32	-3.36
		公共管理与公共服务用地			0.06	0.17	0.00	0.00	-0.06
		商业服务业用地			0.00	0.00	0.00	0.00	0.00
		工业用地			0.00	0.00	0.00	0.00	0.00
		仓储用地			0.00	0.00	0.00	0.00	0.00
		村庄内部道路用地			0.31	0.92	0.54	1.60	0.23
		交通场站用地			0.00	0.00	0.00	0.00	0.00
		其他交通设施用地			0.00	0.00	0.00	0.00	0.00
		公用设施用地			0.01	0.03	0.65	1.92	0.64
		绿地与开敞空间用地			0.00	0.00	0.12	0.37	0.12
		留白用地			0.00	0.00	0.00	0.00	0.00
		空闲地			0.00	0.00	0.00	0.00	0.00
		合计			10.56	31.43	8.77	26.08	-1.80
		合计			10.56	31.43	11.53	34.29	0.96
		区域基础设施用地			0.74	2.19	3.32	9.87	2.58
	其他建设用地			1.30	3.86	0.00	0.00	-1.30	
	合计				12.60	37.48	14.84	44.16	2.24
	陆地水域				0.00	0.00	0.00	0.00	0.00
	渔业用海				0.00	0.00	0.00	0.00	0.00
	工矿通信用海				0.00	0.00	0.00	0.00	0.00
交通运输用海				0.00	0.00	0.00	0.00	0.00	
游憩用海				0.00	0.00	0.00	0.00	0.00	
特殊用海				0.00	0.00	0.00	0.00	0.00	
其他土地				1.21	3.61	1.23	3.65	0.01	
其他海域				0.00	0.00	0.00	0.00	0.00	
总计				33.62	100.00	33.62	100.00	0.00	


序号	指标	属性	单位	现状基期年	规划目标年
一、村庄发展性指标					
1	村域建设用地总面积	约束性	公顷	12.60	14.84
2	村域城乡建设用地面积	约束性	公顷	10.56	11.53
3	村庄建设用地规模	预期性	公顷	10.56	8.77
4	公共管理与公共服务用地规模	预期性	公顷	0.06	0.00
5	公用设施用地规模	预期性	公顷	0.01	0.65
6	人均村庄建设用地面积	预期性	平方米/人	71.38	70.13
二、村庄保护性指标					
7	生态保护红线面积	约束性	公顷	0.00	0.00
8	永久基本农田保护面积	约束性	公顷	10.94	10.94
9	耕地保有量	约束性	公顷	14.55	12.54
10	林地保有量	约束性	公顷	2.61	3.25
11	湿地面积	约束性	公顷	0.00	0.00
12	大陆自然海岸线保有率	约束性	%	85	95
13	自然和文化遗产	预期性	处	0.00	0.00

主要农村居民点总平面示意图

- 1 东光村党群服务中心
- 2 休闲健身广场
- 3 大王宫
- 4 陈氏宗祠
- 5 林氏宗祠
- 6 郑氏宗祠
- 7 东岳嶽宗
- 8 东岳前基督教堂
- 9 瞭望平台
- 10 农业采摘体验
- 11 石厝民宿群
- 12 药用植物园
- 13 休闲步行栈道
- 14 鲍鱼牧场
- 15 渔船码头
- 16 光裕澳沙滩
- 17 望海亭
- 18 休憩景观平台
- 19 新建老年人活动中心



农村居民点规划布局图

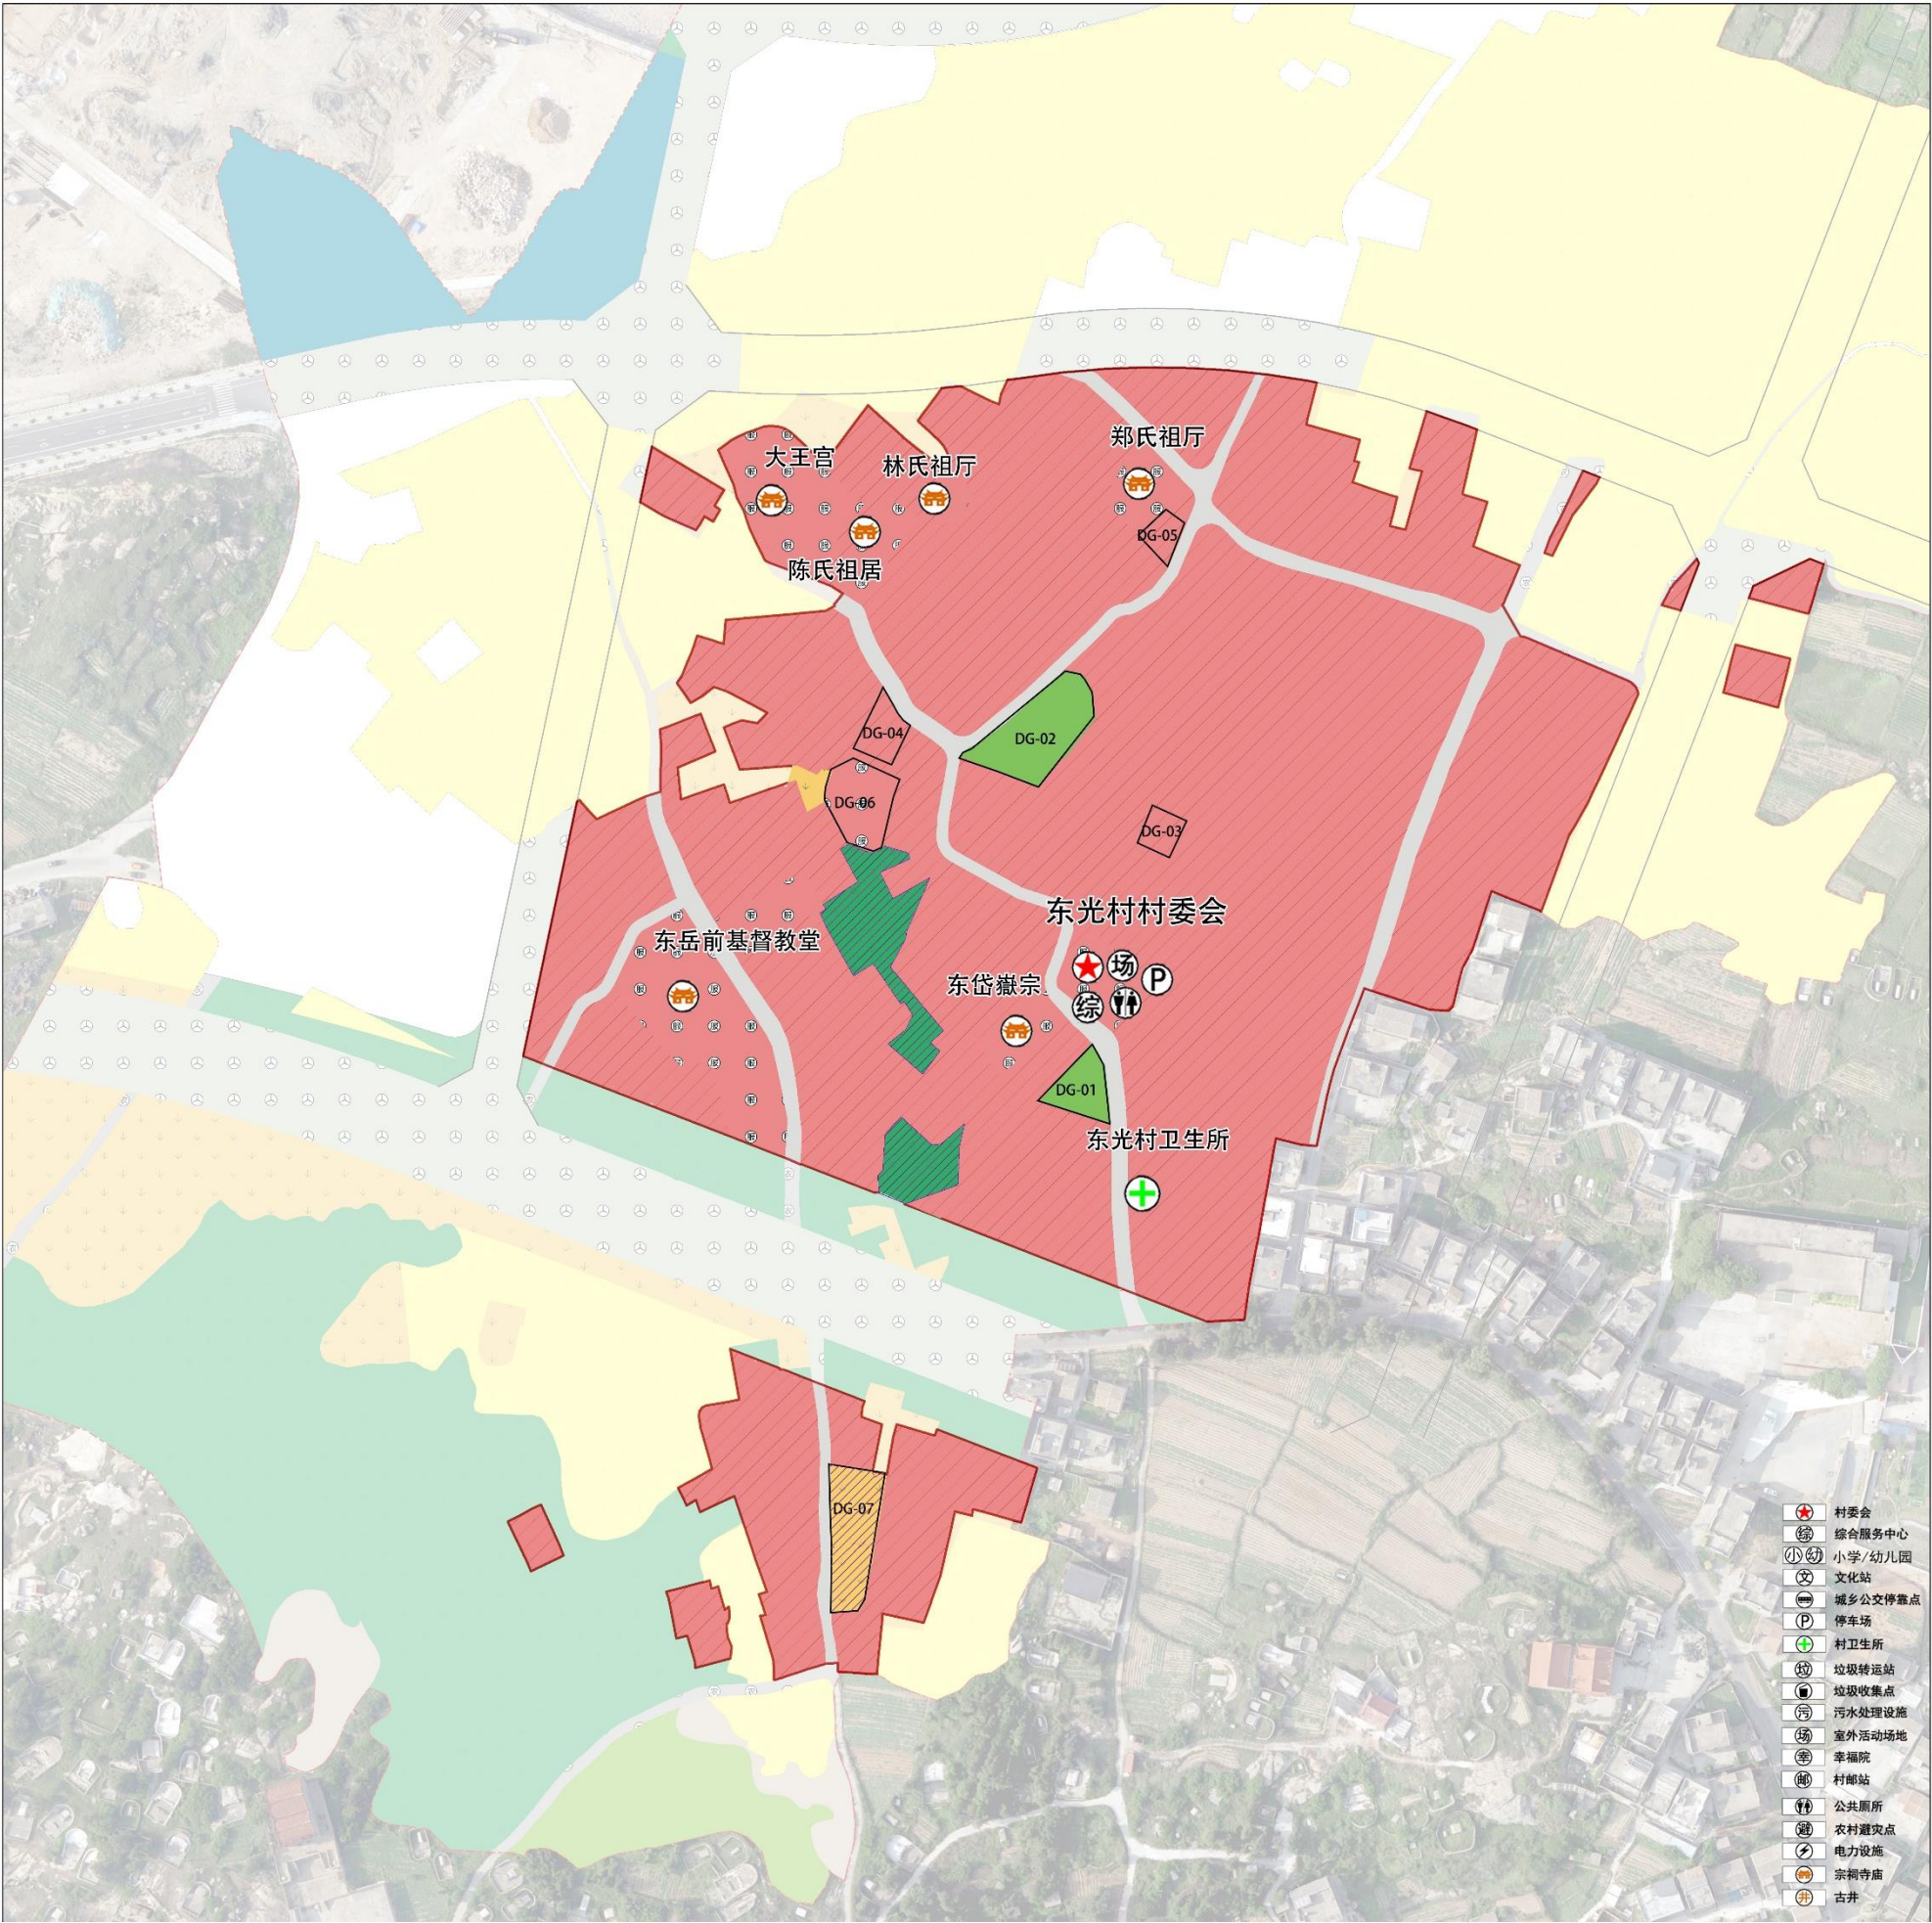

指标一览表							
地块编号	用地		户数		建筑高度	名称	备注
	用地代码	用地性质	现状户数	规划户数			
DG-01	1401	公园绿地	351	0	0	限高8m 口袋公园	结合村委会前的现状空闲地，提升改造口袋公园，增设公园休憩座椅
DG-02	1401	公园绿地	883	0	0	限高8m 街角公园	合理利用村内空闲地，提升改造室外健身活动场地；配套健身器材
DG-03	0703	农村宅基地	509	0	2	3.5层、12m以内 零星建设	补画建设用地，为后期地块内村民拆旧建新、插空建设提供条件。
DG-04	0703	农村宅基地	394	0	1	3.5层、12m以内 零星建设	集约用地，插空建设，合理利用村内用地
DG-05	0703	农村宅基地	389	0	1	3.5层、12m以内 零星建设	根据村内需求，补画建设用地，为后期地块内村民拆旧建新、插空建设提供条件。
DG-06	0704	农村社区服务设施用地	524	0	0	3.5层、12m以内 老年人活动中心	规划新建一处老年人活动中心，附设食堂餐厅，休息室等功能
DG-07	-	耕地	743	-	-	- 待定	划定村庄弹性发展区用地，为村庄远期发展预留空间

管制规则

村庄公共设施：村委会设置党群服务中心、配建卫生所、室内活动场地，附设村邮所、广播室等功能。规划选址新建一处老年人活动中心，附设食堂餐厅、床位等功能；保留现状卫生所、维护现状文化活动中心并增设相关配套设施。

道路交通设施：现状对外交通主要由澳前路及村内主干道承担，村庄内部道路交通沿用村中已有的道路，在原有的基础上维护并新增部分内部道路打通村内断头路；拆除部分质量较差建筑，优化道路线行，满足道路规范要求；利用街头空闲地改建停车场。

市政设施：沿道路按30-50m距离设置垃圾收集点，按服务半径约300m配建公厕，服务游客和村民；完善村庄水电配套，远期采用雨污分离排放模式，按照不大于120m的距离配建消防栓，文保单位重点设置。

村庄住宅管制：村庄居民点住宅建筑以保留及改造为主，原则上不大量新增宅基地，严禁核心保护区内开发建设村民住宅，建设控制地带内严控建设高度、体量、色彩，严格按照本次设计户型建设，风貌与村落协调一致。建筑严格按照“一户一宅”政策，每户宅基地面积控制在120㎡以内，新建住宅建筑层数不超过3层，高度不得超过12m，每户住宅面积控制在300㎡以内，住宅建筑间距与前建筑高度比不低于1:1，相邻建筑山墙间距不低于4m，建筑宜朝南、南偏东或偏西布置，建筑后退村庄道路不得少于1m。

根据《福建省村庄规划编制指南（试行）》中指出：“对村民进行集中安置的新村安置小区、公共服务设施、经营性用地可根据需求适当增加建筑高度，原则上不应超过 6 层。”新建住宅每户住宅占地面积控制120㎡以内。