



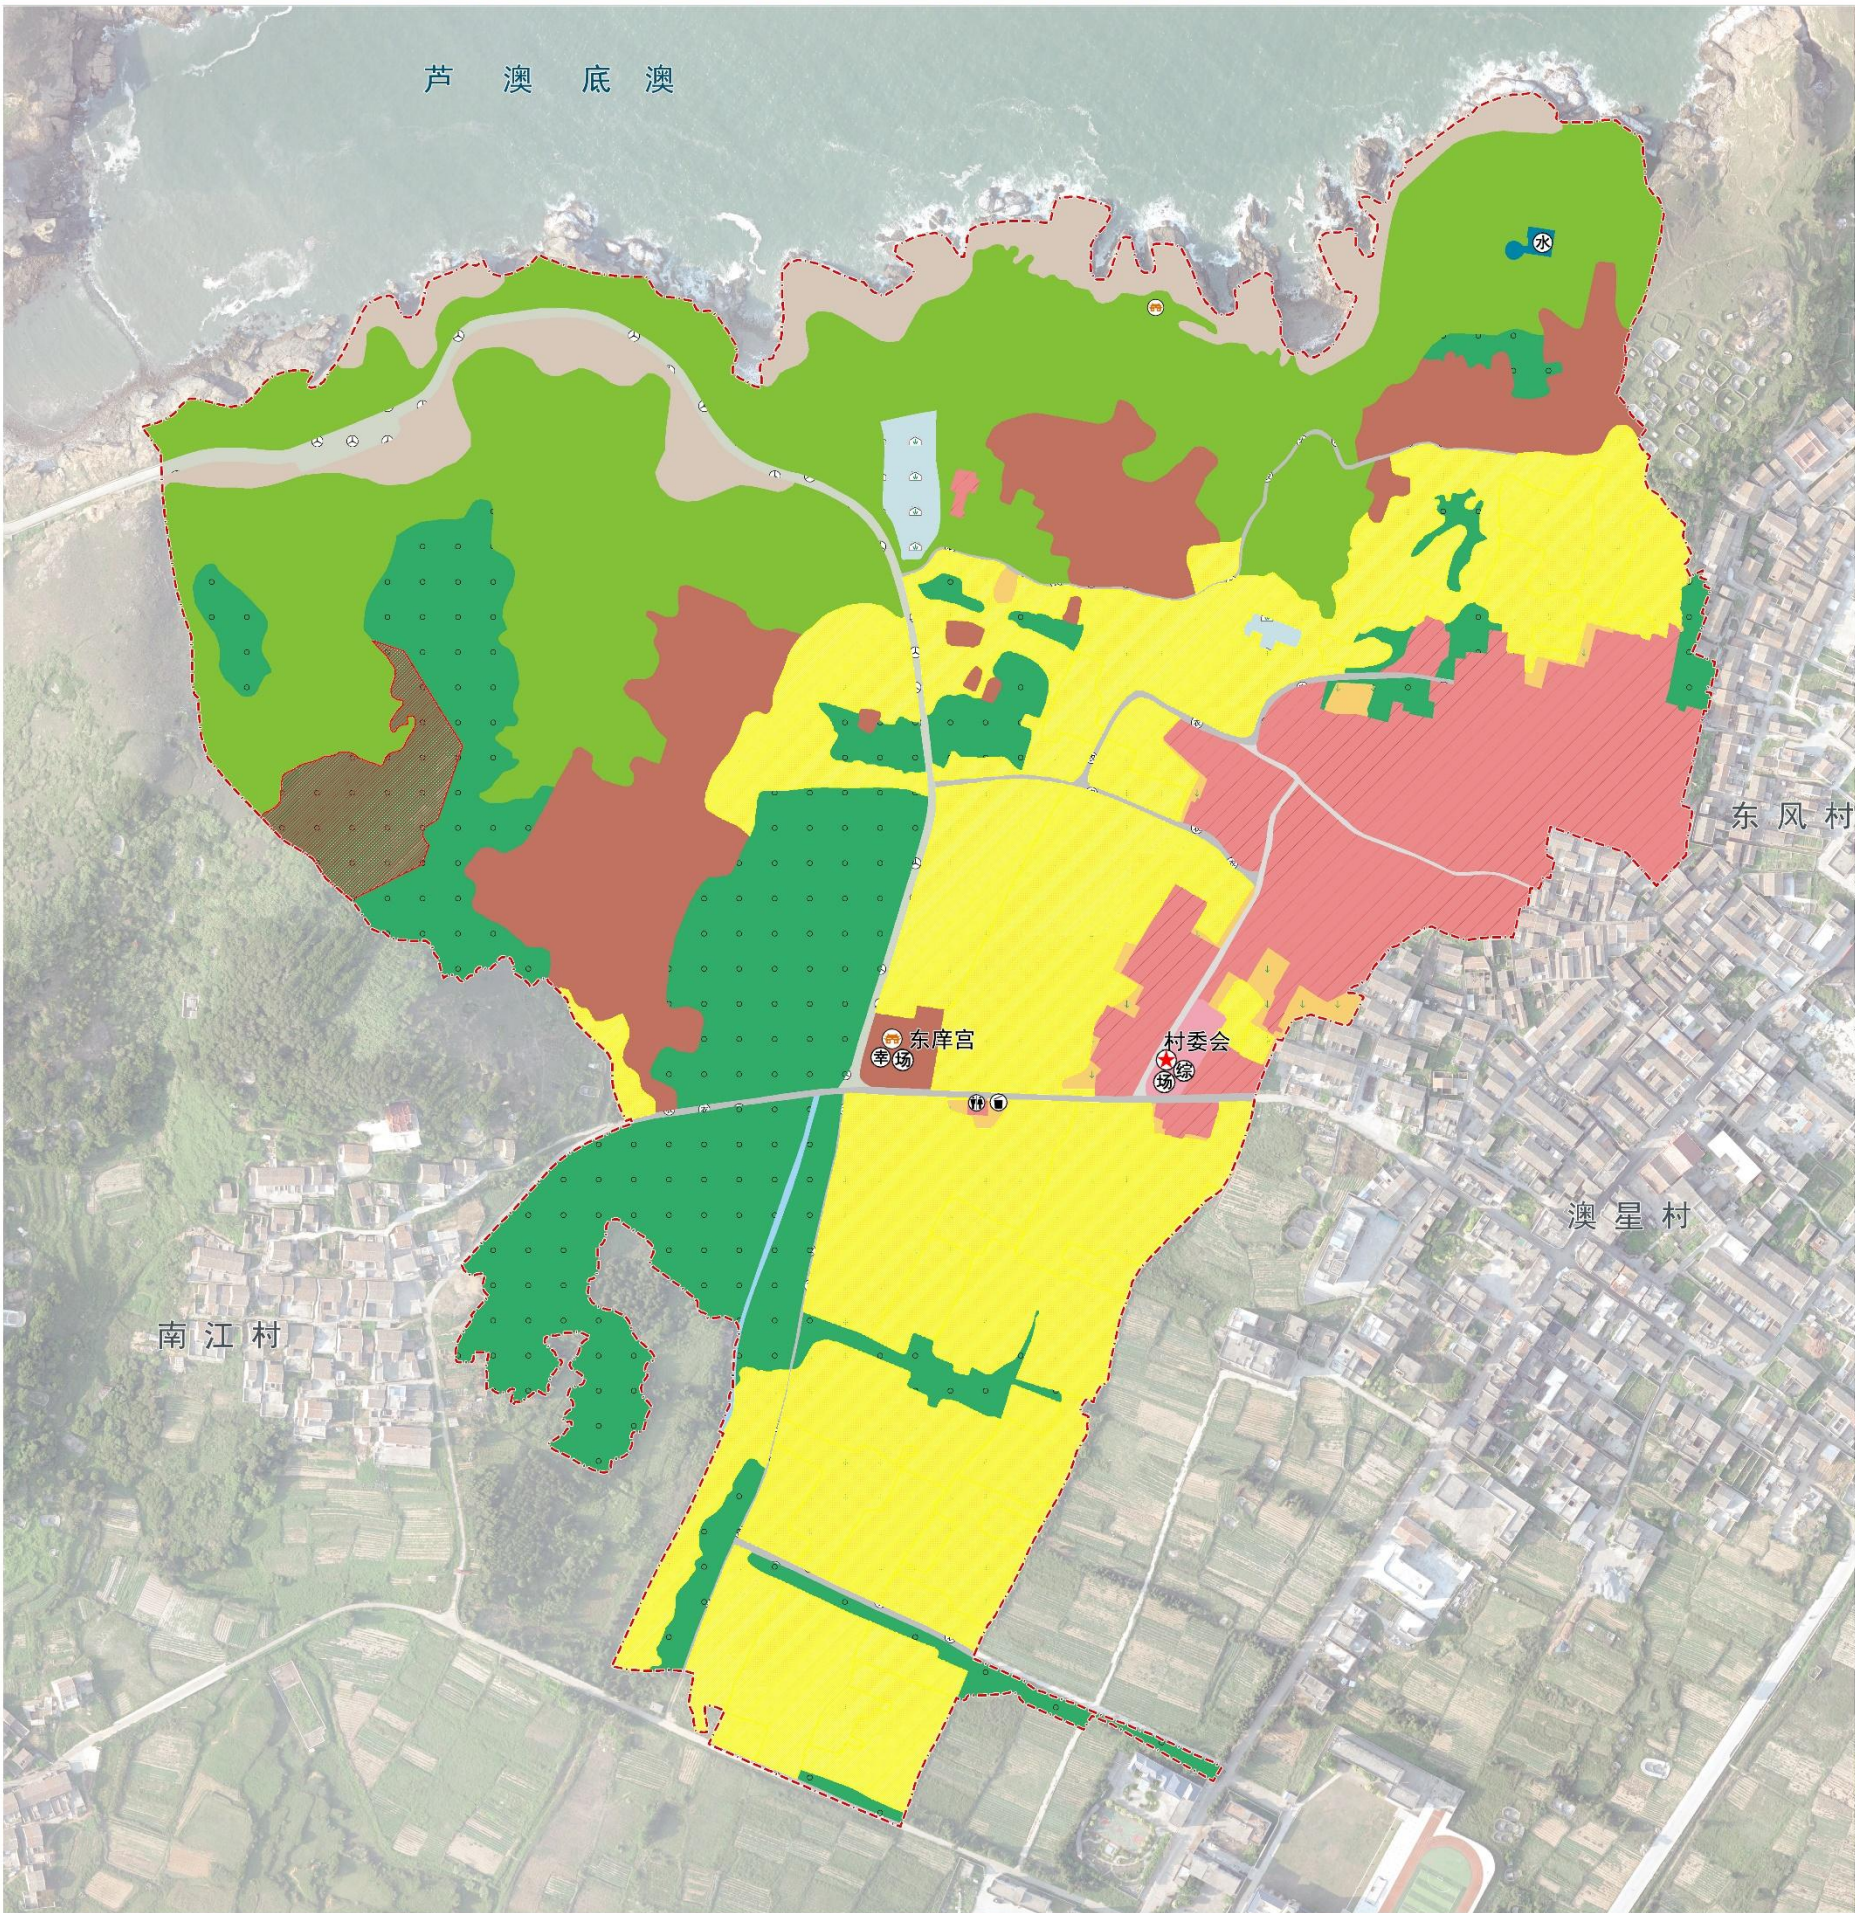

风玫瑰与比例尺

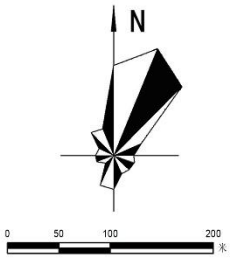

区位图



图例

- 村行政区界限

永久基本农田

生态保护红线

公共管理与公共服务用地

公用设施用地

公路用地

其他土地

农村宅基地

村庄内部道路用地

村道用地

林地

水产养殖设施建设用地

特殊用地

耕地

草地

陆地水域

村委会

综合服务中心

室外活动场地

公共厕所

垃圾收集点

宗祠寺庙

供水设施


幸福院
- 村域用地现状表
- | 用地用海类型 | | 规划基期年 | | | |
|----------|------------|------------|-------------|-------|------|
| | | 面积（公顷） | 比重（%） | | |
| 耕地（01） | | 13.67 | 30.21 | | |
| 园地（02） | | 0.00 | 0.00 | | |
| 林地（03） | | 8.38 | 18.52 | | |
| 草地（04） | | 10.94 | 24.17 | | |
| 湿地（05） | | 0.00 | 0.00 | | |
| 合计 | | 32.99 | 72.90 | | |
| 农业设施建设用地 | 村道用地 | 0.55 | 1.22 | | |
| | 种植设施建设用地 | 0.00 | 0.00 | | |
| | 畜禽养殖设施建设用地 | 0.00 | 0.00 | | |
| | 水产养殖设施建设用地 | 0.27 | 0.59 | | |
| | 合计 | 0.82 | 1.81 | | |
| 村域建设用地 | 村域城乡建设用地 | 城镇用地 | 0.00 | 0.00 | |
| | | 农村社区服务设施用地 | 居住用地 | 0.00 | 0.00 |
| | | | 农村宅基地 | 4.29 | 9.49 |
| | | 村庄建设用地 | 公共管理与公共服务用地 | 0.12 | 0.26 |
| | | | 商业服务业用地 | 0.00 | 0.00 |
| | | | 工业用地 | 0.00 | 0.00 |
| | | | 仓储用地 | 0.00 | 0.00 |
| | | | 村庄内部道路用地 | 0.11 | 0.24 |
| | | | 交通场站用地 | 0.00 | 0.00 |
| | | | 其他交通设施用地 | 0.00 | 0.00 |
| | | | 公用设施用地 | 0.03 | 0.07 |
| | | | 绿地与开敞空间用地 | 0.00 | 0.00 |
| | | | 留白用地 | 0.00 | 0.00 |
| | | | 空闲地 | 0.00 | 0.00 |
| | | 合计 | 4.56 | 10.07 | |
| | | 区域基础设施用地 | 4.56 | 10.07 | |
| | | 其他建设用地 | 0.51 | 1.13 | |
| | | 合计 | 4.13 | 9.12 | |
| 合计 | | 9.19 | 20.32 | | |
| 陆地水域 | | 0.06 | 0.12 | | |
| 渔业用海 | | 0.00 | 0.00 | | |
| 工矿通信用海 | | 0.00 | 0.00 | | |
| 交通运输用海 | | 0.00 | 0.00 | | |
| 游憩用海 | | 0.00 | 0.00 | | |
| 特殊用海 | | 0.00 | 0.00 | | |
| 其他土地 | | 2.19 | 4.84 | | |
| 其他海域 | | 0.00 | 0.00 | | |
| 总计 | | 45.26 | 100.00 | | |




平潭综合实验区君山片区东庠乡东进村村庄规划（2023-2035）

VILLAGE PLANNING OF DONGJIN VILLAGE, DONGXIANG TOWNSHIP

村域综合规划图

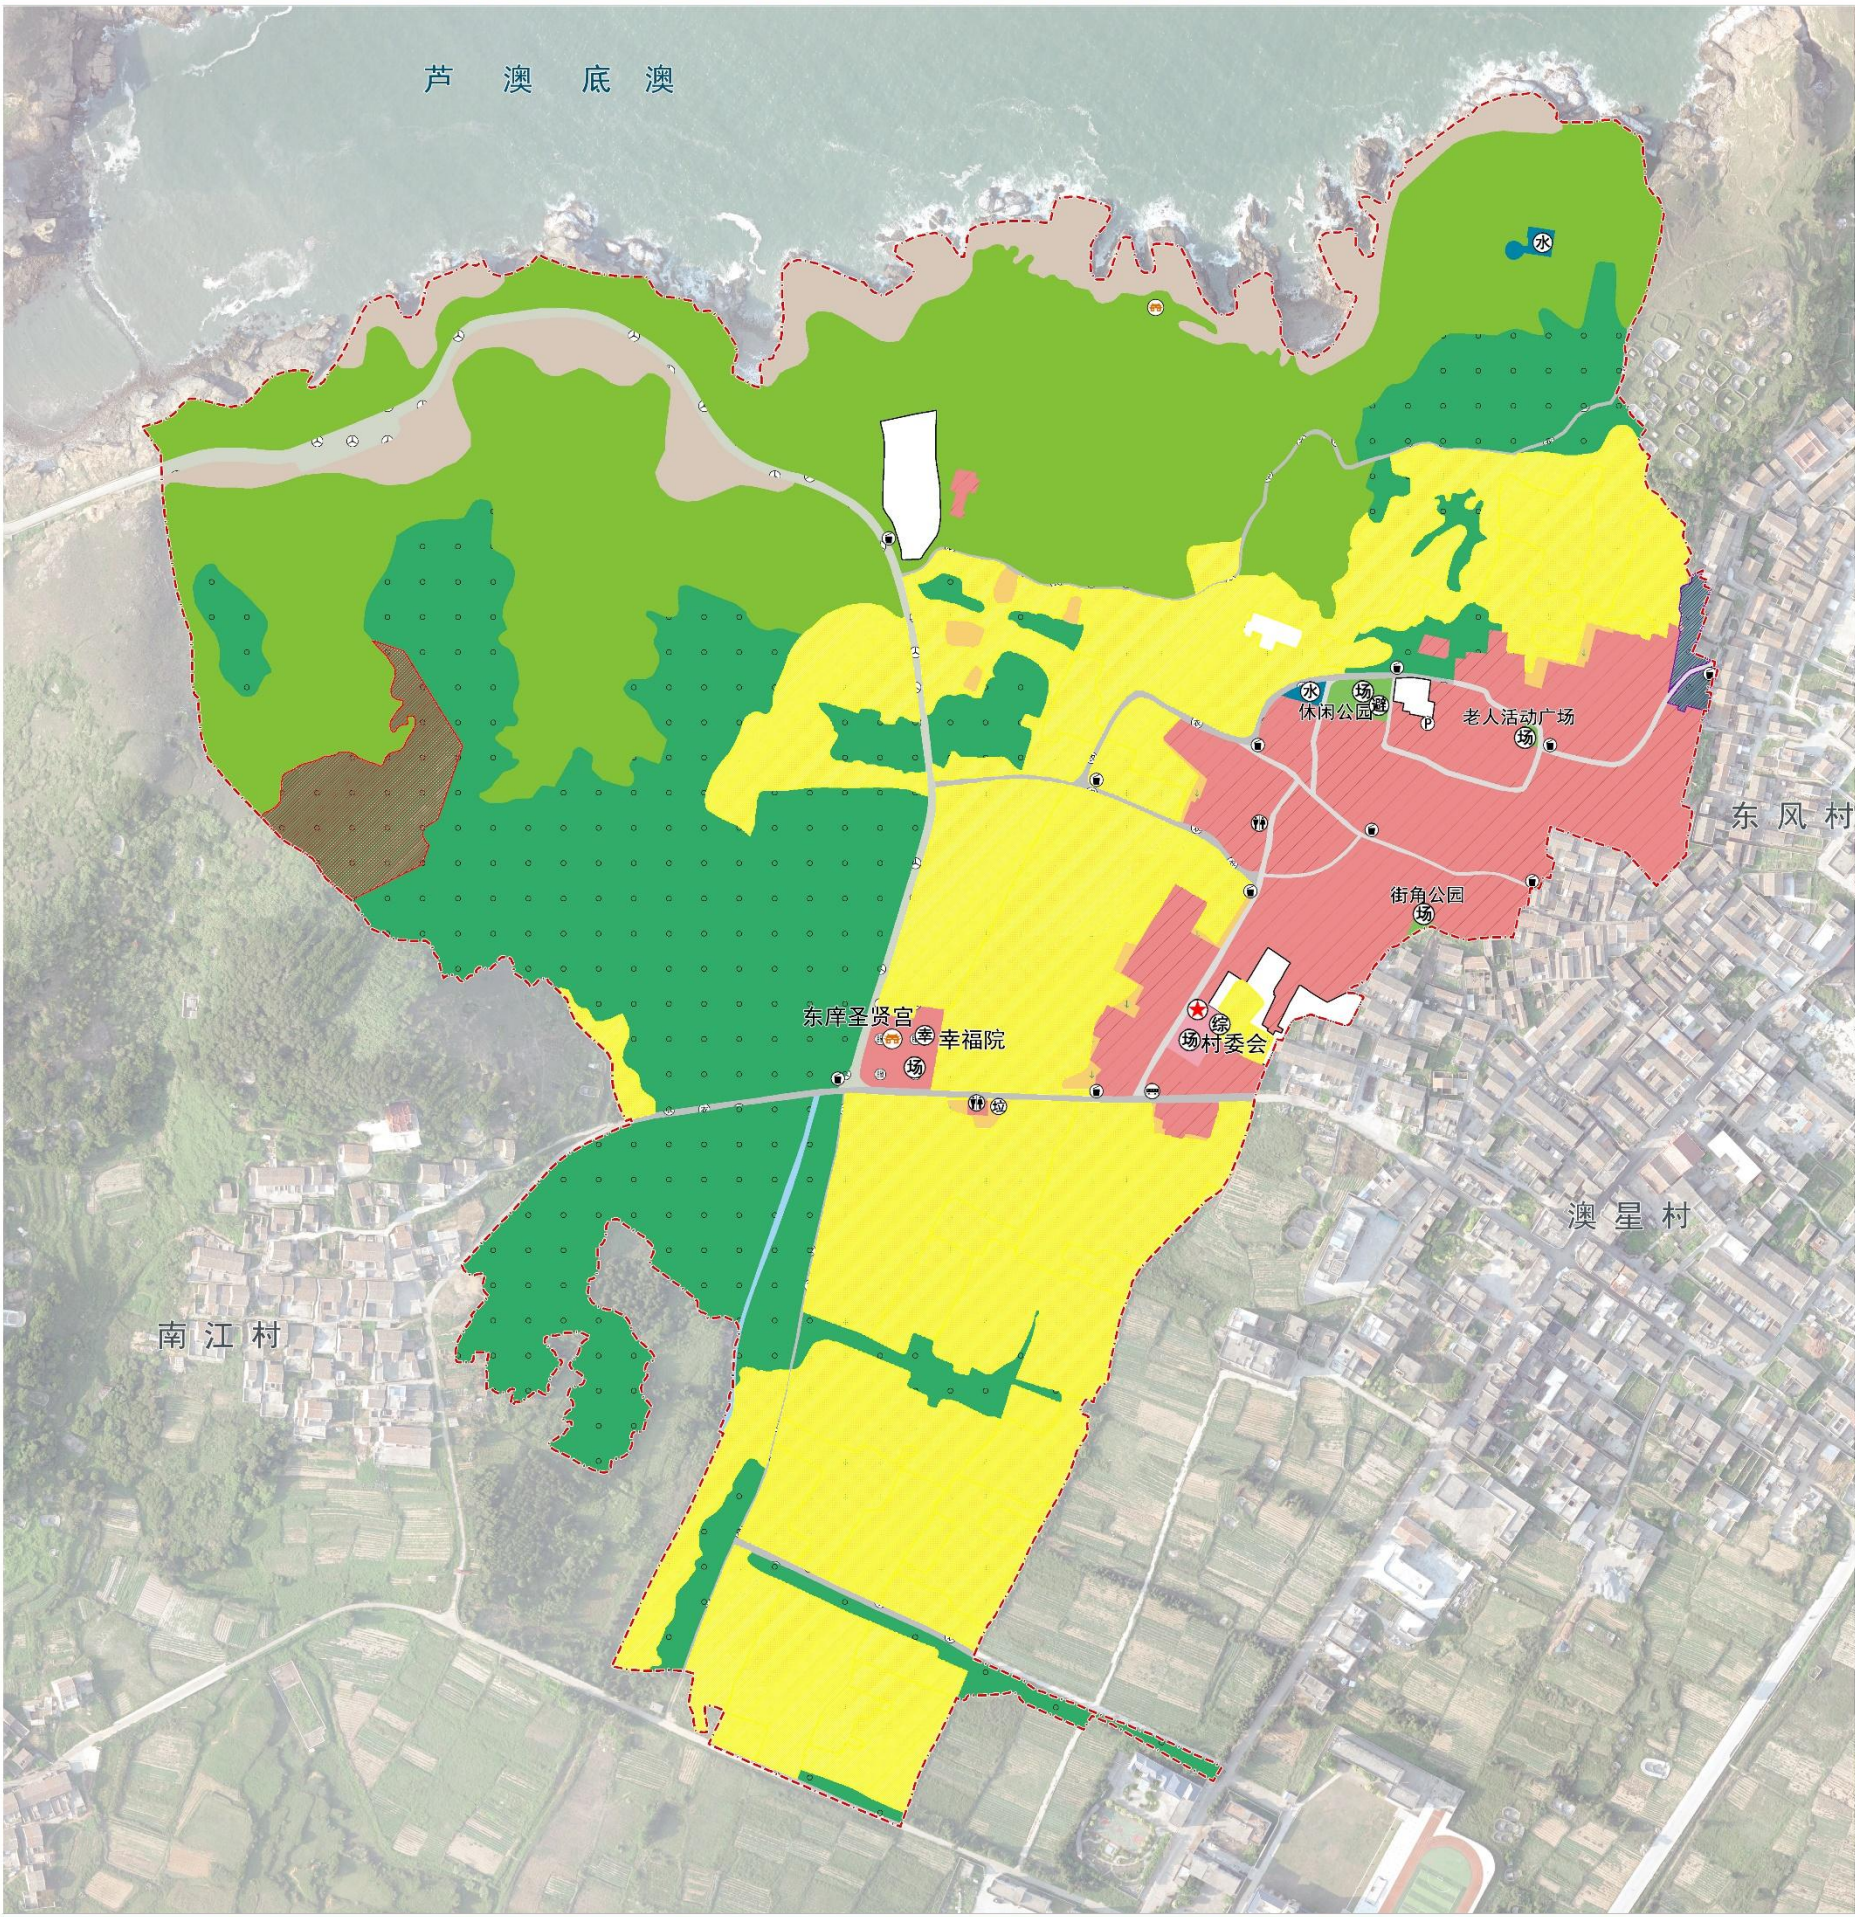

风玫瑰与比例尺

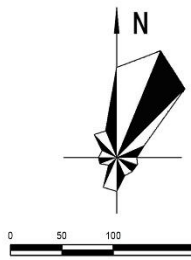

区位图



图例

- 村行政区界限

永久基本农田

生态保护红线

村庄弹性发展区

公共管理与公共服务用地

公用设施用地

公路用地

其他土地

农村宅基地

农村社区服务设施用地

村庄内部道路用地

村道用地

林地

水产养殖设施建设用地

留白用地

绿地与开敞空间用地

耕地

草地

陆地水域
- 村委会

综合服务中心

室外活动场地

公共厕所

垃圾收集点

宗祠寺庙

供水设施

幸福院

农村避灾点

垃圾转运站

停车场

城乡公交停靠点

空间功能结构调整表


用地用海类型		规划基期年		规划目标年		用地调整（公顷）
		面积（公顷）	比重（%）	面积（公顷）	比重（%）	
耕地（01）		13.67	30.21	13.55	29.95	-0.12
园地（02）		0.00	0.00	0.00	0.00	0.00
林地（03）		8.38	18.52	11.35	25.07	2.96
草地（04）		10.94	24.17	11.81	26.11	0.88
湿地（05）		0.00	0.00	0.00	0.00	0.00
合计		32.99	72.90	36.71	81.13	3.72
农业设施建设用地	村道用地	0.55	1.22	0.57	1.26	0.02
	种植设施建设用地	0.00	0.00	0.00	0.00	0.00
	畜禽养殖设施建设用地	0.00	0.00	0.00	0.00	0.00
	水产养殖设施建设用地	0.27	0.59	0.00	0.00	-0.27
合计		0.82	1.81	0.57	1.26	-0.25
村域建设用地	村域城乡建设用地	城镇用地	0.00	0.00	0.00	0.00
		居住用地	0.00	0.00	0.18	0.18
		农村社区服务设施用地	4.29	9.49	4.14	-0.16
		农村宅基地	0.12	0.26	0.07	-0.05
		公共管理与公共服务用地	0.00	0.00	0.00	0.00
		商业服务业用地	0.00	0.00	0.00	0.00
		工业用地	0.00	0.00	0.00	0.00
		仓储用地	0.00	0.00	0.00	0.00
		交通用地	0.11	0.24	0.24	0.13
		其他交通设施用地	0.00	0.00	0.00	0.00
		公用设施用地	0.03	0.07	0.05	0.02
		绿地与开敞空间用地	0.00	0.00	0.09	0.09
		留白用地	0.00	0.00	0.44	0.44
		空闲地	0.00	0.00	0.00	0.00
		合计	4.56	10.07	5.21	0.65
	区域基础设施用地	4.56	10.07	5.21	11.52	0.65
	其他建设用地	0.51	1.13	0.51	1.13	0.00
合计		4.13	9.12	0.00	0.00	-4.13
合计		9.19	20.32	5.72	12.64	-3.47
陆地水域		0.06	0.12	0.06	0.12	0.00
渔业用海		0.00	0.00	0.00	0.00	0.00
工矿通信用海		0.00	0.00	0.00	0.00	0.00
交通运输用海		0.00	0.00	0.00	0.00	0.00
游憩用海		0.00	0.00	0.00	0.00	0.00
特殊用海		0.00	0.00	0.00	0.00	0.00
其他土地		2.19	4.84	2.19	4.84	0.00
其他海域		0.00	0.00	0.00	0.00	0.00
总计		45.26	100.00	45.26	100.00	0.00




平潭综合实验区君山片区东庠乡东进村村庄规划（2023-2035）

VILLAGE PLANNING OF DONGJIN VILLAGE,DONGXIANG TOWNSHIP

农村居民点规划布局图

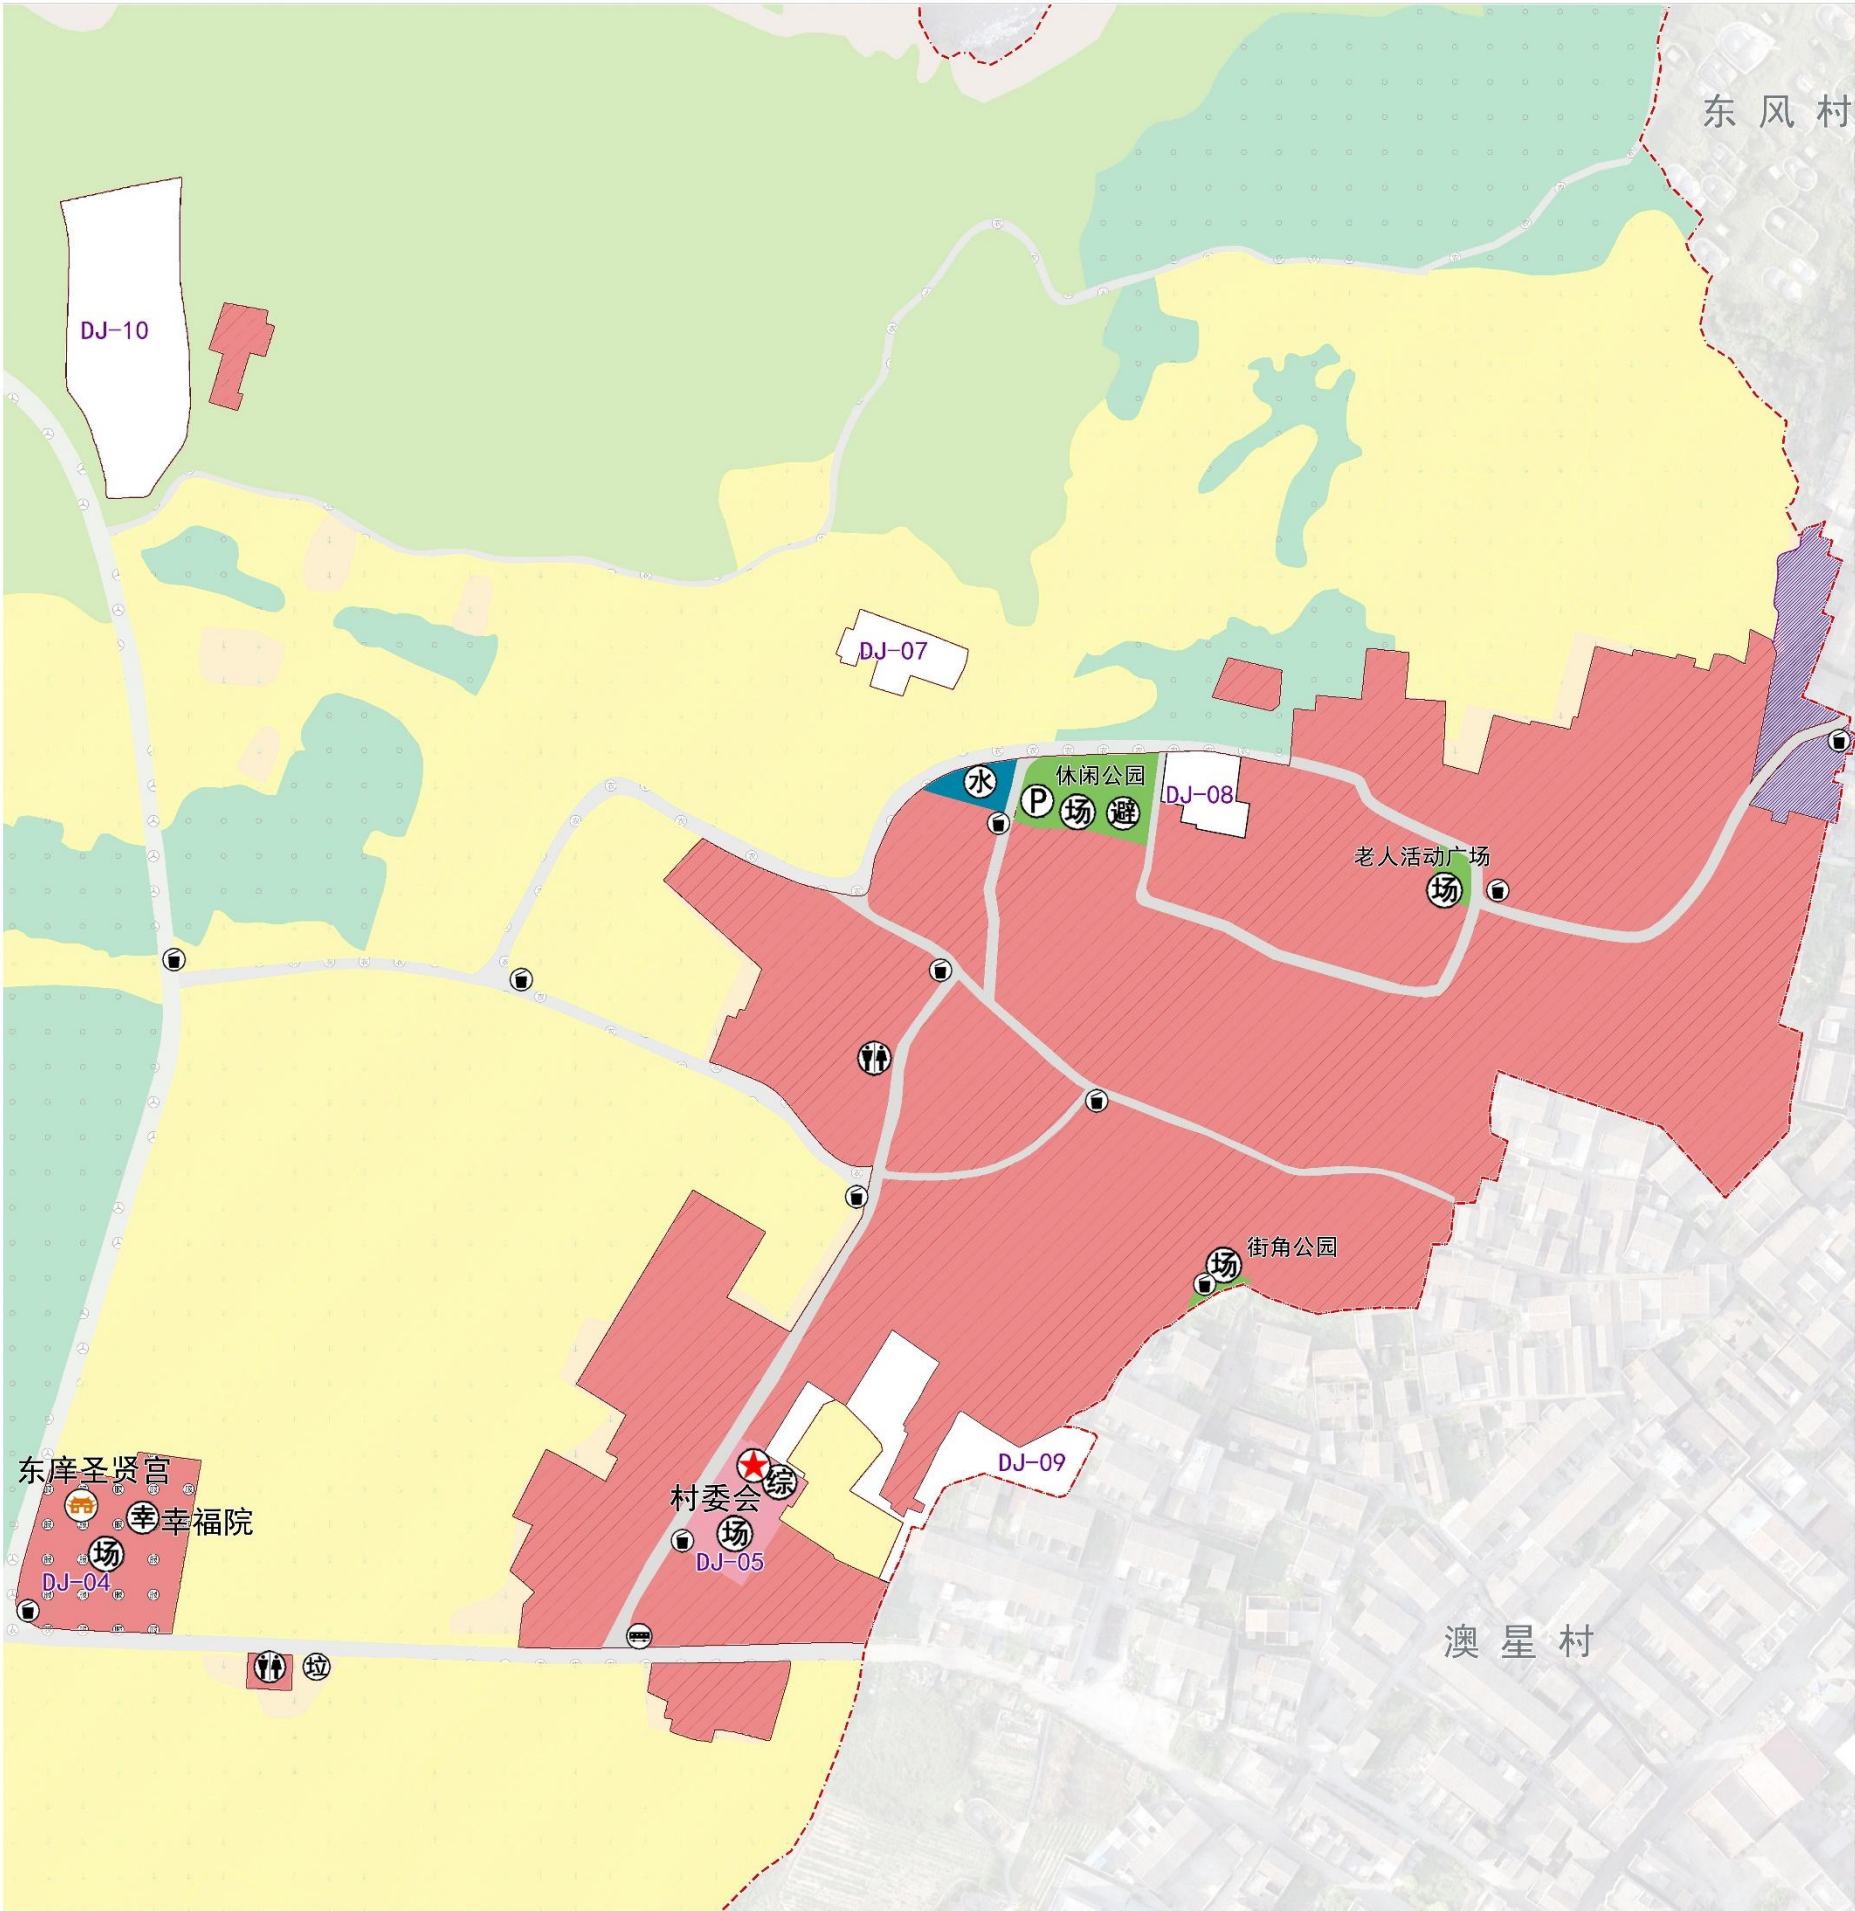

风玫瑰与比例尺

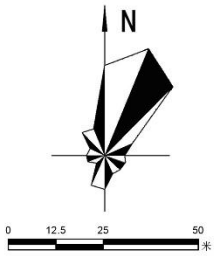

区位图



图例

- 村行政区界限

永久基本农田

生态保护红线

村庄弹性发展区

村庄建设边界

公共管理与公共服务用地

公用设施用地

公路用地

其他土地

农村宅基地

农村社区服务设施用地

村庄内部道路用地

村道用地

林地

水产养殖设施建设用地

留白用地

绿地与开敞空间用地

耕地

草地

陆地水域
- 村委会

综合服务中心

室外活动场地

公共厕所

垃圾收集点

宗祠寺庙

供水设施

幸福院

农村避灾点

垃圾转运站

停车场

城乡公交停靠点

指标一览表

地块编号	用地			建筑高度	名称	地块指引
	用地代码	用地性质	地块面积 (m²)			
DJ-01	14	绿地与开敞空间用地	712	限高12m	休闲公园	整理现状场地，拆除破旧建筑，改造为绿地空间，配套健身器材，增加绿化
DJ-02	14	绿地与开敞空间用地	133	限高12m	老人活动广场	现状村庄独居老人人数较多，选址居民点内部中心地段增设老人休闲活动场所，增设休闲座椅、凉亭等，方便村内老年人交流活动
DJ-03	14	绿地与开敞空间用地	85	限高12m	街角公园	利用街头空闲地打造街角小公园，提升绿化景观，满足村民休闲活动。
DJ-04	0704	农村社区服务设施用地	1764	限高12m	老人幸福院	提升老人幸福院，增设活动室、棋牌室、餐厅、医疗室等配套设施
DJ-05	08	公共管理与公共服务用地	686	限高12m	党群服务中心	结合现状村委会改造党群服务中心，扩大现状村委楼建设，增设广播室、文服中心等功能
DJ-06	1301	公用设施用地	200	限高12m	水塔建设	利用废旧水塔场地，重新改造设置水塔，提升内部设
DJ-07	16	留白用地	1200	限高12m		
DJ-08	16	留白用地	392	限高12m	零星建房	居民点住宅建筑以保留以及改造为主，原则上不大量新增基地；此地块拟用于预备近期村民建房需求
DJ-09	16	留白用地	433	限高12m		
DJ-10	16	留白用地	2249	限高12m	留白用地	现状村内闲置水产养殖厂，远期可结合产业改造利用

居民点管控规则

村庄公共设施：提升党群服务中心、配建文化服务中心、室内活动场地，附设村邮所、广播室等功能。结合现状东庠宫设置提升老人幸福院附设食堂餐厅、床位等功能；居民点内部利用空闲地改造活动场所，提供村民活动空间，配套相关休闲娱乐设施。

道路交通设施：对外交通主要为现状村庄主干道，村庄内部道路交通沿用村中已有的道路，打通部分端头路，在原有的基础上维护；拆除部分质量较差建筑，优化道路线行，满足道路规范要求；利用街头空闲地改建停车场。局部村道未硬化，近期建议采用柏油硬化水泥路面，并提升两侧绿化环境；


市政设施：沿道路按30-50m距离设置垃圾收集点，按服务半径约300m配建公厕，居民点内部增设一处公厕，服务游客和村民；完善村庄水电配套，远期采用雨污分离排放模式，按照不大于120m的距离配建消防栓，文保单位重点设置。

村庄住宅管制：村庄居民点住宅建筑以保留及改造为主，原则上不大量新增宅基地，严禁核心保护区内开发建设村民住宅，建设控制地带内严控建设高度、体量、色彩，严格按照本次设计户型建设，风貌与村落协调一致。建筑严格按照“一户一宅”政策，每户宅基地面积控制在120m²以内，新建住宅高度不得超过12m，每户住宅面积控制在300m²以内，住宅建筑间距与前建筑高度比不低于1:1，相邻建筑山墙间距不低于2m，建筑宜朝南、南偏东或偏西布置，建筑后退村庄道路不得少于1m。

村民建房应当遵守相关技术标准规定，详见《福州市规范农村宅基地和建房管理实施细则（试行）》



风玫瑰与比例尺

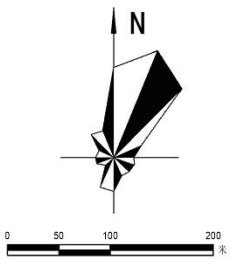

区位图



图例

- | | | | |
|--------|--------|---------|------|
| 公共建筑 | 室外活动场地 | 城乡公交停靠点 | 古民居 |
| 村委会 | 幸福院 | 停车场 | 宗祠寺庙 |
| 综合服务中心 | 村卫生所 | 垃圾转运站 | 古街古巷 |
| 文化站 | 集贸市场 | 垃圾收集点 | 古树 |
| 中学 | 村邮站 | 污水处理设施 | 古井 |
| 小学 | 公共厕所 | 农村避灾点 | 古桥 |
| 幼儿园 | 供水设施 | 电力设施 | |

村域用地现状表

9mX13m地块
(二层住宅模式)



村民建房应当遵守以下技术标准规定：

(一) 规划：村民建房要符合国土空间总体规划及各类专项规划，靠近城市、县城、乡镇所在地住宅小区，引导参照城市居住区规划设计相关标准，鼓励建设多层单元式住宅。

(二) 选址：村民建房选址应避开地质复杂、地基承载力差、地势低洼不易排涝以及易受风口、滑坡、雷电和洪水侵袭等自然灾害影响的地段，杜绝安全隐患问题。

- (三) 层数和面积：农村独栋式、并联式或联排式自建住宅不得超过三层，每户住宅建筑面积控制在300平方米以内；多层单元式住宅的，每户住宅建筑面积控制在200平方米左右。
- (四) 层高：一层层高控制在4.5米以内，二层以上层高控制在3.3米以内，建筑总高度不超过12米，建筑屋顶原则上应按坡屋顶设计。
- (五) 间距和朝向：住宅建筑前后间距与建筑高度比一般不低于1:1，相邻房屋山墙之间（外墙至外墙）的间距不低于4米，建筑宜朝南、朝南偏东或偏西布置。新建建筑宜后退村庄干路红线3米以上，后退村庄支路红线1米以上。因旧房改造、扩建等受用地条件限制的，根据实际情况由属地乡镇人民政府合理确定相邻距离。
- (六) 抗震：新建住宅必须符合工程抗震设防要求，板、梁、柱不得采用石结构。
- (七) 建筑单体：应满足村民生产生活需求，住宅平面布局应设有客厅、卧室、厨房、卫生间、储藏间（农具堆放间）应满足面积、通风、采光等要求。房屋造型简洁美观，宜采用坡屋面，符合地方建筑特色，外观应进行一次装修。
- (八) 配套：应同步配建化粪池等处理设施；集中建设住宅小区的，给水排水、电力通信、道路、广电、绿化和社区服务等配套设施要同步规划建设，小区建筑密度控制在30%左右，绿地率不低于30%。


其他细则参考《福州市规范农村宅基地和建房管理实施细则(试行)》。




平潭综合实验区君山片区东庠乡东进村村庄规划（2023-2035）

VILLAGE PLANNING OF DONGJIN VILLAGE,DONGXIANG TOWNSHIP

近期实施项目图

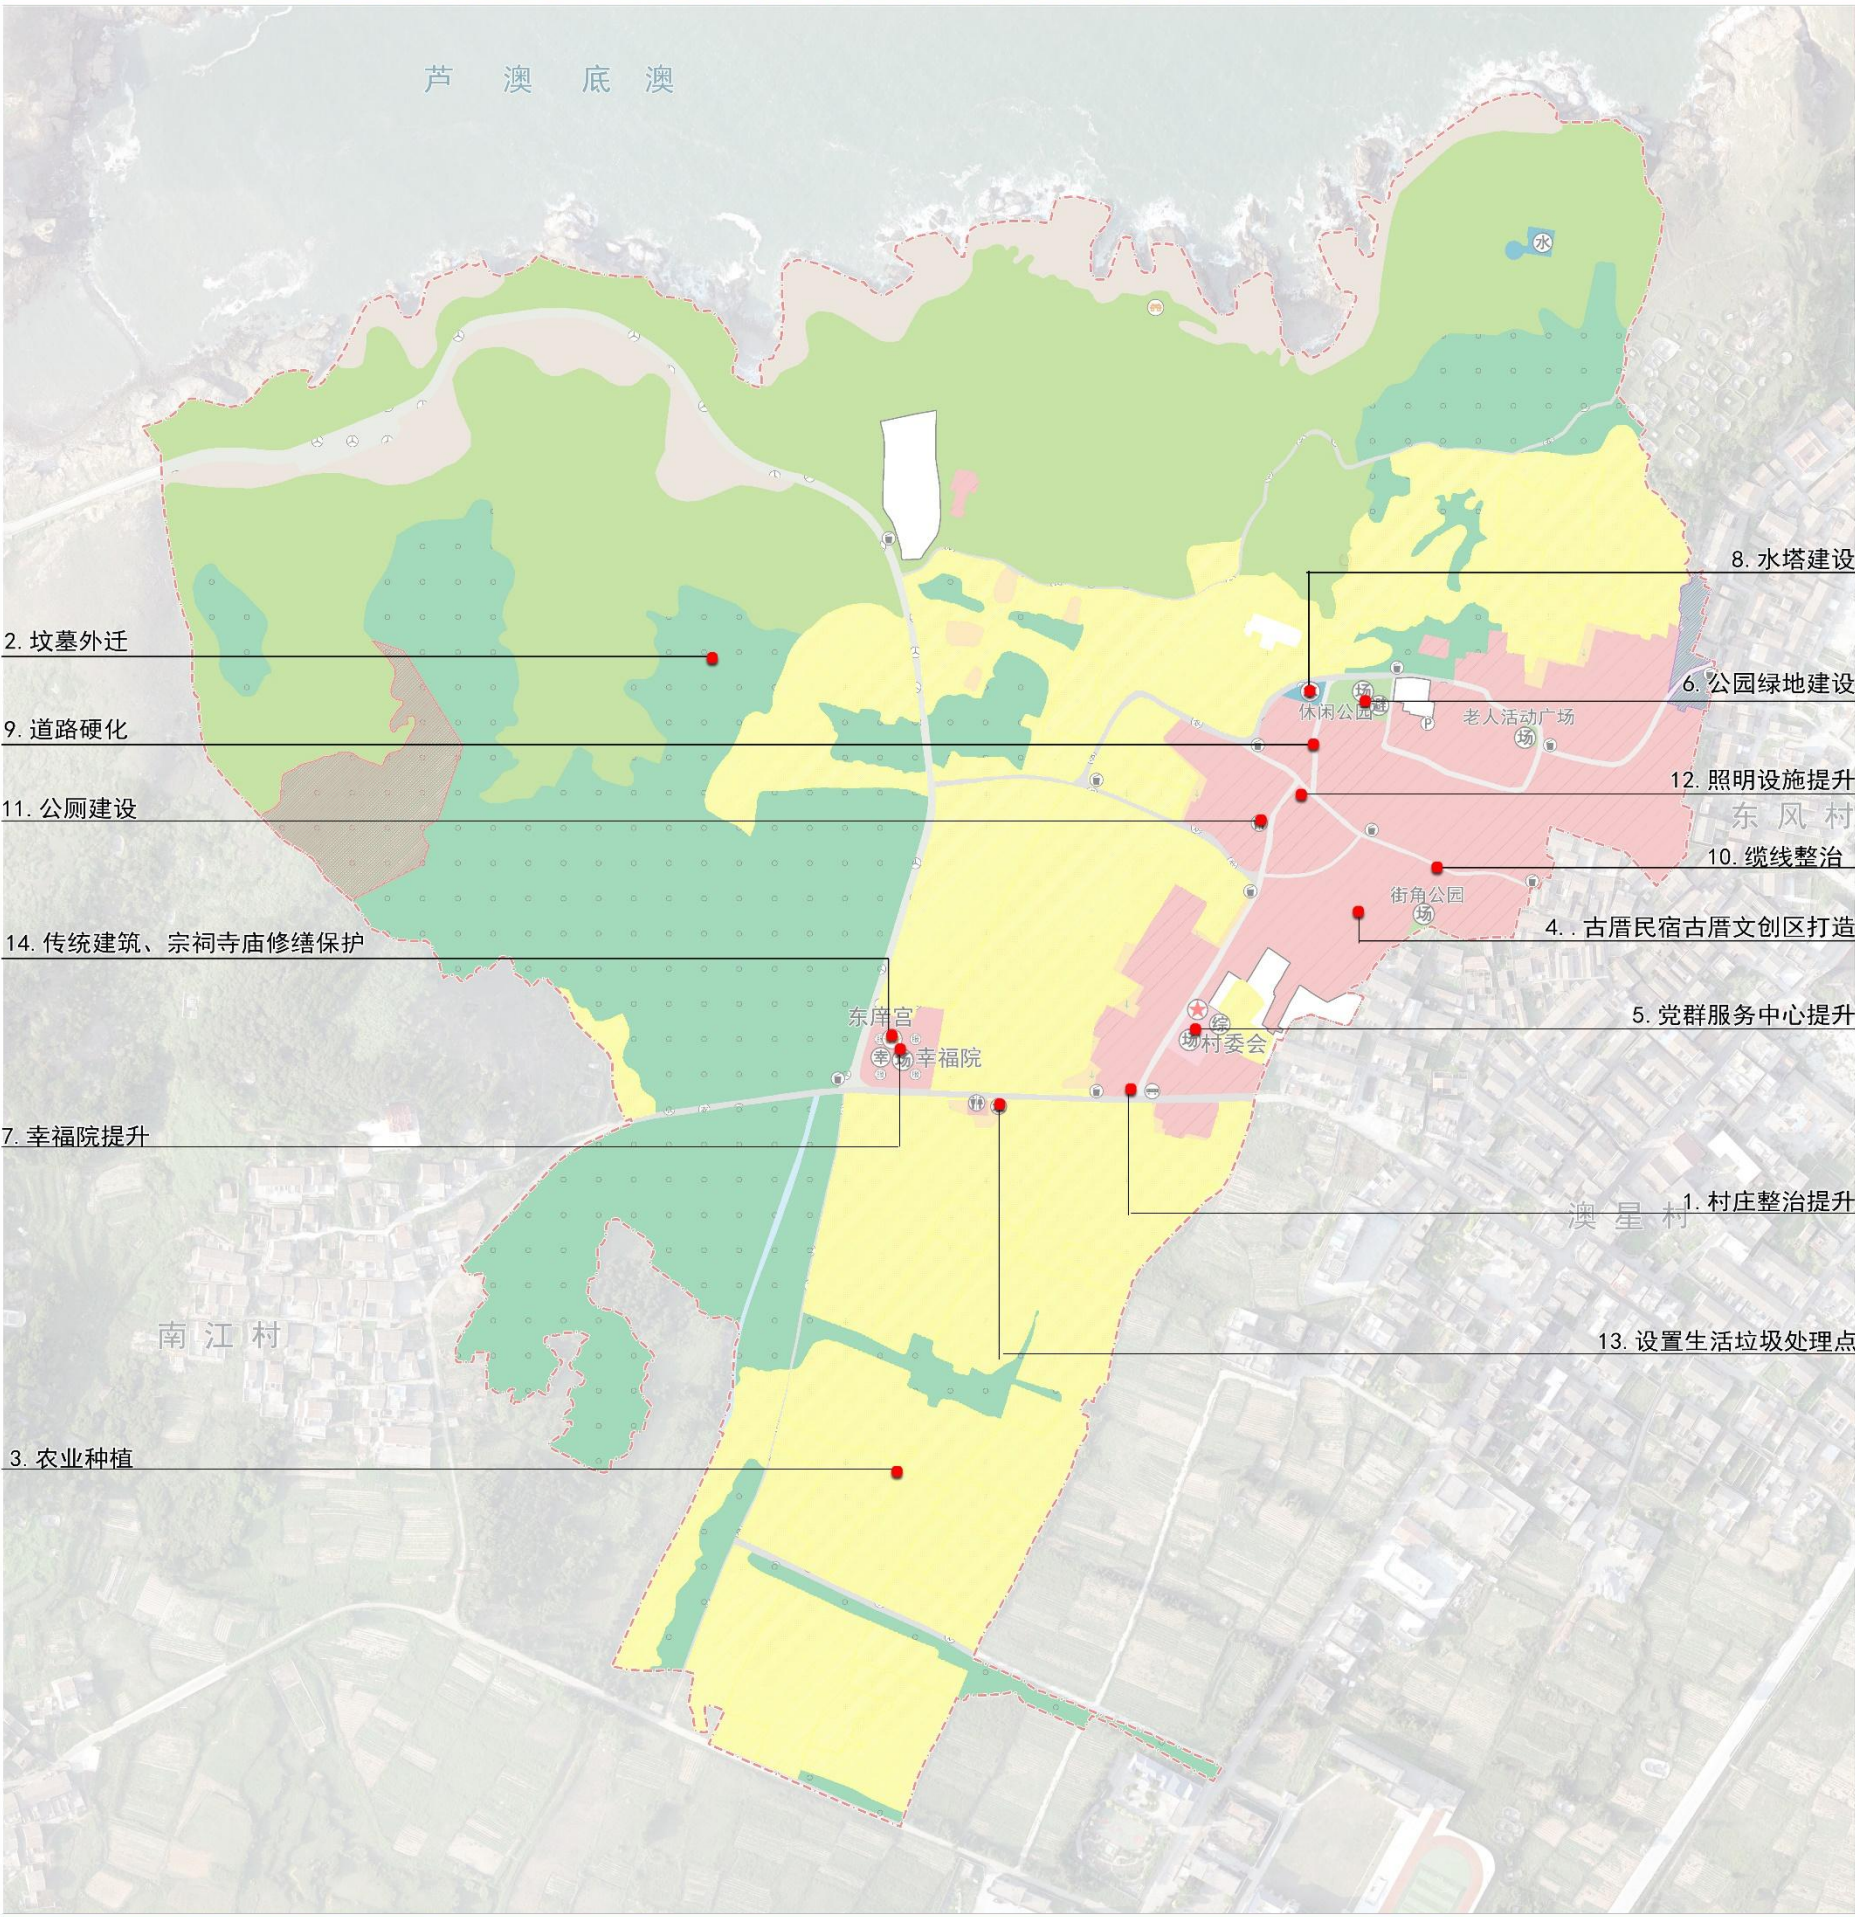

风玫瑰与比例尺

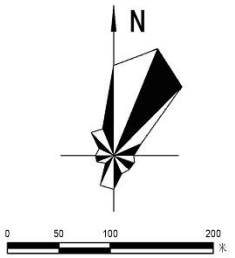

区位图



近期实施项目表

序号	项目类型	项目名称	建设年限	投资额(万元)	建议资金来源	开发主体	用地面积(平方米)	其他
1	村庄整治提升	村庄入口区域改造, 村落环境整治、边角空间利用、特色节点打造	2023-2025	20	村财	村	-	建筑宅前屋后整理、建筑周边环境提升, 村容村貌治理, 村庄生活环境整治。
2	生态修复国土整治	坟墓外迁	2023-2028	-	专项资金	专项资金	39508	村落内裸露山林环境治理主要是坟墓外迁, 植树种草、补种绿色植物覆盖
3	产业发展	农业种植	2023-2030	-	专项资金	专项资金	-	充分利用村庄现有耕地资源, 大力发展农业种植, 林下生态种植。
4		休闲文旅产业	2023-2030	-	专项资金	专项资金	-	结合村内建筑改造, 打造村落古厝民宿古厝特色美食, 注入文创馆、民俗厅等功能; 并修建滨水步道联通规划区内各村
5	公共服务设施	党群服务中心提升	2023-2025	10	村财	村	686	根据村庄发展需求, 利用居民点内现状庙宇改造综合文化服务中心, 完善村内基础服务设施
6		公园绿地建设	2023-2026	15	专项资金	村	930	结合现状闲置建设用地, 改造为活动公园, 进行绿化彩化, 配置活动健身器材
7		幸福院提升	2023-2025	10	专项资金	村	1764	提升老人幸福院, 增设活动室、棋牌室、餐厅、医疗室等配套设施
8	市政基础设施	水塔建设	2023-2026	10	专项资金	村	200	利用废旧水塔场地, 重新改造设置水塔, 提升内部设备, 为村民提供优质水源
9		道路硬化	2023-2027	10	专项资金	财政出资	200	梳理村内路网, 硬化村庄内部道路, 宽度约3米, 进一步完善村庄路网
10		缆线整治	2023-2028	15	村财	村	5860	梳理村内电力线路, 墙面缆线整治入柜, 提升村貌
11		公厕建设	2023-2028	10	村财	村	50	居民点内部废弃厕所所改造新公厕
12		照明设施提升	2023-2028	5	村财	村	1684	对内部道路两侧路灯进行提升增设灯柱
13		设置生活垃圾处理点	2023-2028	5	村财	村	2511	沿着村内道路每隔100米设置一个垃圾桶, 并设置垃圾处理点
14	历史文化保护	传统建筑、宗祠寺庙修缮保护	2023-2025	5	村财	村	4700	周边环境提升以及修缮破损建筑, 宗祠前空地设为小活动广场
合计				115				