




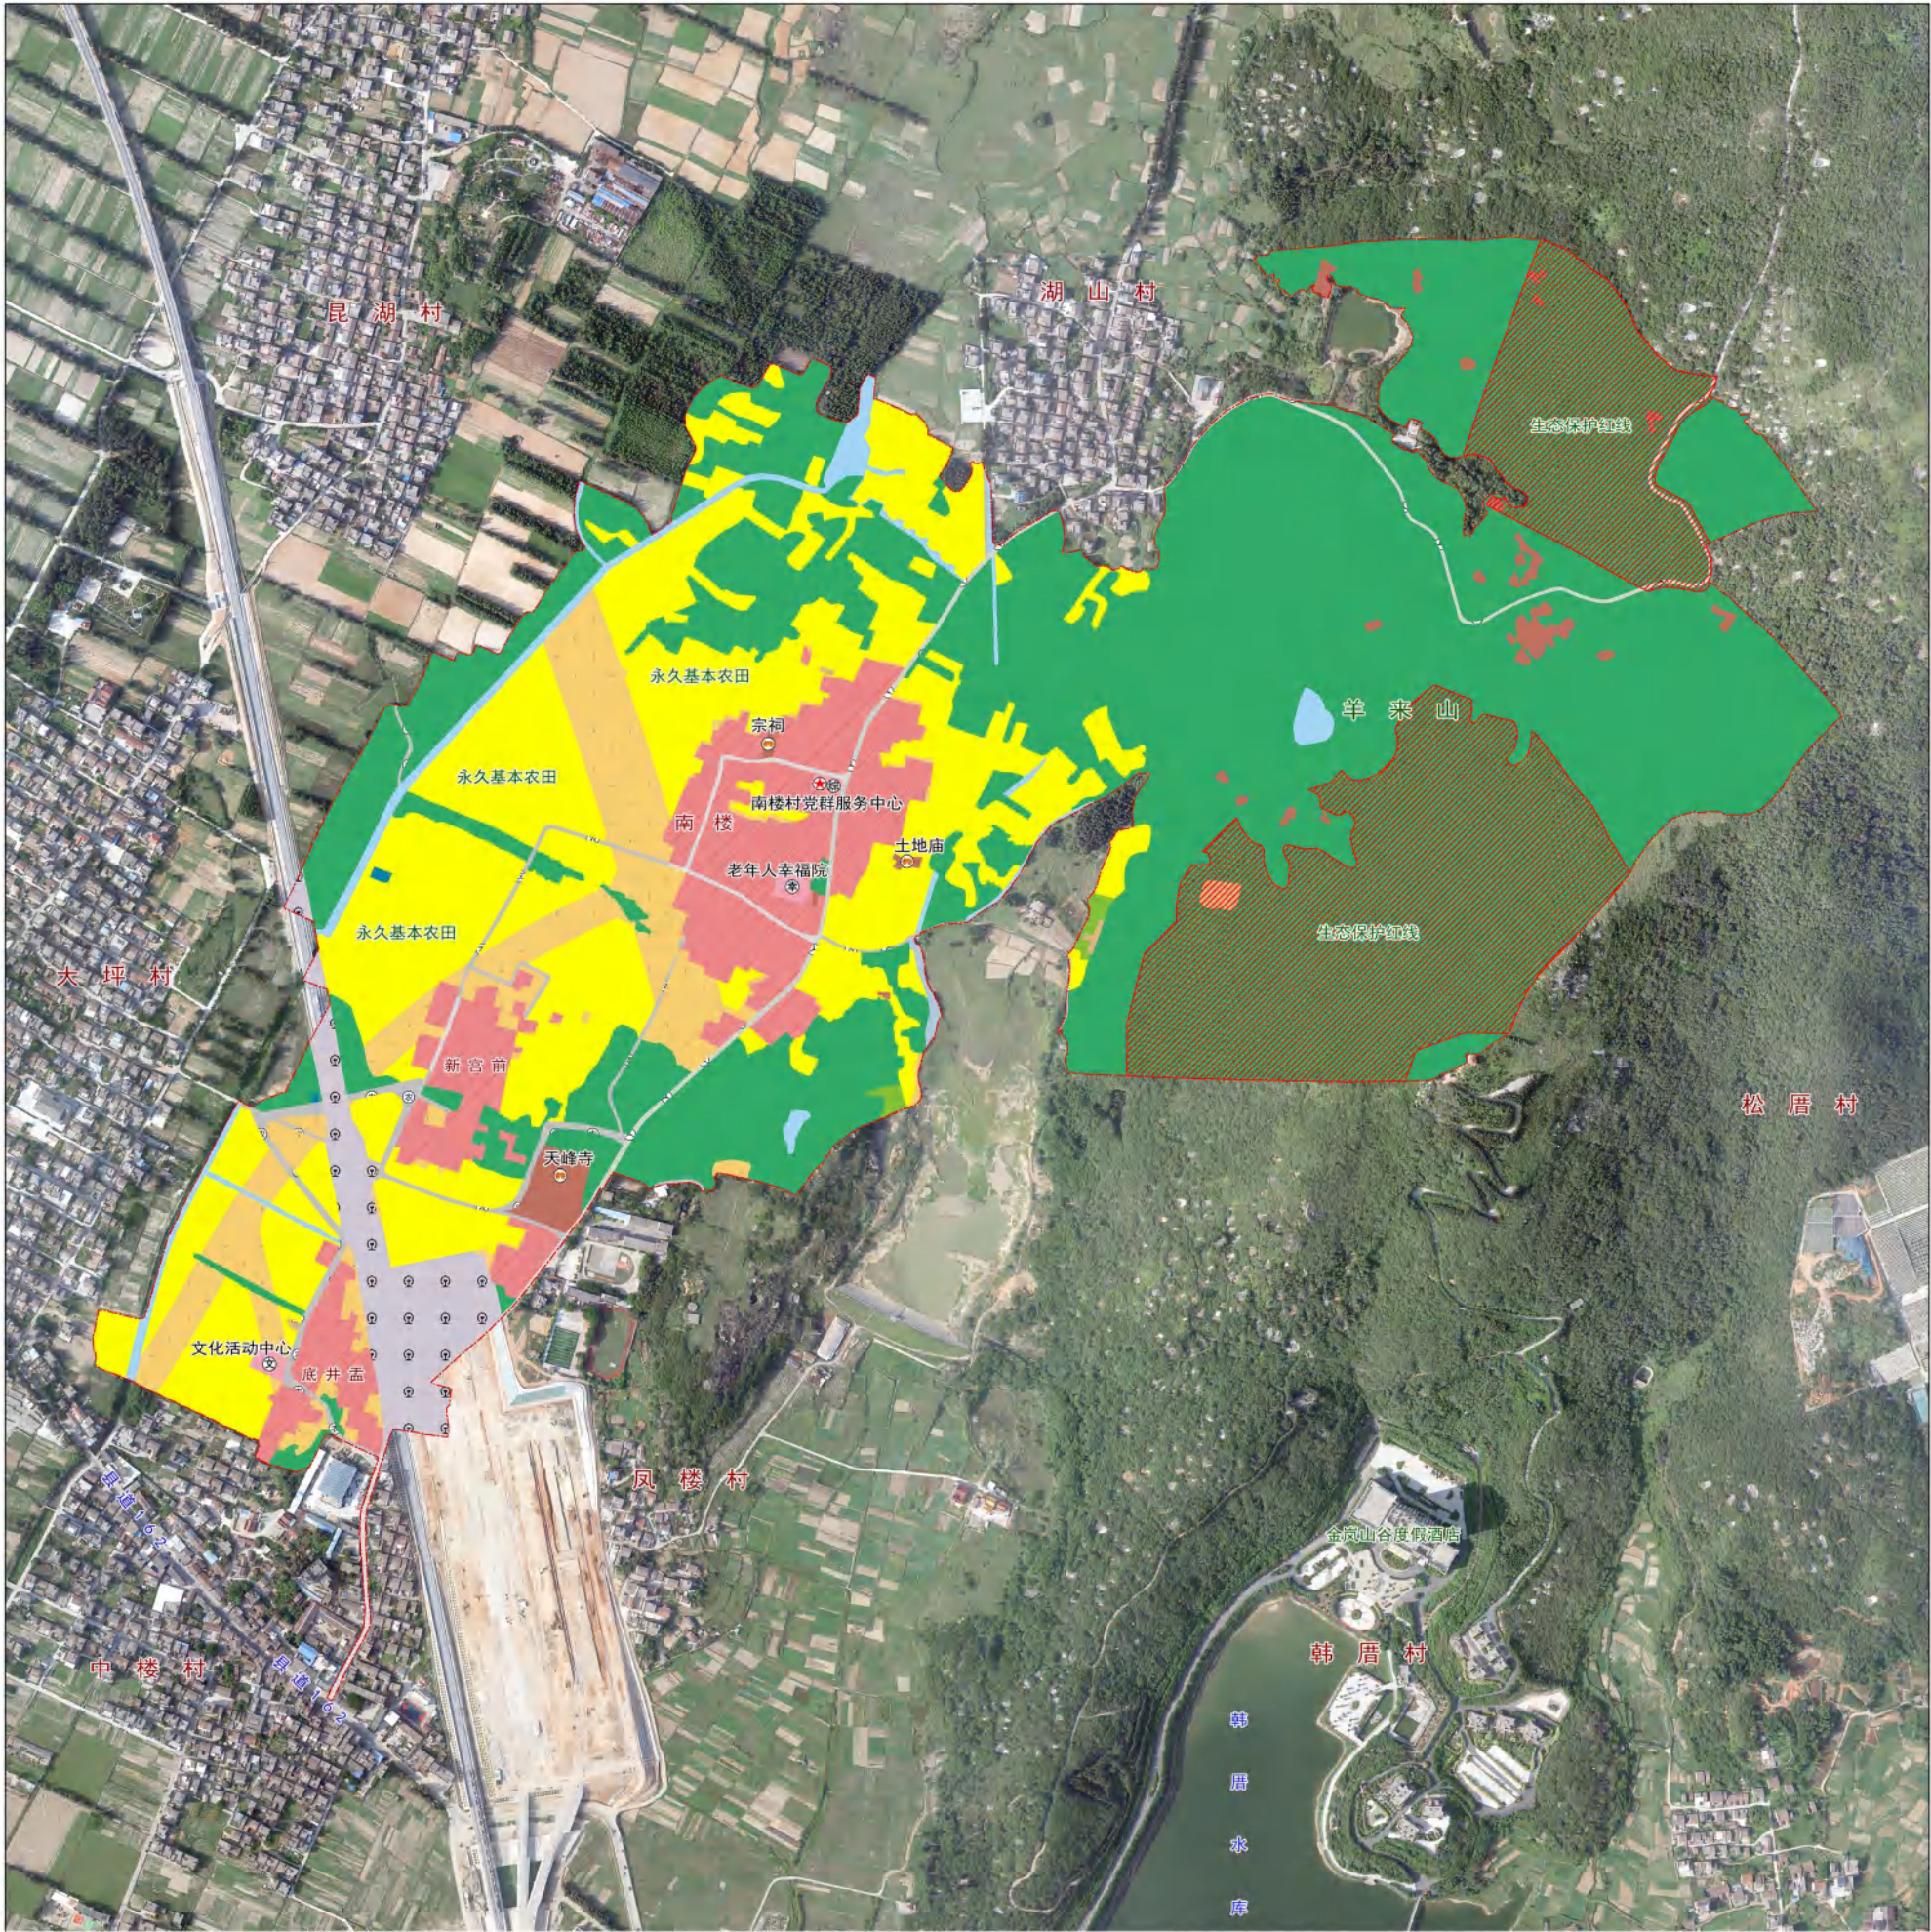

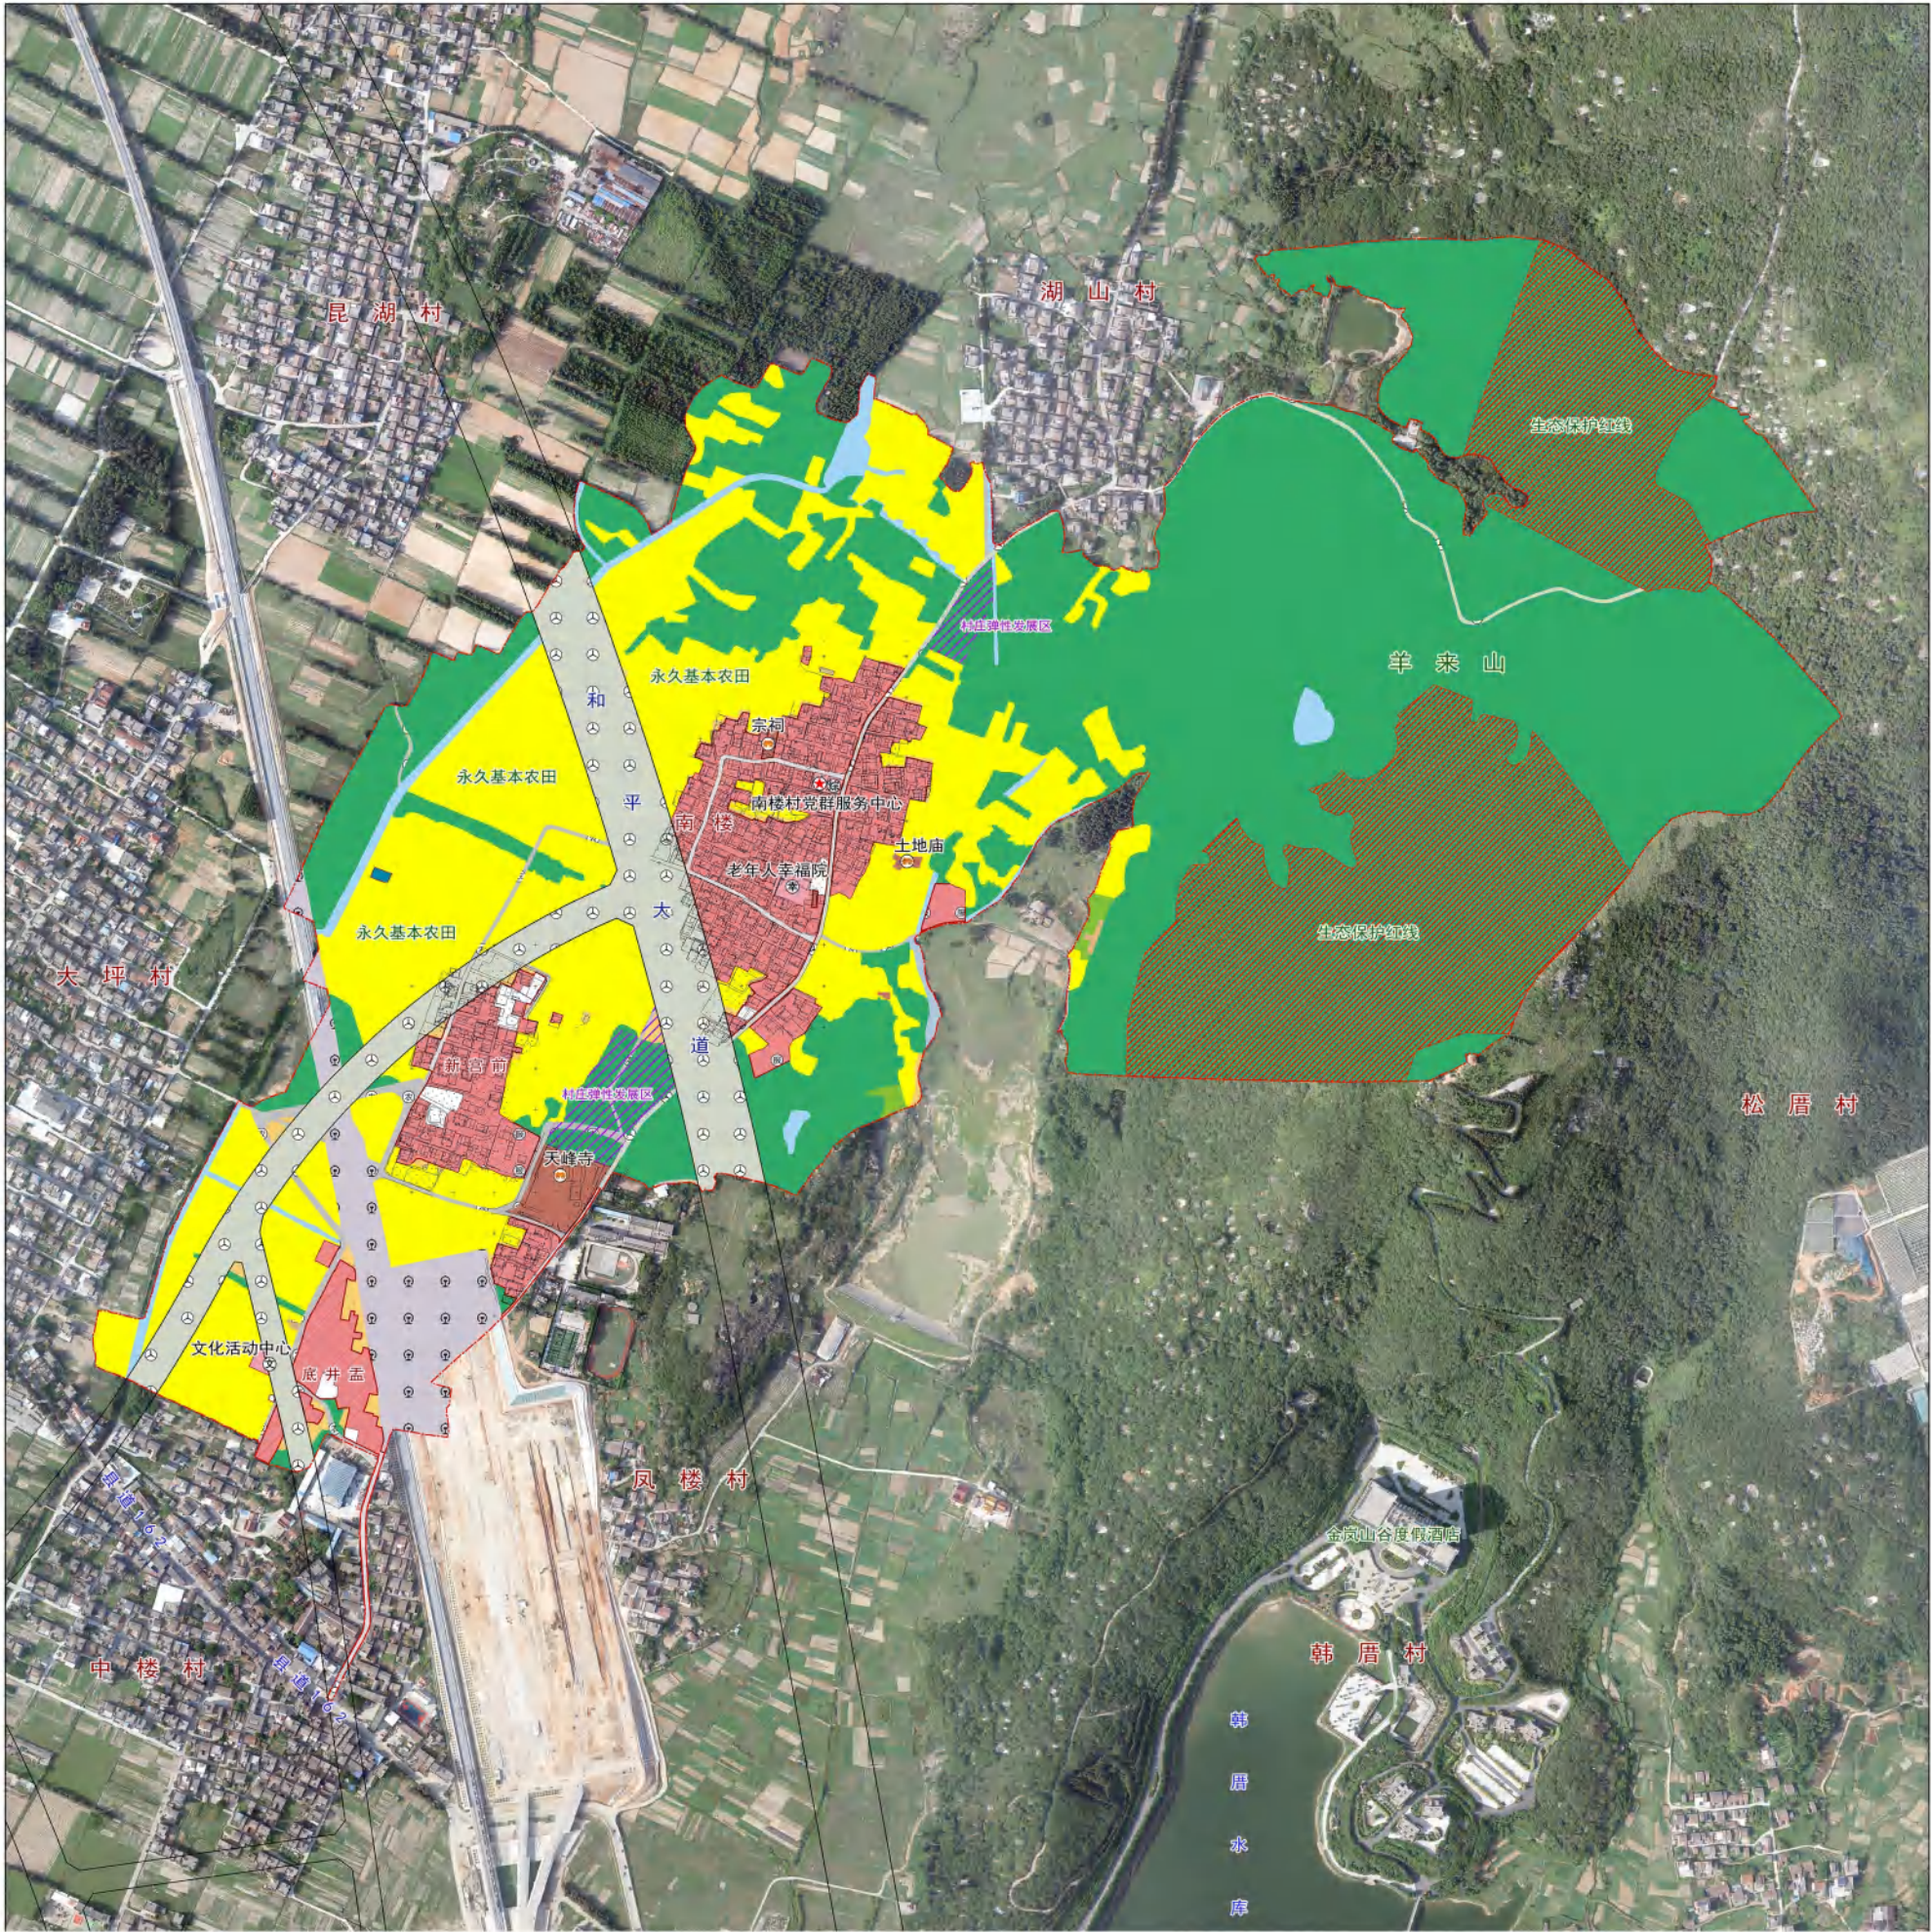

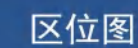

风玫瑰与比例尺



图例



居民点管控规则


公共设施：保留现状村委楼及综合文化服务中心，占地面积约730平方米，结合村委会周边场地配套建设停车场、健身器材场地等；保留现状老年人活动中心，占地面积约1300平方米，幸福院东面空地暂时作为留白用地预留；规划保留祠堂、戏台、寺庙等宗庙设施，占地面积约8100平方米；现状教育用地依托中楼中小学用地；在幸福院东侧，离主要居民点约150米预留一处农村社区服务设施用地，面积约2100平方米；结合居民点街旁空地，村庄入口、天峰寺前广场新建多处公共广场或街头绿地。利用村内空地新建临时公共停车场。



道路交通设施：衔接上位规划道路网，完善道路骨架；规划路（和平大道）纵穿村域内部，道路红线宽度80米；建议两侧建筑后退道路红线不少于15米，两侧应控制15米绿化带，绿化带内的现状宅基地建议予以退出；对外交通主要依托村庄主干道连接到县道162，并向外扩散；村庄内部道路交通沿用村中已有的村道或巷道，在原有的基础上维护；部分路线疏通或新增，新增道路红线宽度应为5米；拆除部分质量较差建筑，优化道路线行，满足道路规范及消防要求；利用街头空地改建停车场。

市政设施：沿道路按30-50m距离设置垃圾收集点，按服务半径约300m配建公厕，服务游客和村民；完善村庄水电配套，远期采用雨污分离排放模式，按照不大于120m的距离配建消防栓，文保单位应重点设置。

村庄住宅管制：村庄居民点住宅建筑以保留及改造为主，原则上不大量新增宅基地，严禁核心保护区内开发建设村民住宅，建设控制地带内严控建设高度、体量、色彩，严格按照本次设计户型建设，风貌与村落协调一致。建筑严格按照“一户一宅”政策，每户宅基地面积控制在120m²以内，新建住宅高度不得超过12m，每户住宅面积控制在300m²以内，住宅建筑间距与前建筑高度比不低于1:1，相邻建筑山墙间距不低于2m，建筑宜朝南、南偏东或偏西布置，建筑后退村庄道路不得少于1m。

预留用地：规划预留1.89公顷弹性发展空间，本村设置留白用地0.54公顷；在不占用永久基本农田和生态保护红线的前提下，主要用于零星分布的农村公共公益设施、公用设施、乡村旅游设施等。建设项目用地。预留机动指标约0.64公顷。

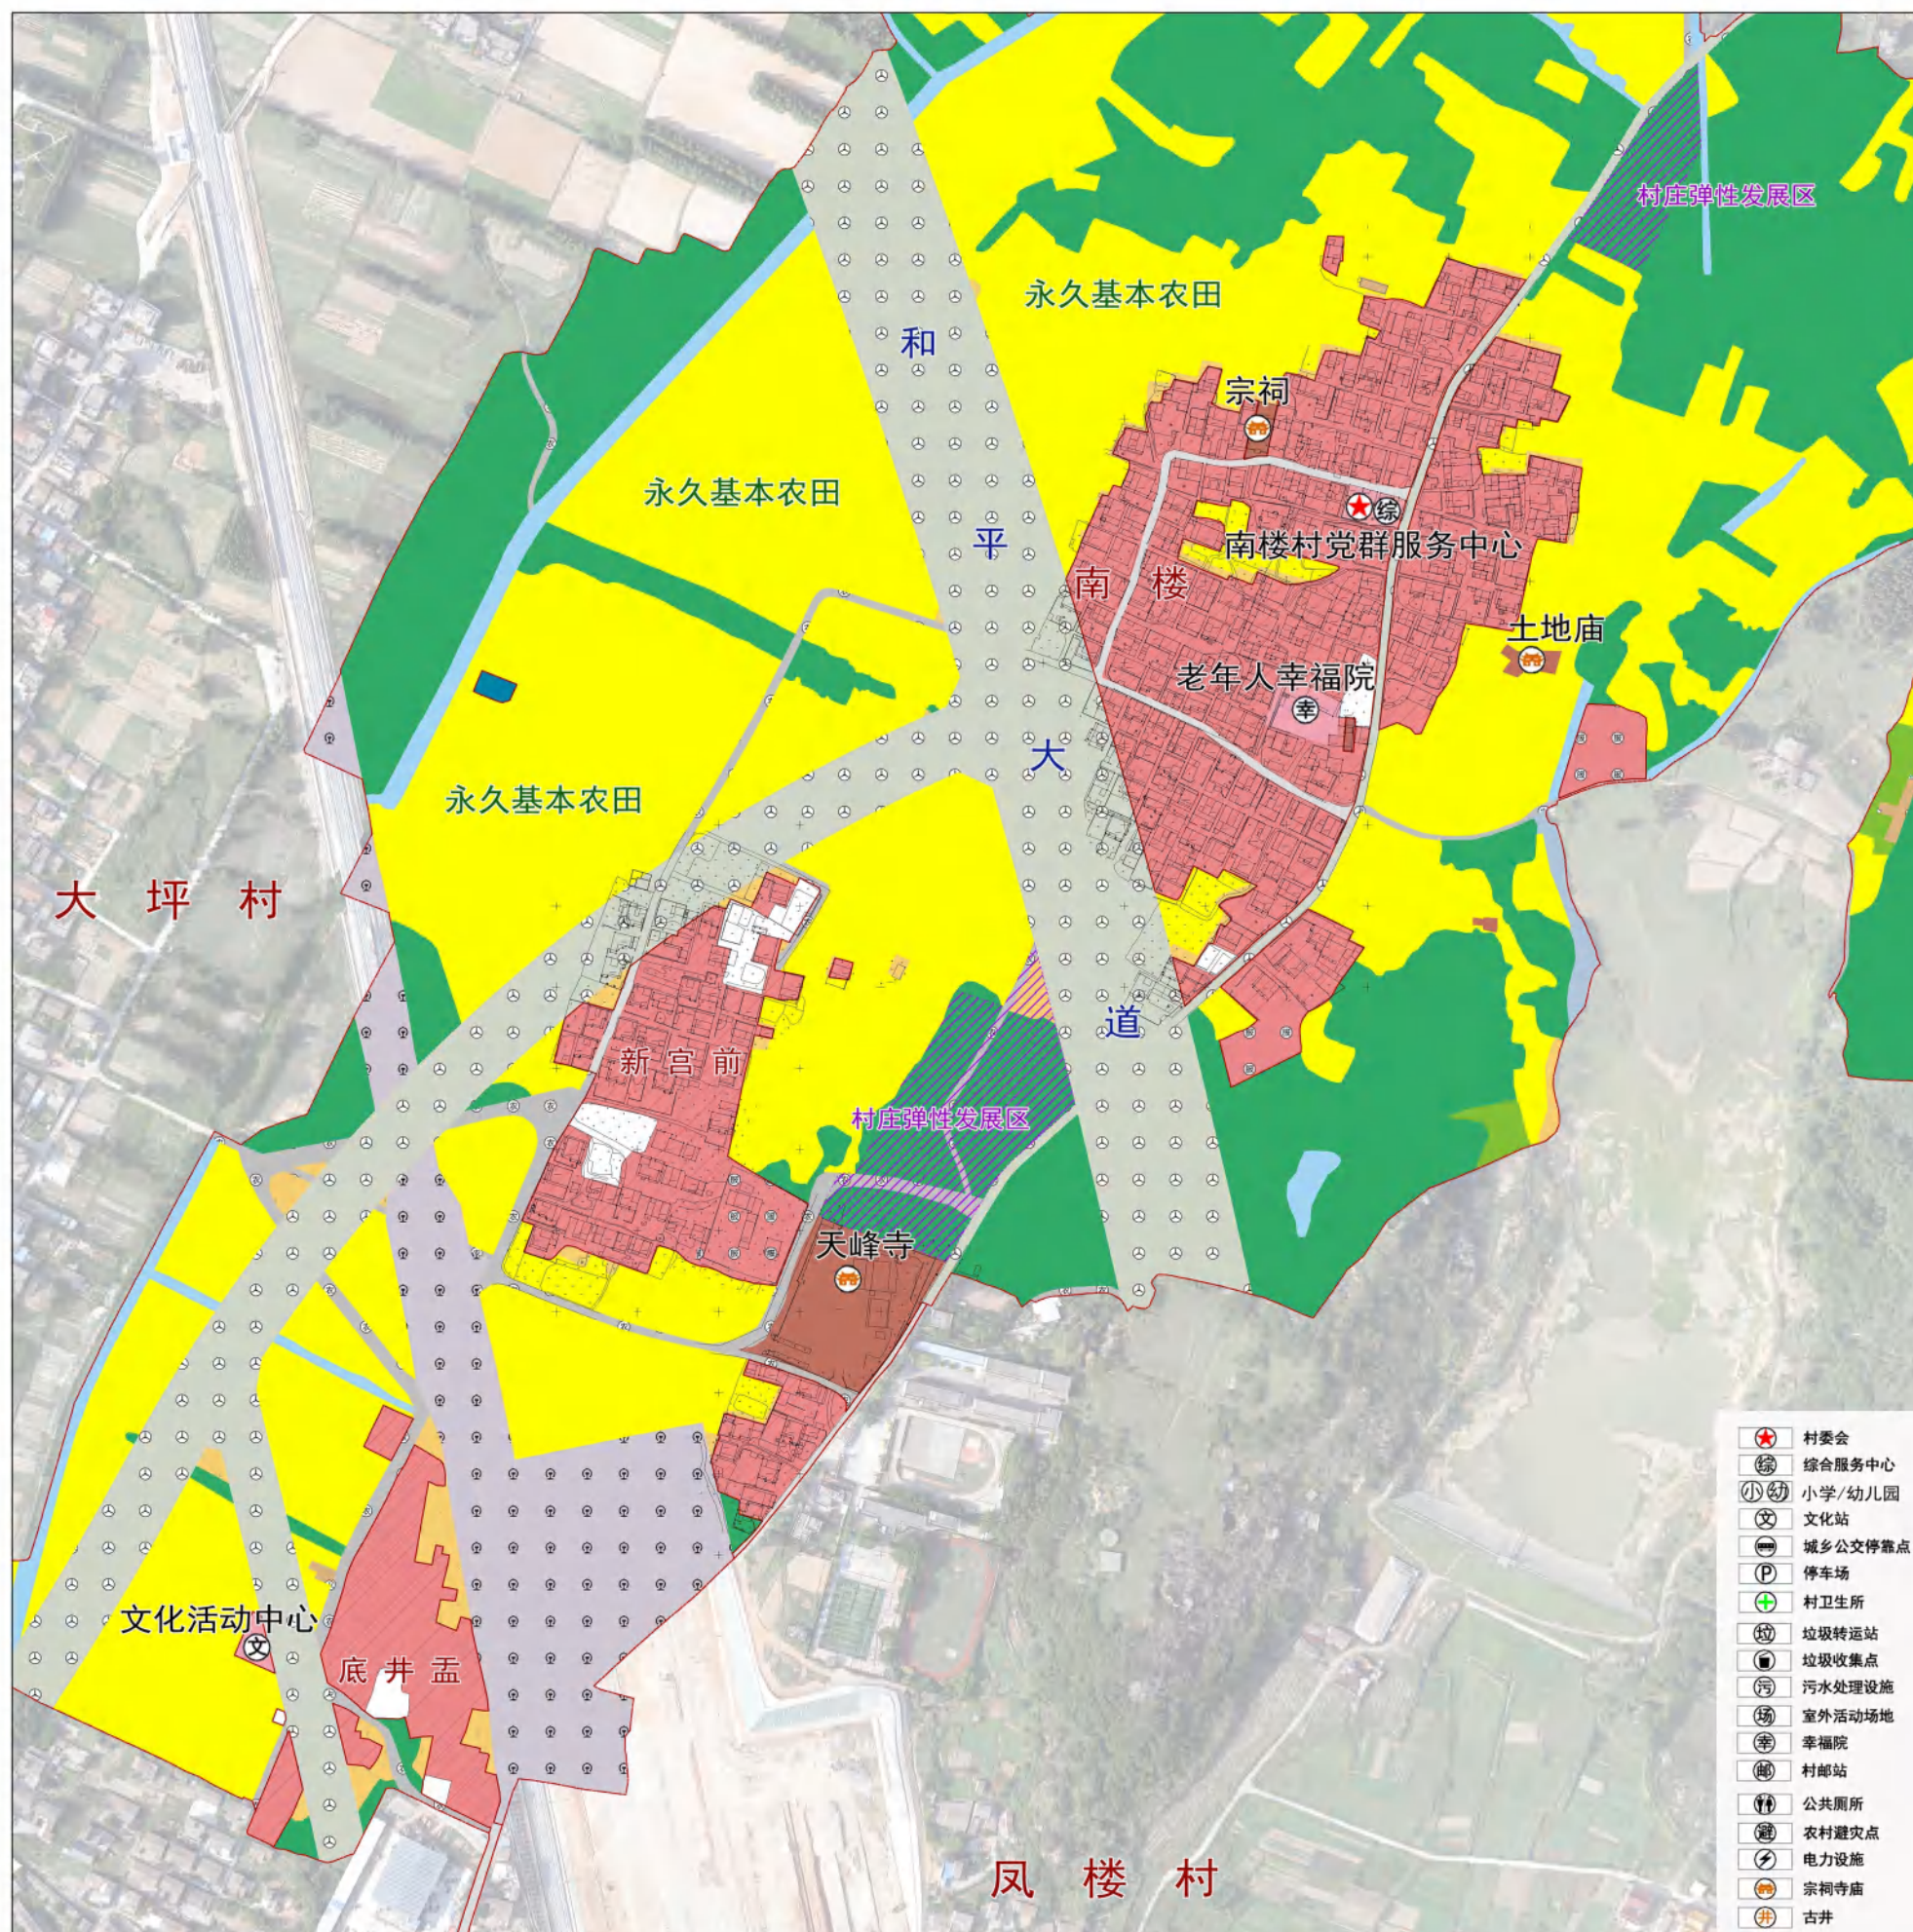

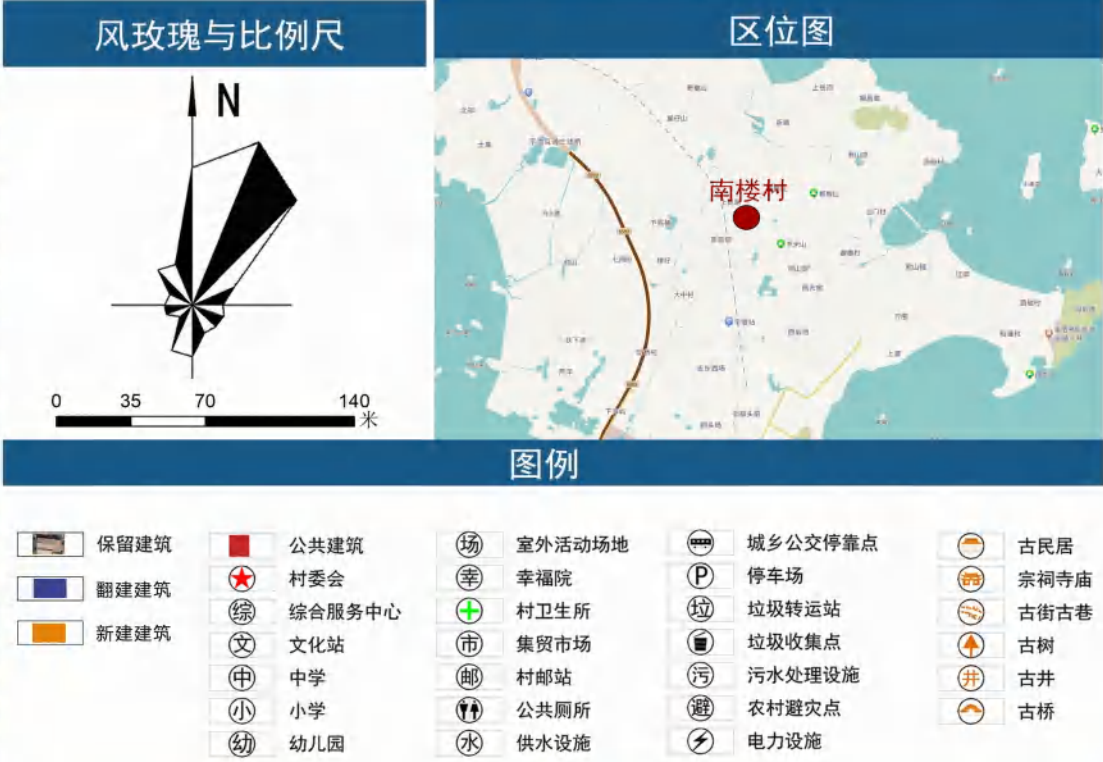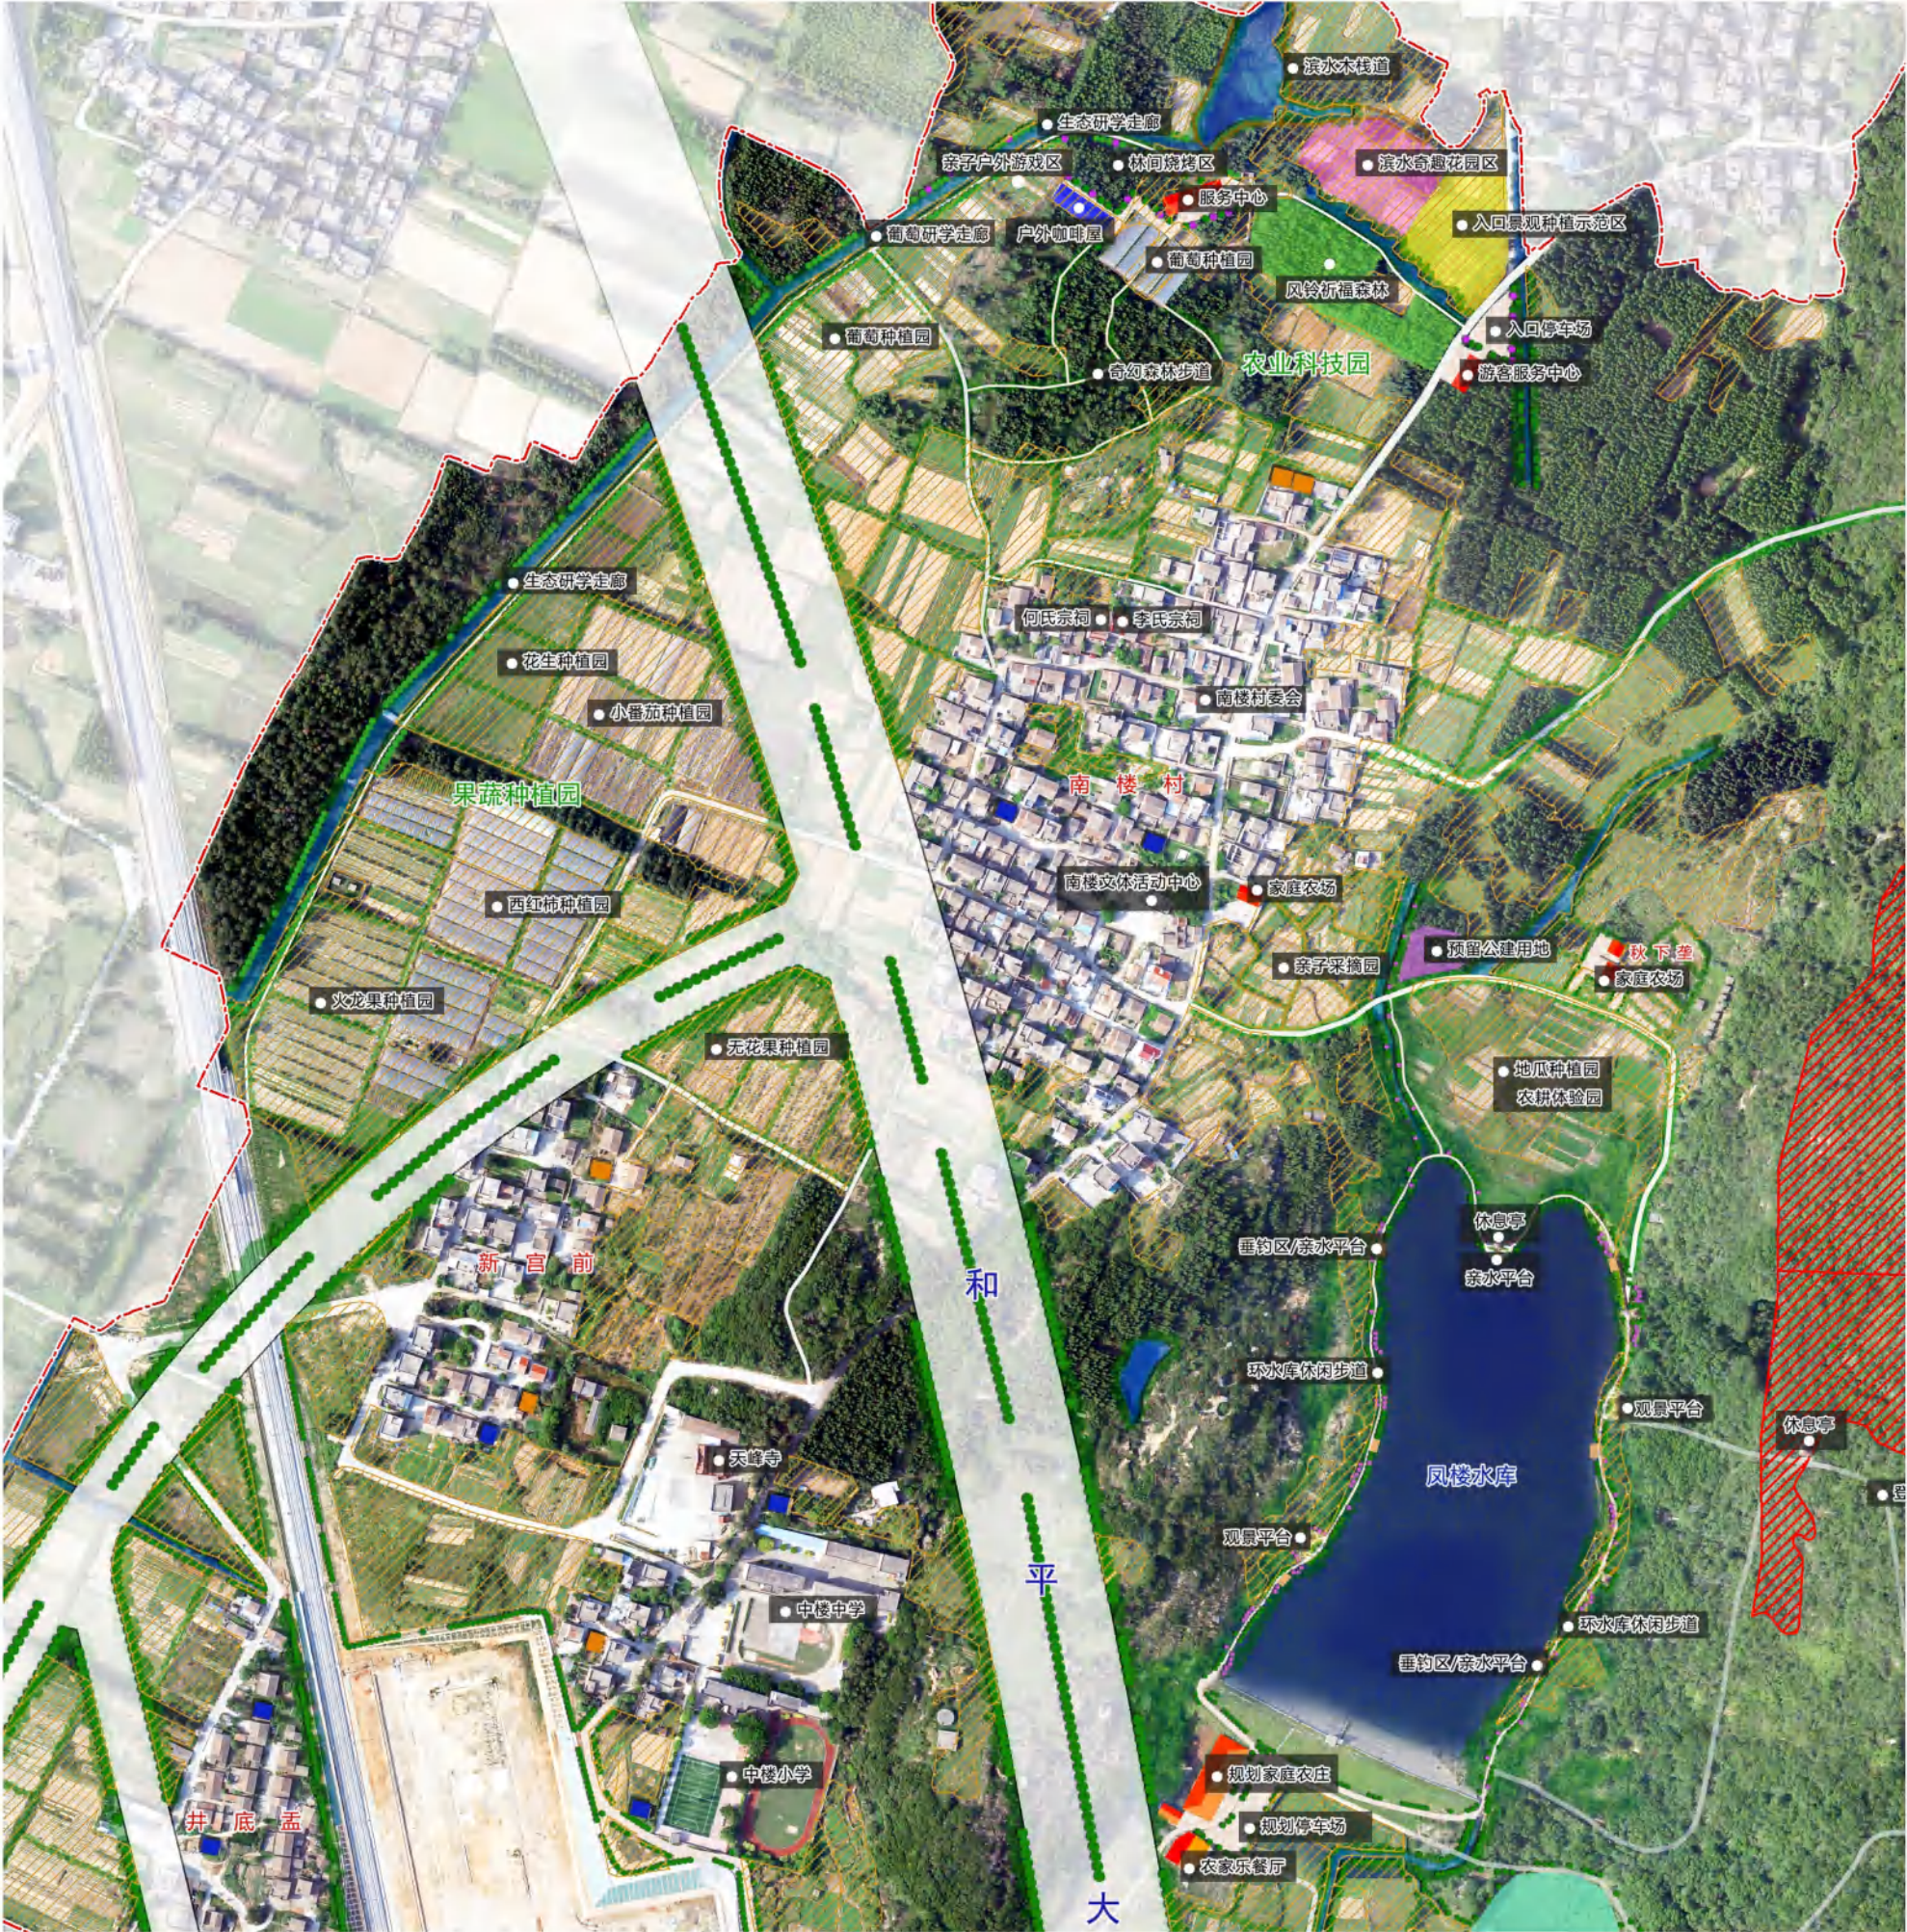

建设方案指引

9mX13m地块
(二层住宅模式)



村民建房应当遵守以下技术标准规定：

(一) 规划：村民建房要符合国土空间总体规划及各类专项规划，靠近城市、县城、乡镇所在地住宅小区，引导参照城市居住区规划设计相关标准，鼓励建设多层单元式住宅。

(二) 选址：村民建房选址应避免地质复杂、地基承载力差、地势低洼不易排涝以及易受风口、滑坡、雷电和洪水侵袭等自然灾害影响的地段，杜绝安全隐患问题。

(三) 层数和面积：农村独栋式、并联式或联排式自建住宅不得超过三层，每户住宅建筑面积控制在300平方米以内；多层单元式住宅的，每户住宅建筑面积控制在200平方米左右。

(四) 层高：一层层高控制在4.5米以内，二层以上层高控制在3.3米以内，建筑总高度不超过12米，建筑屋顶原则上应按坡屋顶设计。



(五) 间距和朝向：住宅建筑前后间距与建筑高度比一般不低于1:1，相邻房屋山墙之间（外墙至外墙）的间距不低于4米，建筑宜朝南、朝南偏东或偏西布置。新建建筑宜后退村庄干路红线3米以上，后退村庄支路红线1米以上。因旧房改造、扩建等受用地条件限制的，根据实际情况由属地乡镇人民政府合理确定相邻距离。

(六) 抗震：新建住宅必须符合工程抗震设防要求，板、梁、柱不得采用石结构。

(七) 建筑单体：应满足村民生产生活需求，住宅平面布局应设有客厅、卧室、厨房、卫生间、储藏间（农具堆放间）应满足面积、通风、采光等要求。房屋造型简洁美观，宜采用坡屋面，符合地方建筑特色，外观应进行一次性装修。

(八) 配套：应同步配建化粪池等处理设施；集中建设住宅小区的，给水排水、电力通信、道路、广电、绿化和社区服务等配套设施要同步规划建设，小区建筑密度控制在30%左右，绿地率不低于30%。

其他细则参考《福州市规范农村宅基地和建房管理实施细则(试行)》和《平潭综合实验区农房建筑立面图集》。

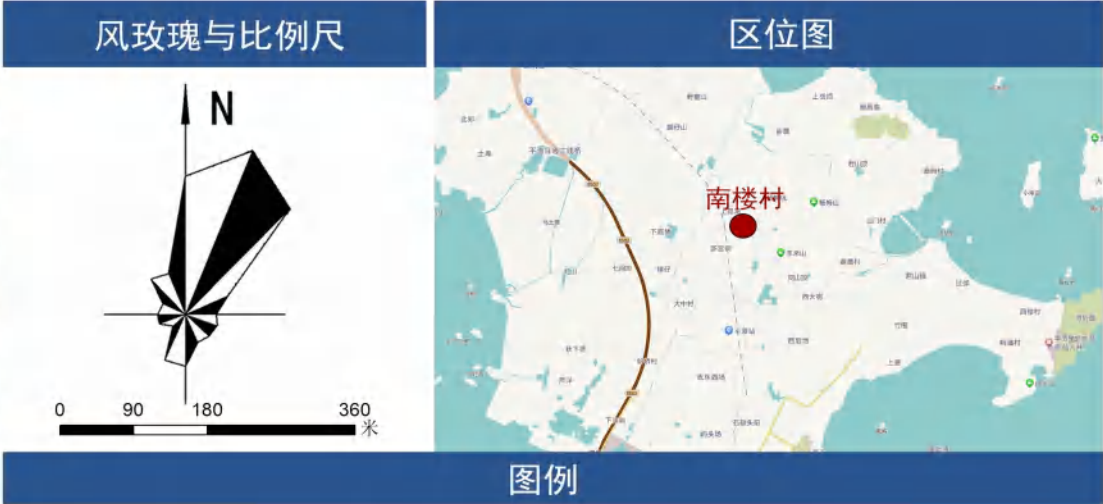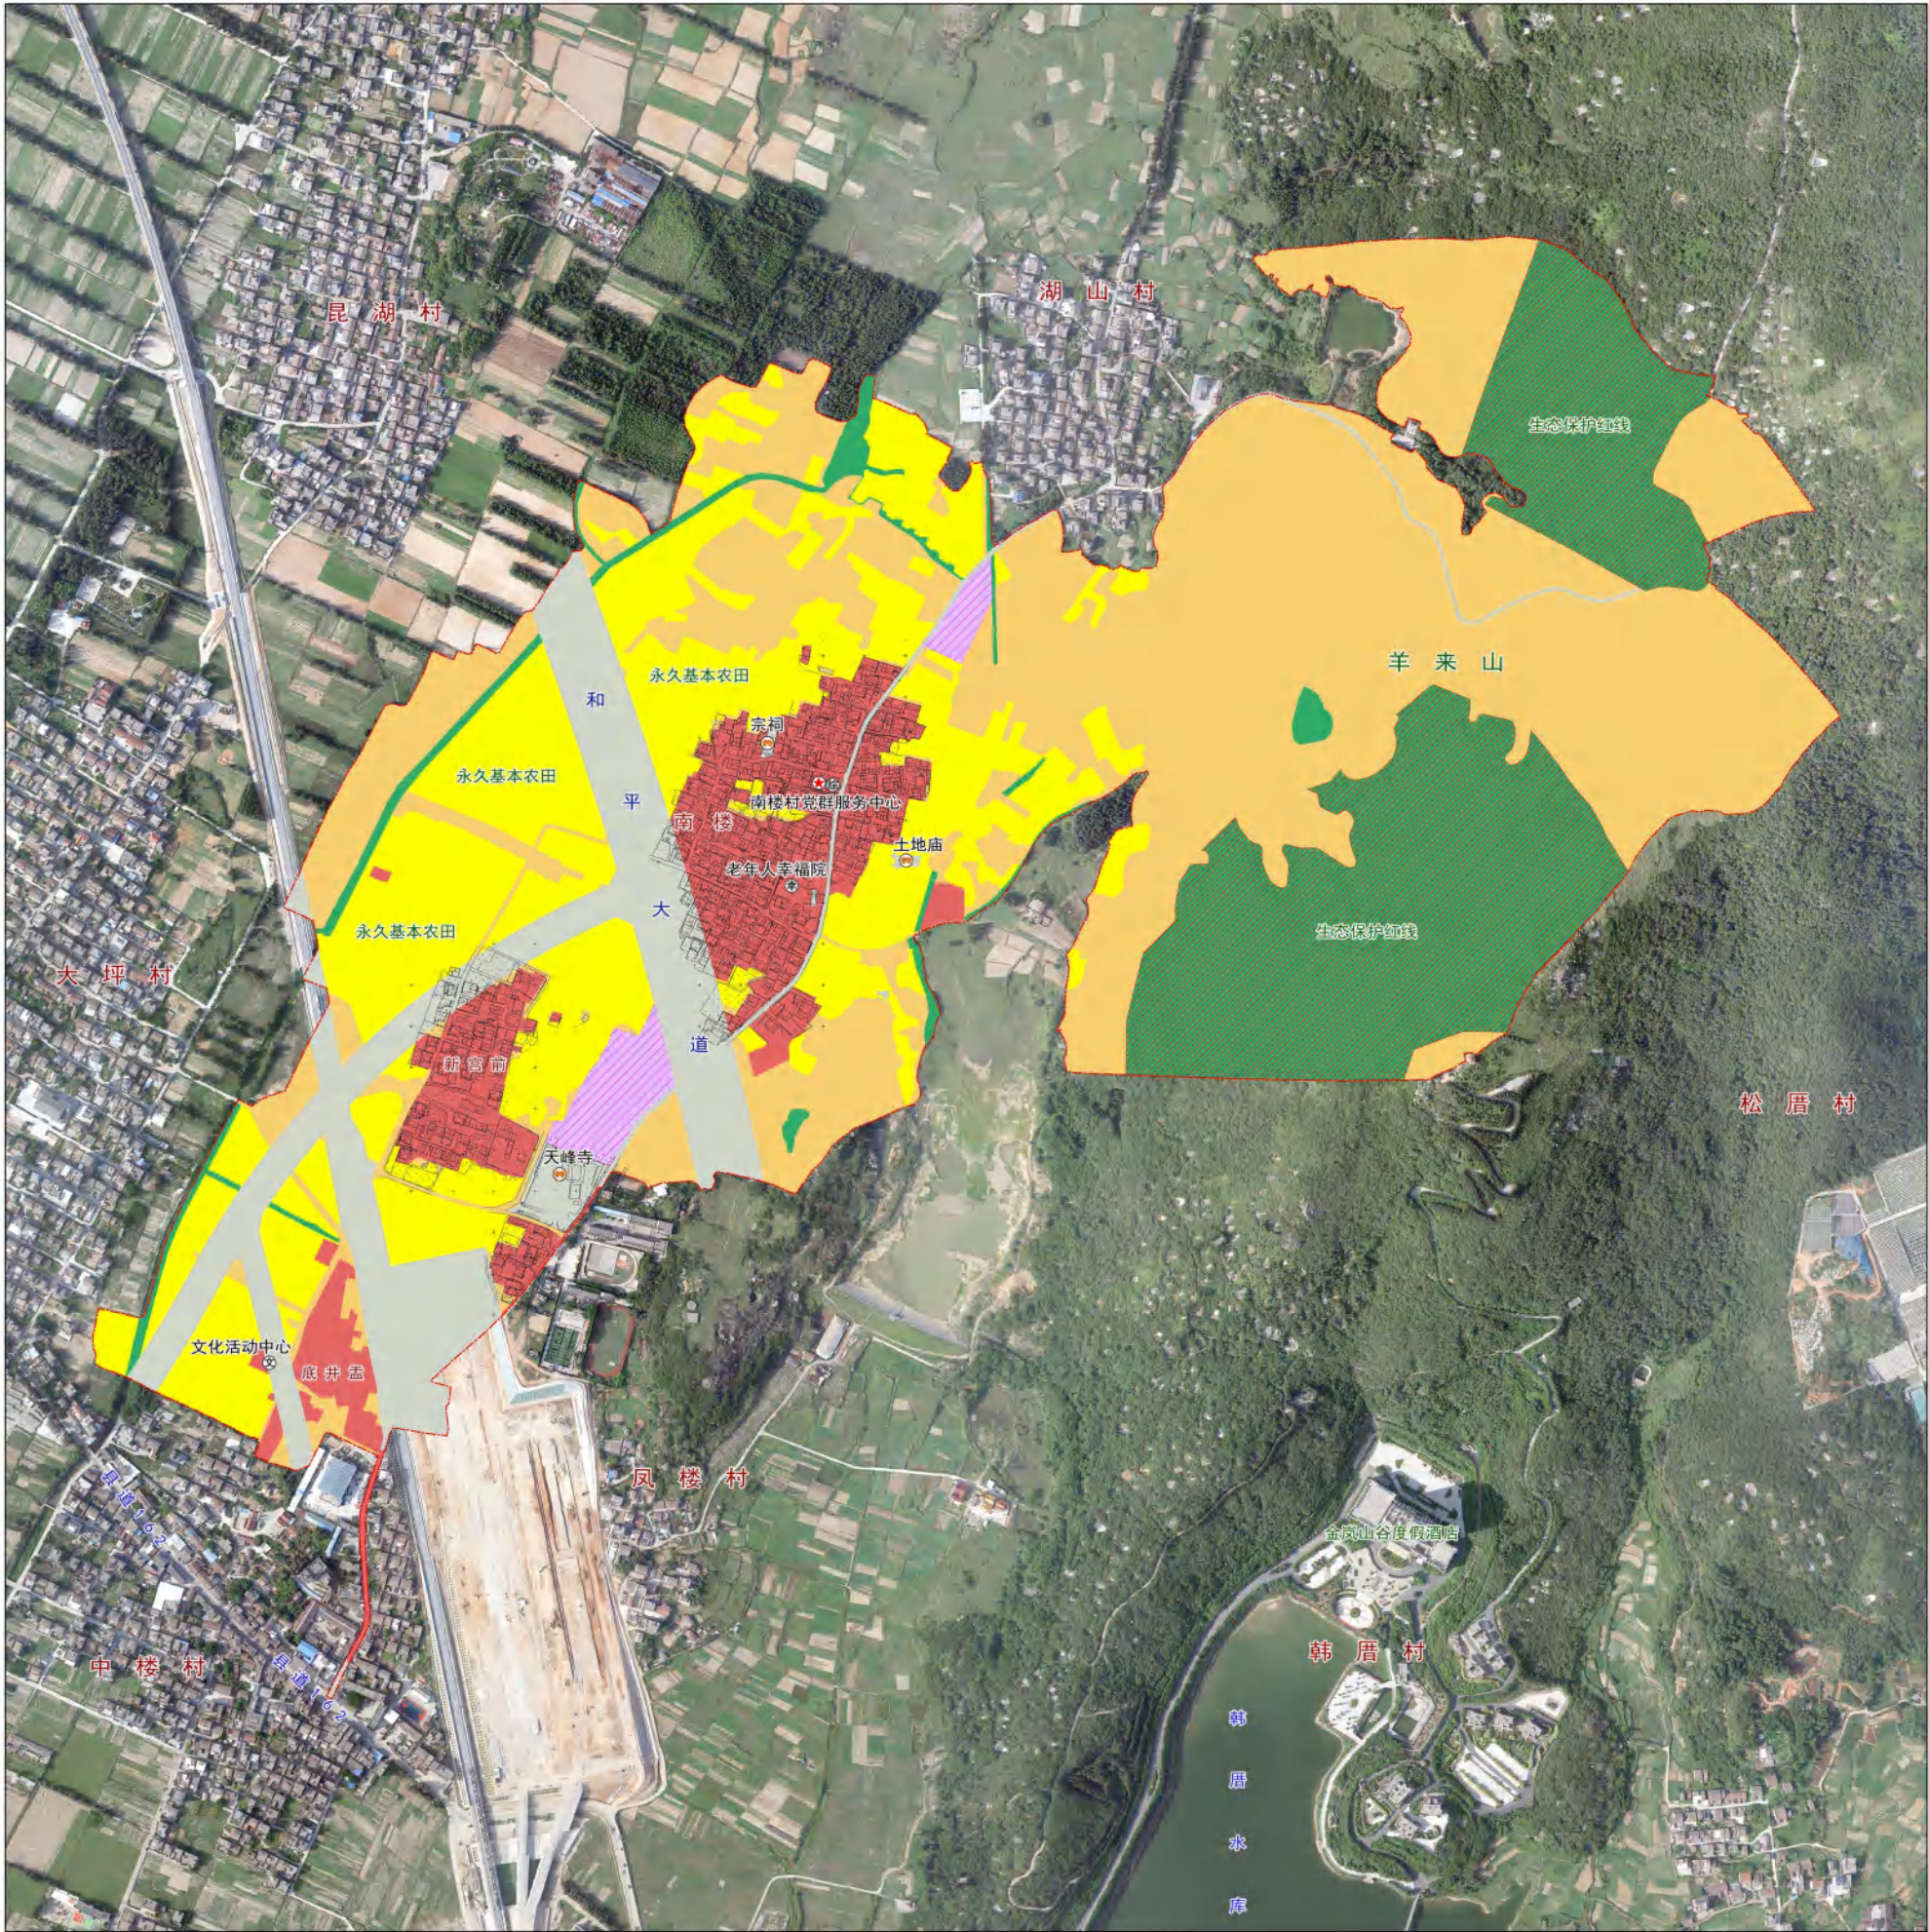

主要管控规则

一、生态空间管制

1. 1生态保护红线

规划区内划定陆域生态保护红线面积24. 86公顷。

1. 2一般生态用地

规划范围内划定一般生态用地2. 40公顷, 主要由陆地水域、以及生态保护红线底下的生态林及其他土地组成。从严控制生态用地向农业用地、建设用地转用; 不得进行破坏生态景观、污染环境的开发建设活动, 做到慎砍树、禁挖山、不填河(湖)。

二、农业空间管制

2. 1永久基本农田

规划范围内划定永久基本农田面积31. 05公顷。

严格按照《土地管理法》、《基本农田保护条例》的有关规定和永久基本农田保护区管制规则保护永久基本农田, 严禁违法占用永久基本农田, 禁止破坏永久基本农田, 任何单位和个人不得擅自占用或改变用途。

2. 2一般农业用地

规划范围内划定一般农业用地57. 13公顷, 主要由一般耕地、林地、园地、草地及农业设施建设用地组成。

严格限制在一般农用地内建房、建窑、建坟、采矿、取土、堆放固体废弃物或者进行其他破坏活动。严格限制农用地转用, 非农建设项目确需占用农用地的, 应当报具有审批权限的自然资源管理部门审查批准。

三、建设空间管制

3. 1村庄集中建设区

规划范围内划定村庄建设用地规模为12. 55公顷, 主要为农村宅基地、农村社区服务设施用地、绿地与开敞空间用地、留白用地等; 其他包括: 区域基础设施用地及其他建设用地, 面积为15. 96公顷。

规划期内村庄集中建设区原则上不得调整, 如需调整按规划修改处理, 严格论证, 报原审批机关批准。村庄集中建设区用地应该优先满足村民住房和农村基本公共服务设施用地需求。严格控制经营性建设用地的开发强度和非农活动影响范围。

3. 2村庄弹性发展区、机动指标

规划范围内划定村庄弹性发展区1. 89公顷; 预留的机动指标面积约0. 64公顷。

农村居民点建设用地布局可在弹性发展区范围内进行调整, 同时相应核减村庄集中建设区用地规模。区内现状农用地在批准改变用途之前, 应当按原用途使用, 不得荒芜。



近期建设项目表							
序号	项目类型	项目名称	项目说明	建设规模	建设年限	投资额(万元)	建议资金来源
1	村容村貌提升	拆旧建新	整合用地，村域范围内原则上不新增建设用地，村内以挖掘存量建设用地为主，建议保留原有建筑风貌，部分建筑修缮改造成民宿或农庄；	-	2023-2028	—	村民自筹
2		村庄村貌治理	村庄主干道沿线、次干道沿线垃圾整治	约3km	2023-2028	30	财政出资
3		日常环卫养护	村内日常环境卫生保养，结合公厕配置垃圾分类收集点1个。垃圾桶沿主干道每100m设置一个；	100m/个	—	20	村财、村民自筹
4	生态修复国土整治	低效建设用地整治	对村内现状存在的特殊用地进行整治，主要为坟墓用地征迁，远期由政府统筹安置。	7700m2	2023-2028	—	专项资金
5	产业发展	家庭农场	利用现状闲置石头厝，招商引资，新建家庭农庄，配套农业采摘园，农耕体验，亲子娱乐等田园项目；	3000m2	2023-2028	—	村民自筹 招商引资
6		农业科技园	规划在村庄北面打造农业科技园，作为本村的品牌名片，依托现状成规模的葡萄种植园发展采摘经济，吸引游客；周边规划建设户外亲子游戏区、户外咖啡屋、风铃祈福森林、林间奇幻步道、葡萄文化研学区等。	100亩	2023-2035	—	招商引资
7	公共基础设施	党群服务中心提升	综合服务中心平台场所建设、志愿服务队伍建设，便民服务中心，规模730平方米；	730m2	2023-2025	50	村财、 村民自筹
8		日间照料中心/文化活动中心	提升改造现状老年人活动中心；新增文化活动中心，并配套长者食堂等相关基础设施。	1300m2	2023-2028	50	
9		街角公园、休闲广场	结合村委会新建1处室外活动场地，提升绿化及相关健身器材设施；利用村内闲置地和空闲地，建设街头小广场；总面积约1800平方米；	1800m2	2023-2028	50	
10	市政基础设施	实施厕所革命	现状村庄有一处公厕，规划拟建一处三类标准旅游公厕，并配建垃圾是分类收集站；面积100平方米；	100m2	2023-2028	30	专项资金
11		停车场建设	结合路边现状空闲地，平整土地，作为临时社会公共停车场地，供游客临时停车使用，面积约800平方米；	800m2	2023-2028	10	村财、村民自筹
12	历史文化保护	宗祠、寺庙	宗祠、祖厅、寺庙周边环境整治提升，增加绿植、健身器材设施、垃圾桶、民俗、宗教文化宣传栏等；	-	2023-2028	20	专项资金
合计						260	

用地用海类型				规划基期年		规划目标年		用地调整（公顷）	
				面积（公顷）	比重（%）	面积（公顷）	比重（%）		
耕地（01）				39.51	27.09	31.91	21.88	-7.59	
园地（02）				0.00	0.00	0.00	0.00	0.00	
林地（03）				82.99	56.91	81.01	55.55	-1.98	
草地（04）				0.24	0.16	0.24	0.16	0.00	
湿地（05）				0.13	0.09	0.13	0.09	0.00	
合计				122.87	84.26	113.29	77.69	-9.58	
农业设施建设用地	村道用地			1.66	1.14	1.38	0.95	-0.28	
	种植设施建设用地			0.21	0.15	0.21	0.15	0.00	
	畜禽养殖设施建设用地			0.00	0.00	0.00	0.00	0.00	
	水产养殖设施建设用地			0.00	0.00	0.00	0.00	0.00	
合计				1.87	1.28	1.59	1.09	-0.28	
村域建设用地	村域城乡建设用地	城镇用地			0.00	0.00	0.00	0.00	0.00
		居住用地	农村社区服务设施用地	0.00	0.00	0.71	0.48	0.71	
			农村宅基地	11.27	7.73	10.54	7.23	-0.73	
			公共管理与公共服务用地			0.33	0.22	0.25	0.17
		商业服务业用地			0.00	0.00	0.00	0.00	0.00
		工业用地			0.00	0.00	0.00	0.00	0.00
		仓储用地			0.00	0.00	0.00	0.00	0.00
		村庄内部道路用地			0.54	0.37	0.48	0.33	-0.05
		交通场站用地			0.00	0.00	0.00	0.00	0.00
		其他交通设施用地			0.00	0.00	0.00	0.00	0.00
		公用设施用地			0.04	0.03	0.03	0.02	-0.01
		绿地与开敞空间用地			0.00	0.00	0.00	0.00	0.00
		留白用地			0.00	0.00	0.54	0.37	0.54
		空闲地			0.00	0.00	0.00	0.00	0.00
		合计			12.17	8.35	12.55	8.60	0.38
		合计			12.17	8.35	12.55	8.60	0.38
		区域基础设施用地			5.00	3.43	15.29	10.48	10.29
	其他建设用地			1.52	1.04	0.83	0.57	-0.69	
合计				18.69	12.81	28.67	19.66	9.98	
陆地水域				2.40	1.64	2.27	1.56	-0.12	
渔业用海				0.00	0.00	0.00	0.00	0.00	
工矿通信用海				0.00	0.00	0.00	0.00	0.00	
交通运输用海				0.00	0.00	0.00	0.00	0.00	
游憩用海				0.00	0.00	0.00	0.00	0.00	
特殊用海				0.00	0.00	0.00	0.00	0.00	
其他土地				0.00	0.00	0.00	0.00	0.00	
其他海域				0.00	0.00	0.00	0.00	0.00	
总计				145.82	100.00	145.82	100.00	0.00	

序号	指标	属性	单位	现状基期年	规划目标年	备注
一、村庄发展性指标						
1	村域建设用地总面积	约束性	公顷	18. 69	28. 67	
2	村域城乡建设用地面积	约束性	公顷	12. 17	12. 55	
3	村庄建设用地规模	预期性	公顷	12. 17	12. 55	
4	公共管理与公共服务用地规模	预期性	公顷	0. 33	0. 25	
5	公用设施用地规模	预期性	公顷	0. 04	0. 03	
6	人均村庄建设用地面积	预期性	平方米/人	98. 95	102. 84	
二、村庄保护性指标						
7	生态保护红线面积	约束性	公顷	24. 86	24. 86	
8	永久基本农田保护面积	约束性	公顷	31. 05	31. 05	
9	耕地保有量	约束性	公顷	39. 51	31. 91	
10	林地保有量	约束性	公顷	82. 99	81. 01	
11	湿地面积	约束性	公顷	0. 13	0. 13	
12	大陆自然海岸线保有率	约束性	%	0. 00	0. 00	
13	自然和文化遗产	预期性	处	0	0	

序号	项目类型	项目名称	项目说明	建设规模	建设年限	投资额(万元)	建议资金来源
1	村容村貌提升	拆旧建新	整合用地，村域范围内原则上不新增建设用地，村内以挖掘存量建设用地为主，建议保留原有建筑风貌，部分建筑修缮改造成民宿或农庄；	-	2023-2028	——	村民自筹
2		村容村貌治理	村庄主干道沿线、次干道沿线垃圾整治	约3km	2023-2028	30	财政出资
3		日常环卫养护	村内日常环境卫生保养，结合公厕配置垃圾分类收集点1个。垃圾桶沿主干道每100m设置一个；	100m/个	——	20	村财、村民自筹
4	生态修复 国土整治	低效建设用地整治	对村内现状存在的特殊用地进行整治，主要为坟墓用地征迁，远期由政府统筹安置。	7700m2	2023-2028	——	专项资金
5	产业发展	家庭农场	利用现状闲置石头厝，招商引资，新建家庭农庄，配套农业采摘园，农耕体验，亲子娱乐等田园项目；	3000m2	2023-2028	——	村民自筹 招商引资
6		农业科技园	规划在村庄北面打造农业科技园，作为本村的品牌名片，依托现状成规模的葡萄种植园发展采摘经济，吸引游客；周边规划建设户外亲子游戏区、户外咖啡屋、风铃祈福森林、林间奇幻步道，葡萄文化研学区等。	100亩	2023-2035	——	招商引资
7	公共服务设施	党群服务中心提升	综合服务中心平台场所建设、志愿服务队伍建设，便民服务中心，规模730平方米；	730m2	2023-2025	50	村财、 村民自筹
8		日间照料中心/文化活动中心	提升改造现状老年人活动中心；新增文化活动中心，并配套长者食堂等相关基础设施。	1300m2	2023-2028	50	
9		街角公园、休闲广场	结合村委会新建1处室外活动场地，提升绿化及相关健身器材设施；利用村内闲置地和空闲地，建设街头小广场；总面积约1800平方米；	1800m2	2023-2028	50	
10	市政基础设施	实施厕所革命	现状村庄有一处公厕，规划拟建一处三类标准旅游公厕，并配建垃圾是分类收集站；面积100平方米；	100m2	2023-2028	30	专项资金
11		停车场建设	结合路边现状空闲地，平整土地，作为临时社会公共停车场地，供游客临时停车使用，面积约800平方米；	800m2	2023-2028	10	村财、村民自筹
12	历史文化保护	宗祠、寺庙	宗祠、祖厅、寺庙周边环境整治提升，增加绿植、健身器材设施、垃圾桶、民俗、宗教文化宣传栏等；	-	2023-2028	20	专项资金
合计						260	